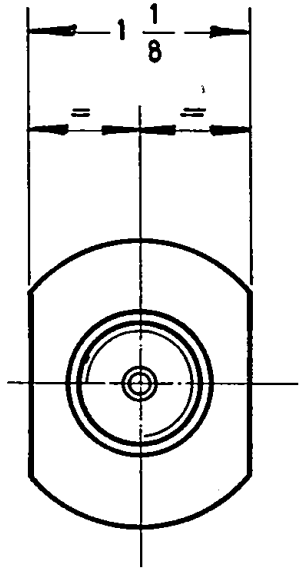

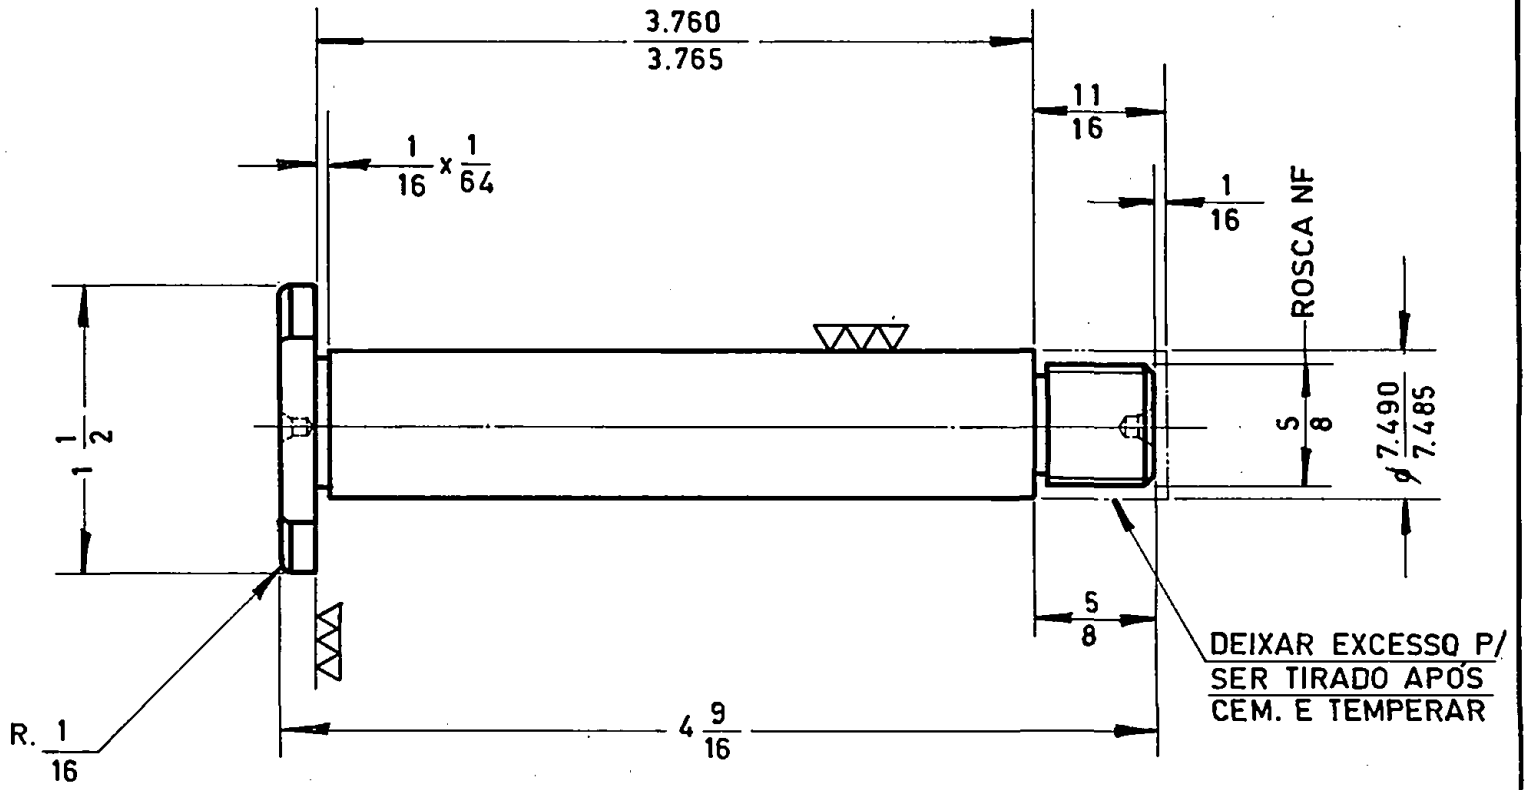

5 - C.C.

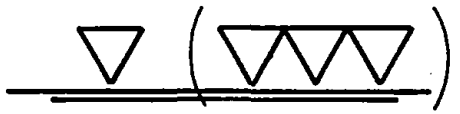

TOLERÂNCIAS STANDARD PARA SUPERFÍCIES USINADAS SEM TOLERÂNCIA INDICADA DECIMAL ± 005" FRAÇÃO DE 0" ATÉ 5" ± 1/64 DE 5" ATÉ 24" ± 1/32 ACIMA DE 24" ± 1/16	VIDROS VITON LTDA. AÇO VB-20 ø 1 1/2 INSERT BOLT 5" C.C. CEMENTAR 0,8 m.m. PROF. TEMP. 50÷55 RC.	DES. Francisco ESCALA 1:1 PEÇA 1500-565-508-1

FOLHA 59 (M)