

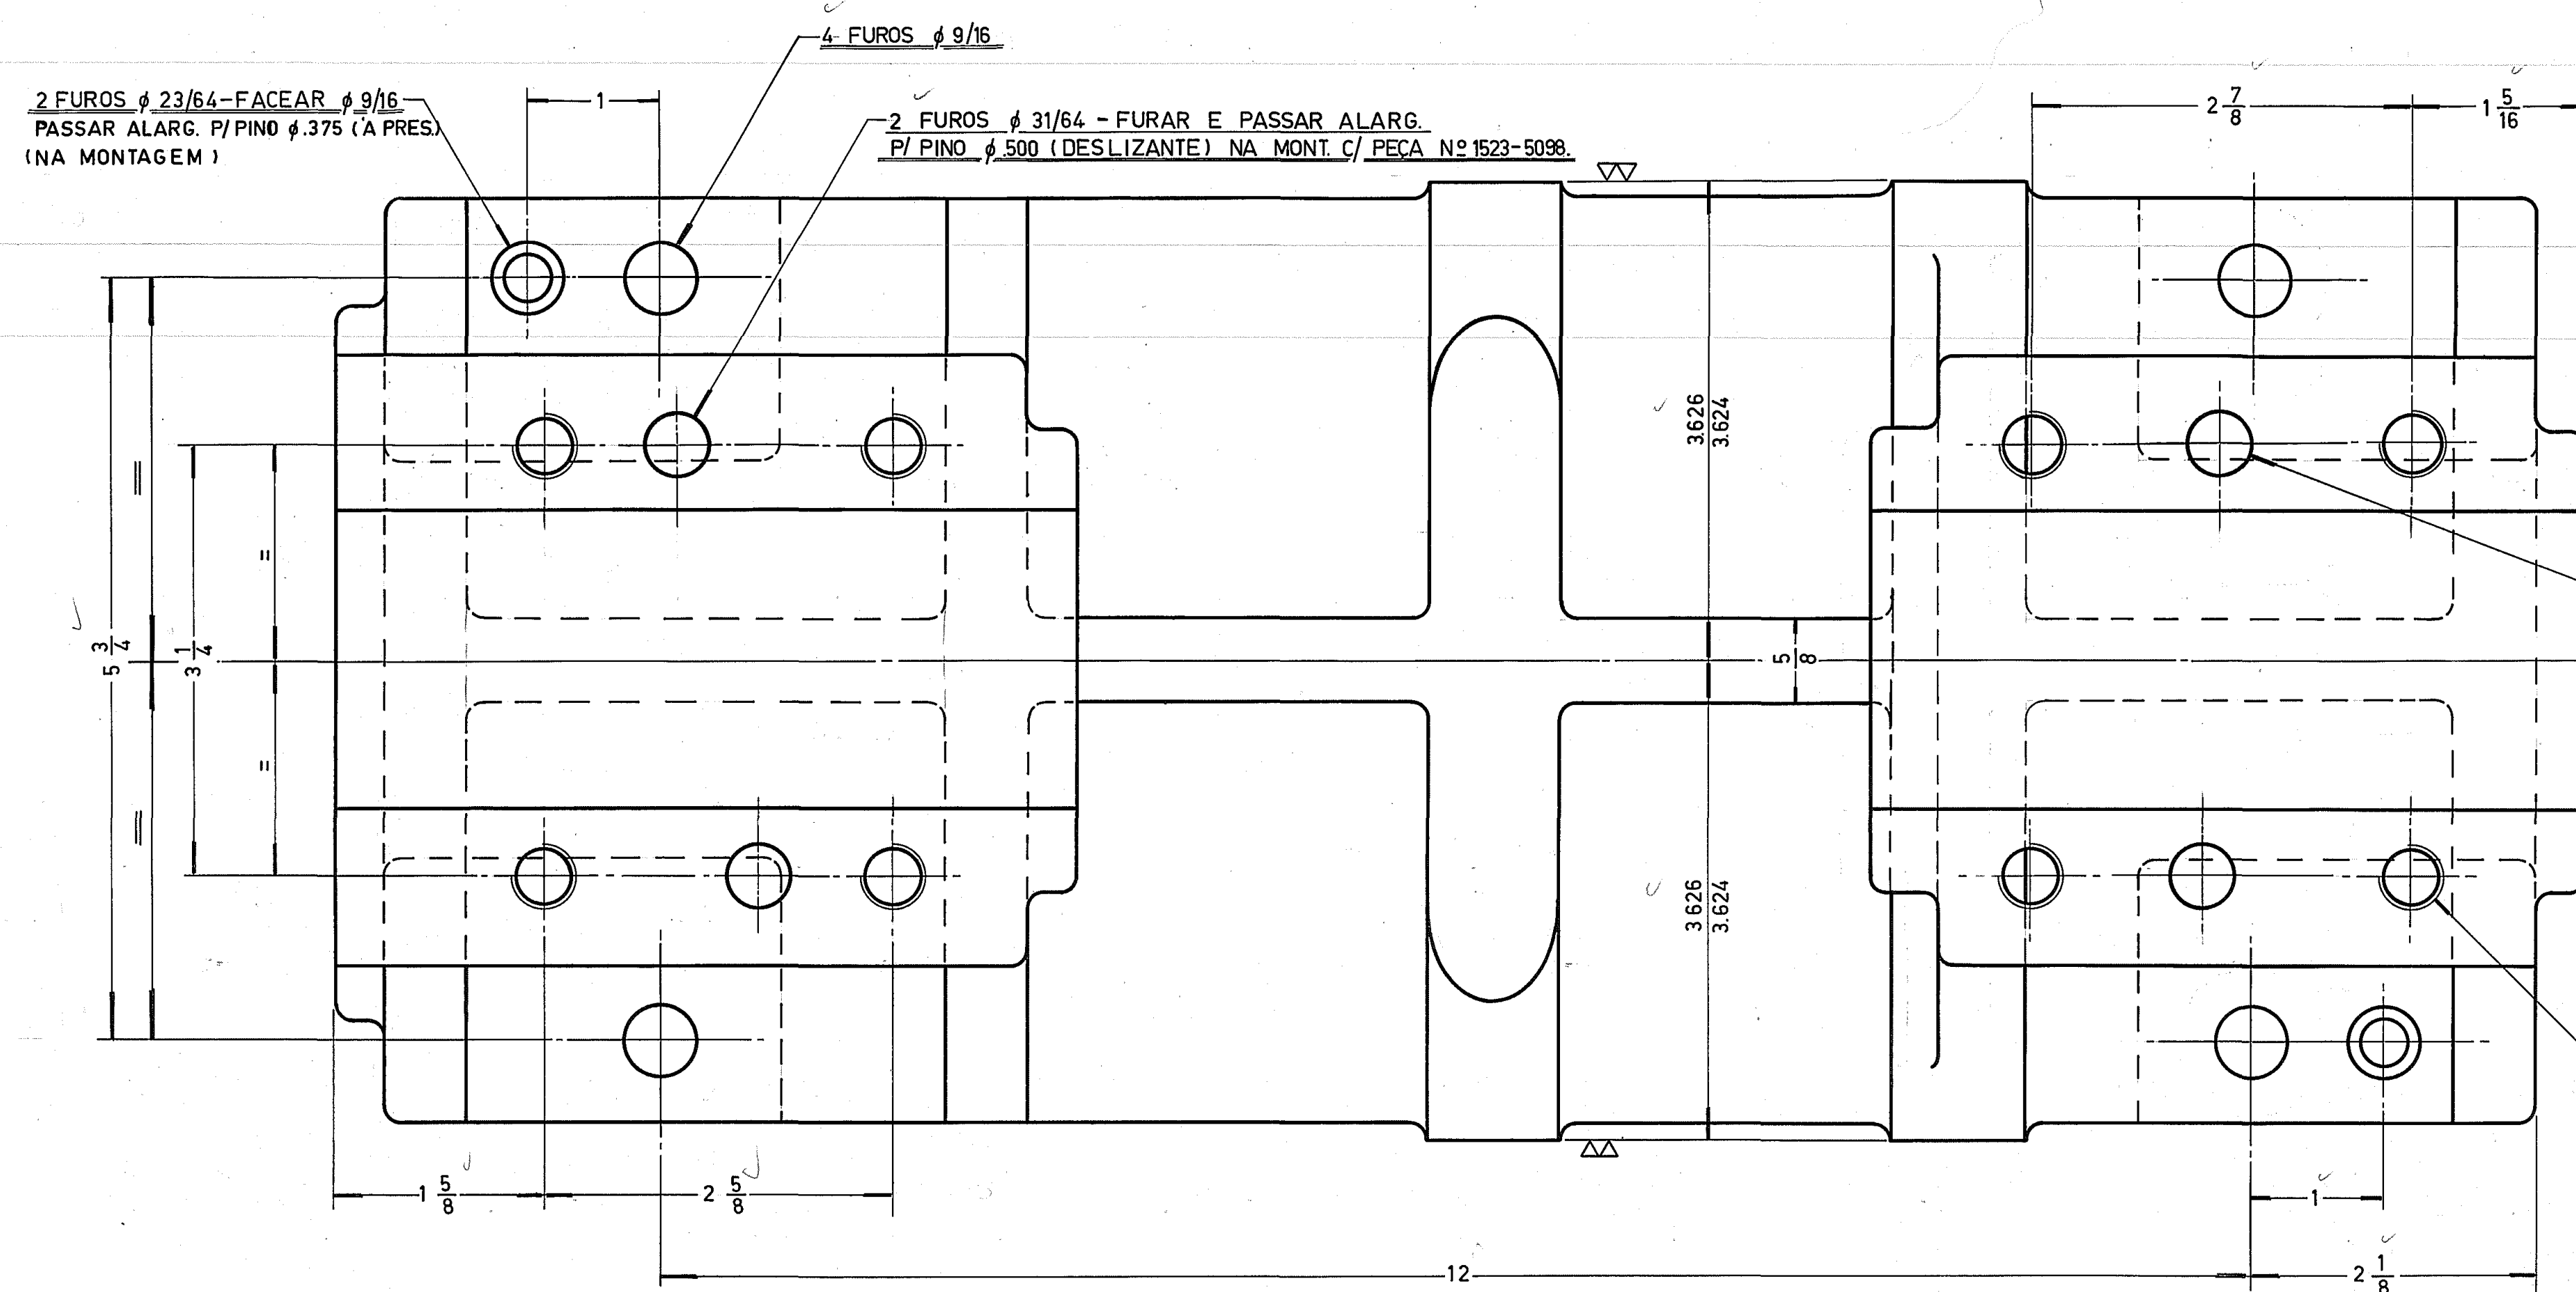
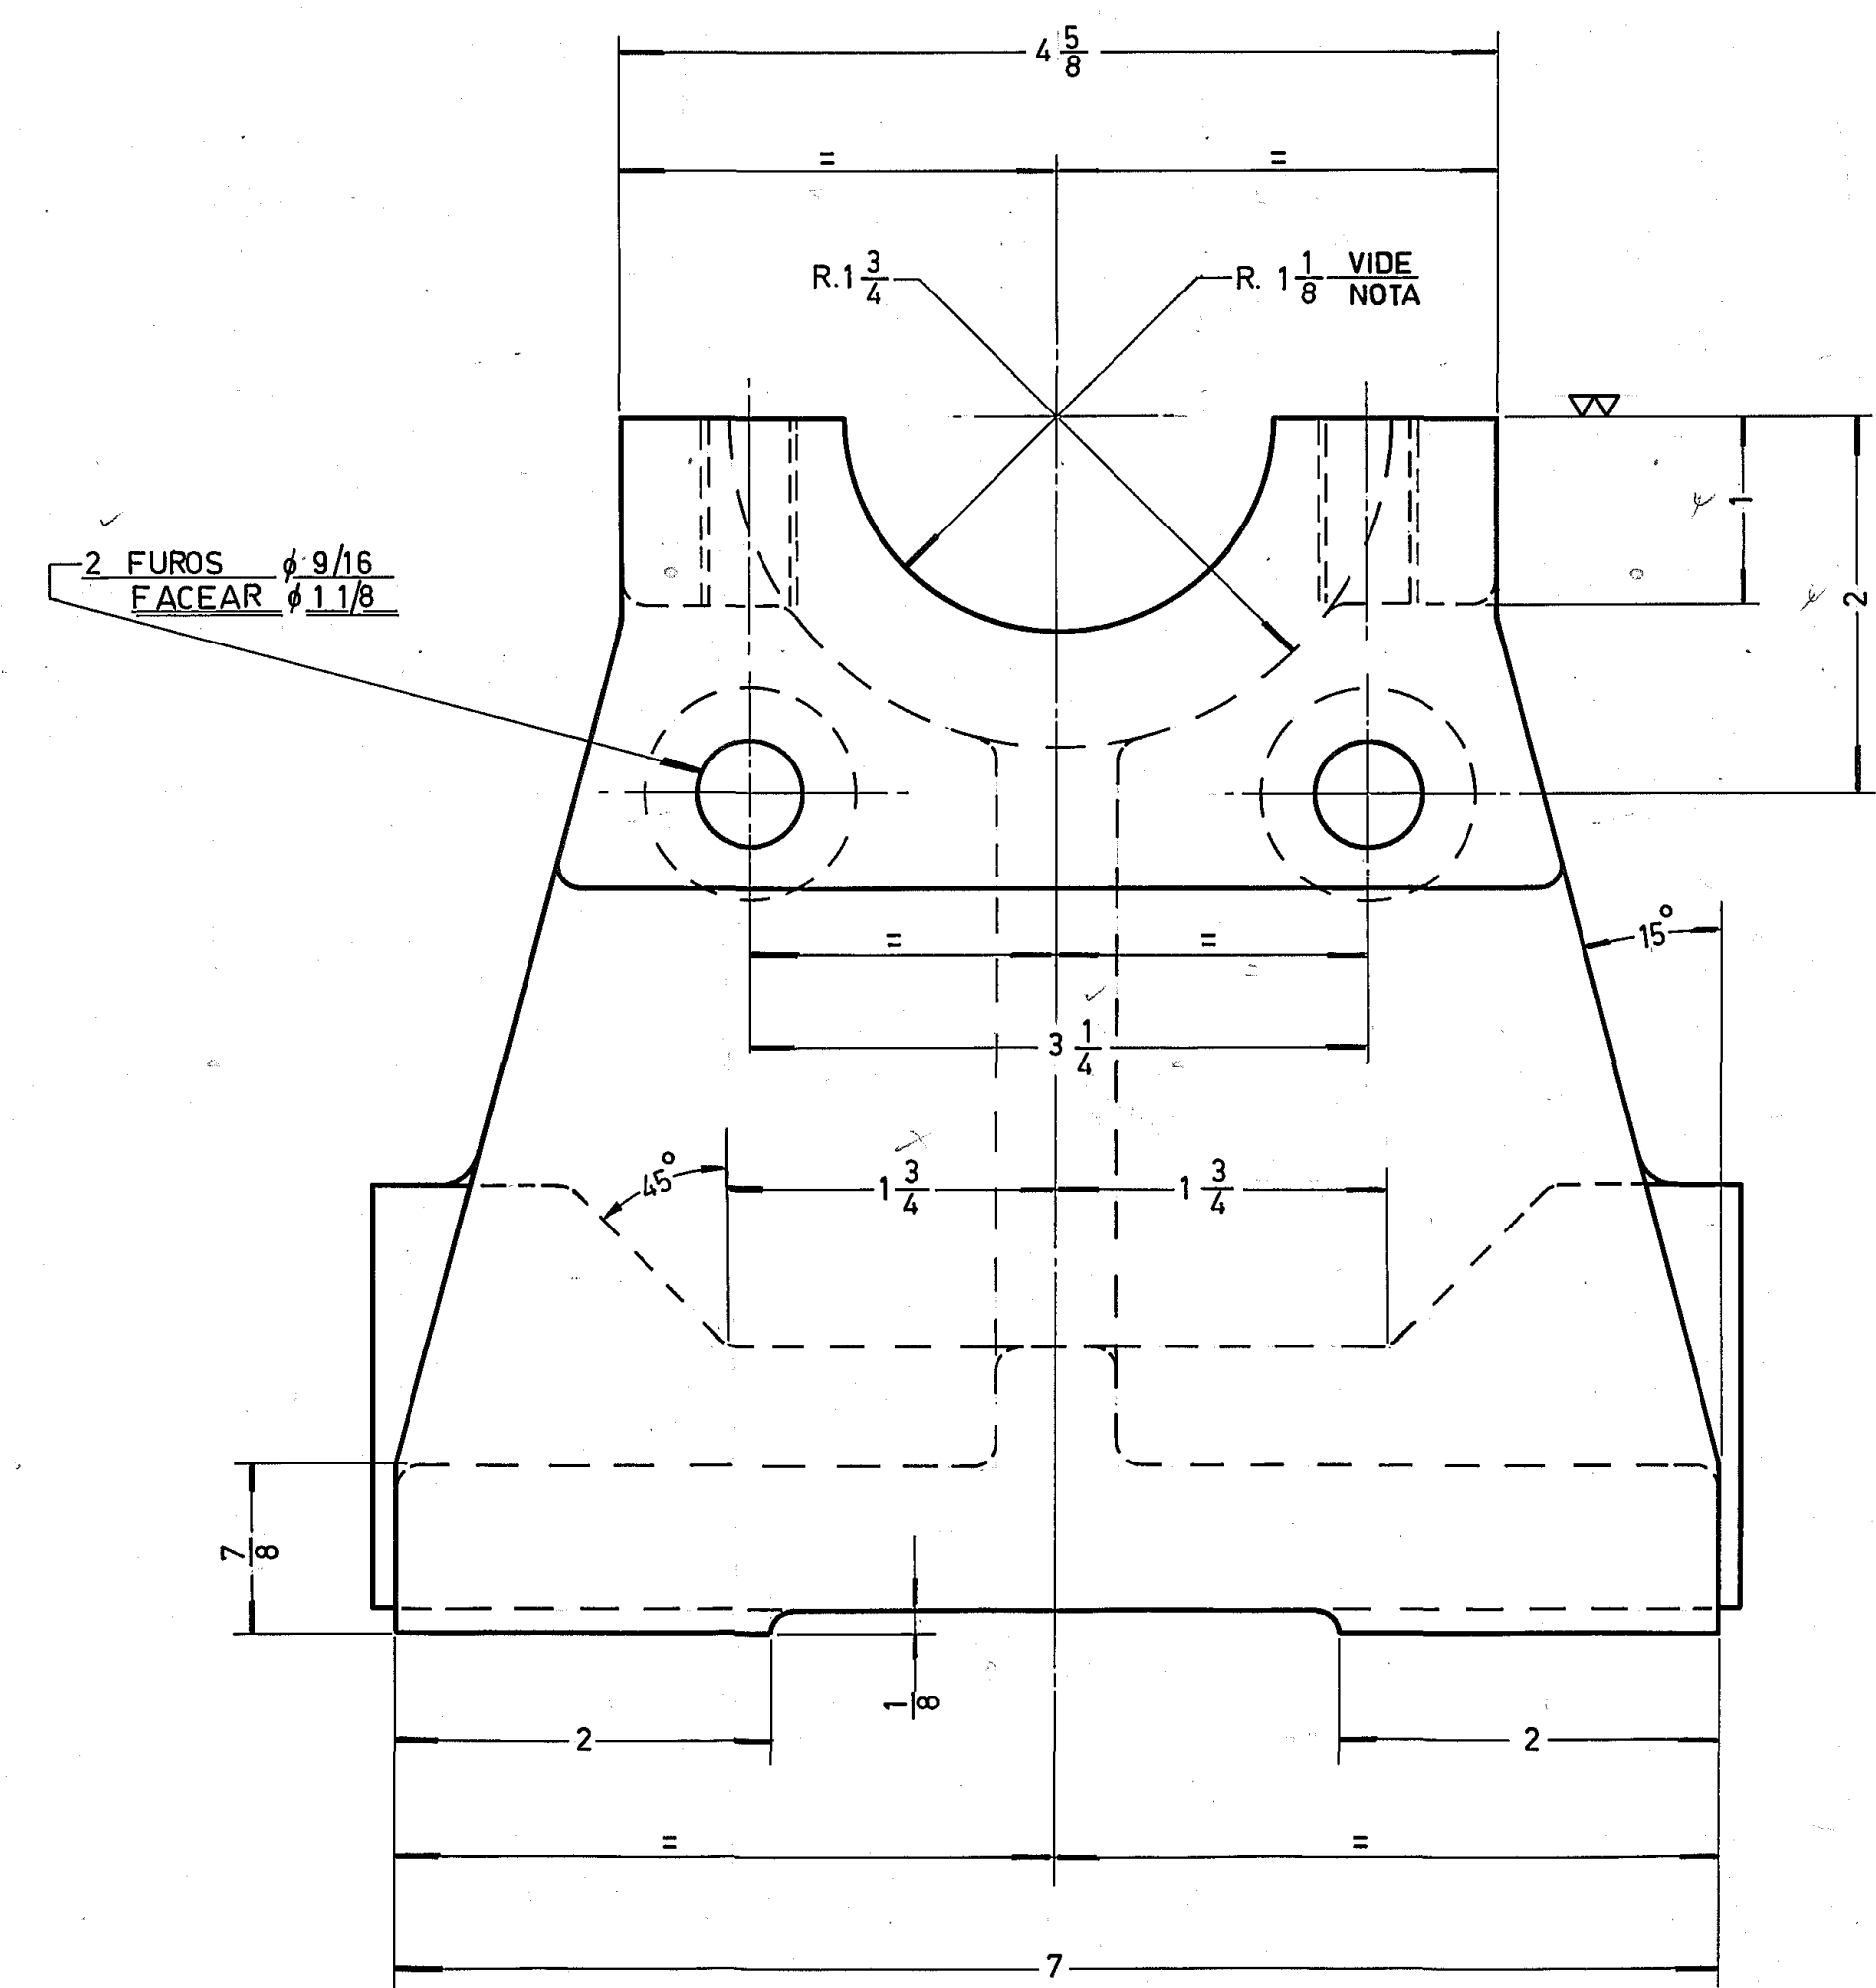


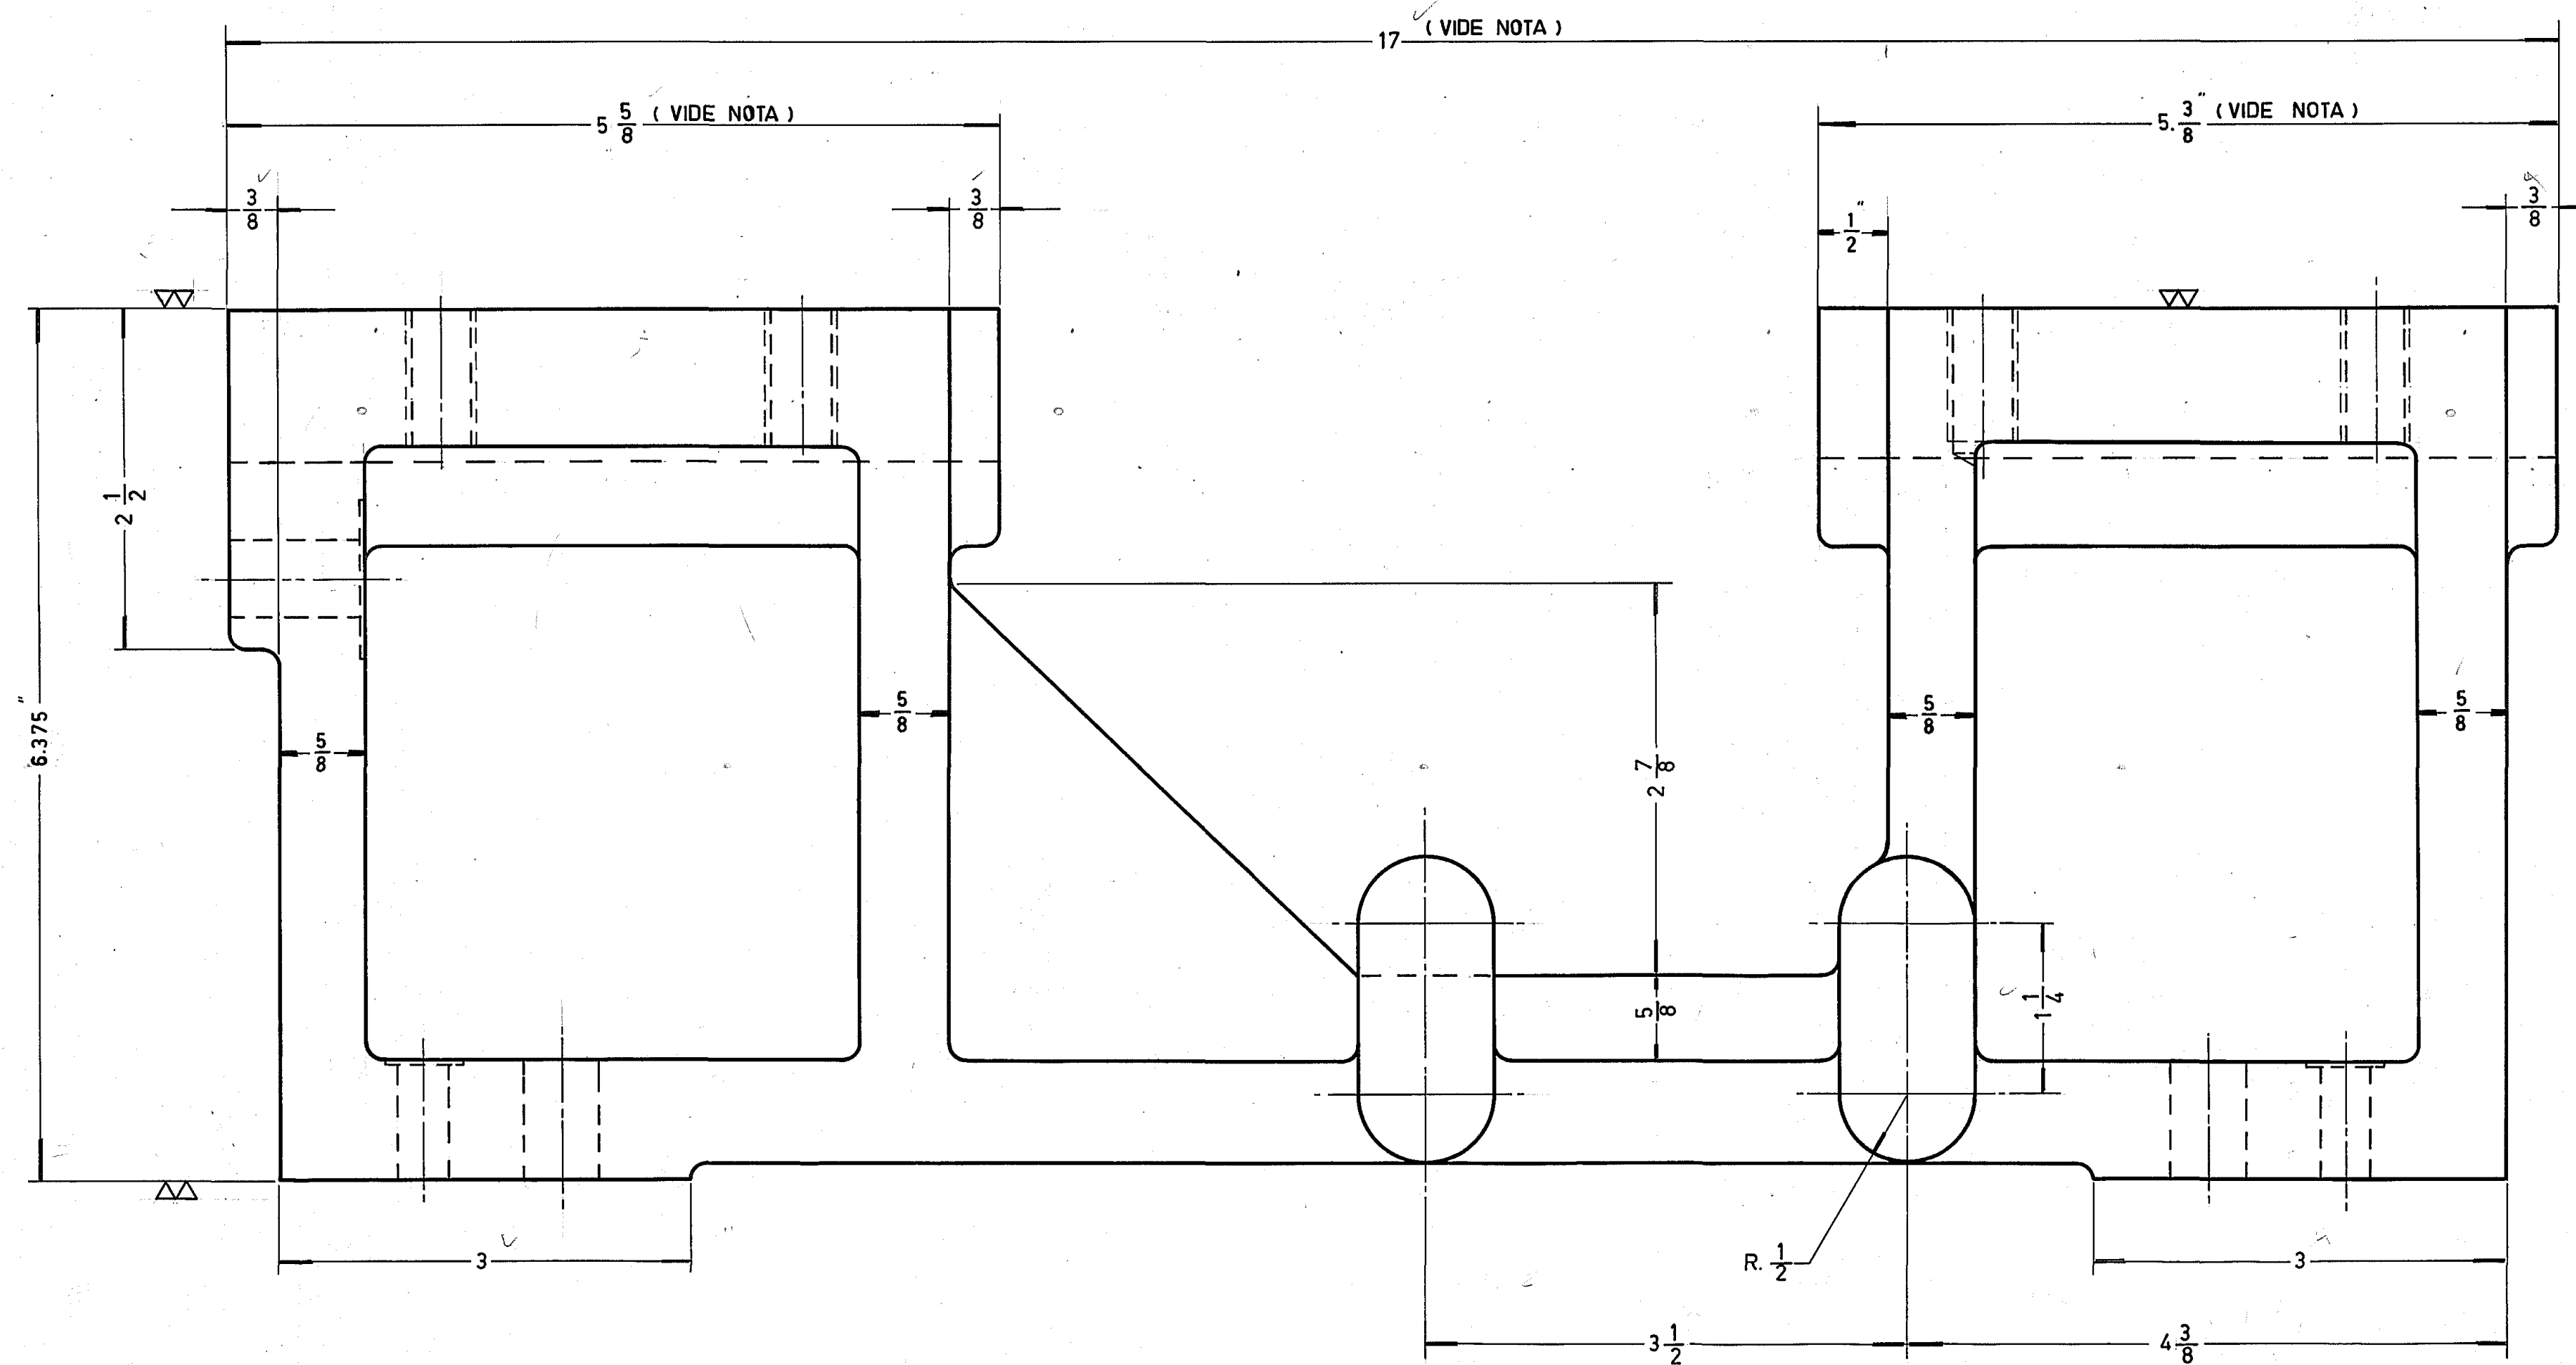

2 FUROS Ø 31/64 - FURAR E PASSAR ALARG.
P/ PINO Ø 500 (DESLIZANTE) NA MONT. C/ PEÇA Nº 191-2195.

8 FUROS Ø 27/64 C/ ROSCA 1/2NC - 13FPP

NOTA:
PEÇA SEMI-TERMINADA. USINAR C/ TAMPAS
Nº 1523-5098 e 191-2195. VIDE DES. 1523-51

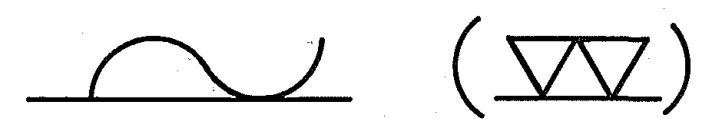

DATA	REVISÃO	ITEM	Qtd. 29-09-86	VIDROS VITON LTDA.	DES. <i>Carvalho</i>
			TOLERÂNCIAS STANDARD PARA SUPERFÍCIES USINADAS SEM TOLERÂNCIA INDICADA	MAT. FERRO FUNDIDO GG 20	VER. <i>Carvalho</i>
			DECIMAL ± 0.05"	N.º DO PROJ. BASE & CAPS	N.º DO PROJ. 1523-51
			FRAÇÃO DE 0" ATÉ 5" ± 1/64 DE 5" ATÉ 24" ± 1/32 ACIMA DE 24" ± 1/16	N.º DA PEÇA BASE	N.º DA PEÇA 1523-5095
				ESCALA 1:1	N.º DO DES.