

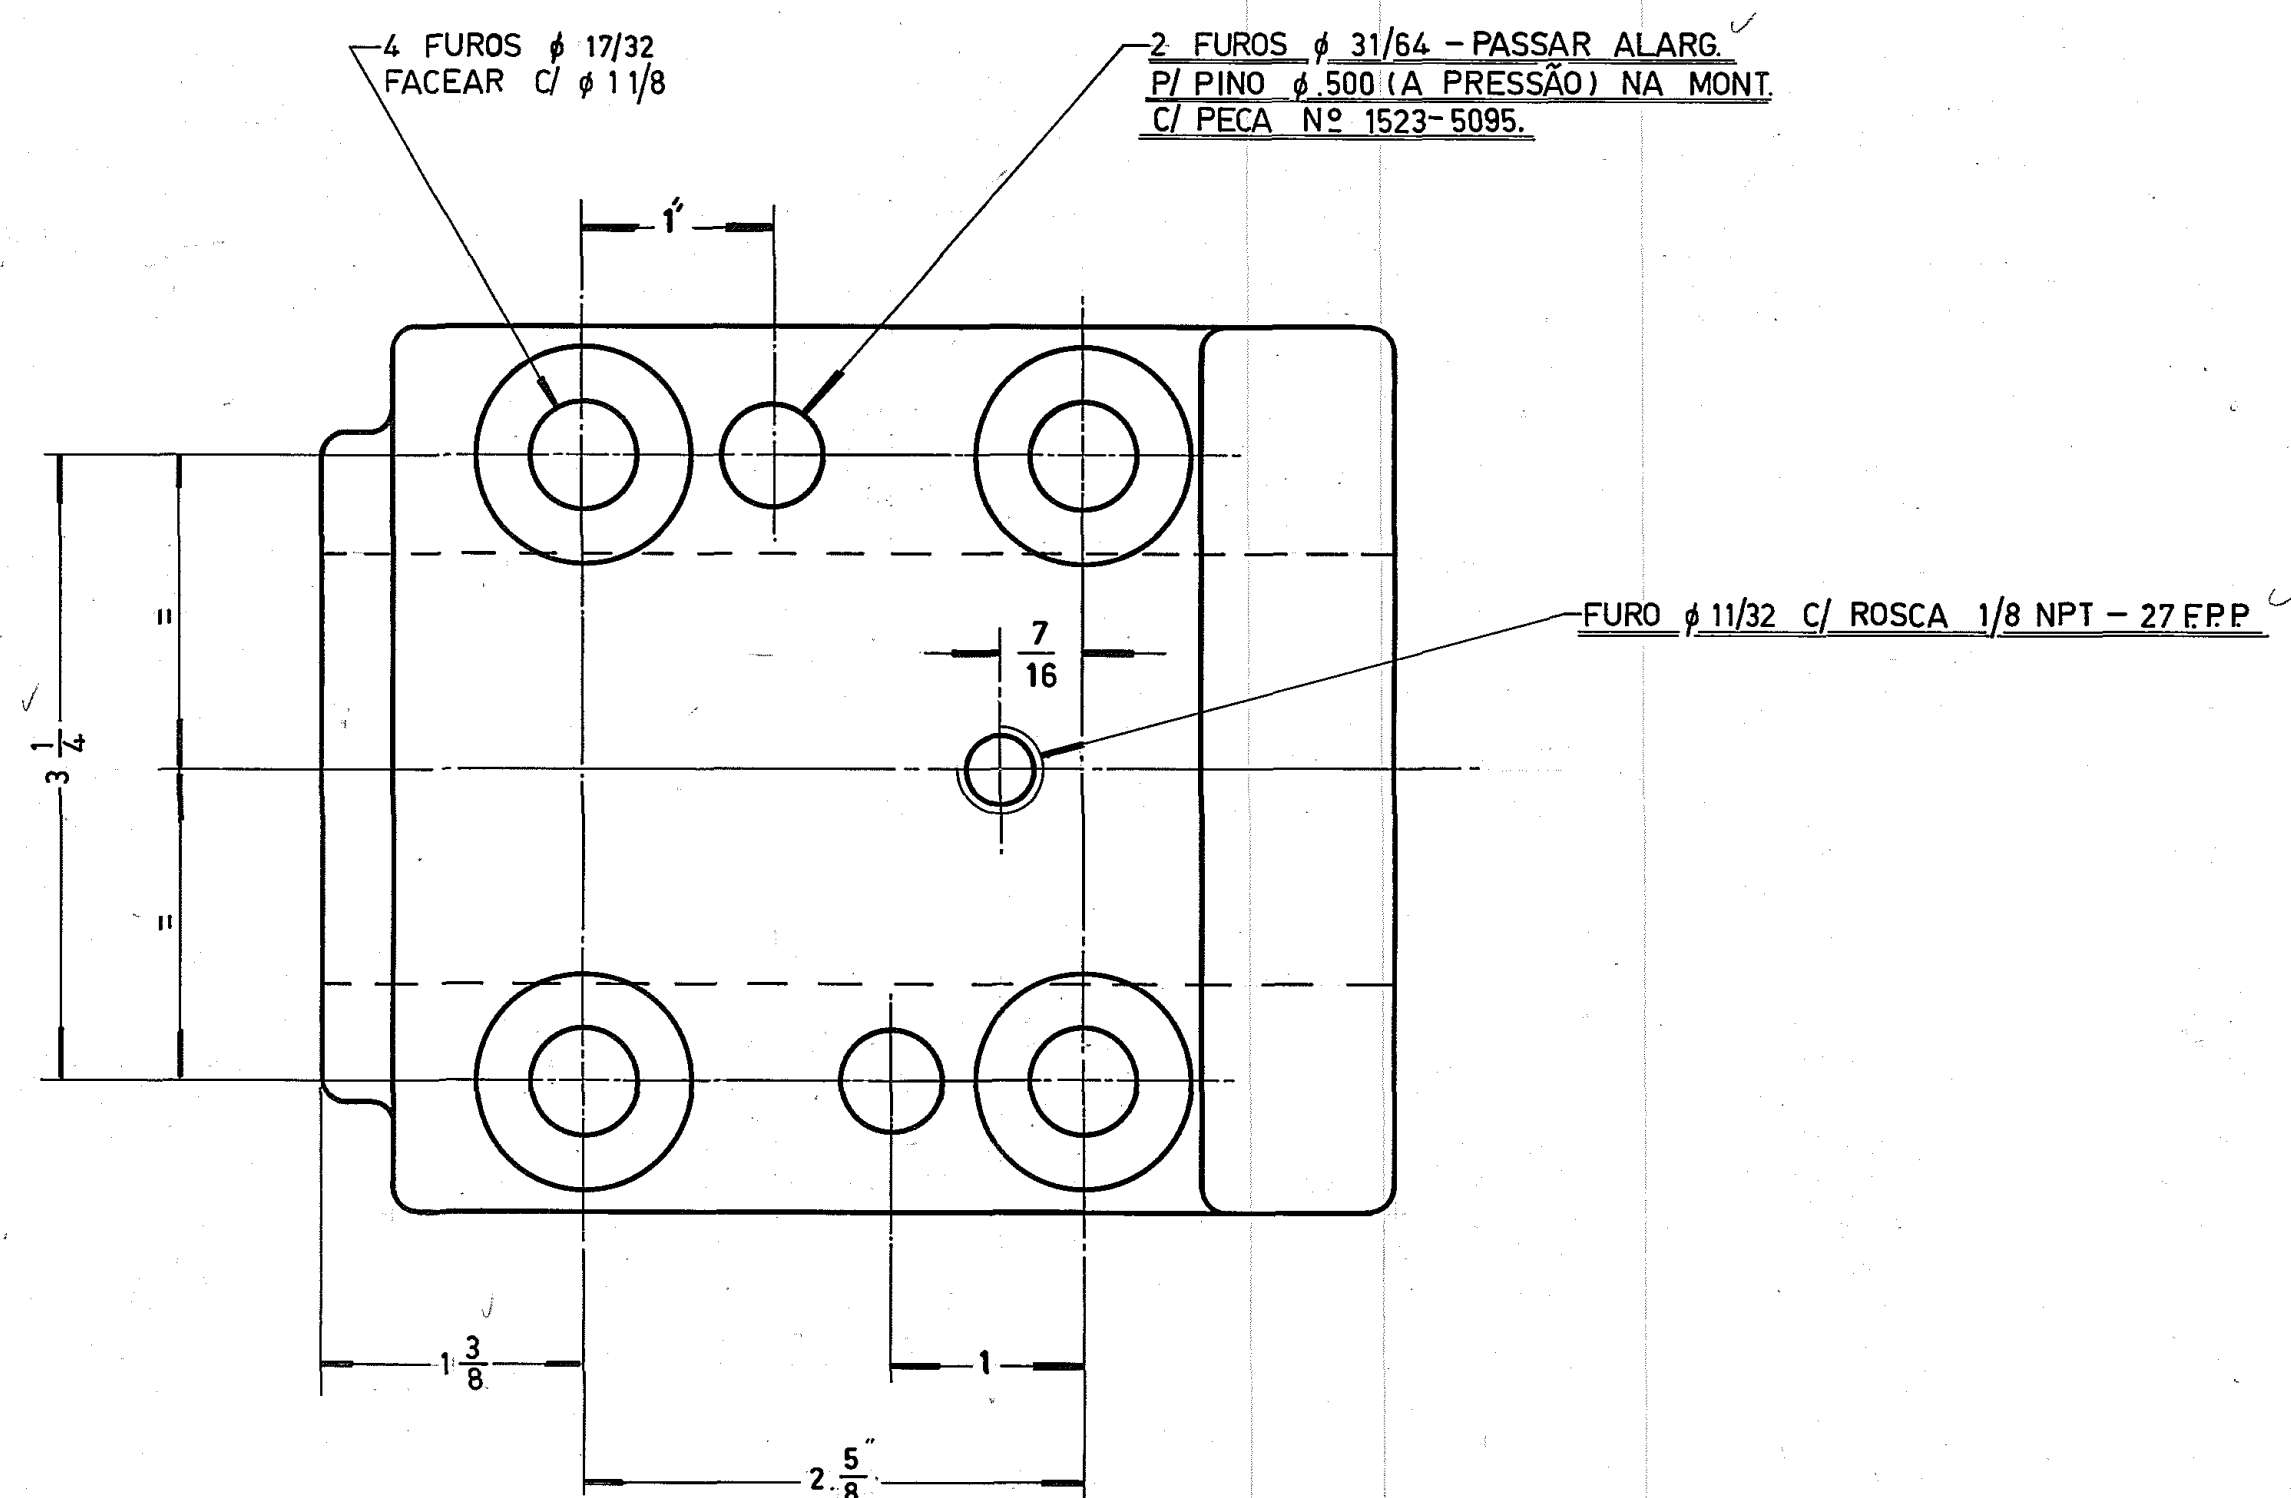


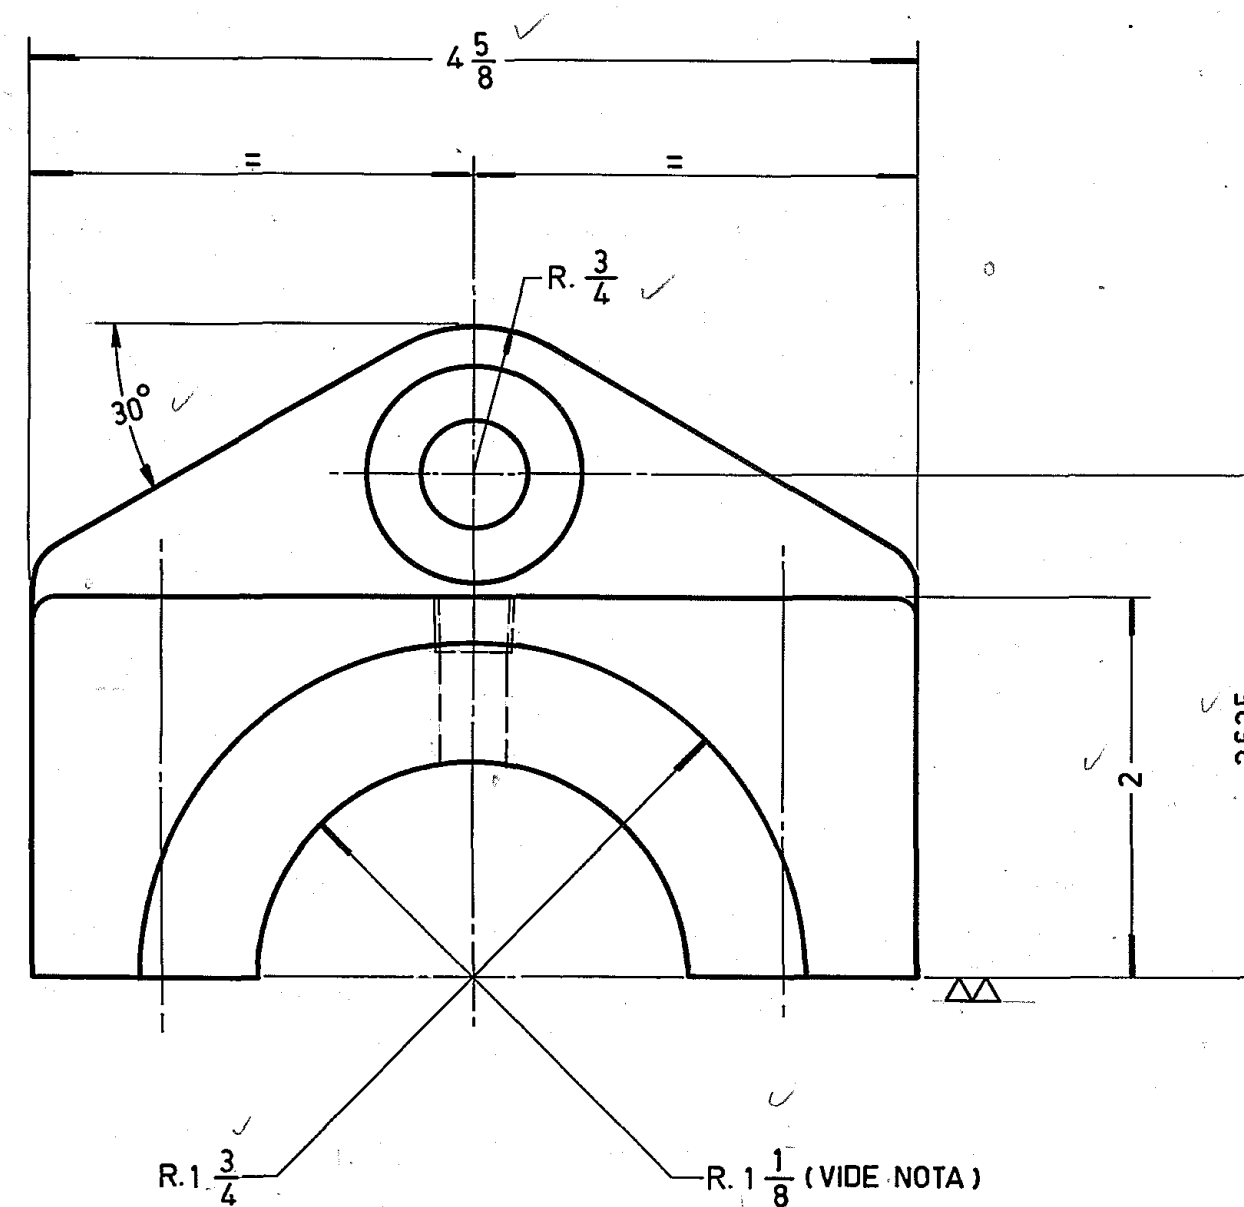

**NOTA:**  
PEÇA SEMI-TERMINADA-USINAR COM  
A BASE - VIDE DES. Nº 1523-51

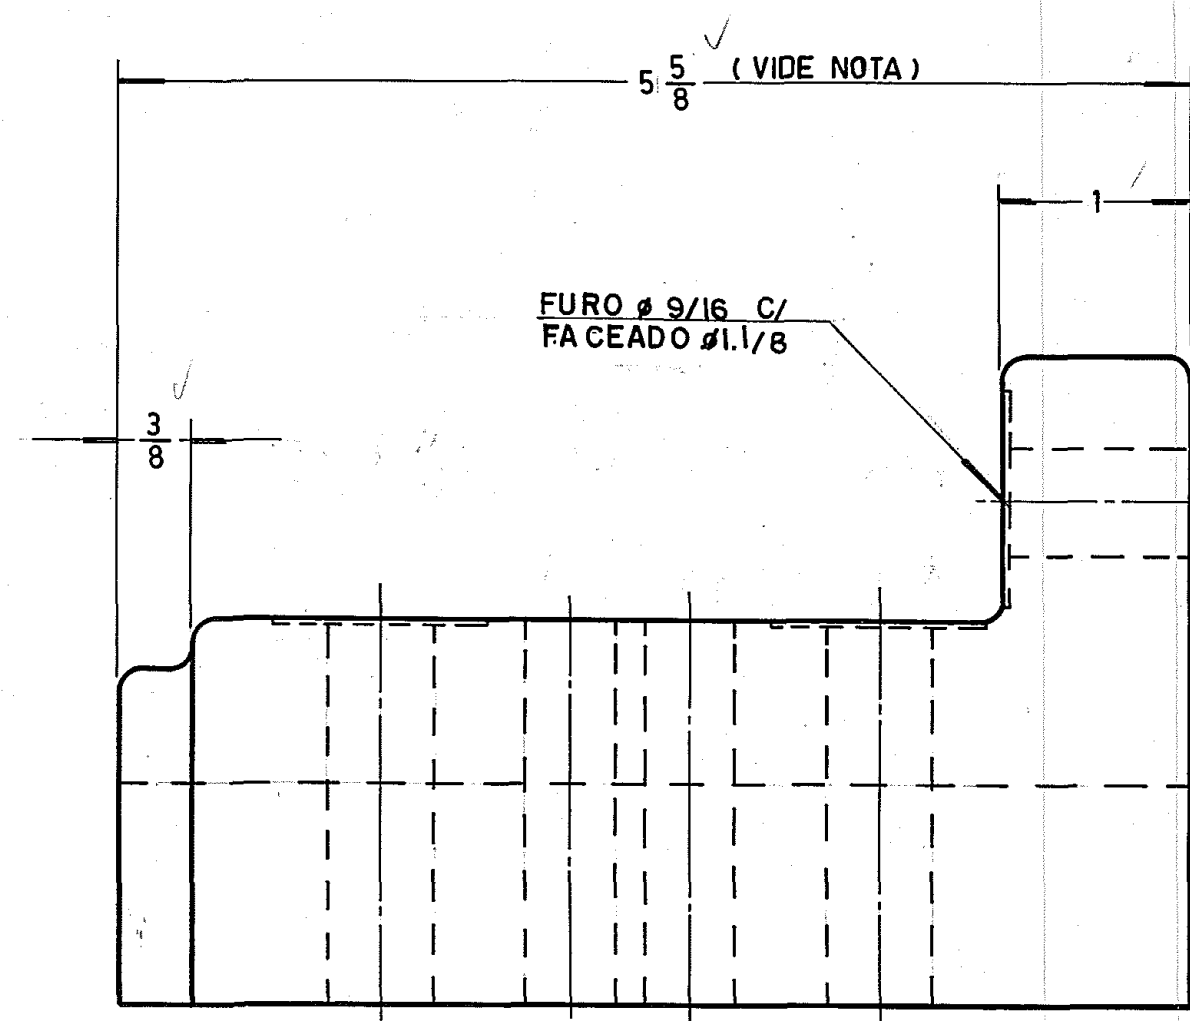

|      |         |      |                                                                                 |                       |
|------|---------|------|---------------------------------------------------------------------------------|-----------------------|
| DATA | REVISÃO | ITEM | DATA: 06-10-86                                                                  | DES. J. Carlos        |
|      |         |      | TOLERANCIAS STANDARD<br>PARA SUPERFICIES<br>USINADAS SEM<br>TOLERANCIA INDICADA | VER. J. Carlos        |
|      |         |      | DESMAL ± 0.05"                                                                  | APROV. J. Carlos      |
|      |         |      | FRAÇÃO                                                                          | N.º DO CONJ. 1523-51  |
|      |         |      | DE 0" ATÉ 5" ± 1/64                                                             | N.º DA PEÇA 1523-5098 |
|      |         |      | DE 5" ATÉ 24" ± 1/32                                                            | N.º DO DES.           |
|      |         |      | ACIMA DE 24" ± 1/16                                                             |                       |
|      |         |      | ESCALA 1:1                                                                      |                       |
|      |         |      | TERM.                                                                           |                       |
|      |         |      | VIDROS VITON LTDA.                                                              |                       |
|      |         |      | MAT. FERRO FUNDIDO GG-20                                                        |                       |
|      |         |      | N.º DA PEÇA                                                                     |                       |
|      |         |      | BASE & CAPS                                                                     |                       |
|      |         |      | CAP                                                                             |                       |