
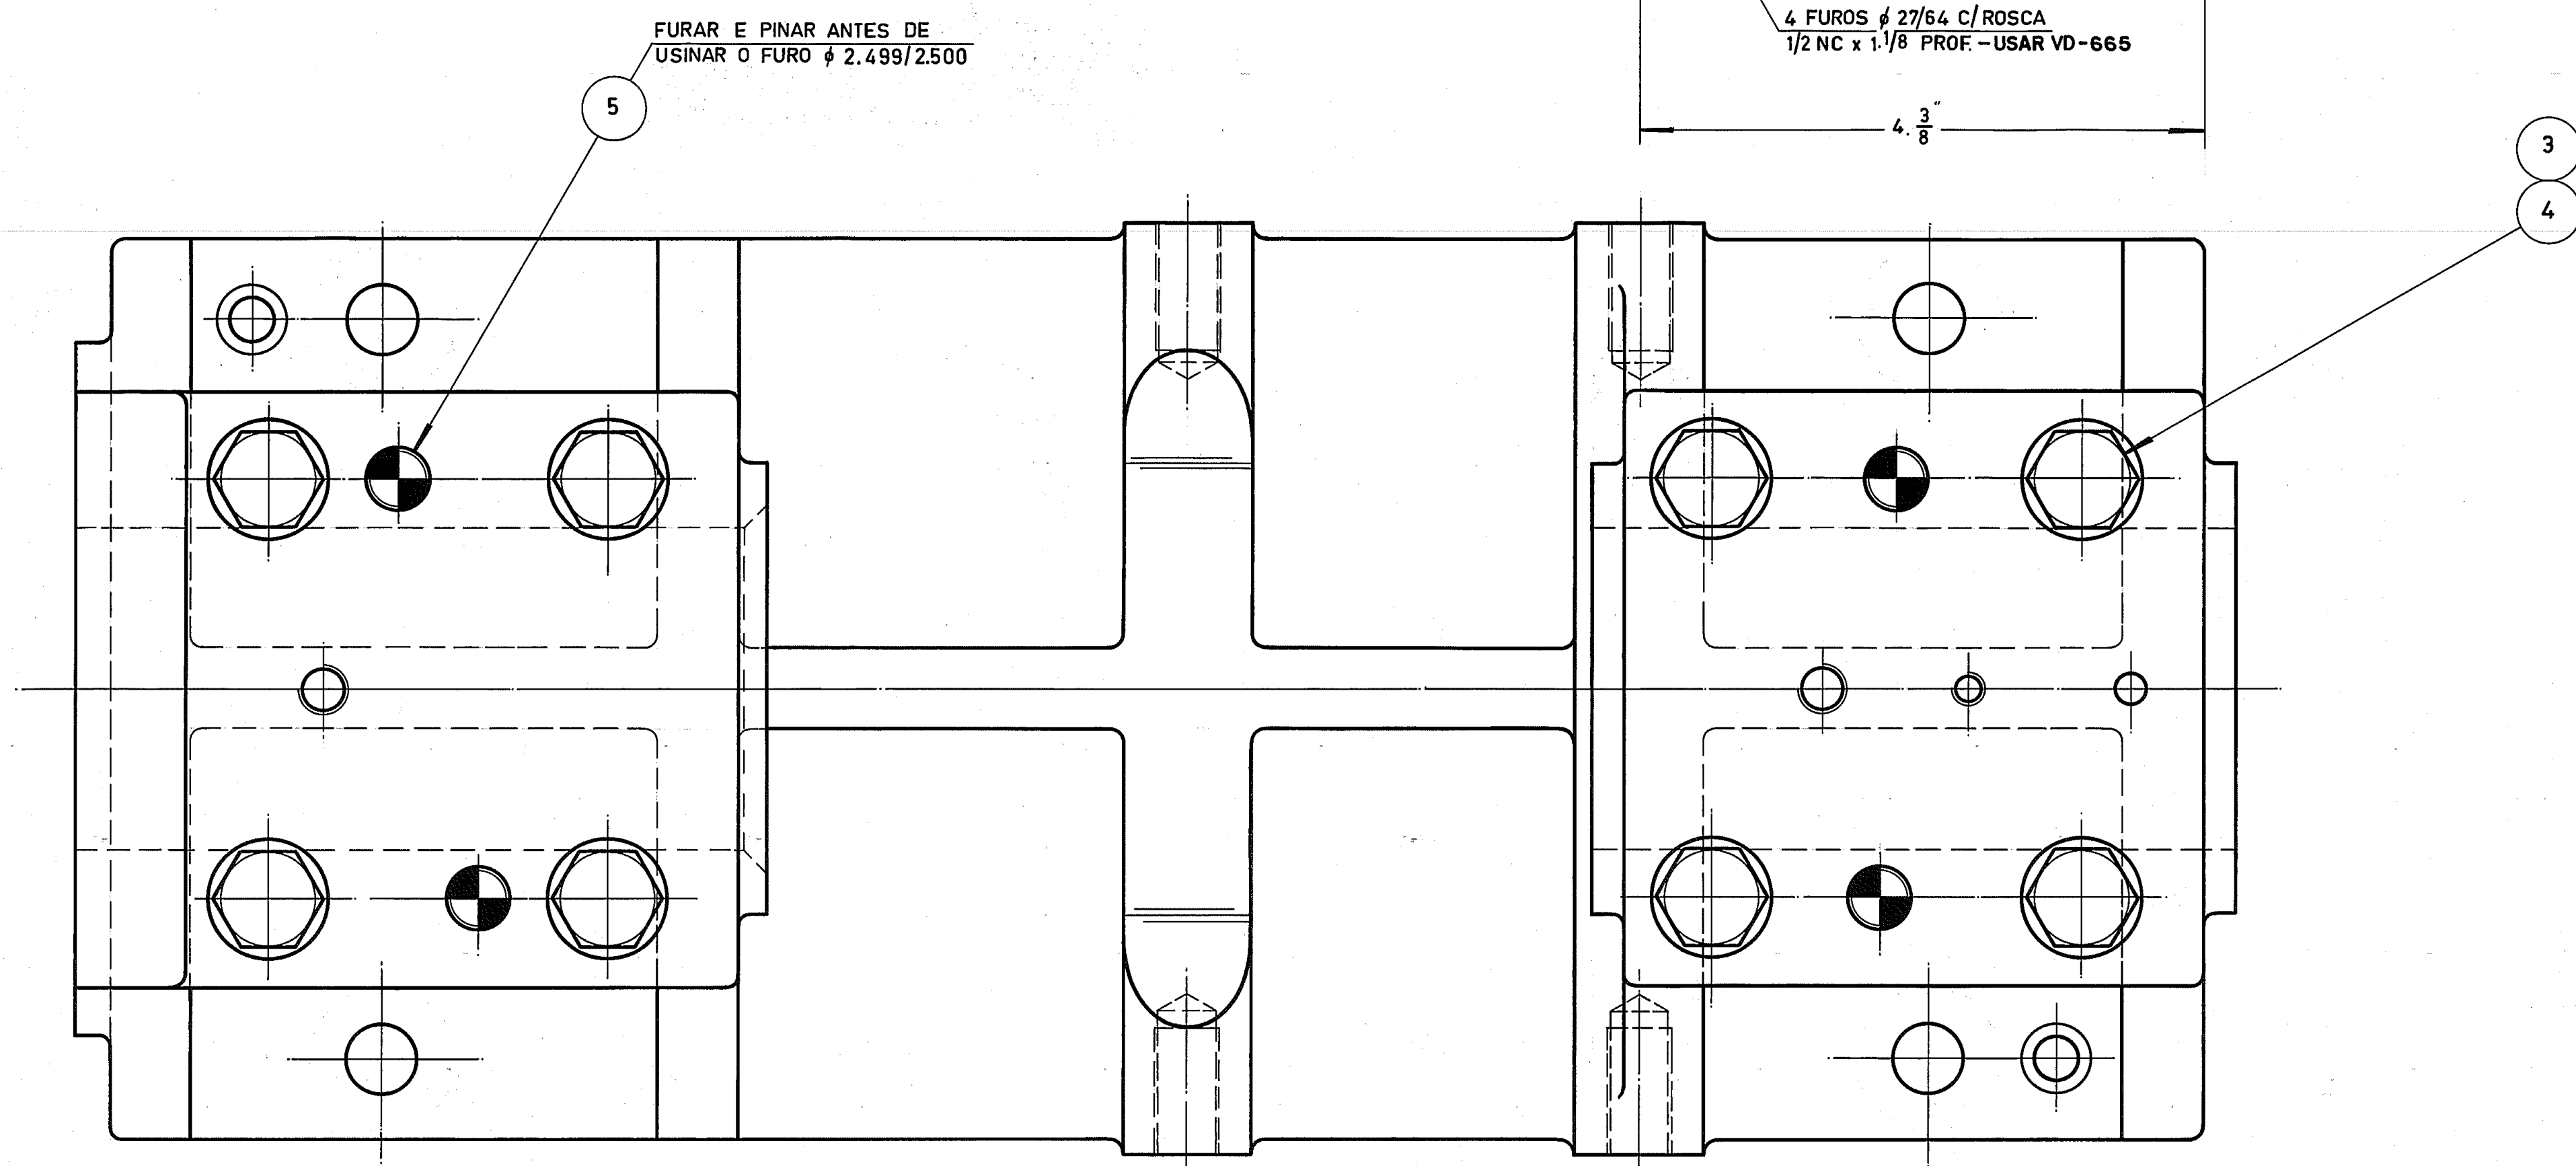


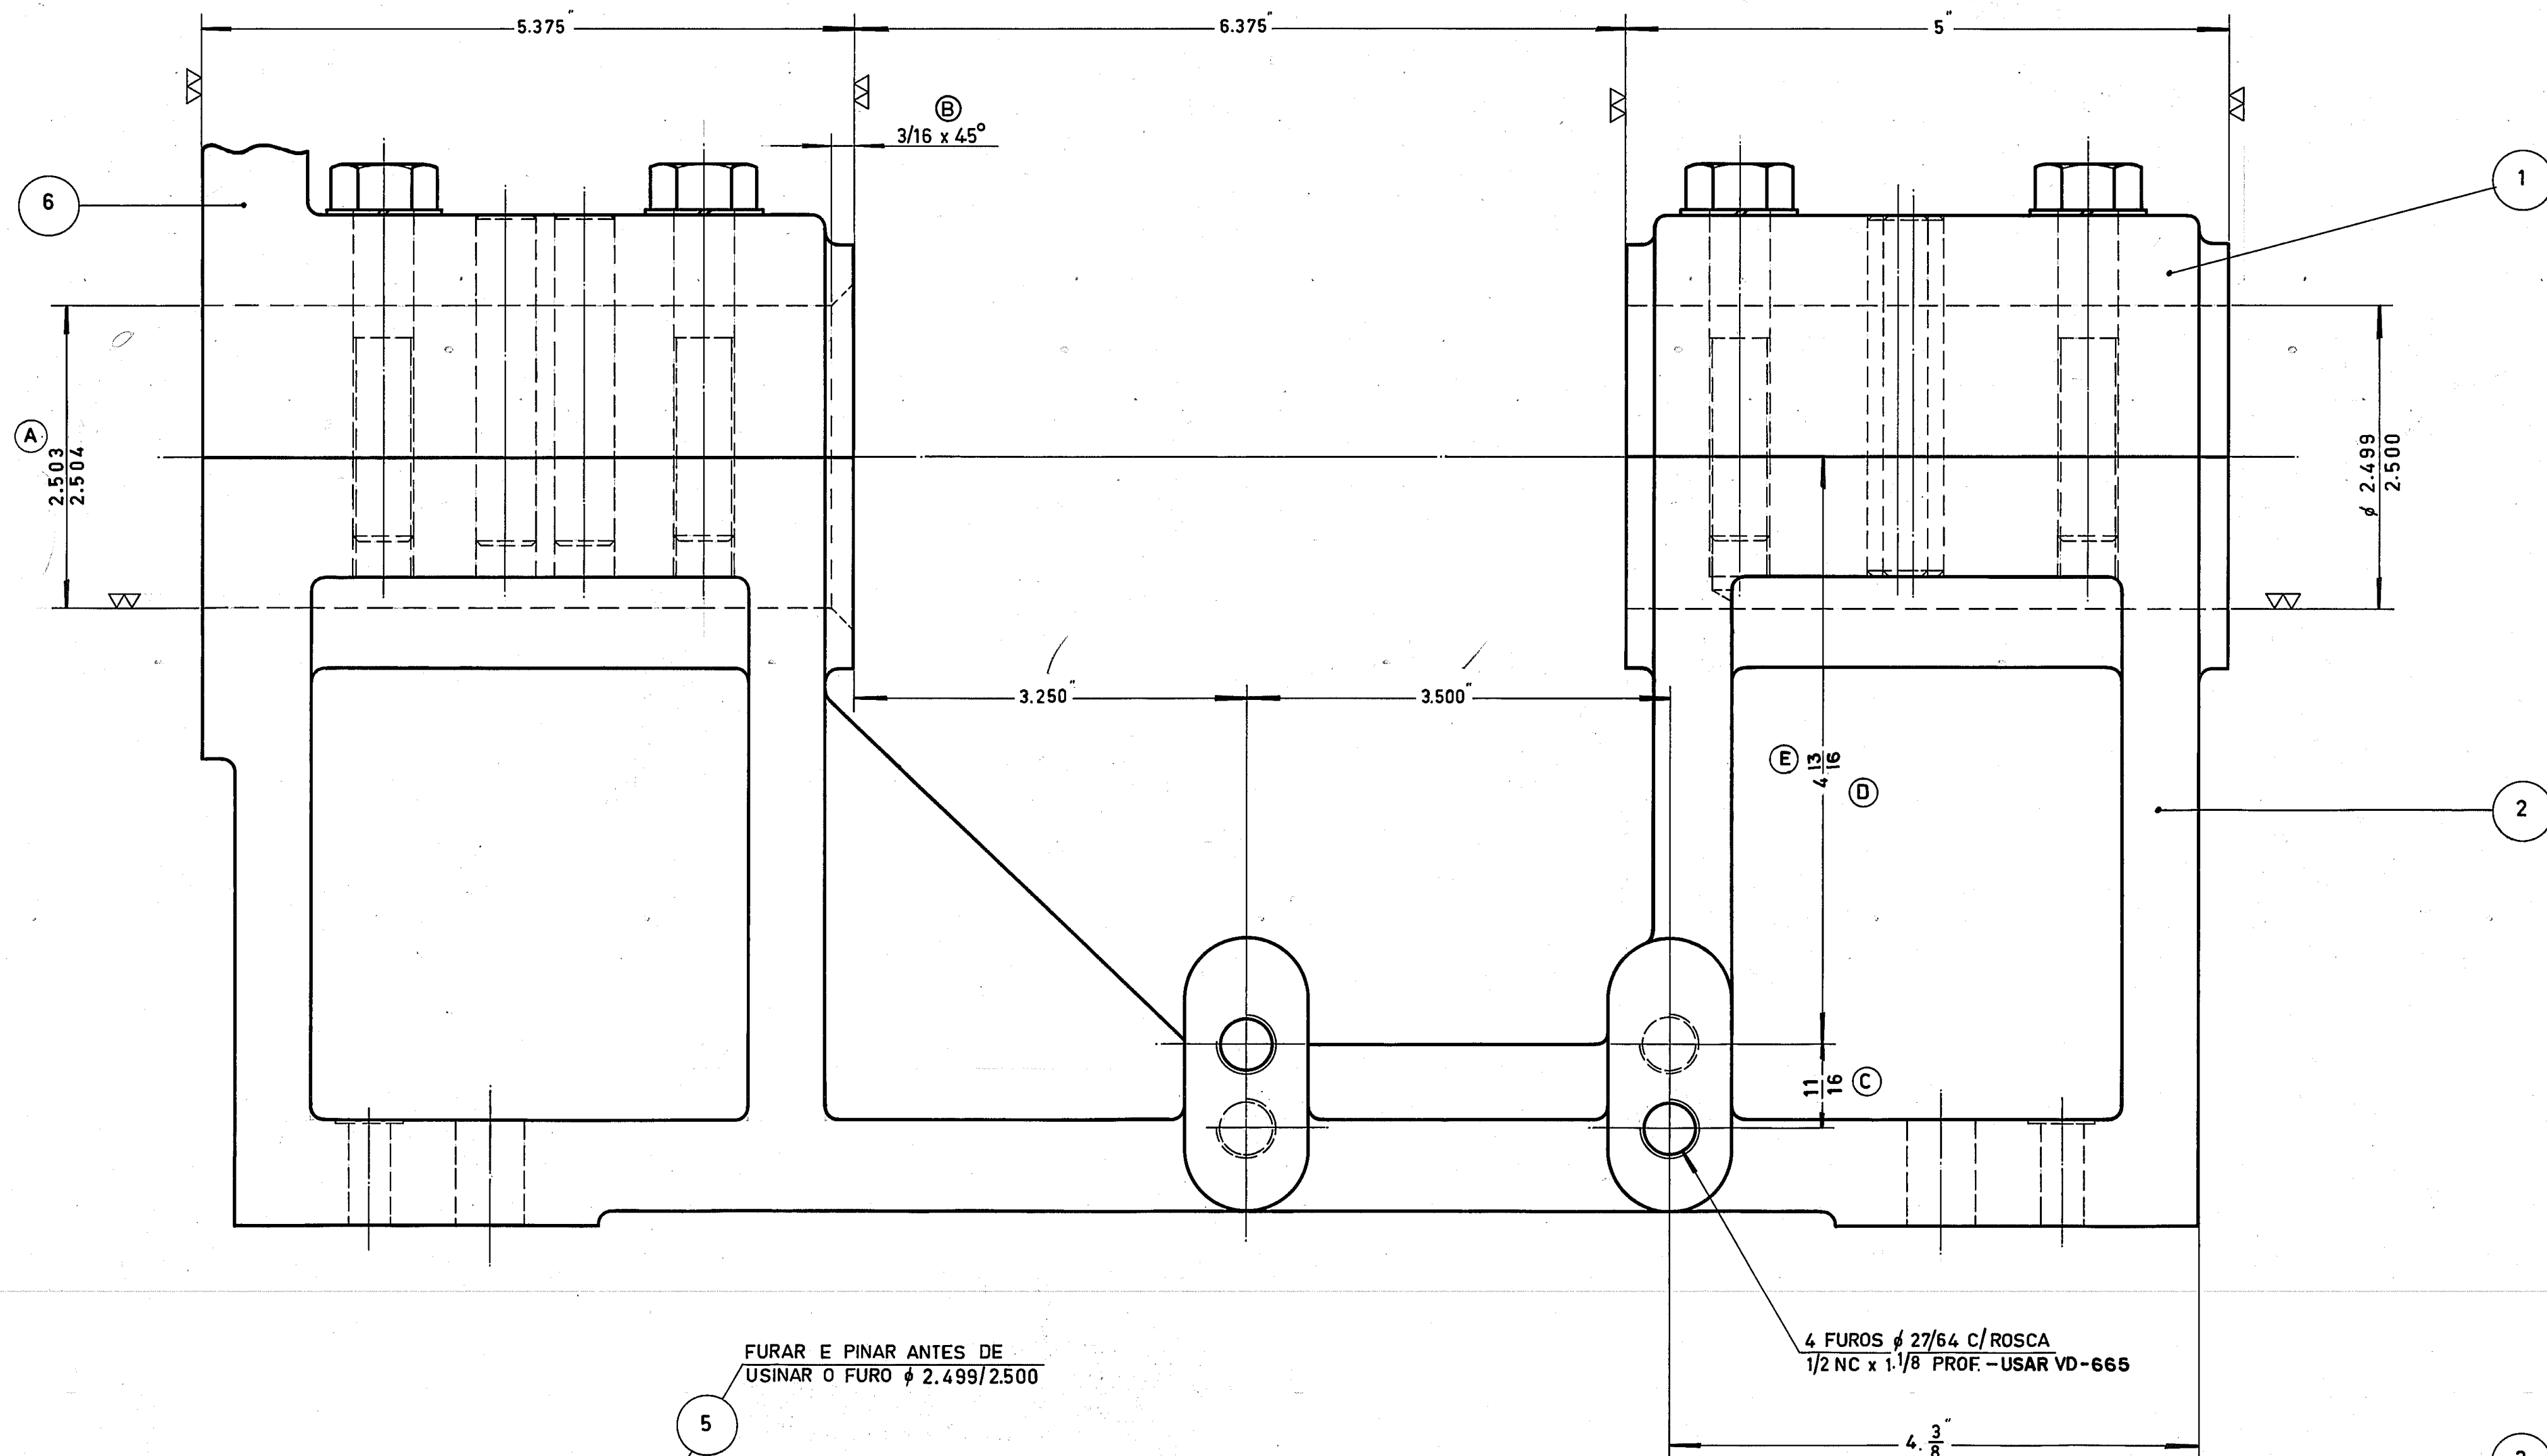

E	ERA: 4.7/8	Ricardo 21-02-95
D	ERA: 4.875	Adilson 31-01-89
C	ERA: .625	Adilson 31-01-89
B	ACRESC. CHANFRO	Adilson 24-09-87
A	ERA FURO Ø 2.499 2.500	Adilson 31-08-87
MOD	MODIFICAÇÕES	DATA

1	6	CAP	1523-5098	F. FUND.	
4	5	PINO DE GUIA	COMERCIAL	AÇO PRATA	Ø 1/2 x 2 3/4"
8	4	PARAF. CAB. SEXT.	COMERCIAL	AÇO	1/2 NC x 2 3/4"
8	3	ARRUELA DE PRESSAO	COMERCIAL	AÇO	Ø 1/2"
1	2	BASE	1523-5095	F. FUND.	
1	1	CAP	191-2195	F. FUND.	
QTD.	POS.	DENOMINAÇÃO	PEÇA Nº	MATERIAL	OBS.
1	GR. Nº	VIDROS VITON LTDA.			DES. VER. DATA 07-10-86
DESCRIÇÃO DO GRUPO	MAT:	MANUAL DIFFERENTIAL			N.º DO CORN. 1523-D-9
	NOME DO CORN.	BASE & CAPS			N.º DA PEÇA 1523-51
	TRAJ. TERM.	ESCALA 1:1			N.º DO DES.