
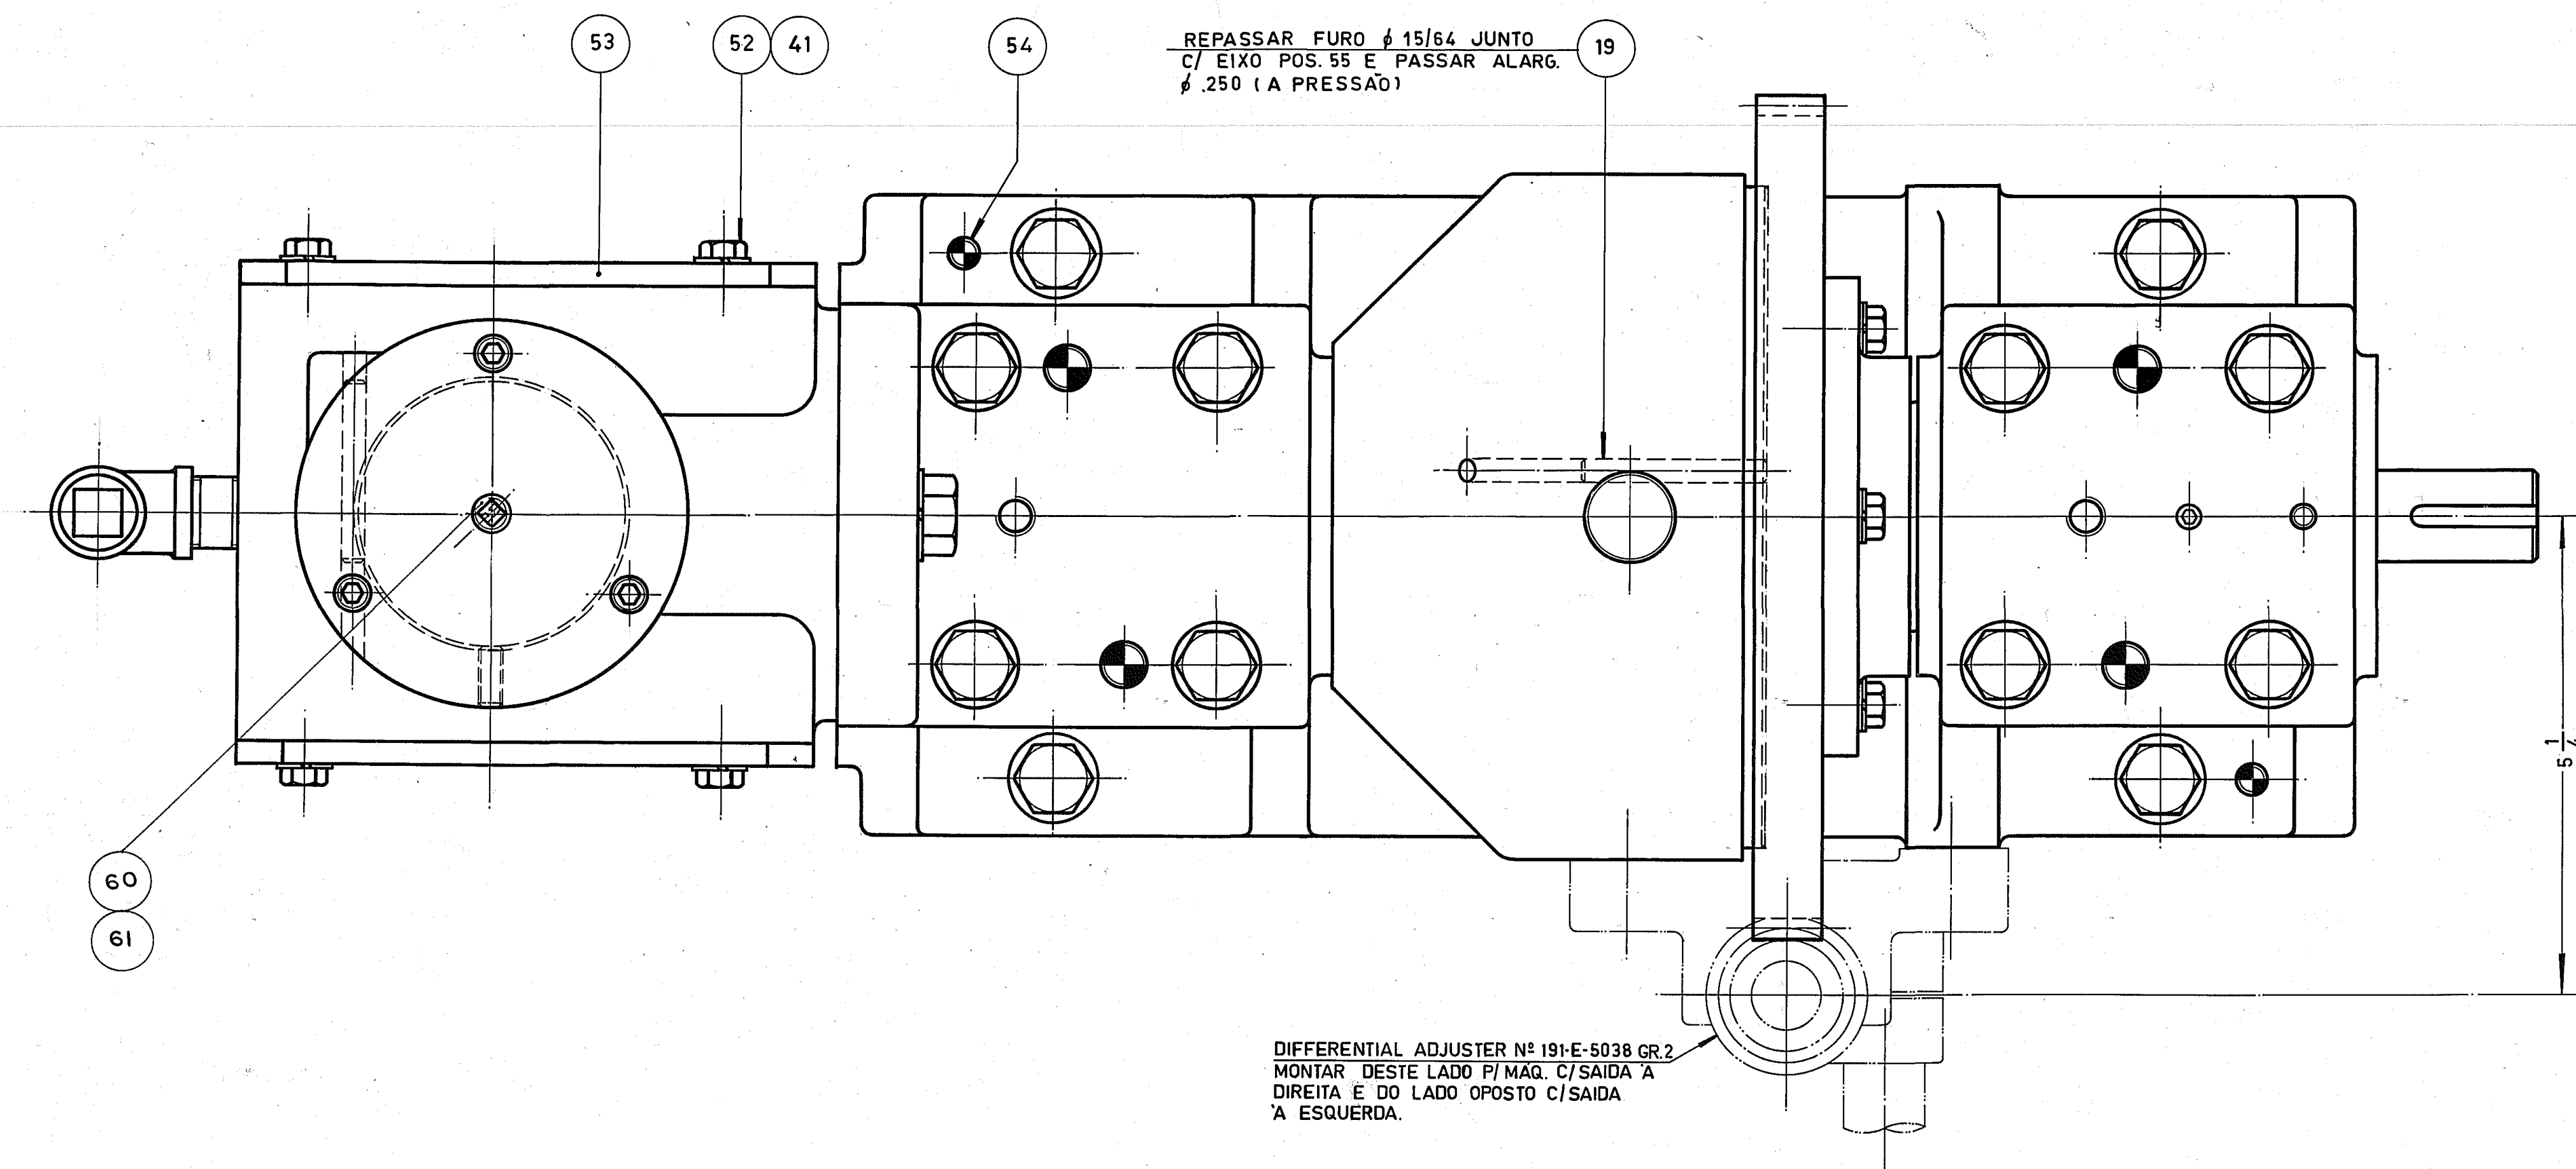


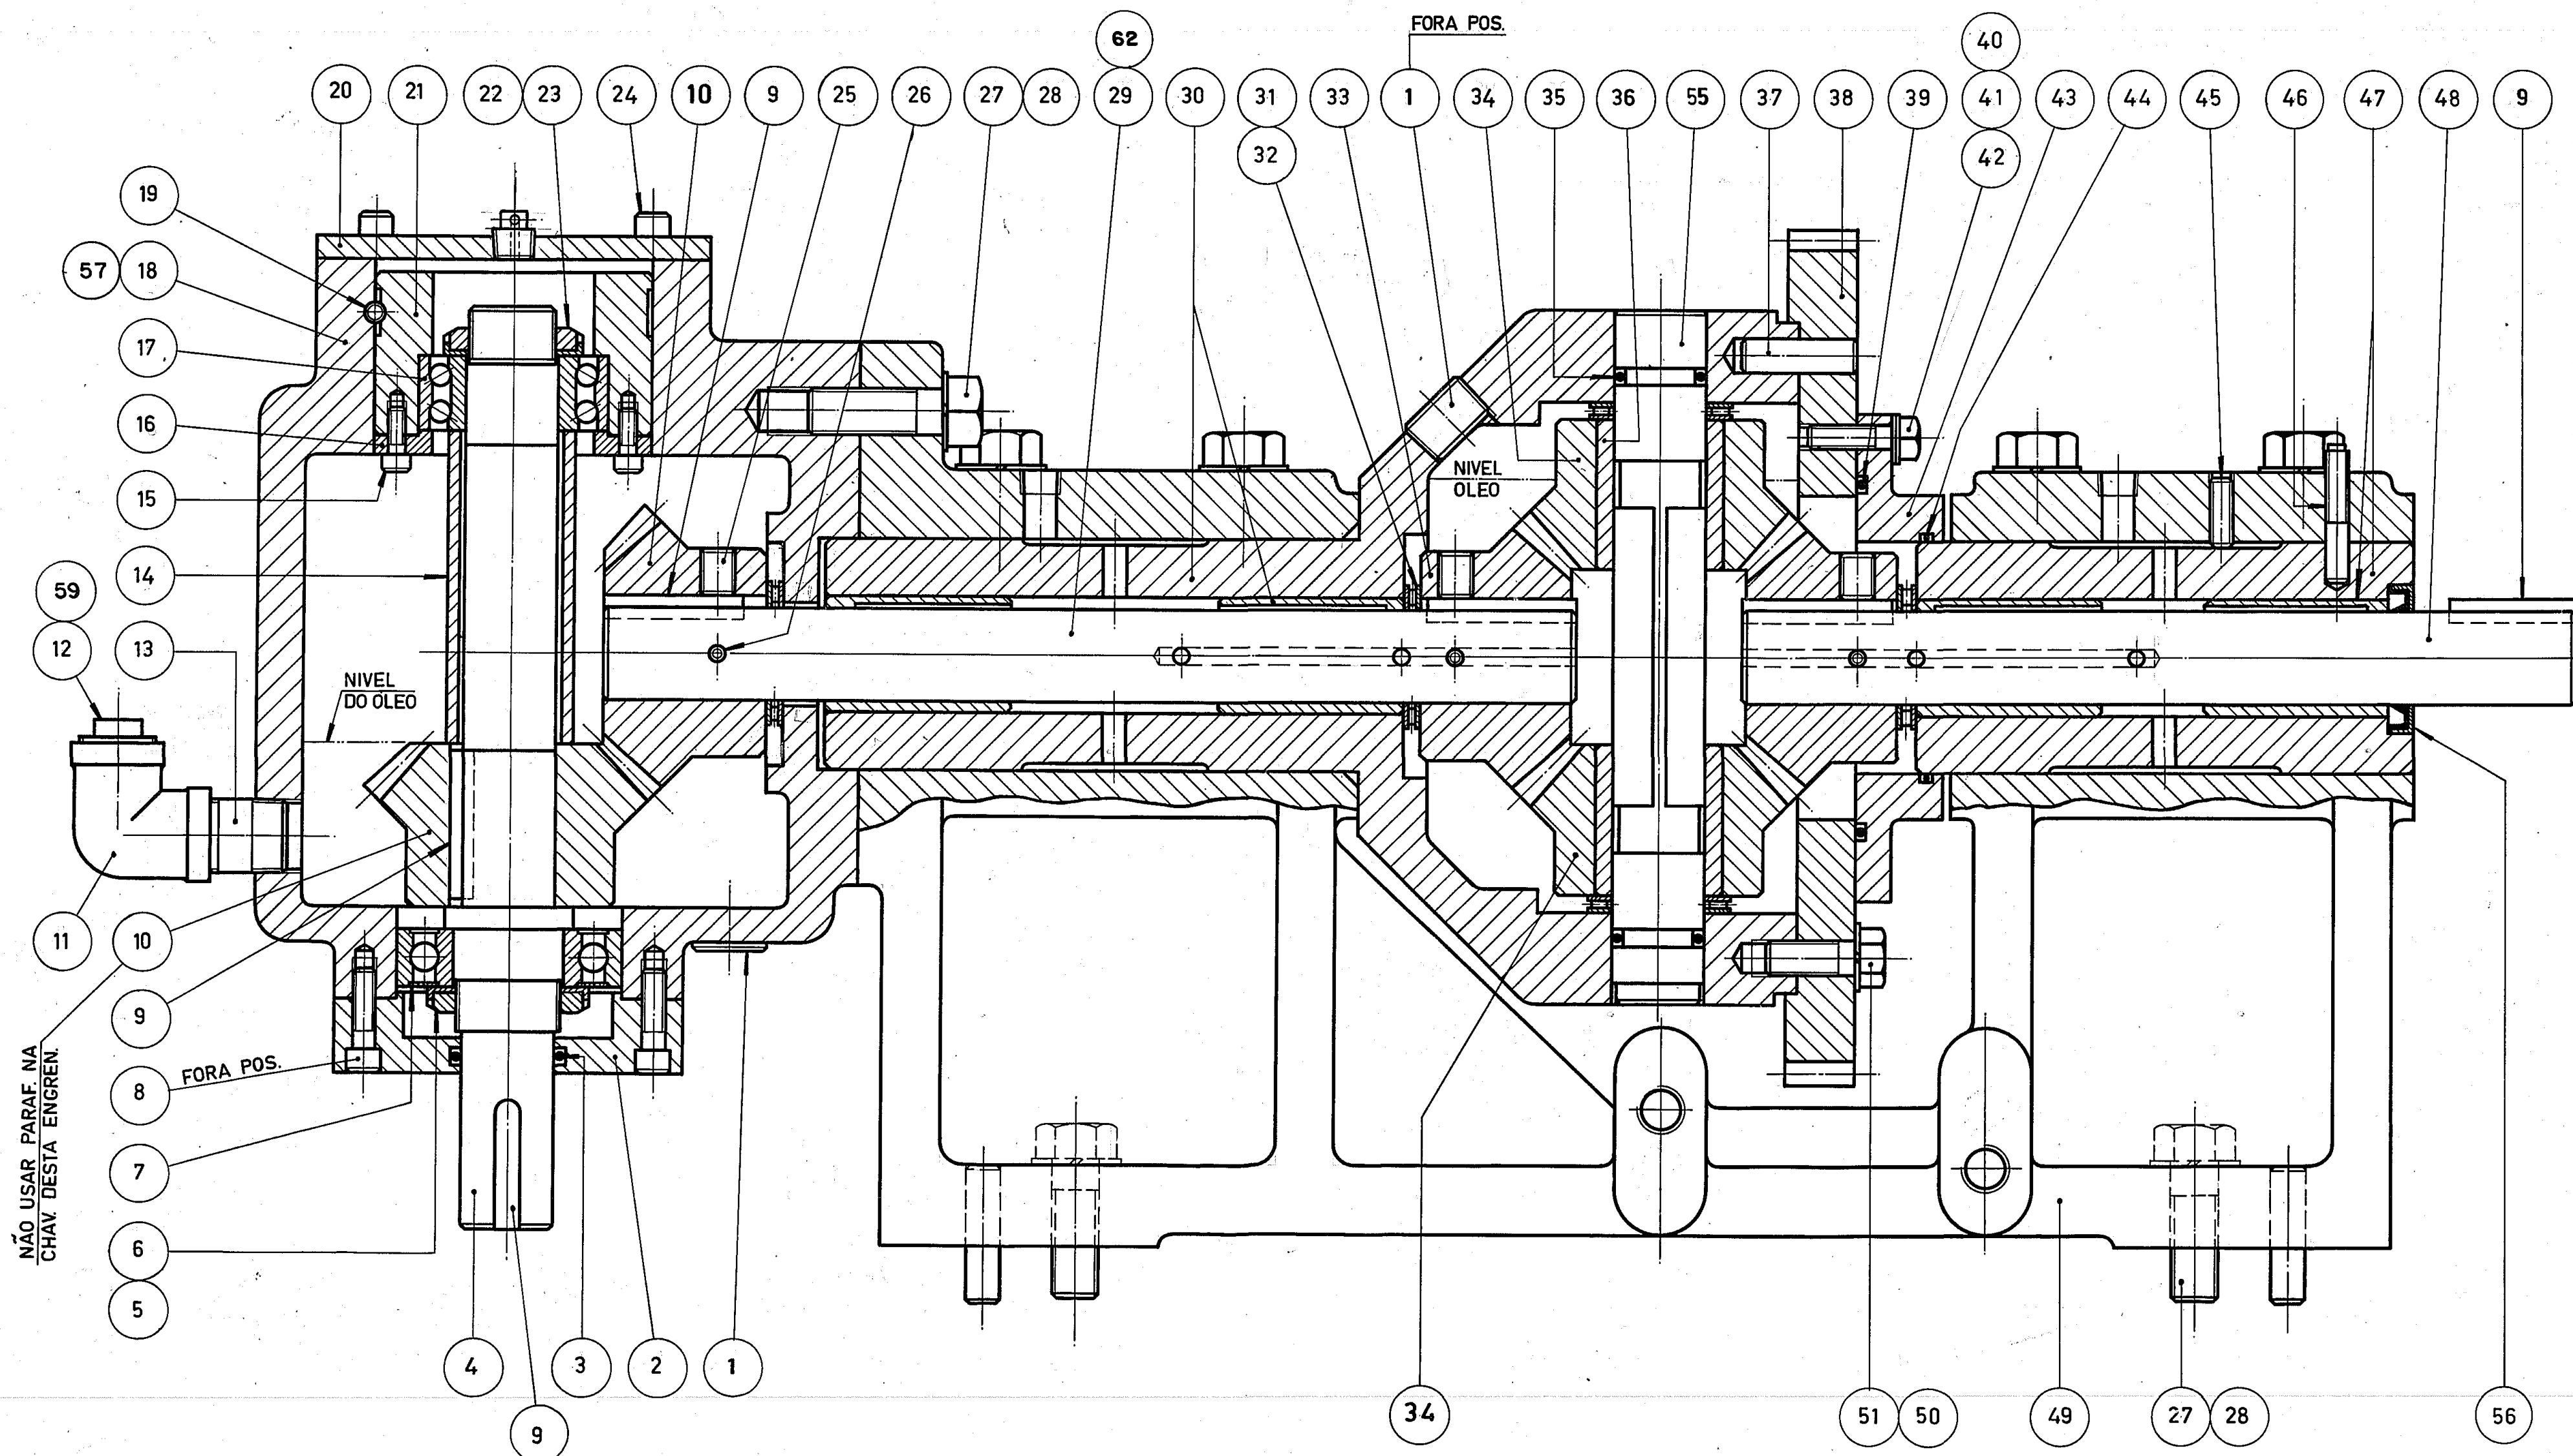

NOTA:
USAR VEDANTE NAS JUNTAS,
ONDE FOR NECESSÁRIO.

1	—	62	EIXO	VV-5206	AÇO	
1	—	61	PLUG ALLEN S/ CAB.	COMERCIAL 175-B-1	AÇO	Ø 1/8 NPT
—	1	60	PLUG ESPECIAL	VV-5659	LATAO	
1	—	59	PLUG ESPECIAL	VV-5121	AÇO	
1	—	57	HOUSING	VV-5203	F. FUND.	
—	1	56	RETENTOR	COMERCIAL		VEDABRAS Nº 24.623-A2
—	1	55	GEAR SHAFT	1523-5485	AÇO	
—	2	54	PINO DE GUIA	COMERCIAL	AÇO PRATA	Ø 3/8 x 1 1/2
2	2	53	COVER	1523-5106	AÇO	
8	8	52	PARAF. CAB. SEXT.	COMERCIAL	AÇO	1/4 NC x 3/4
—	3	51	ARRUELA DE PRESSÃO	COMERCIAL	AÇO	Ø 3/8"
—	3	50	PARAF. CAB. SEXT.	COMERCIAL	AÇO	3/8 NC x 1 1/4
—	1	49	BASE & CAPS	1523-51		SUB-CONJ.
—	1	48	SHAFT	1523-5100	AÇO	
—	1	47	BUSHING	1523-5105	AÇO	
—	1	46	PINO DE TRAVA	VV-2447	AÇO	
—	2	45	PARAF. ALLEN S/ CAB.	COMERCIAL	AÇO	1/4 NC x 3/4
—	1	44	ANEL DE VEDAÇÃO	COMERCIAL	BORRACHA	VAB-165 2 1/2 DI x 2 1/16 DE x 3/32
—	1	43	OIL SEAL PLATE	1523-5483	AÇO	
—	3	42	ARRUELA LISA	COMERCIAL	AÇO	Ø 1/4"
8	11	41	ARRUELA DE PRESSÃO	COMERCIAL	AÇO	Ø 1/4"
—	3	40	PARAF. CAB. SEXT.	COMERCIAL	AÇO	1/4 NC x 1"
—	1	39	ANEL DE VEDAÇÃO	COMERCIAL	BORRACHA	VAB-116 3 3/8 DI x 4 DE x 1/8
—	1	38	HELICAL GEAR	1523-5099	F. FUND.	
—	1	37	PINO	COMERCIAL	AÇO PRATA	Ø 3/8 x 1 1/4"
—	2	36	BUCHA	VV-2445	BRONZE	
—	2	35	ANEL DE VEDAÇÃO	COMERCIAL	BORRACHA	VAB-103 3/4 DI x 1 DE x 1/8
—	2	34	MITER GEAR - 24 T.	1523-5484	AÇO	
—	2	33	MITER GEAR - 24 T.	48-2264	AÇO	
2	10	32	ARRUELA DE ENCOSTO	COMERCIAL	AÇO	TORRINGTON TRA-1625
1	5	31	ROLAMENTO DE ESCORA	COMERCIAL	AÇO	TORRINGTON NTA-1625
—	1	30	GEAR HOUSING & BUSH.	1523-5097	F. FUND.	
—	1	29	SHAFT	1523-5101	AÇO	
—	7	28	ARRUELA DE PRESSÃO	COMERCIAL	AÇO	Ø 1/2"
—	7	27	PARAF. CAB. SEXT.	COMERCIAL	AÇO	1/2 NC x 1 1/2"
1	3	26	PINO ELÁSTICO	COMERCIAL	AÇO	SEEGER 70125 4,5 x 50 mm
1	3	25	PARAF. ALLEN S/ CAB.	COMERCIAL	AÇO	1/4 NC x 1/2
3	3	24	PARAF. ALLEN C/ CAB.	COMERCIAL	AÇO	1/4 NC x 1/2
1	1	23	ARRUELA DE TRAVA	COMERCIAL	AÇO	SKF-MB 5
1	1	22	PORCA DE FIXAÇÃO	VV-2444	AÇO	
1	1	21	BUSHING	1523-5104	AÇO	
1	1	20	COVER	1523-5107	AÇO	
2	2	19	PINO DE TRAVA	COMERCIAL	AÇO PRATA	Ø 1/4 x 2"
—	1	18	HOUSING	1523-5096	F. FUND.	
1	1	17	ROLAMENTO	COMERCIAL	AÇO	SKF-3205
1	1	16	BEARING RETAINER	1523-5108	AÇO	
4	4	15	PARAF. ALLEN C/ CAB.	COMERCIAL	AÇO	Nº 10 NC x 1/2
1	1	14	SPACER	1523-5109	AÇO	
1	1	13	NIPLE	COMERCIAL	F. GALVAN.	1/2 NPT x 1
—	1	12	PLUG C/ CAB.	COMERCIAL	AÇO	1/2 NPT
1	1	11	COTOVELO - 90°	COMERCIAL	F. GALVAN.	1/2 NPT
2	2	10	MITER GEAR - 24 T.	48-2254	AÇO	
3	6	9	CHAVETA	COMERCIAL	AÇO P/CHAV.	1/4 x 1 3/8
3	3	8	PARAF. ALLEN C/ CAB.	COMERCIAL	AÇO	1/4 NC x 7/8
1	1	7	ROLAMENTO	COMERCIAL	AÇO	SKF-6206-Z
1	1	6	ARRUELA DE TRAVA	COMERCIAL	AÇO	SKF-MB 6
1	1	5	PORCA DE FIXAÇÃO	VV-2443	AÇO	
1	1	4	SHAFT	1523-5103	AÇO	
2	1	3	ANEL DE VEDAÇÃO	COMERCIAL	BORRACHA	VAB-105 1 DI x 1 1/4 DE x 1/8
1	1	2	CAP	1523-5112	AÇO	
—	2	1	PLUG TIPO ALLEN	COMERCIAL	AÇO	1/2 NPT
QUANT.	POS.	DENOMINACAO	PEÇA Nº	MATERIAL	OBS.	
2	1	GR. Nº	VIDROS VITON LTDA.	DE. VER	DATA 02-10-86	
3-3-93	3-3-93	DESCRIPÇÃO DO GRUPO	SISTEMA DE TRANSMISSÃO	Nº DO COT. VVM-362	Nº DA PEÇA 1523-D-9	
			MANUAL DIFFERENTIAL			
				ESCALA 3/4	Nº DO DES.	