


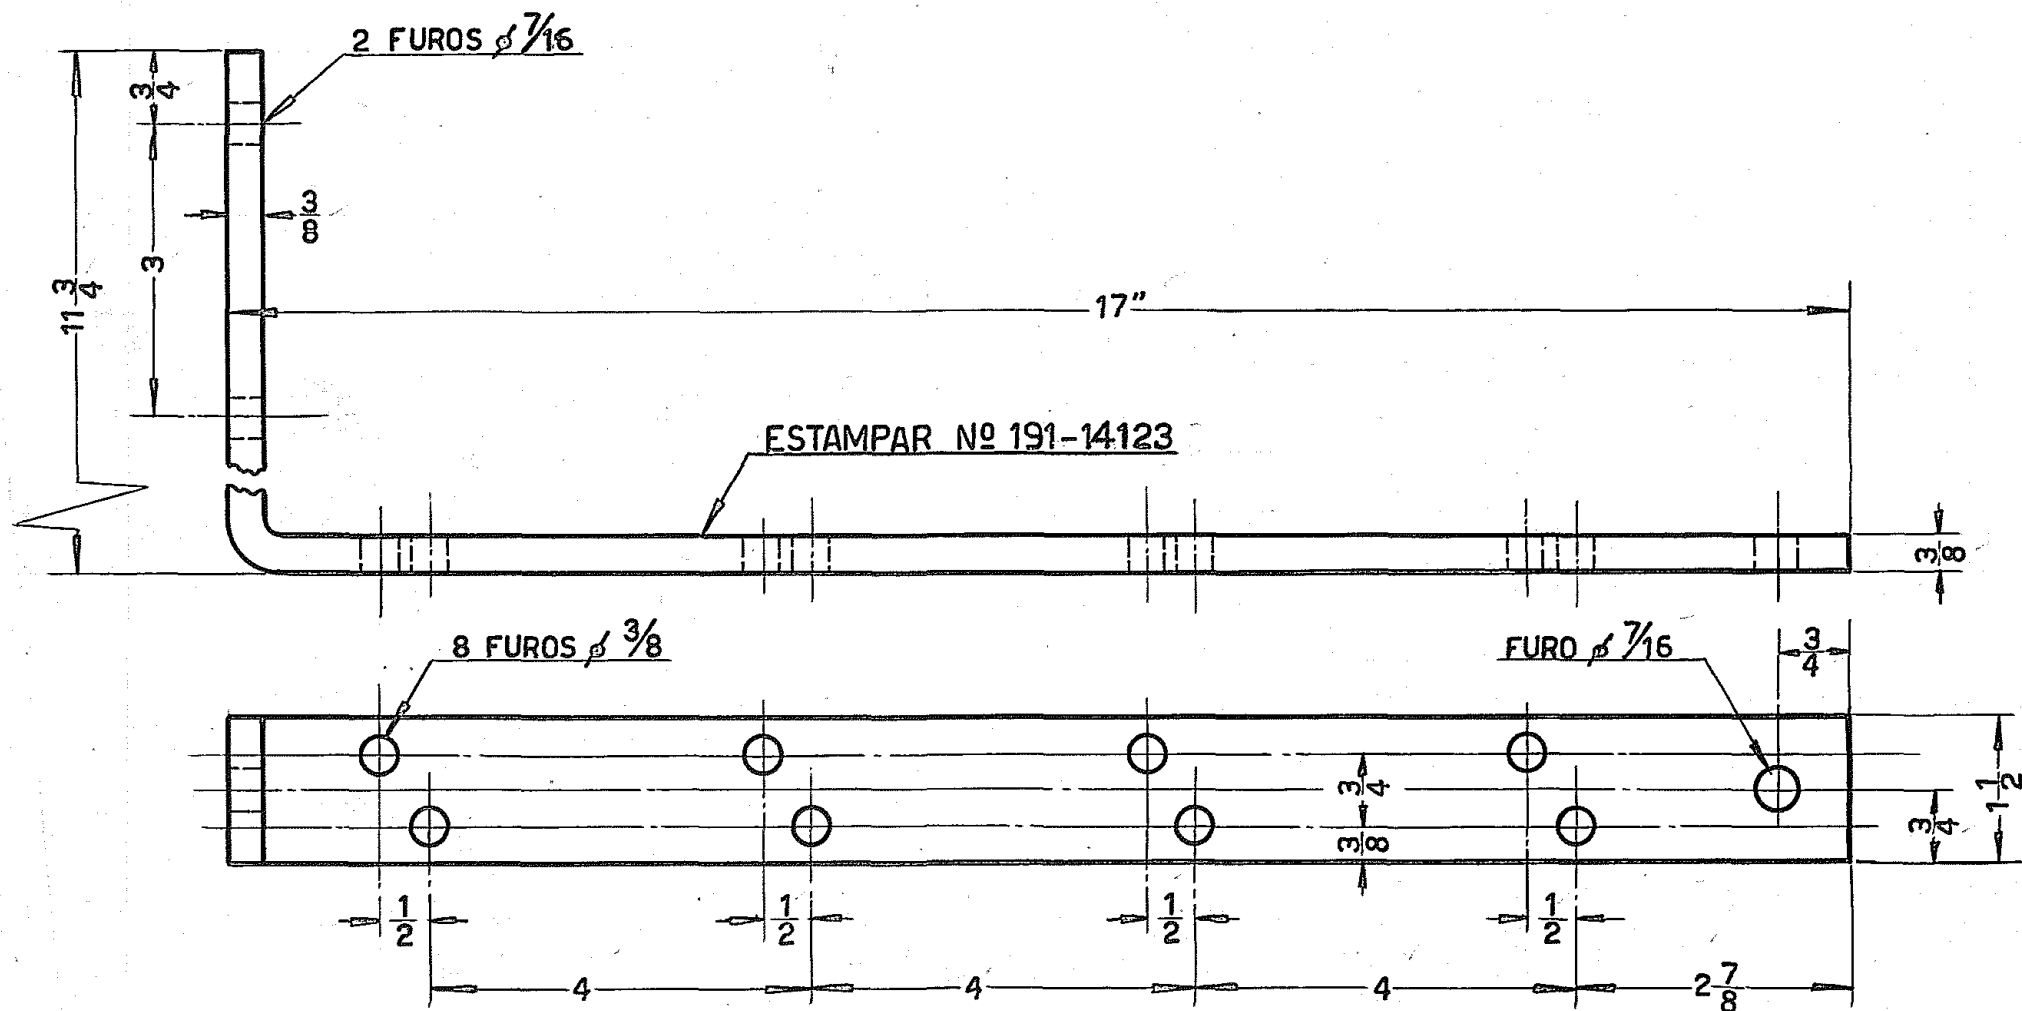

QUANT.-1 PEÇA

NOTA!

QUEBRAR CANTOS VIVOS

DATA: 8-3-1966	TOLERÂNCIAS STANDARD PARA SERRAÇÕES UNIDADES SEM TOLERÂNCIA INDICADA	VIDROS VITON LTDA.	DES. <i>E. Portela</i>
FRAÇÃO	DE 0" ATÉ 5" $\pm 1/64$ DE 5" ATÉ 24" $\pm 1/32$ ACIMA DE 24" $\pm 1/10$	MAT AÇO SAE 1020 (FERRO CHATO)	APROV.
NOME DA PEÇA	BRACKET-R.H.	JOGO DE PROTEÇÕES & SUP. P/ LUBRIF. AUTOM. DA MAQ. I.S.	N.º DO PROJ. VVL-105
TRAT. TERM.		ESCALA 1/2	N.º DO DES. 191-14123