
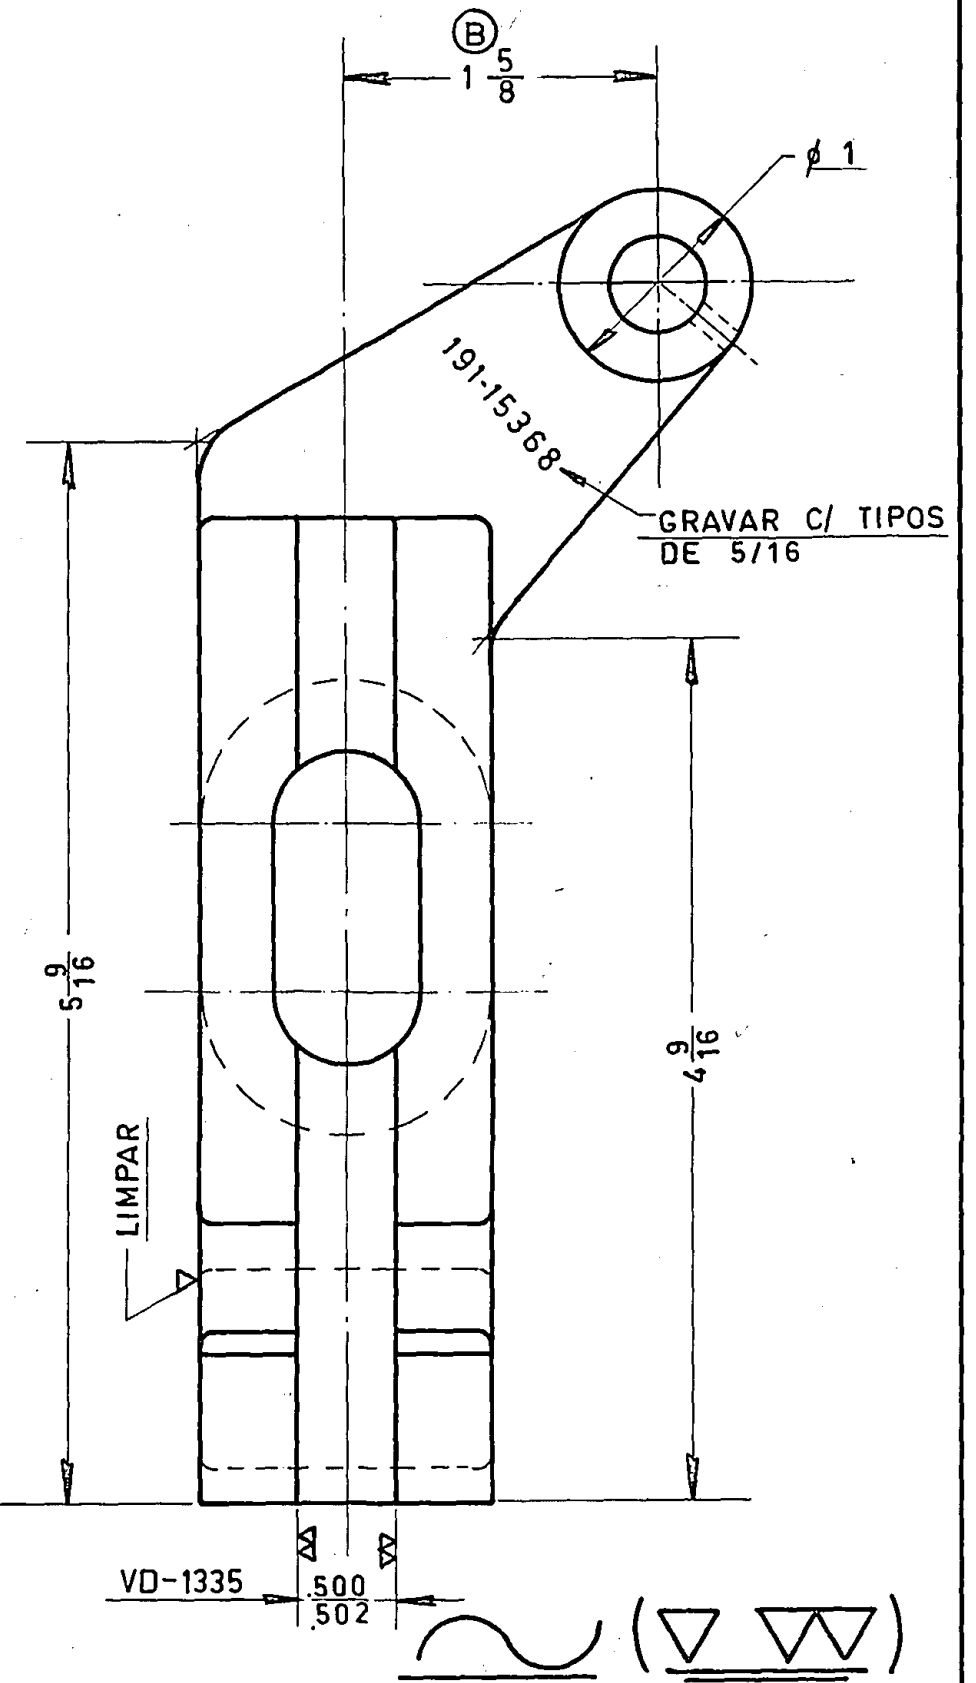
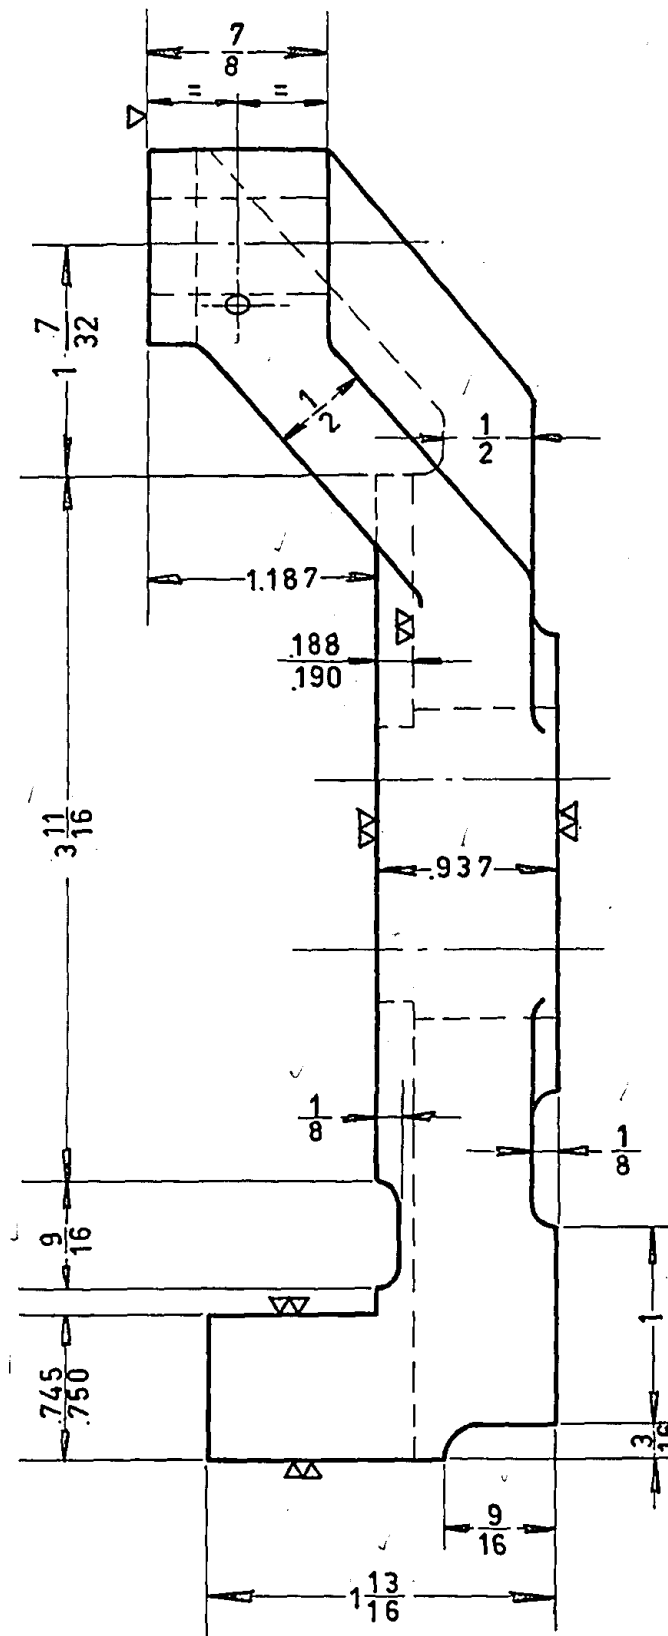


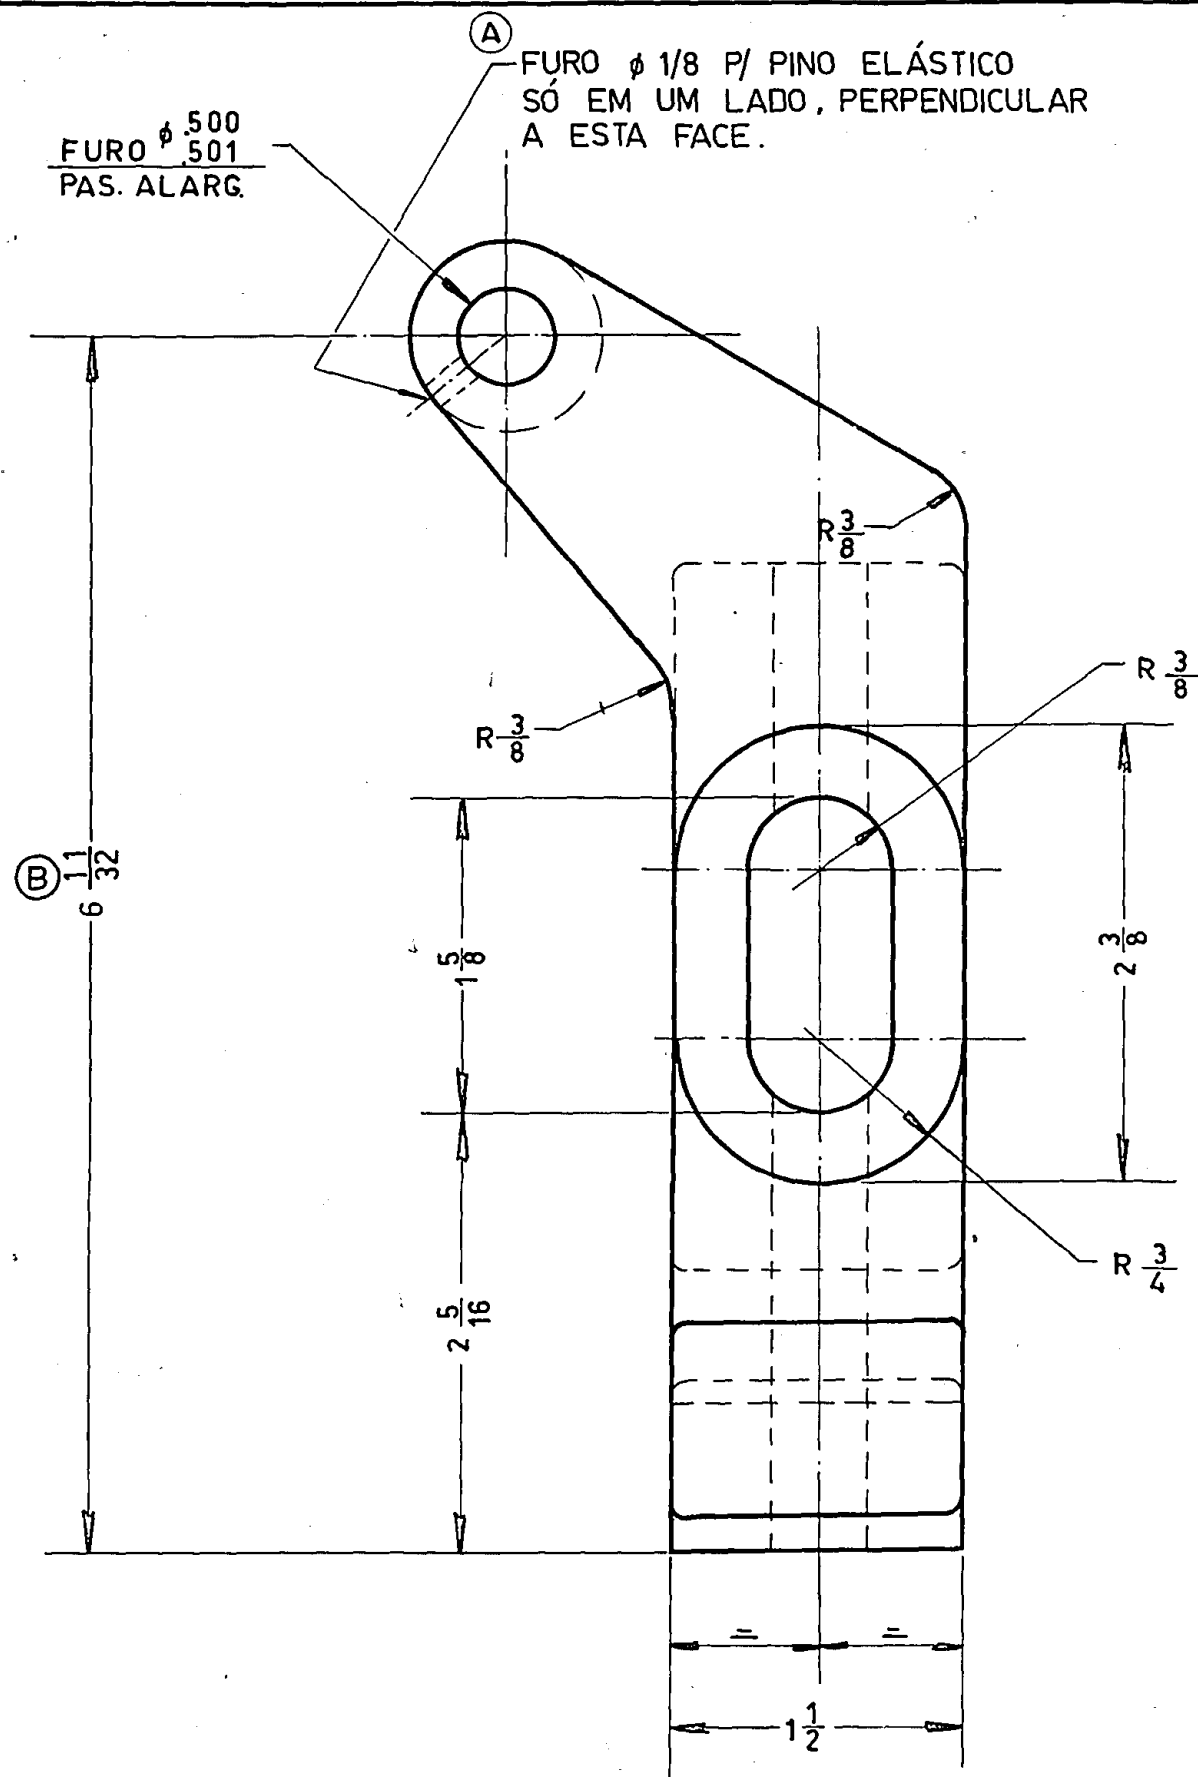

08-12-82		VIDROS VITON LTDA.		D.S. <i>M. S. Silva</i>	
TOLERÂNCIAS STANDARD PARA SUPERFÍCIES UNIFORMES SEM TOLERÂNCIA INDICADA		MAT. FERRO FUNDIDO GG-20		V.R. <i>10/10/82</i>	
DESMAL $\pm$.005"		DELIVERY SYSTEM		PRIC. V.	
F. 00		DOUBLE GOB 8 SEC. IN LINE		Nº DO 191-F-6596	
F. 00		ADJUSTING PLATE		CND.	
F. 00		SEC. 1 INF		Nº DA 191-15368	
F. 00		1:1		FOLHA 16 (L)	