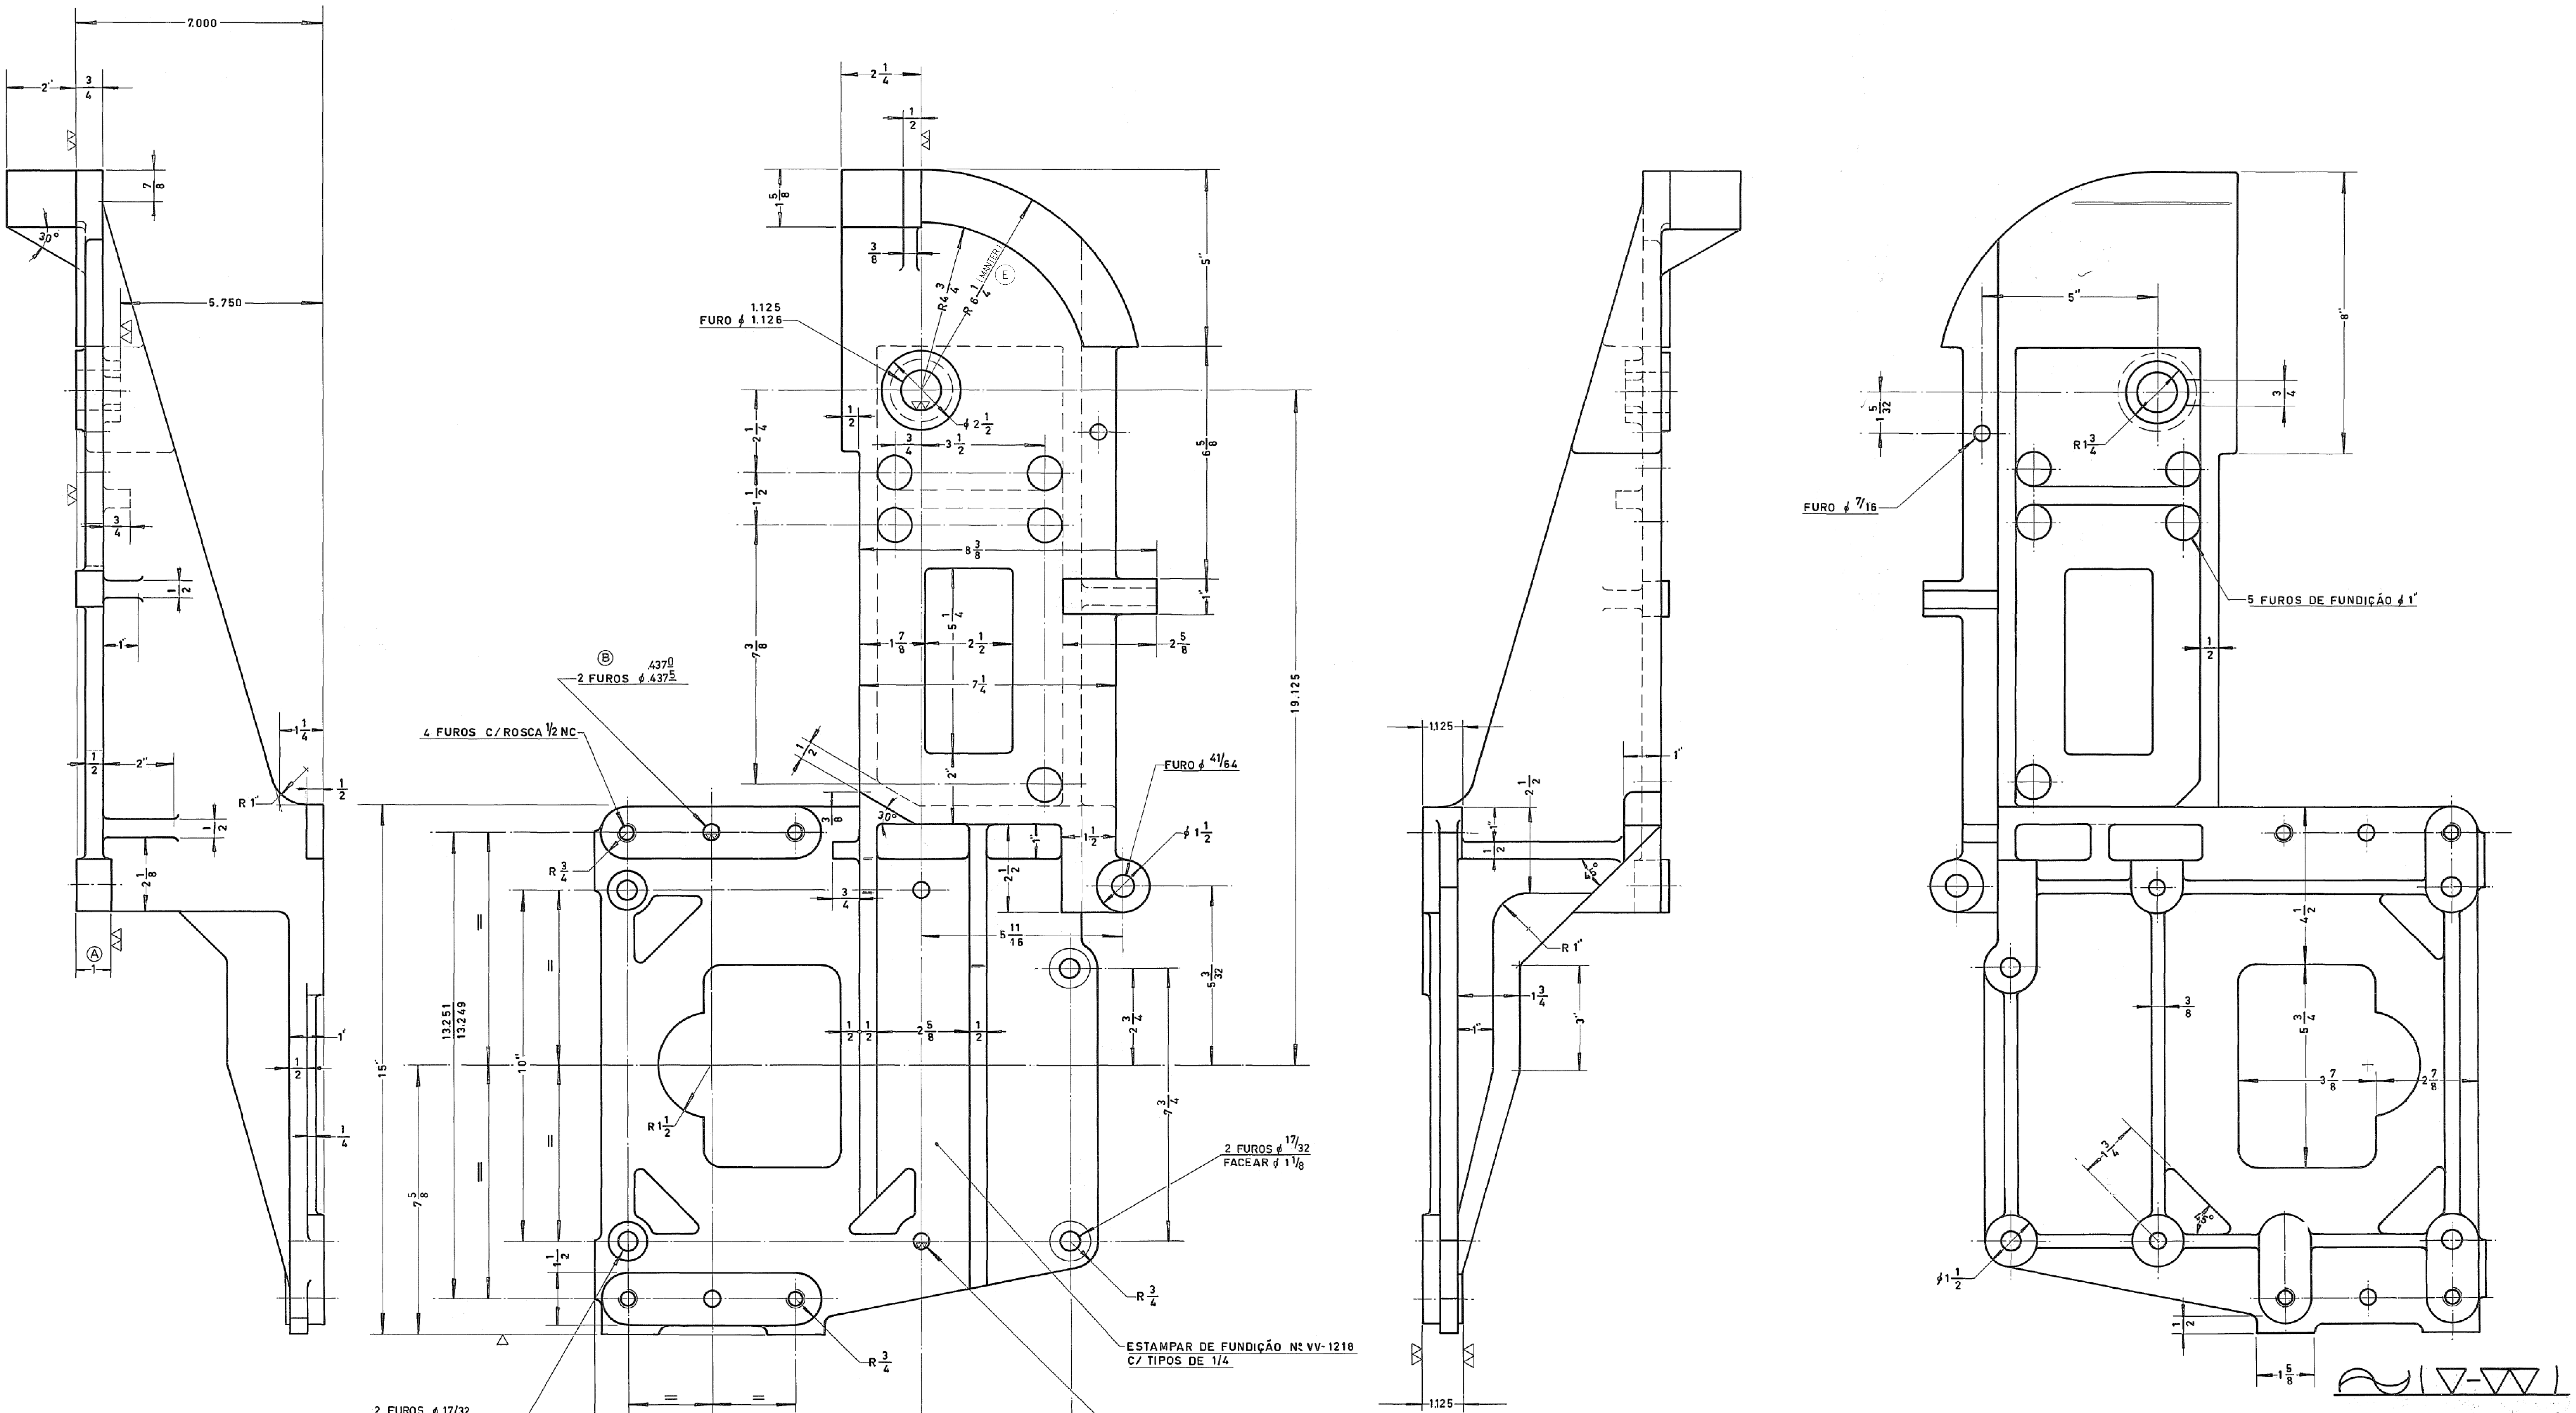

E	D	C	B	A	ITEM
ACRESC.	ERA: GG-20	ERA F.FUND SAE 114	ERA ϕ 31/64 ALARG.ϕ500/501	MUDOU LOCAL COTA	REVISÃO
RODRIGO 23/08/13	Ricardo 8.03.95	5/1/88 Américo	Acácio 12-6-87	Acácio 5-6-87	DATA

DATA: 21-09-81

TOLERÂNCIAS STANDARD PARA SUPERFÍCIES USINADAS SEM TOLERÂNCIA INDICADA

DECIMAL ± .005"

FRAÇÃO
DE 0" ATÉ 5" ± 1/64
DE 5" ATÉ 24" ± 1/32
ACIMA DE 24" ± 1/16

FERRO FUND. GG-25 Ⓒ Ⓓ

OVERHEAD STRUCTURE
MAQ. I.S. 8 SEÇÕES

MOUNTING BRACKET

ESCALA 1/2

VVM-204

191-15437

FOLHA 2 (L)