

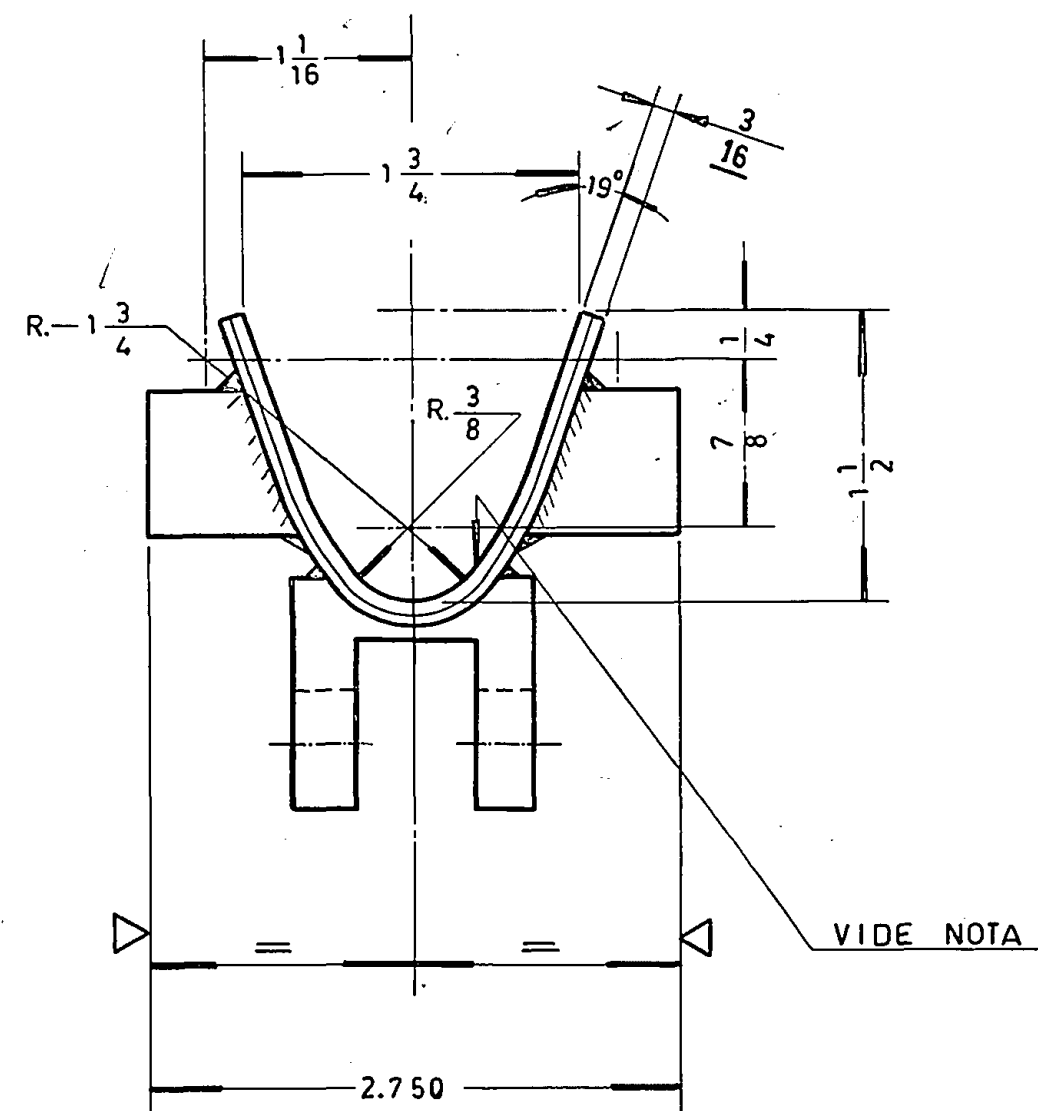


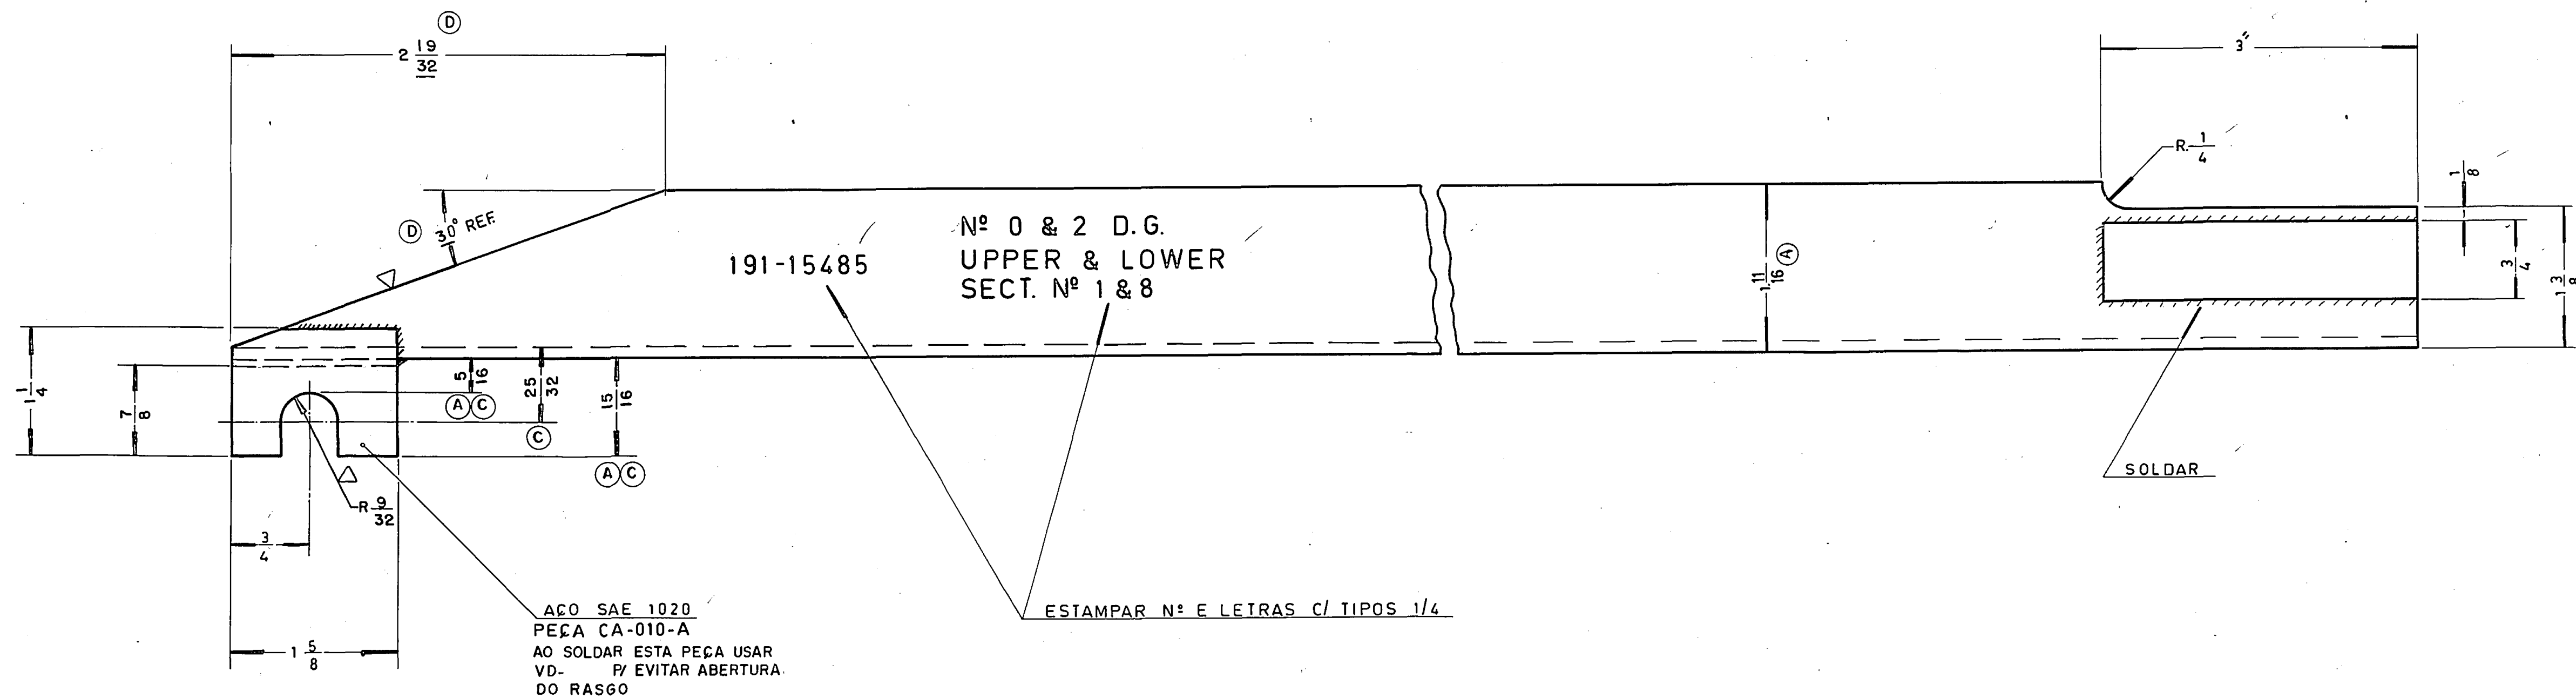

NOTA

ESTAS SUPERFÍCIES INTERNAS DEVEM SER PERFEITAMENTE
LISAS P/ ACEITAR SÓMENTE POLIMENTO

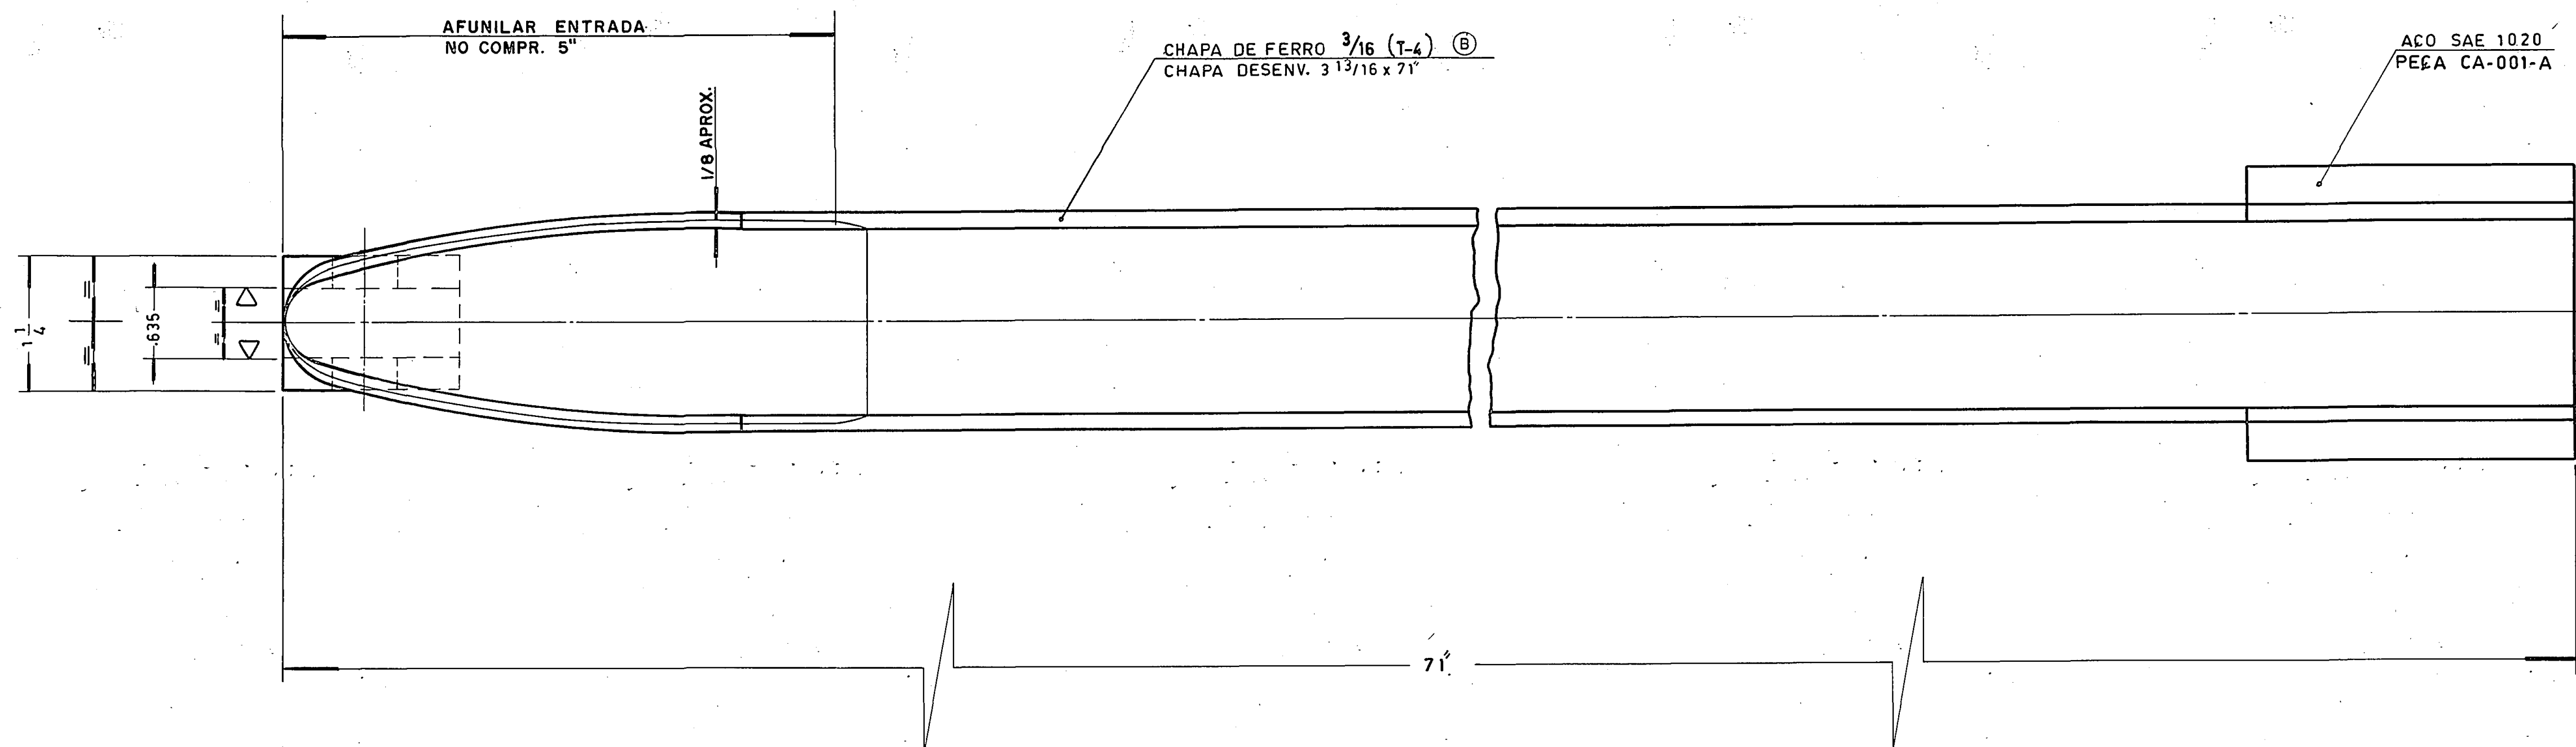

NOTA | DOBRAR CHAPA C/ VD-1829

ERA 207-E		DATA: 21-11-85	VIDROS VITON LTDA.		DES. <i>[Signature]</i>
231055 DM 4.1/8	C	TOLERÂNCIAS STANDARD	TOLERÂNCIAS STANDARD		V. R. <i>[Signature]</i>
241194 29/32 1/16	B	PARA SUPERFÍCIES	PARA SUPERFÍCIES		AFROV. <i>[Signature]</i>
241194 29/32 1/16	A	USINADAS SEM	USINADAS SEM		Nº DO
241194 29/32 1/16	ITEM	TOLERÂNCIA INDICADA	TOLERÂNCIA INDICADA		CODAL 191-6613
241194 29/32 1/16	REVISÃO	DECIMAL ± 0.05"	DECIMAL ± 0.05"		Nº DA
241194 29/32 1/16	DATA	FRACAO	FRACAO		PEÇA 191-15485
241194 29/32 1/16	REVISÃO	DE 0" ATE 5" ± 1/64	DE 0" ATE 5" ± 1/64		Nº JO
241194 29/32 1/16	REVISÃO	DE 5" ATE 24" ± 1/32	DE 5" ATE 24" ± 1/32		DES.
241194 29/32 1/16	REVISÃO	ACIMA DE 24" ± 1/16	ACIMA DE 24" ± 1/16		ESCALA 1:1
241194 29/32 1/16	REVISÃO	TERMO	TERMO		