

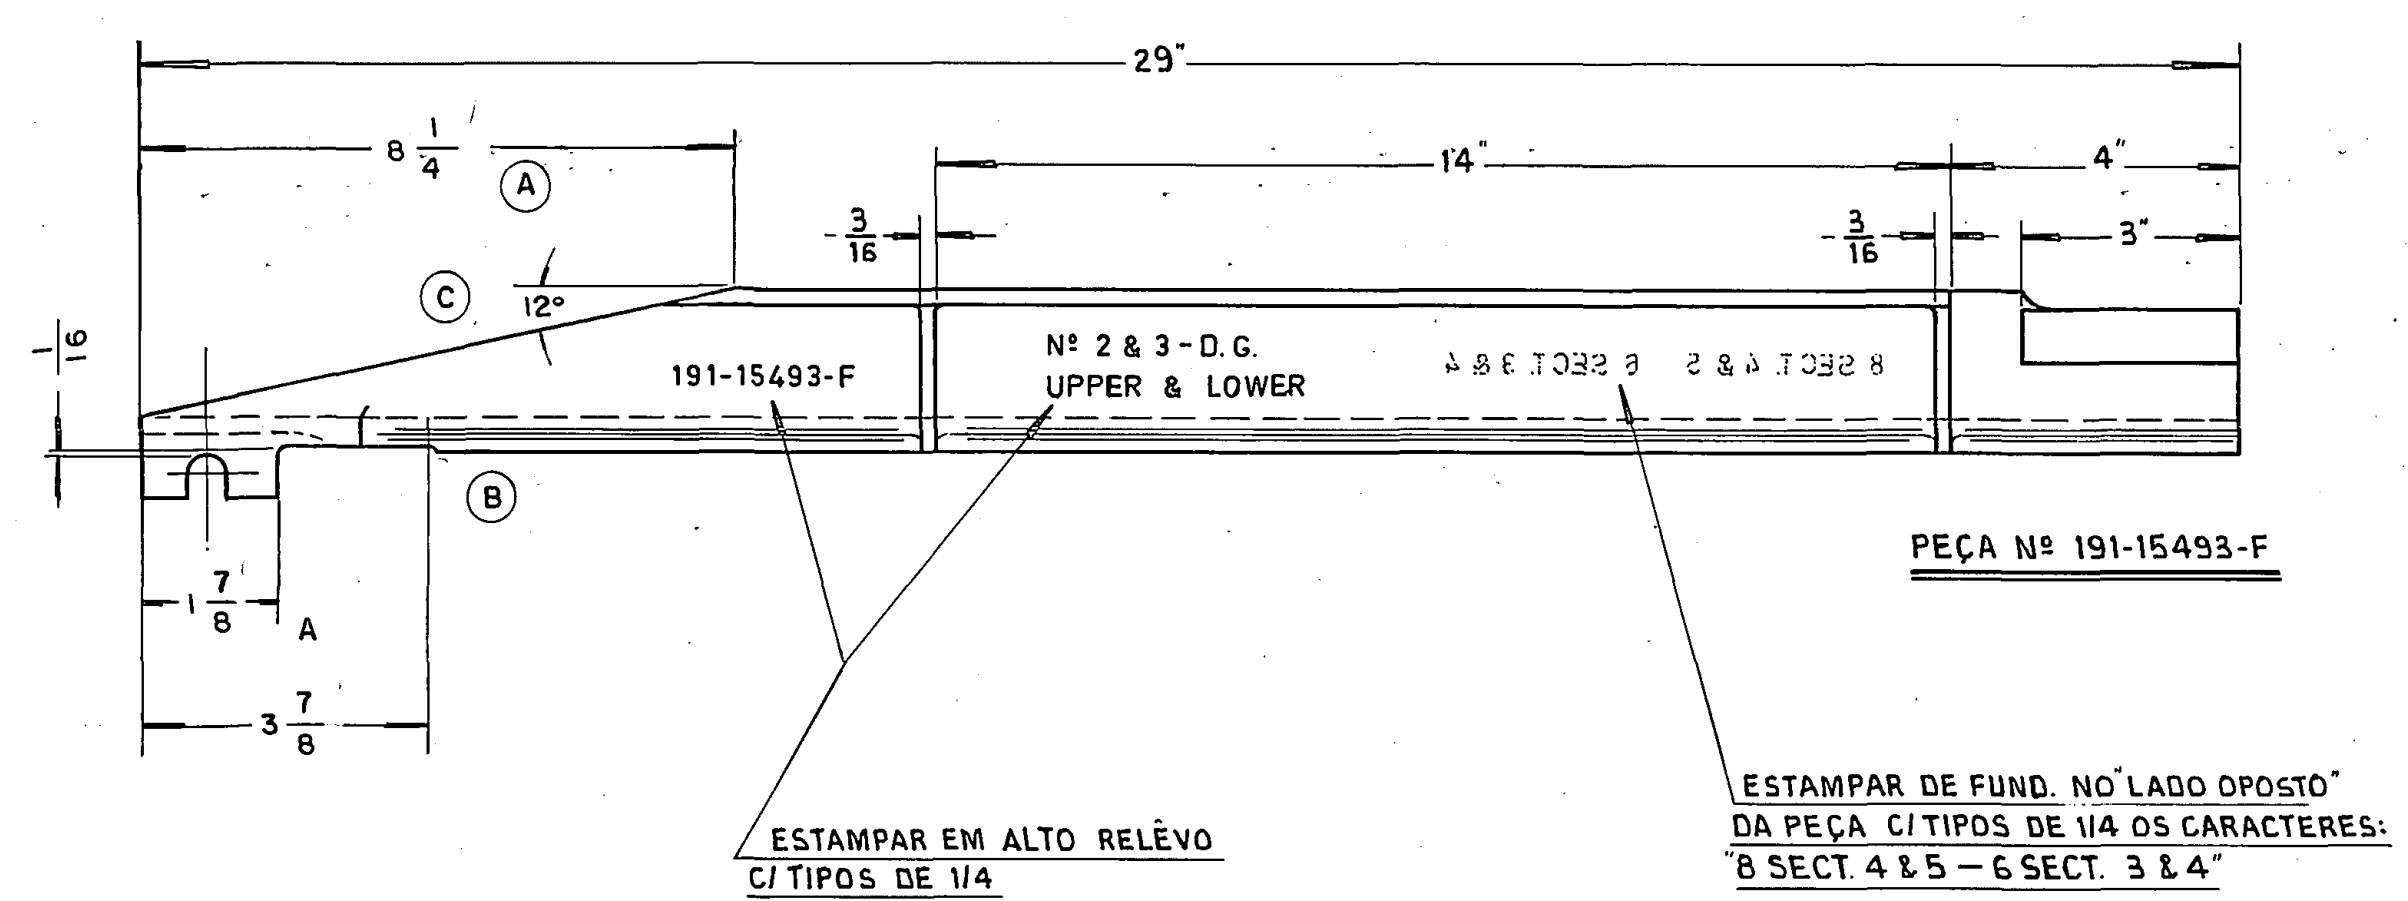


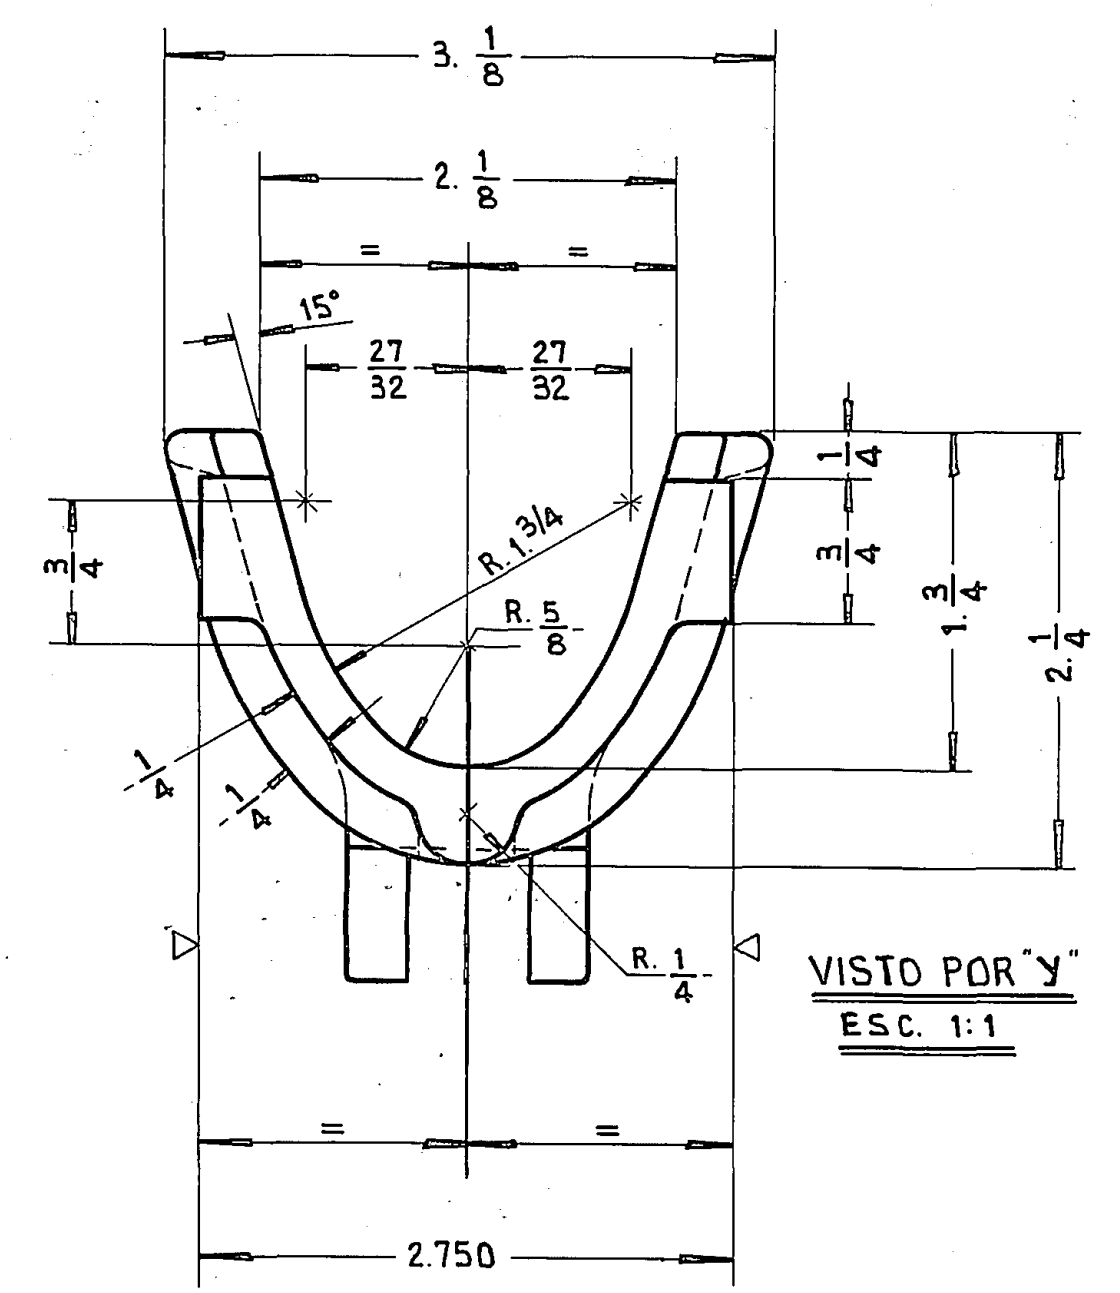

ESTAS SUPERFÍCIES DEVEM SER PERFEITAMENTE LISAS DE FUNDIÇÃO PI
ACEITAR SOMENTE POLIMENTO

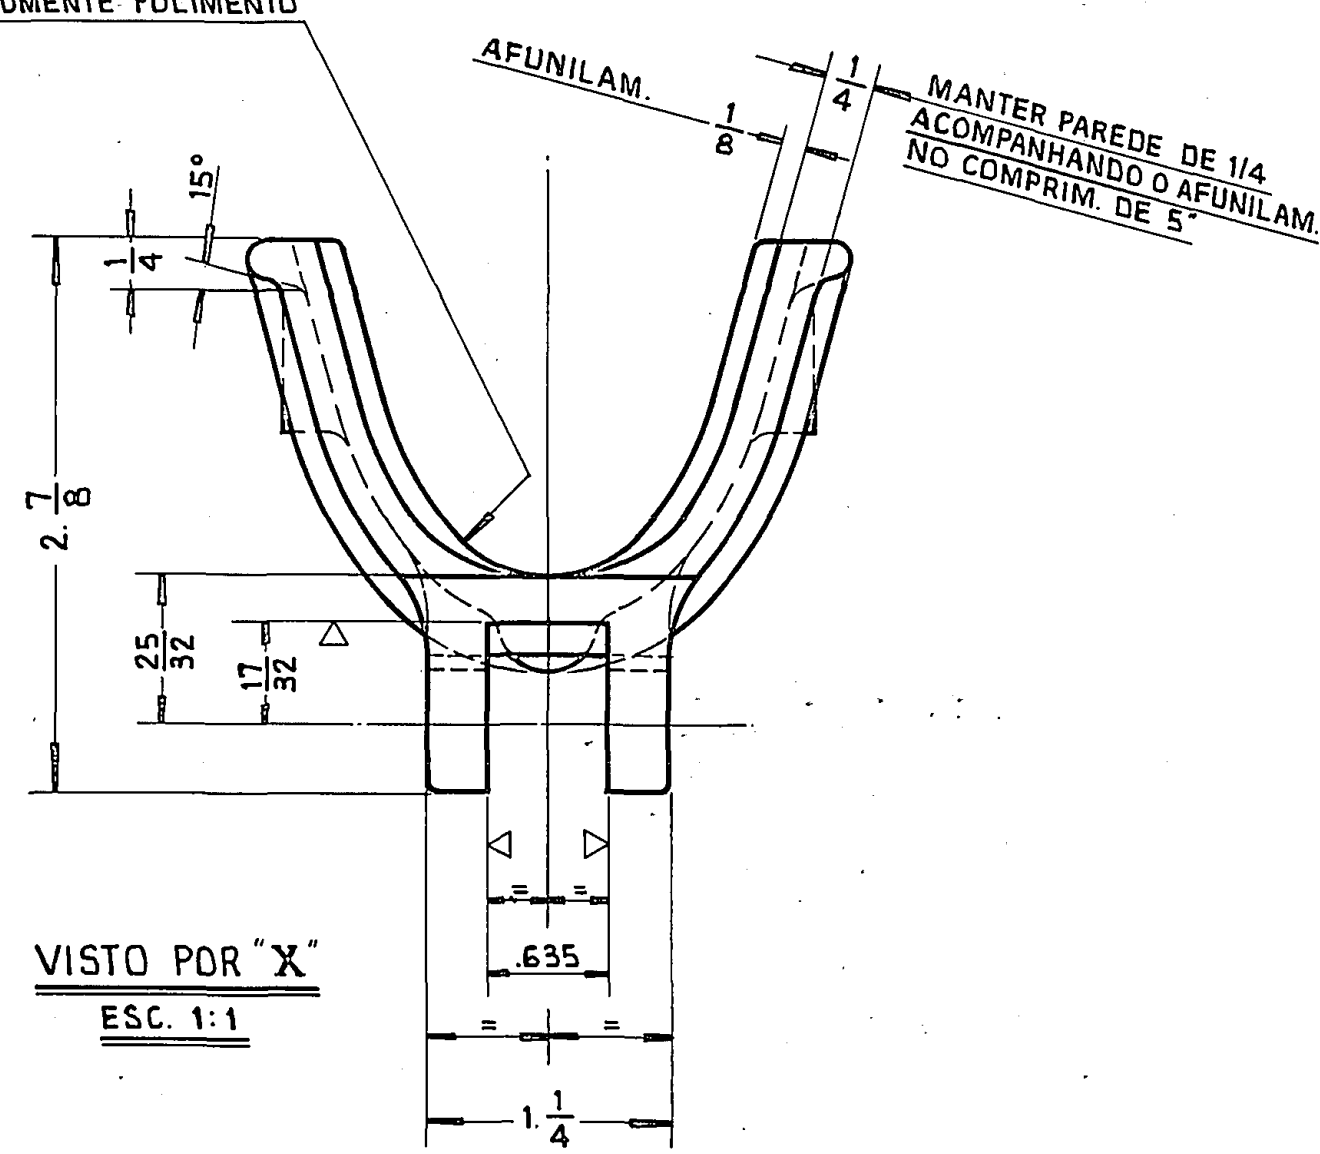

PEÇAS Nº
191-15493-F
191-15492-F
191-15491-F
191-15490-F

[illegible]