



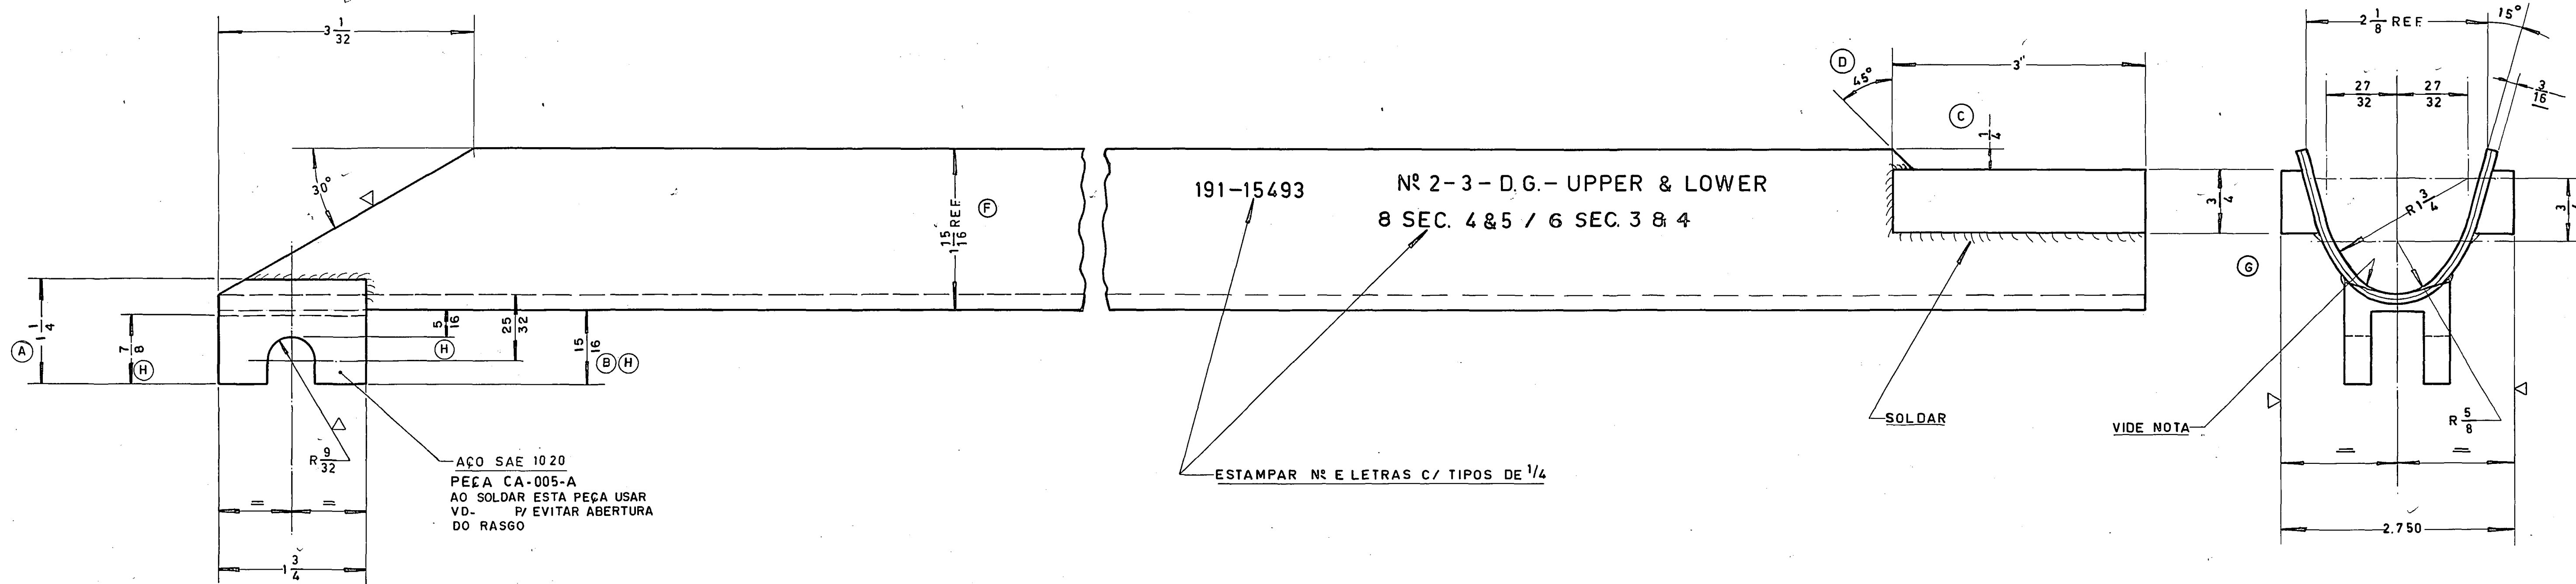

NOTA
ESTAS SUPERFÍCIES INTERNAS DEVEM SER PERFEITAMENTE LISAS P/ ACEITAR SÔMENTE POLIMENTO

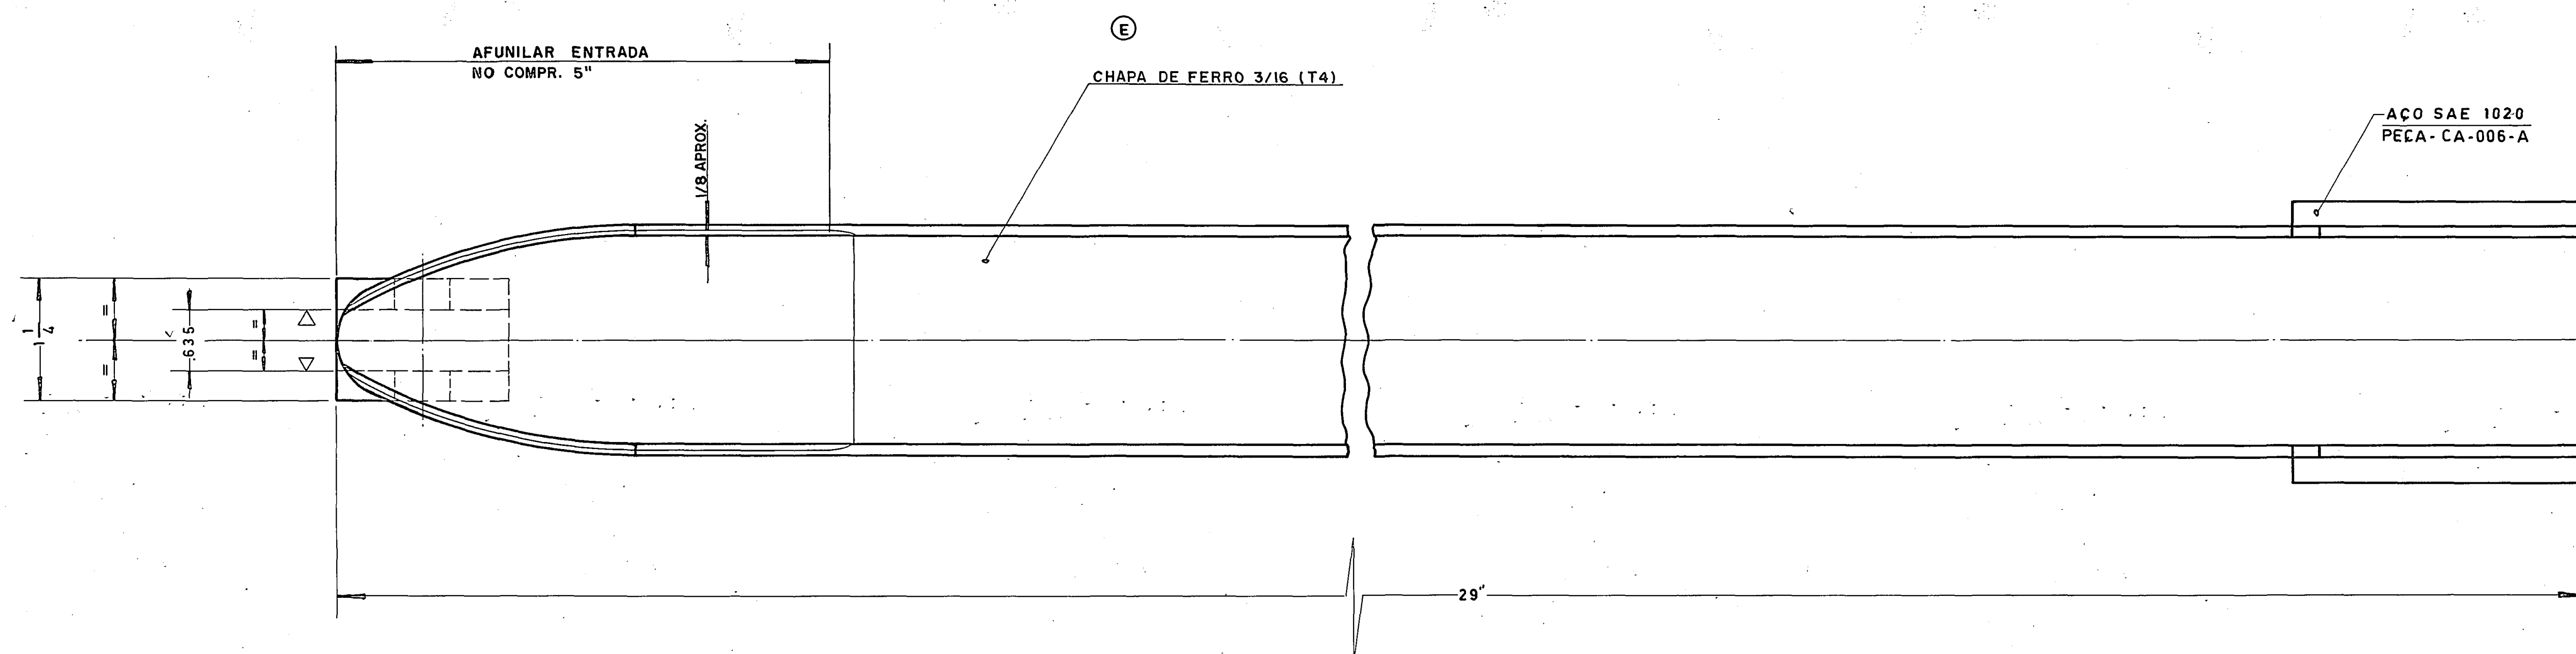

NOTA DOBRAR CHAPA C/ VD-1829



DATA: 22-4-82										VIDROS VITON LTDA.		DES. <i>Roberto</i>
TOLERÂNCIAS STANDARD PARA SUPERFÍCIES USINADAS SEM TOLÉRÂNCIA INDICADA										M.T. VIDE ANOT.		V. <i>Roberto</i>
DE 0\"										Nº 2-3 - D.G. - UPPER & LOWER		191-6613
DE 5\"										PEÇA SEC. 4 & 5 - UPPER & LOWER		191-15493
ACIMA DE 26\"										ESCALA 1:1		Nº DO DES.
ERA 1\"	H	G	F	E	D	C	B	A	DATA	FOLHA 14 (L)		
28/194	3/8	1/8	1/8	1/8	1/8	1/8	1/8	1/8	22-4-82			
23-06-89	23-06-89	23-06-89	23-06-89	23-06-89	23-06-89	23-06-89	23-06-89	23-06-89	23-06-89			
22-5-	22-5-	22-5-	22-5-	22-5-	22-5-	22-5-	22-5-	22-5-	22-5-			
89	89	89	89	89	89	89	89	89	89			
01/08	01/08	01/08	01/08	01/08	01/08	01/08	01/08	01/08	01/08			
101188	101188	101188	101188	101188	101188	101188	101188	101188	101188			