
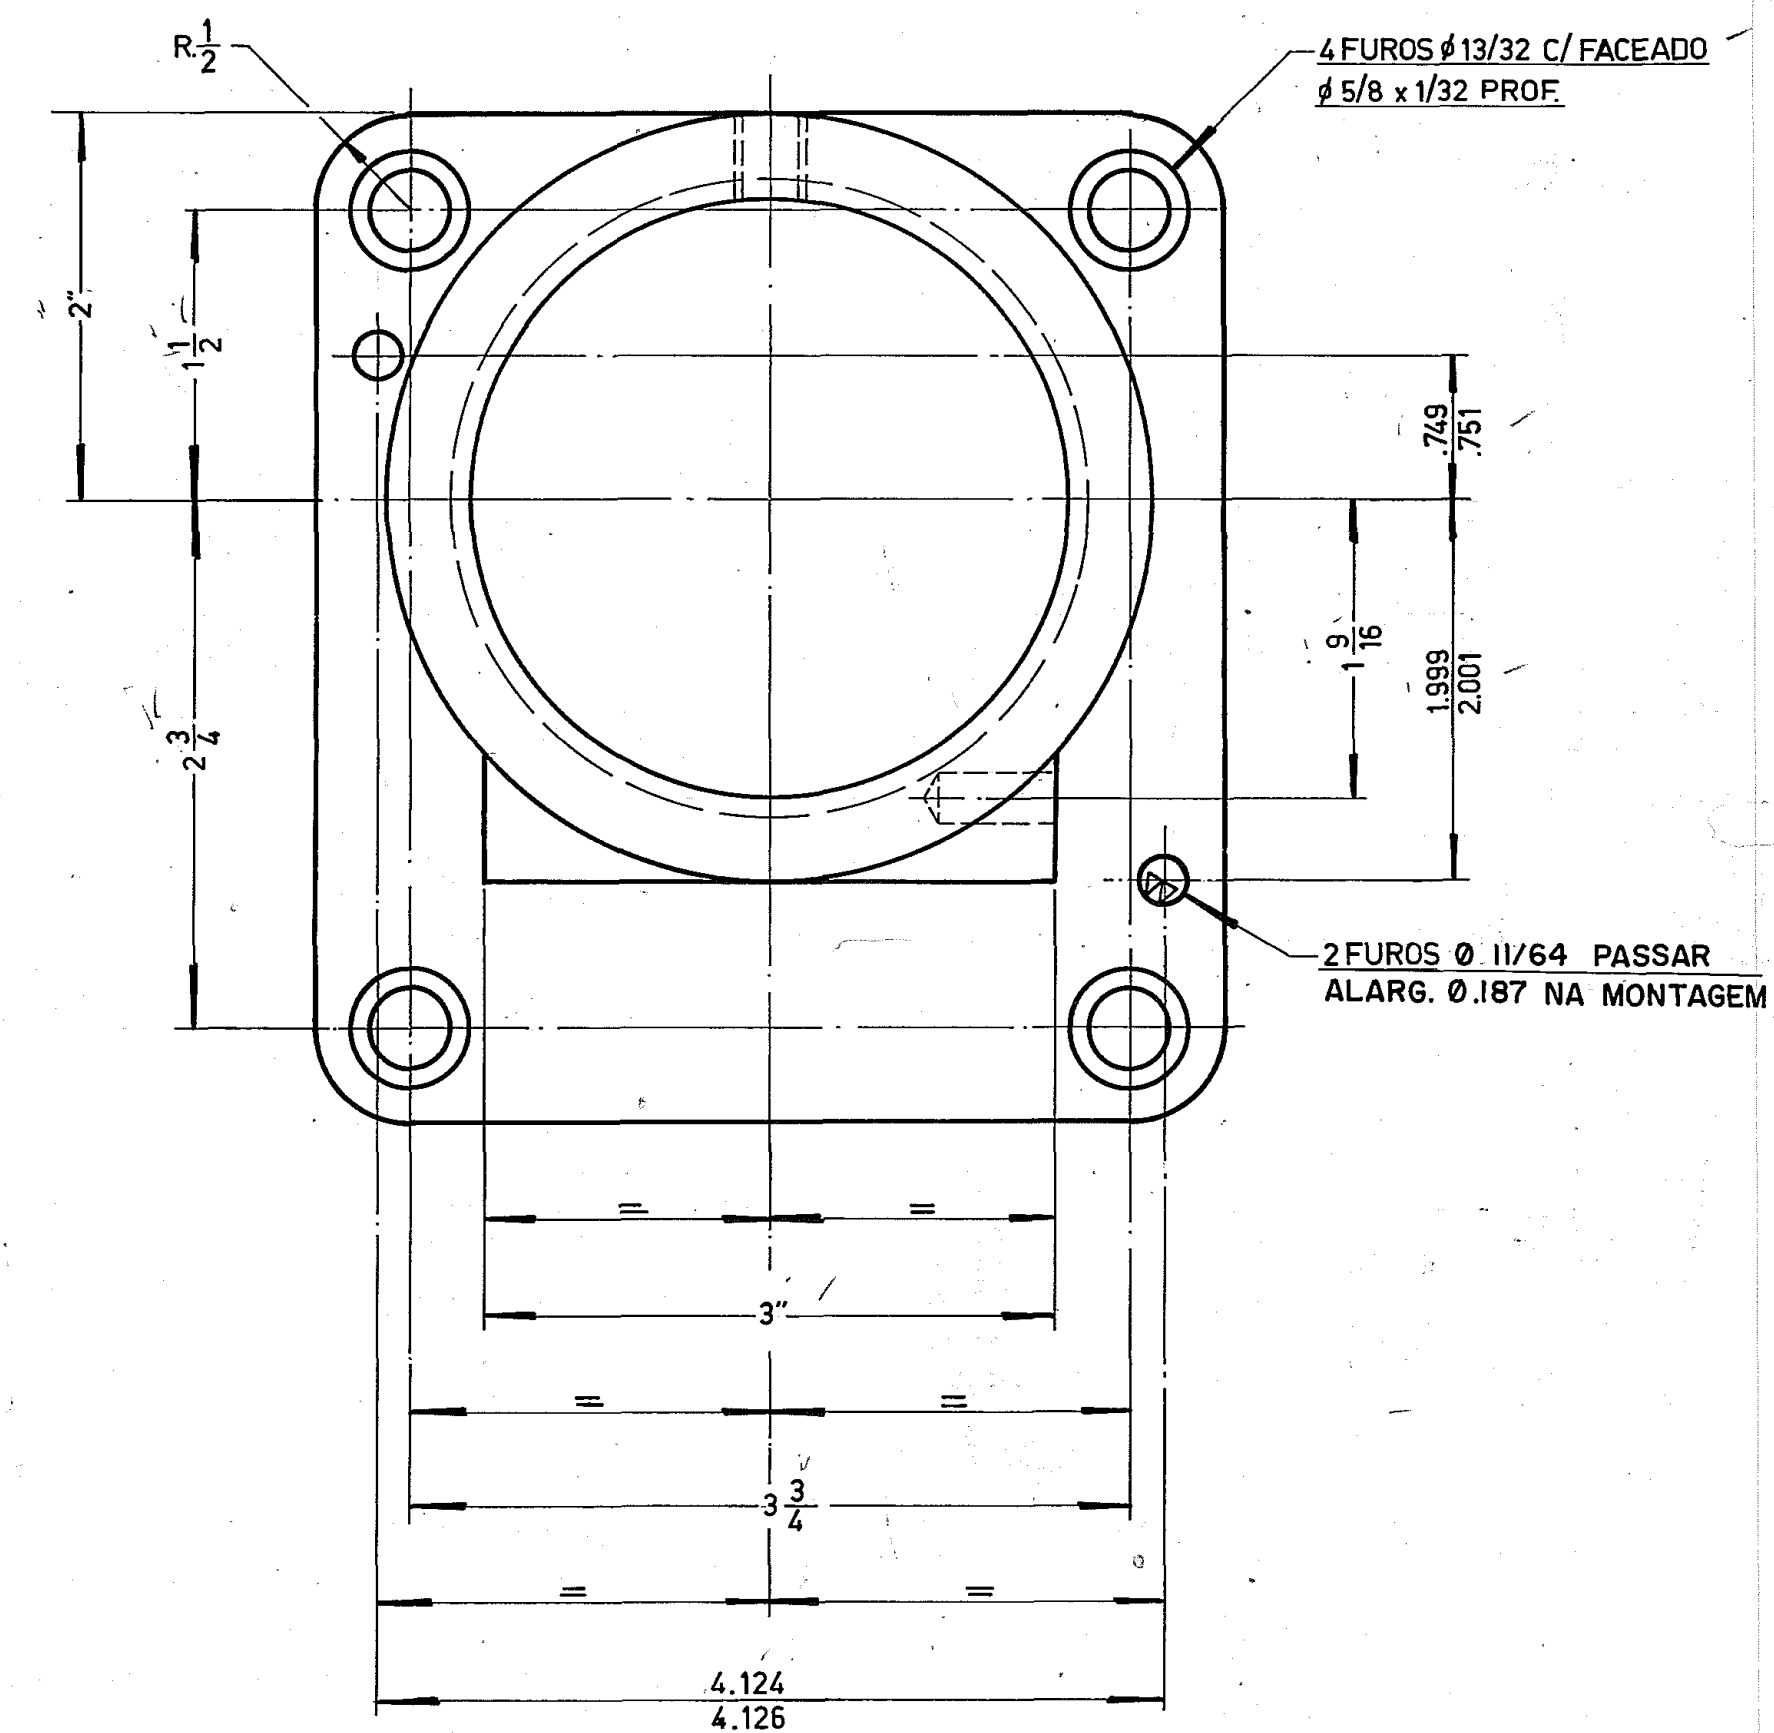


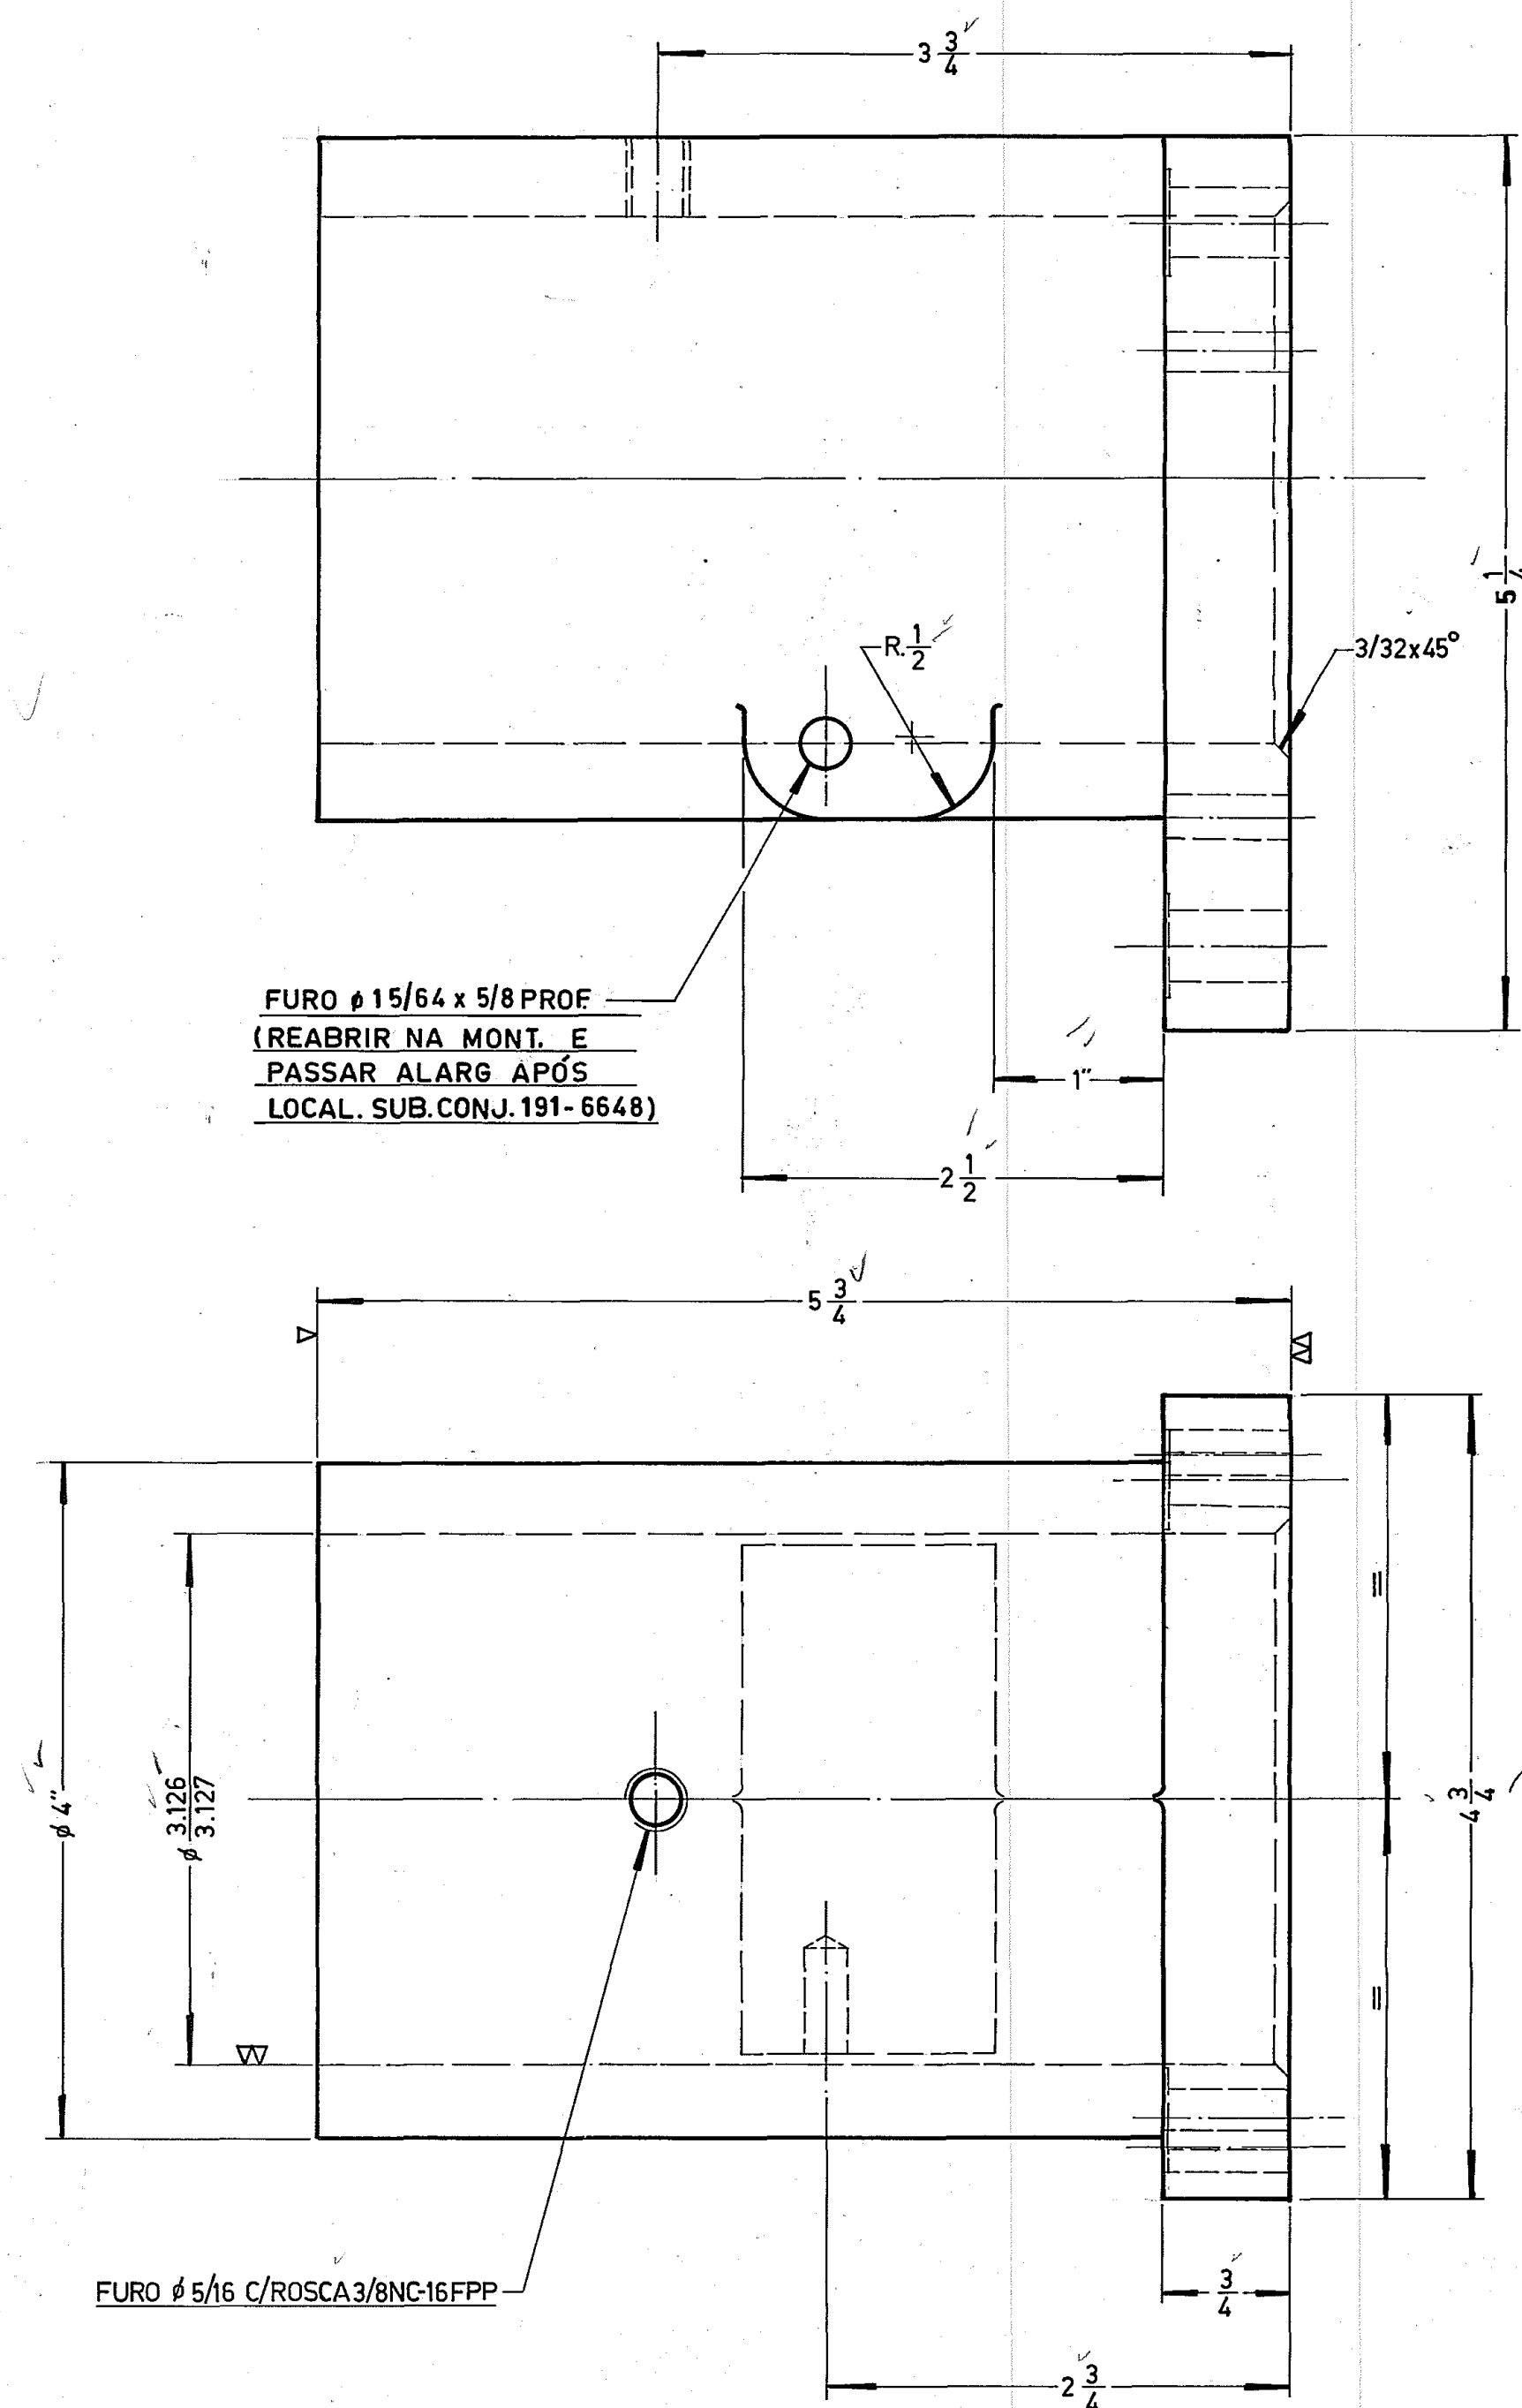

$\sim (\nabla - \nabla)$

194.88 SAE 120 194.88 SAE 120	DATA 04-02-1986 TOLERANCIAS STANDARD PARA SUPERFICIES USINADAS SEM TOLERANCIA INDICADA DECIMAL $\pm .005$ " FRAÇÃO DE 0" ATÉ 6" $\pm 1/64$ DE 6" ATÉ 24" $\pm 1/32$ ACIMA DE 24" $\pm 1/16$	VIDROS VITON LTDA. MAT. FERRO FUNDIDO GG-25 (A) NOME DO J. CONVEYOR & SEL. GOB. DISTR. NOME DA PEÇA HOUSING TRAT. TERM.	DES. <i>Pereira</i> VER. APROV. <i>[Signature]</i> N.º DO CONJ. 191-6647 N.º DA PEÇA 191-15752 N.º DO DES.