


LINHA DE REFERÊNCIA

A

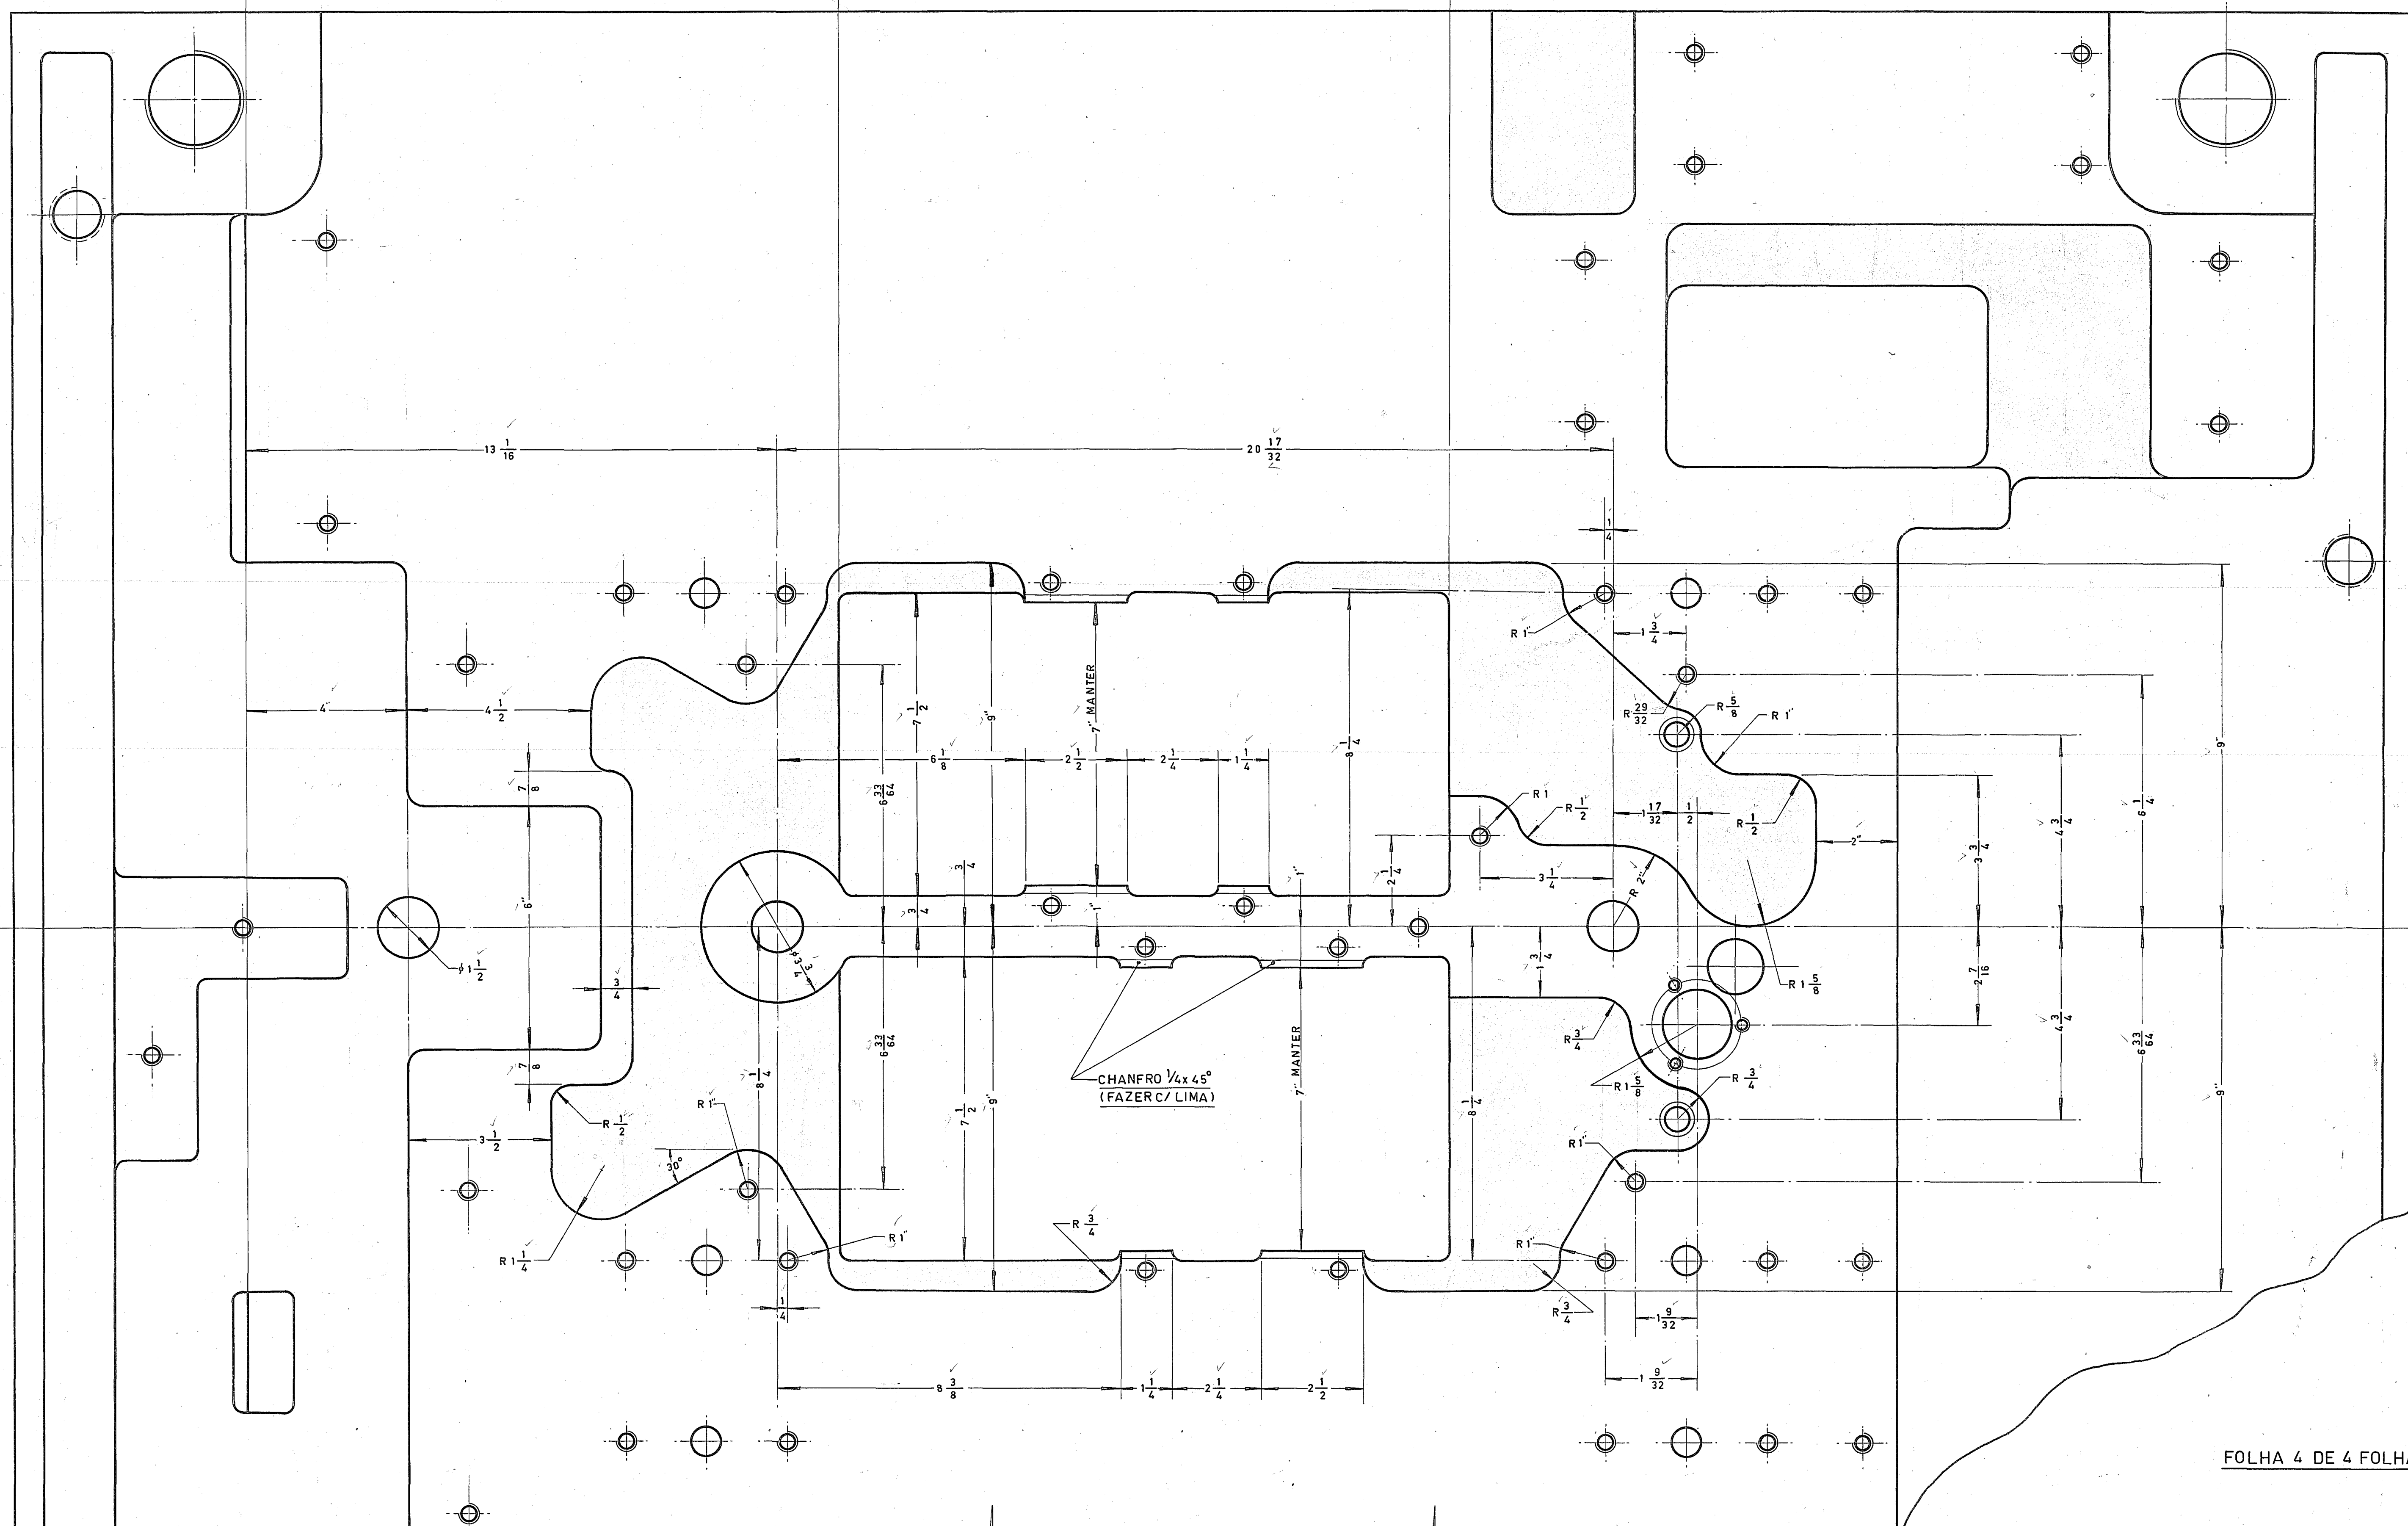

FOLHA 4 DE 4 FOLHAS

27-4-85	DATA: 26-12-85				VIDROS VITON LTDA.			DES. <i>[Signature]</i>
	TOLERÂNCIAS STANDARD PARA SUPERFÍCIES USINADAS SEM TOLERÂNCIA INDICADA				MAT. FERRO FUNDIDO CINZENTO			VER. <i>[Signature]</i>
					M. M. BED AND FRAMES			APROV. <i>[Signature]</i>
					MAQ. I.S. 8 SEC.			N.º DO PROJ. VVM-222
					DETALHE DAS CAVIDADES NO BED			N.º DA PEÇA 915800-700
FRAÇÃO DE 0" AIE 5" ± 1/64 DE 5" AIE 24" ± 1/32 ACIMA DE 24" ± 1/16				TRAT. TERM.			ESCALA 1/2	N.º DO DES.