

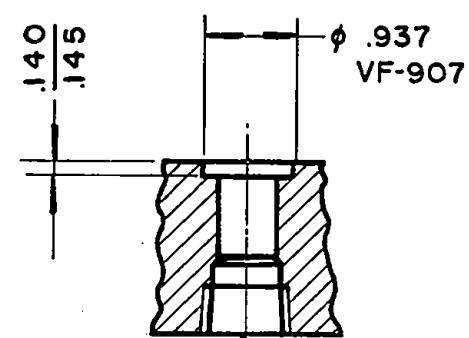


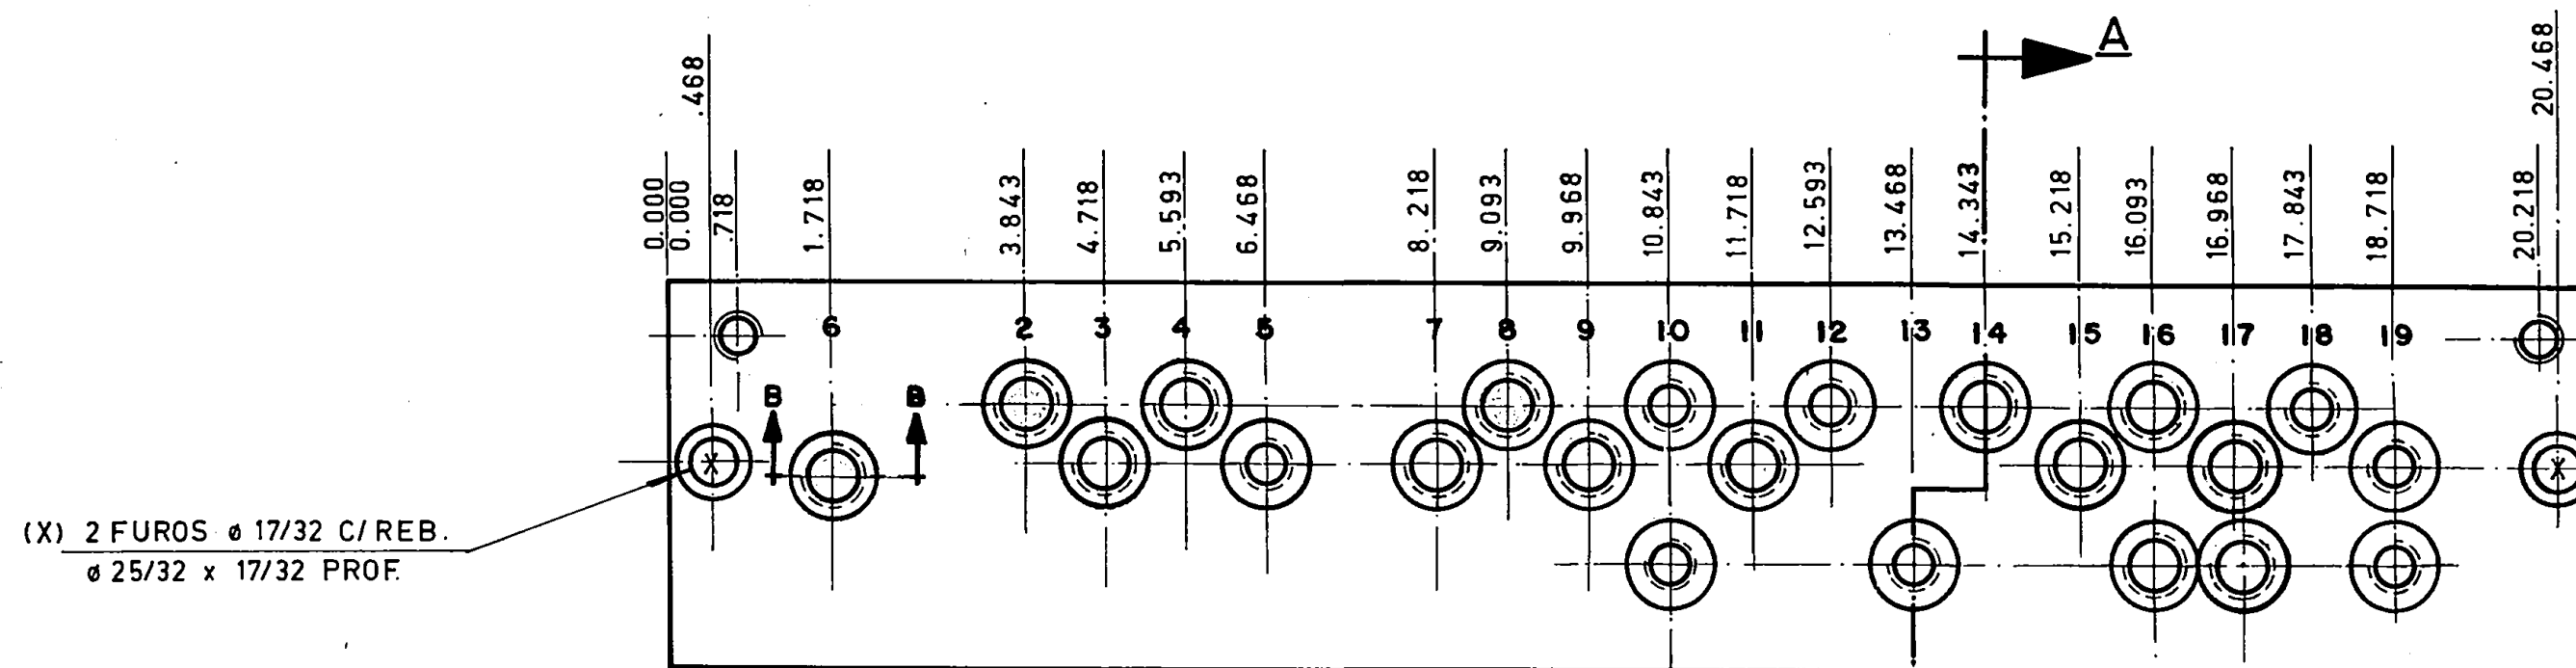


SEÇÃO B-B

3 FUROS ϕ 37/64 C/REB. ϕ 23/32 x
5/8 PROF C/ROSCA 1/2 NPT
NAS SEÇÕES 2-6-8

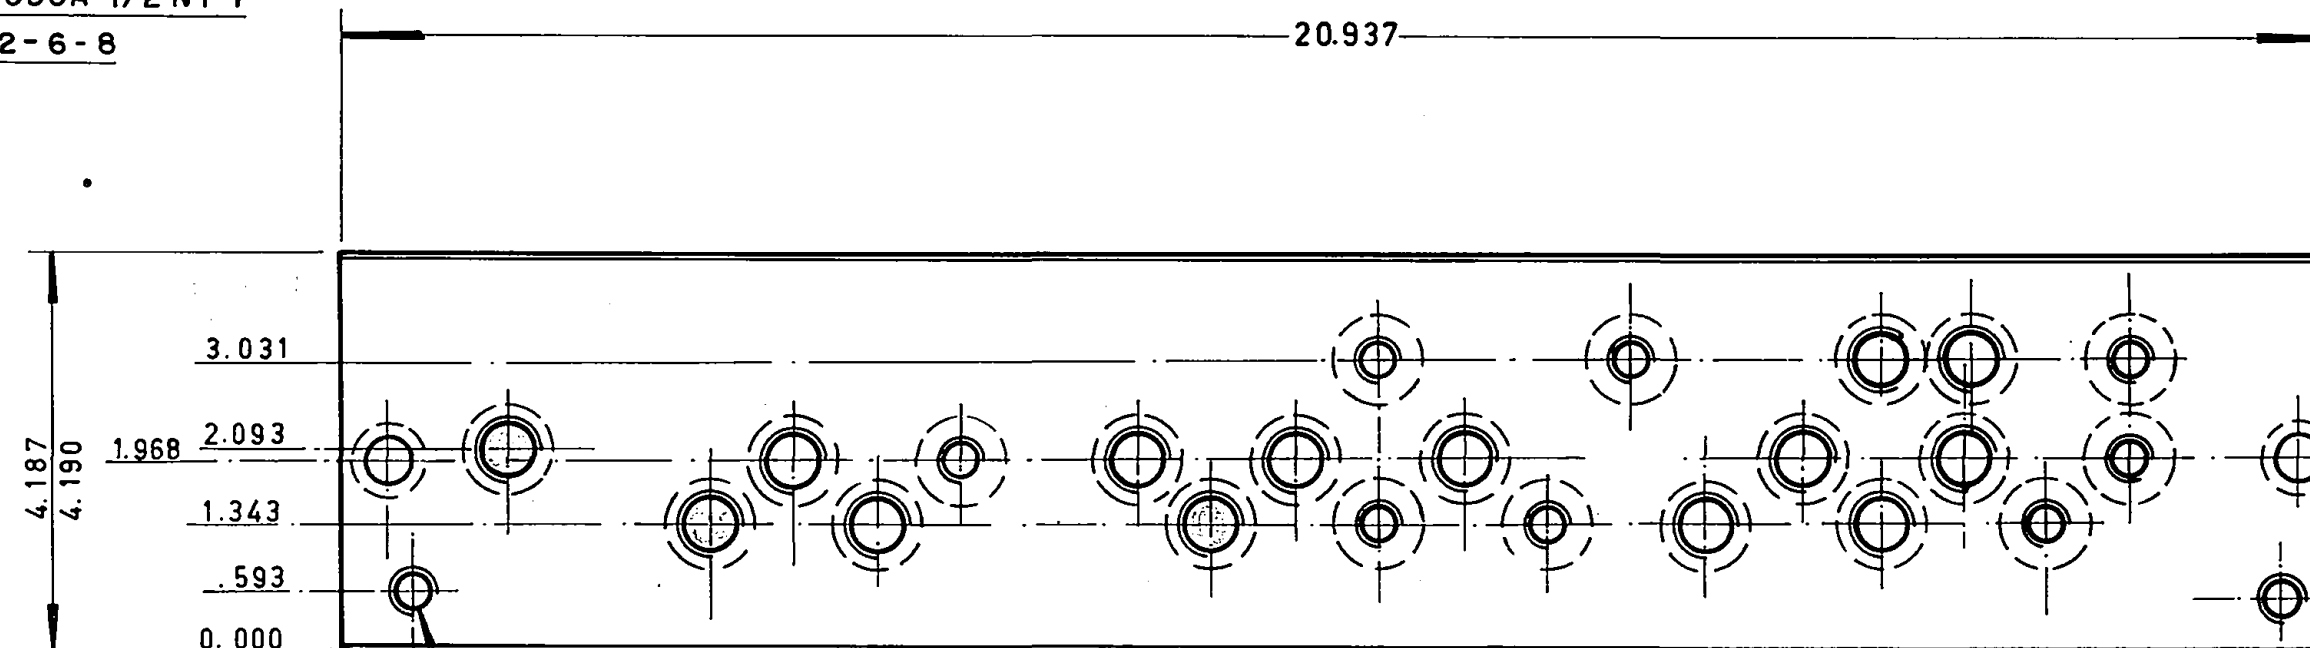

2 FUROS ϕ 27/64 C/ROSCA
 ϕ 1/2 NC - 13 F.P.P. (PASSANTE)

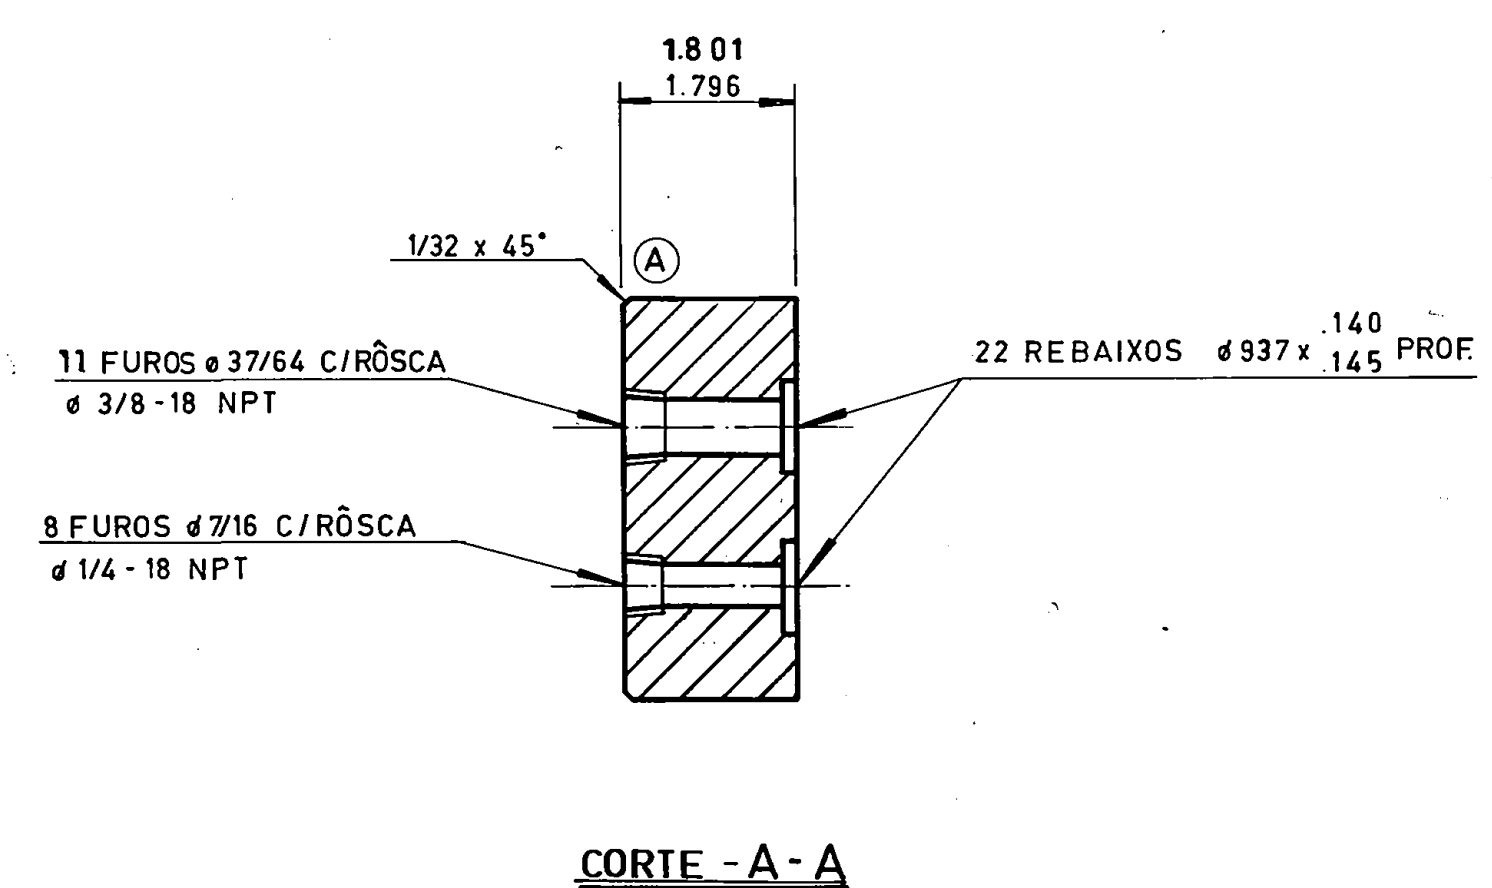

NOTA:

PARA FURAÇÃO USAR
DISP. VD - 327

RET. VERTICAL



ERA ROSCA C	KIYO 21-6.91	B	J. Carlos 25-5-88	A	REVISAO 24.87	DATA: 27-10-86	VIDROS VITON LTDA.		DES. <i>[Signature]</i>
						TOLERANCIAS STANDARD PARA SUPERFICIES USINADAS SEM TOLERANCIA INDICADA	ACAO AÇO SAE 1020	APROV. <i>[Signature]</i>	VER. <i>[Signature]</i>
21-6.91	25-5-88	24.87	24.87	24.87	24.87	FRACAO DE 0" ATE 5" $\pm$ 1/64 DE 5" ATE 24" $\pm$ 1/32 ACIMA DE 24" $\pm$ 1/16	SECTION FRAME ASS'Y, E' MODULE SYSTEM	H.º DA COM. VVM-286	H.º DA PEÇA 191-20016
						ESCALA 1:2	MANIFOLD (19 ESTAÇÕES)	TERC.	DES.