
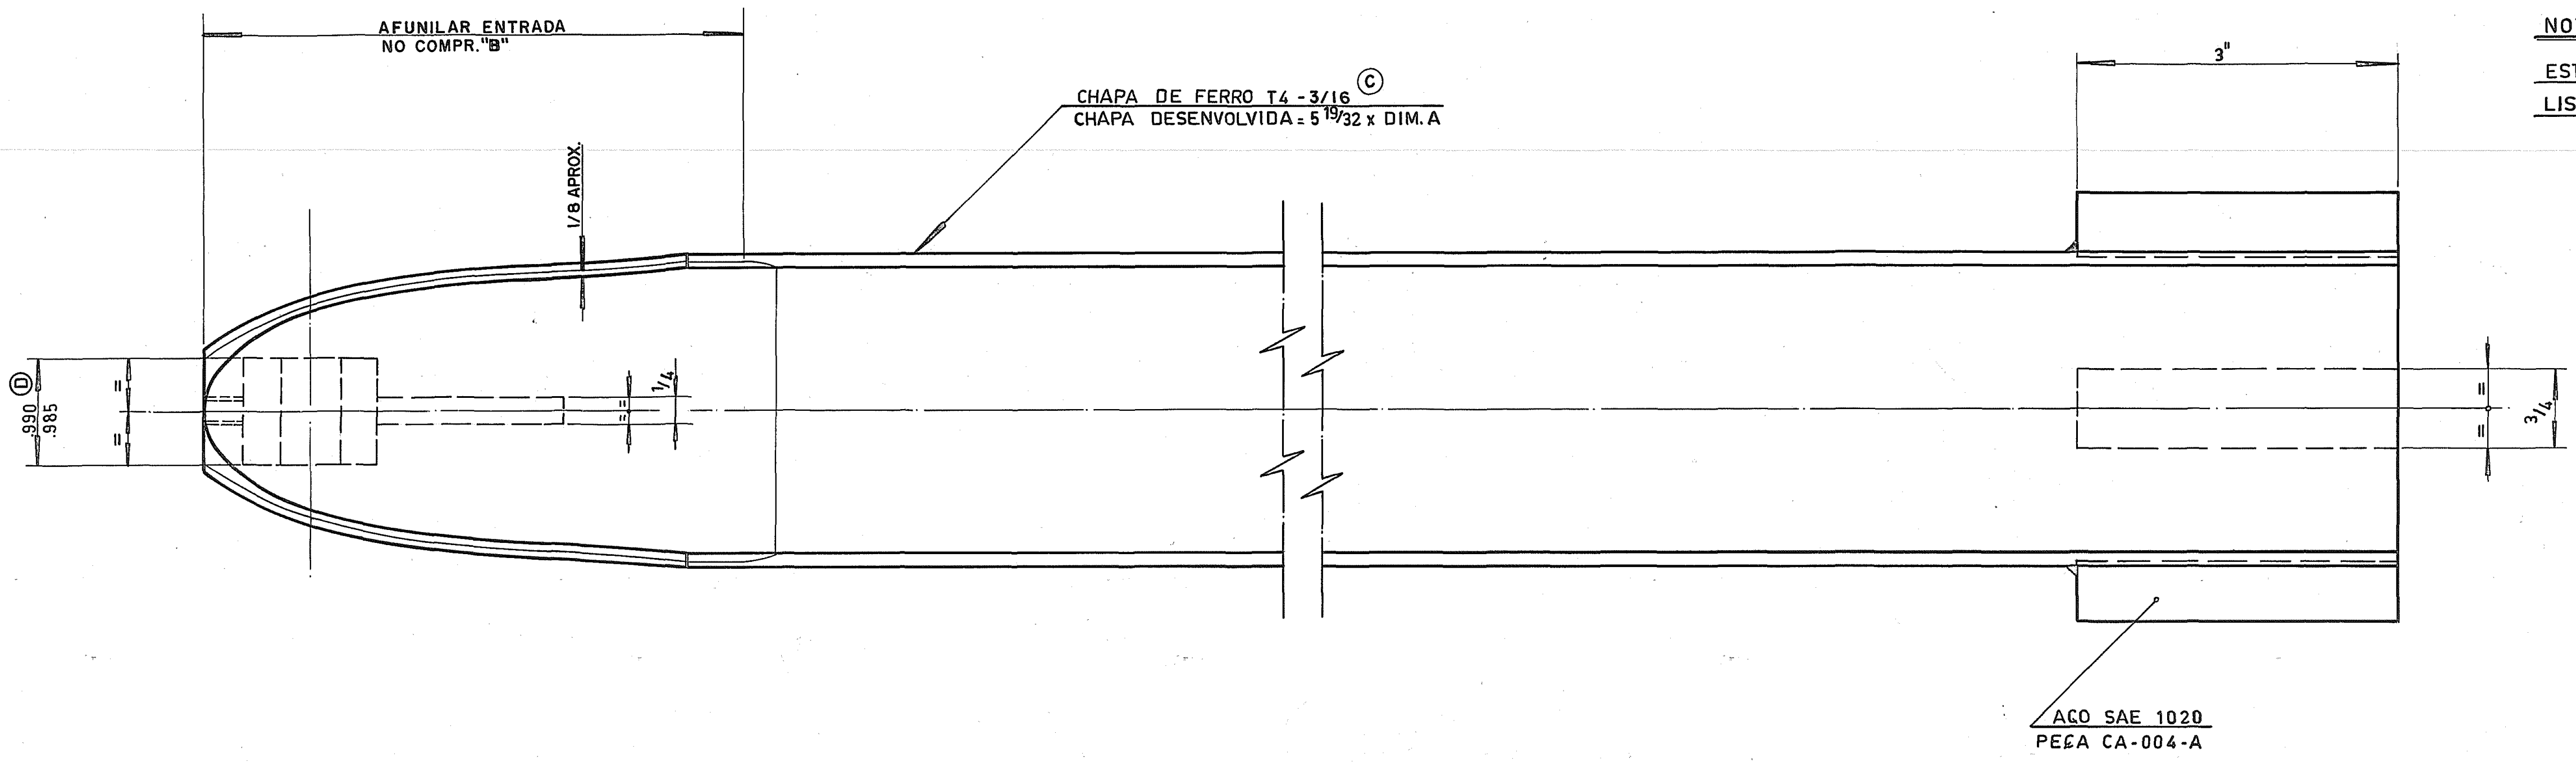
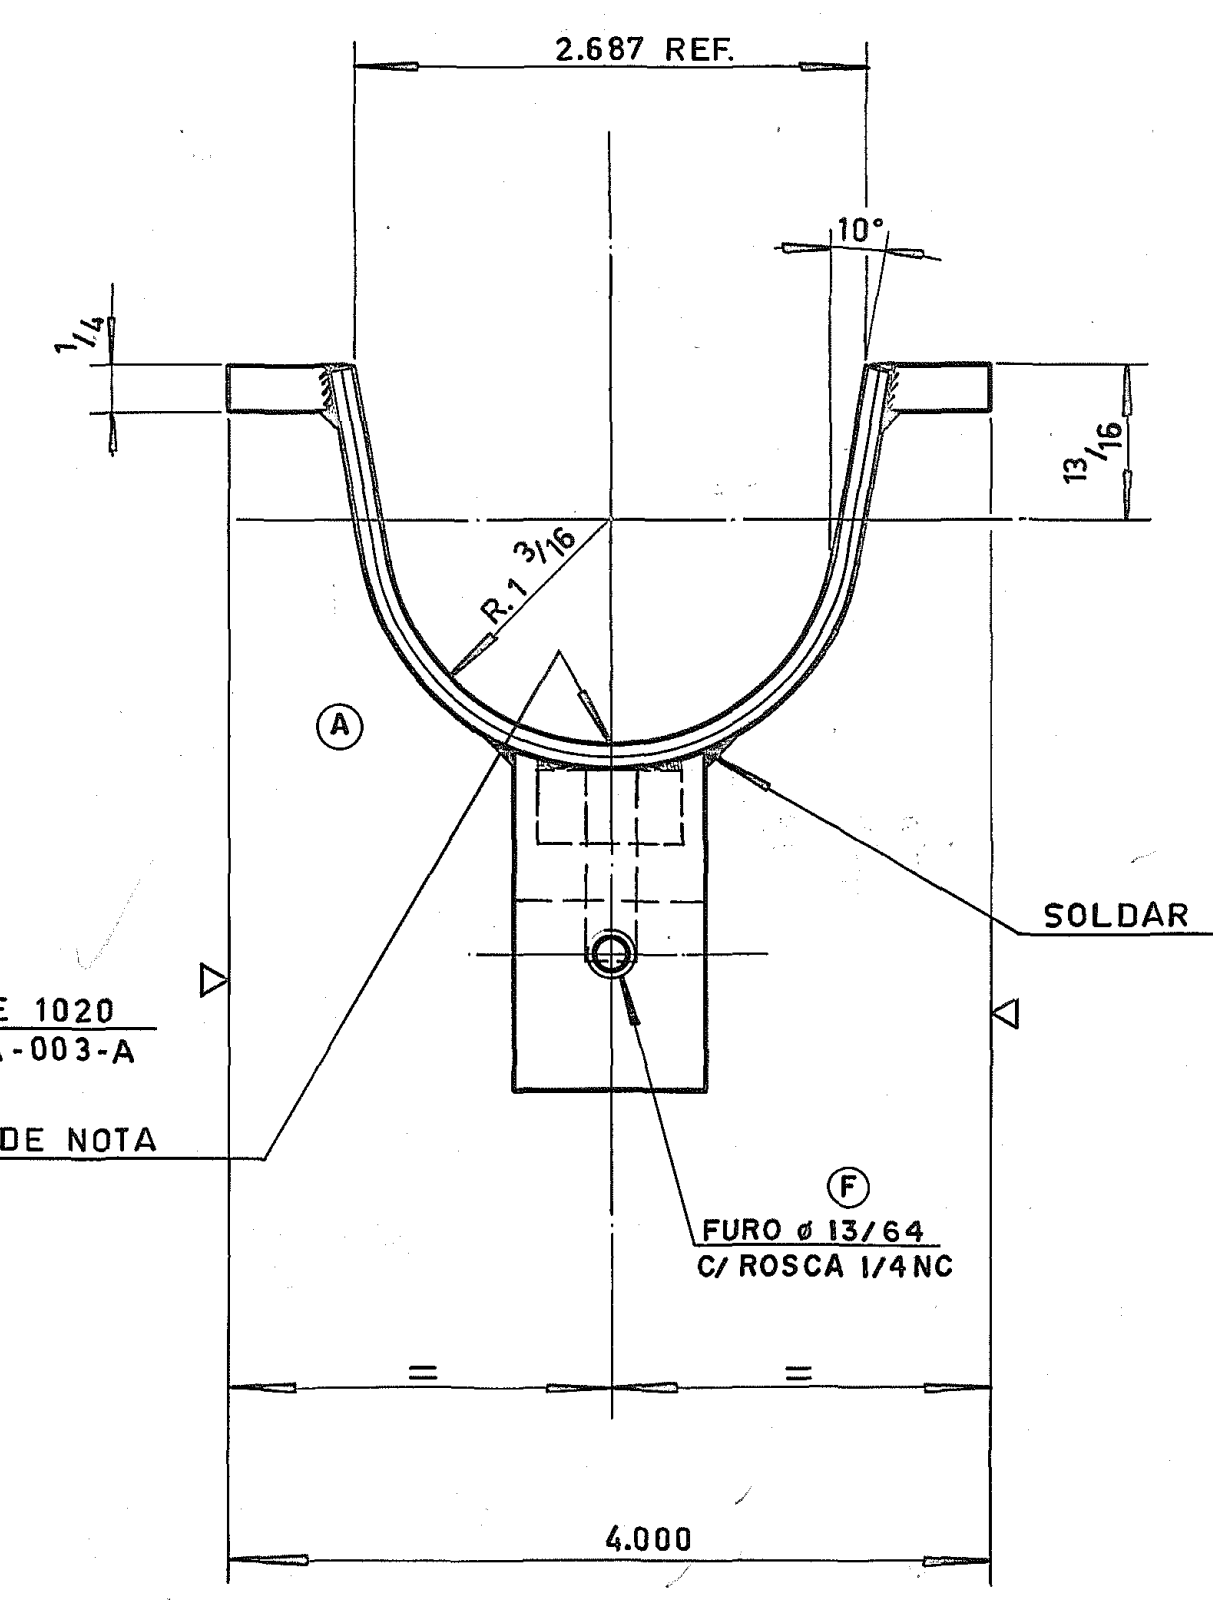


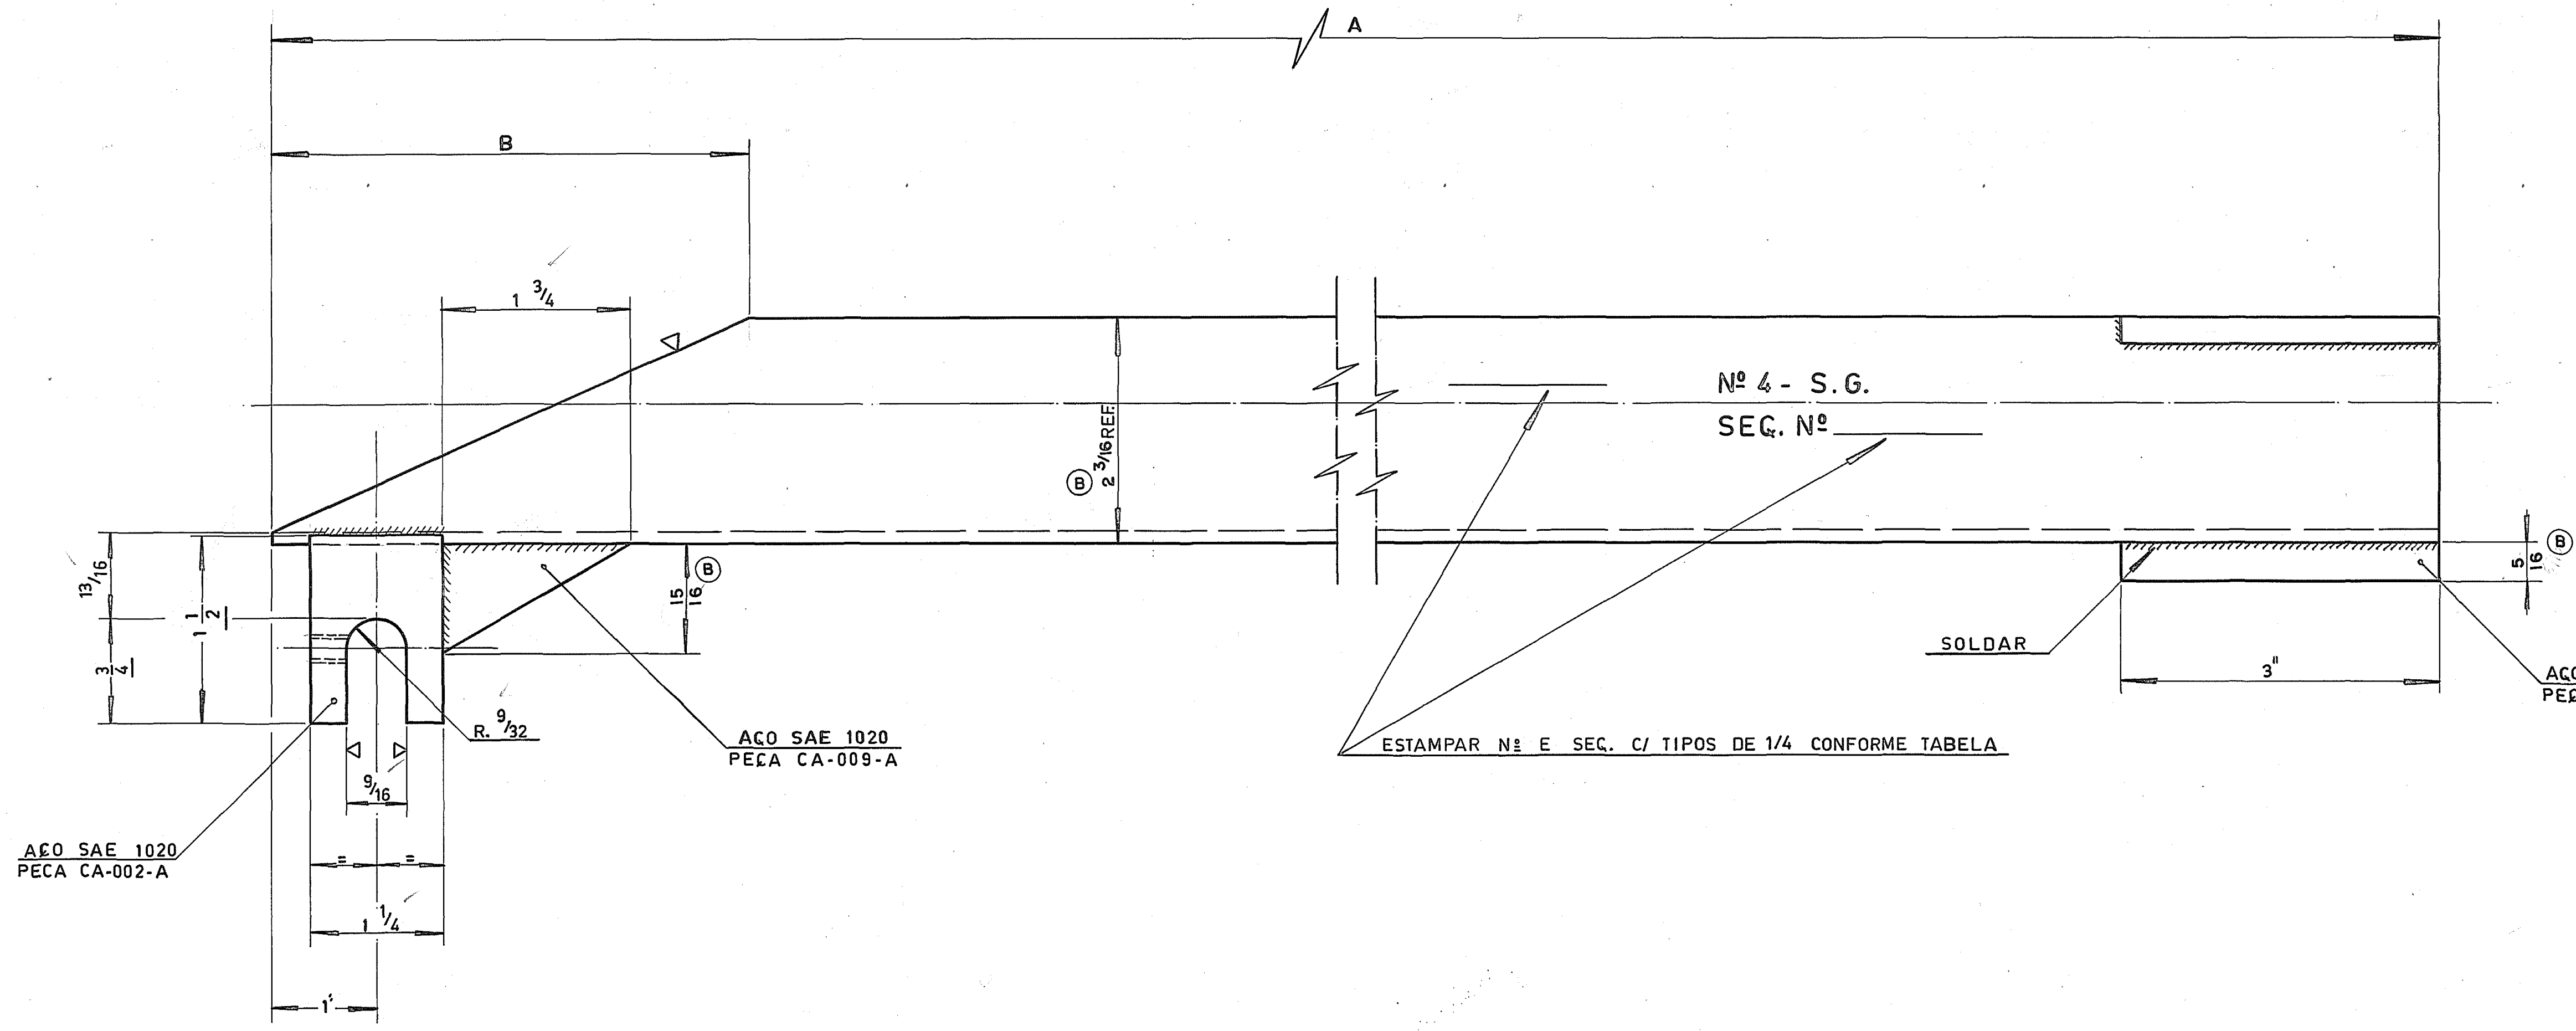

NOTA-
ESTAS SUPERFÍCIES INTERNAS DEVEM SER PERFEITAMENTE LISAS P/ ACEITAR SOMENTE POLIMENTO.

NOTA - DOBRAR CHAPA C/ PUNÇÃO Nº VD-1829-22

191-15739	24 5/8	4 1/2	SEC. 3 & 4	SEC. 4 & 5
VV-3513	33 1/2	4 1/2	SEC. 2 & 5	SEC. 3 & 6
23-7158	67"	8"		SEC. 1 & 8
23-7155	49"	8"	SEC. 1 & 6	SEC. 2 & 7
PEÇA Nº	DIM. A	DIM. B	MAQ. 15.6 SEC. C/DIST. GOTAS	MAQ. 15.8 SEC. C/DIST. GOTAS

191-15739	24 5/8	4 1/2	SEC. 3 & 4	SEC. 4 & 5
VV-3513	33 1/2	4 1/2	SEC. 2 & 5	SEC. 3 & 6
23-7158	67"	8"		SEC. 1 & 8
23-7155	49"	8"	SEC. 1 & 6	SEC. 2 & 7
PEÇA Nº	DIM. A	DIM. B	MAQ. 15.6 SEC. C/DIST. GOTAS	MAQ. 15.8 SEC. C/DIST. GOTAS