
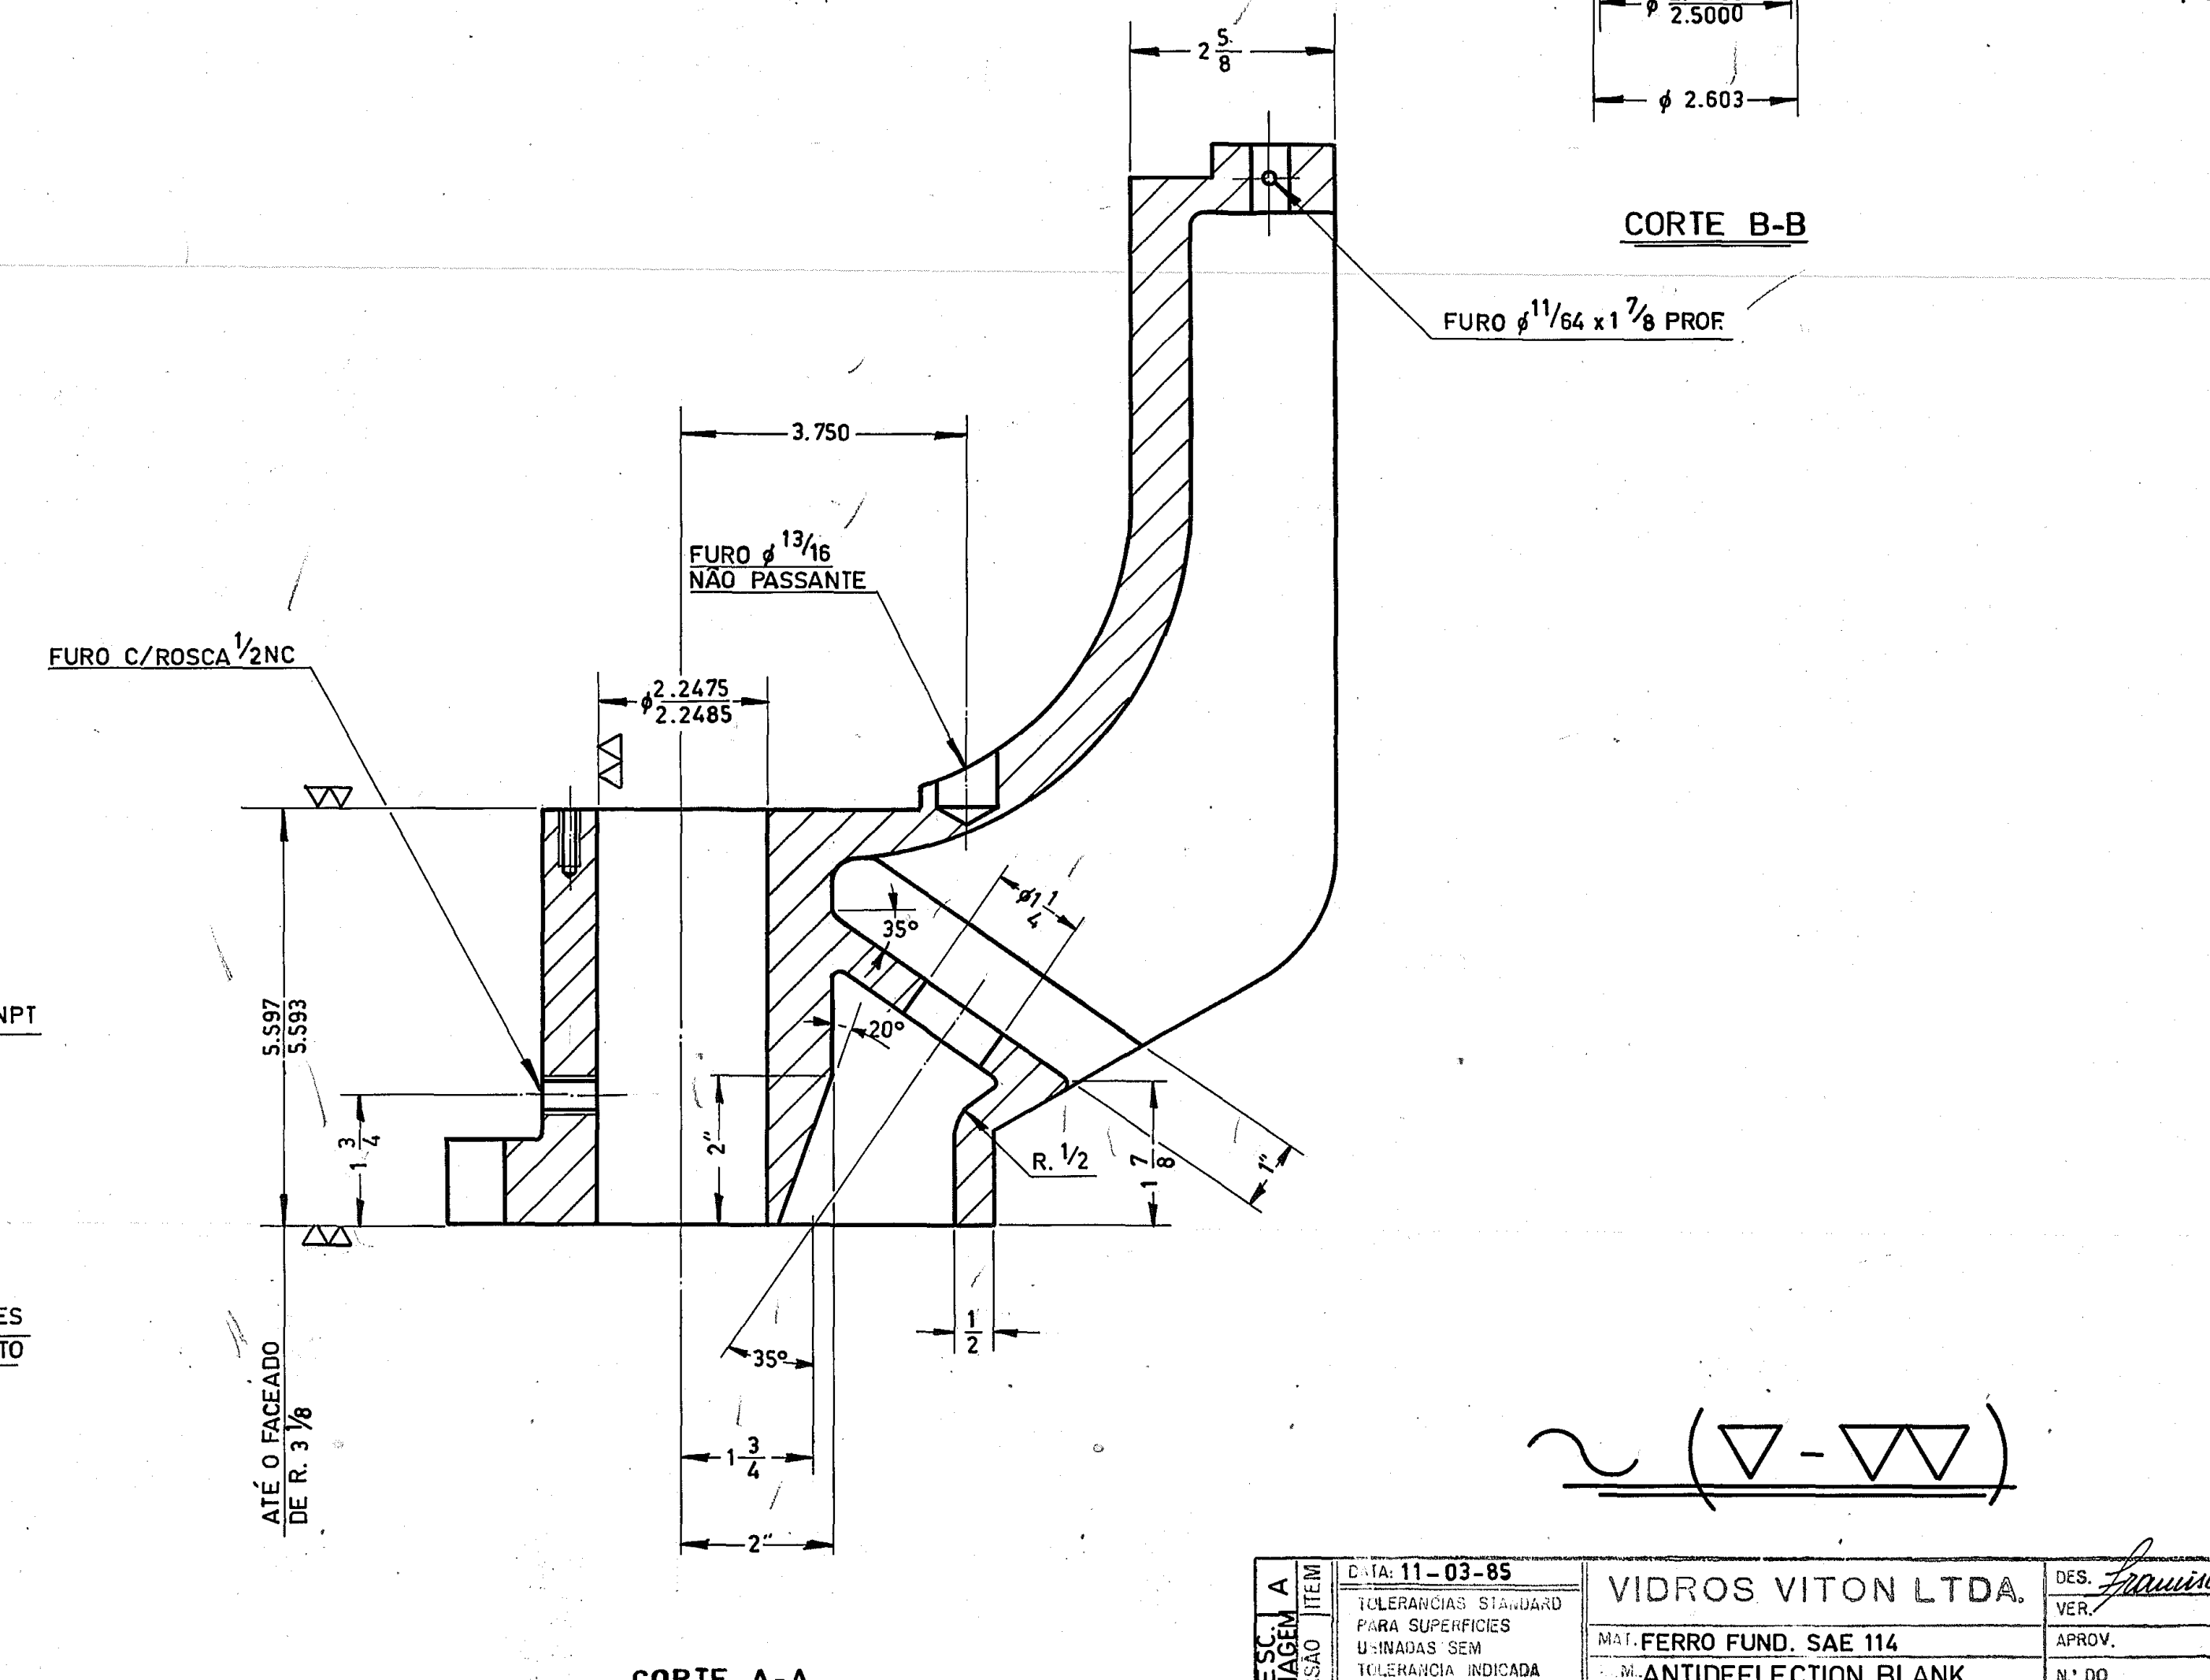
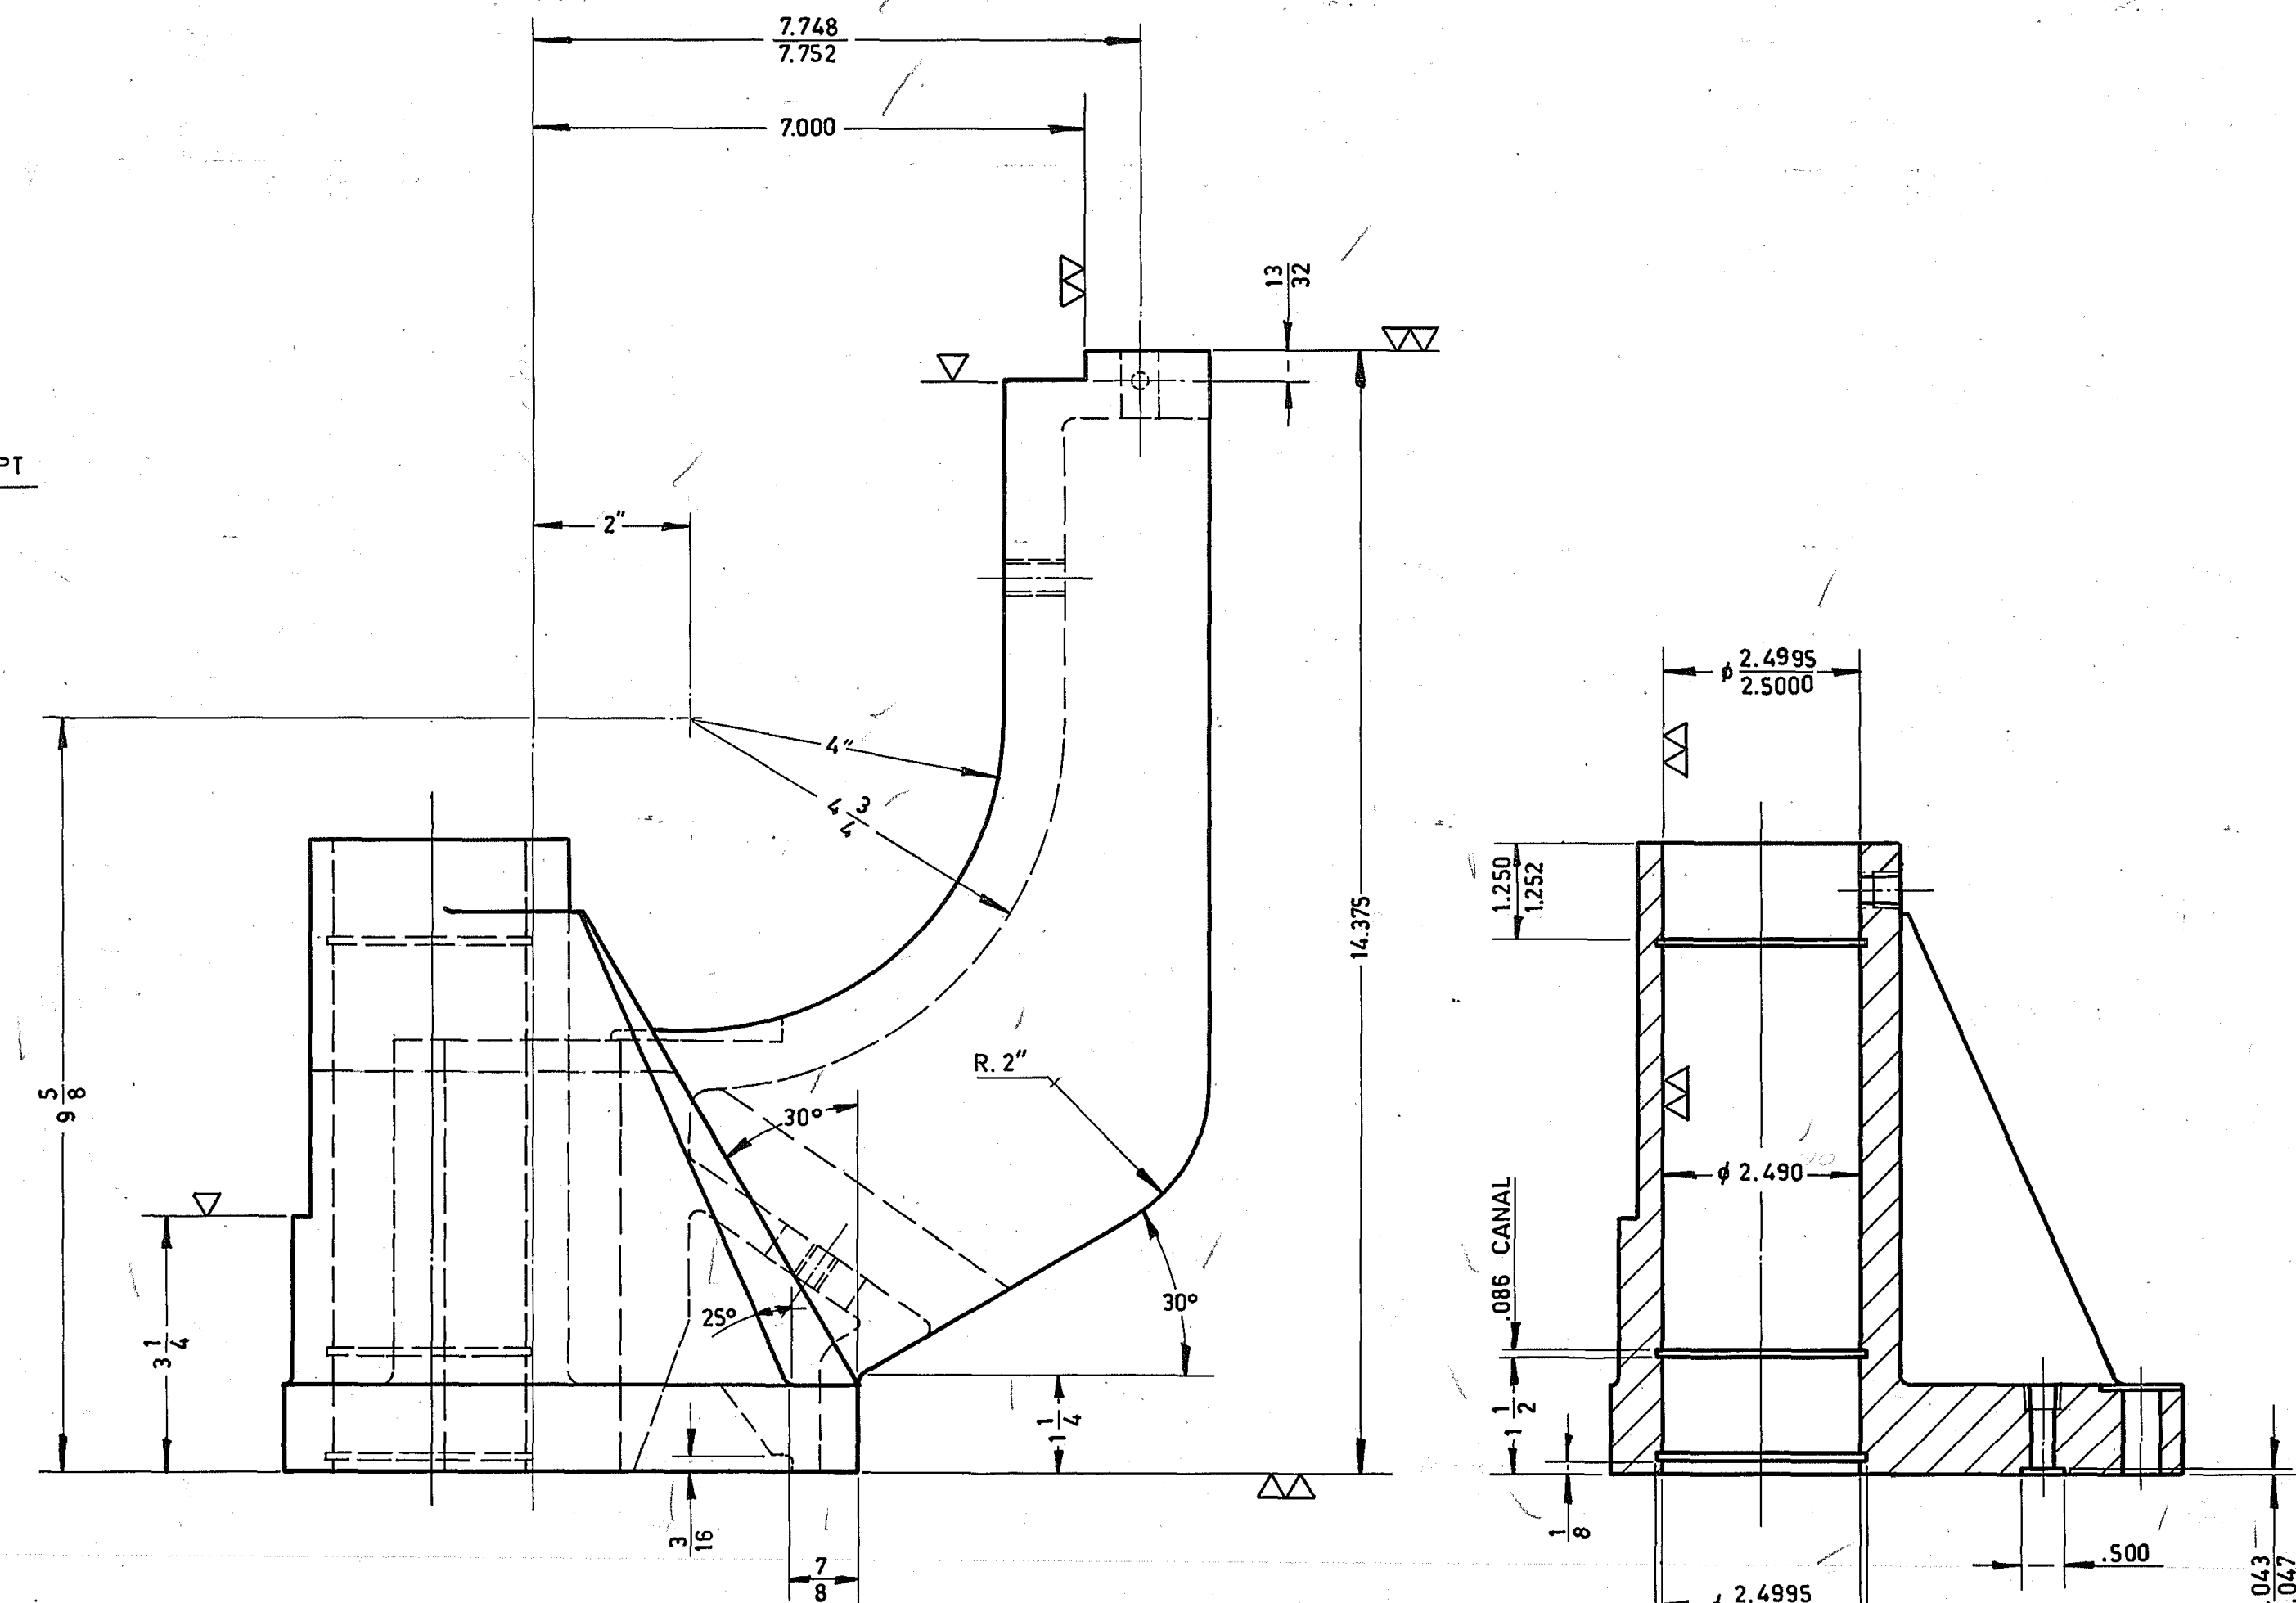


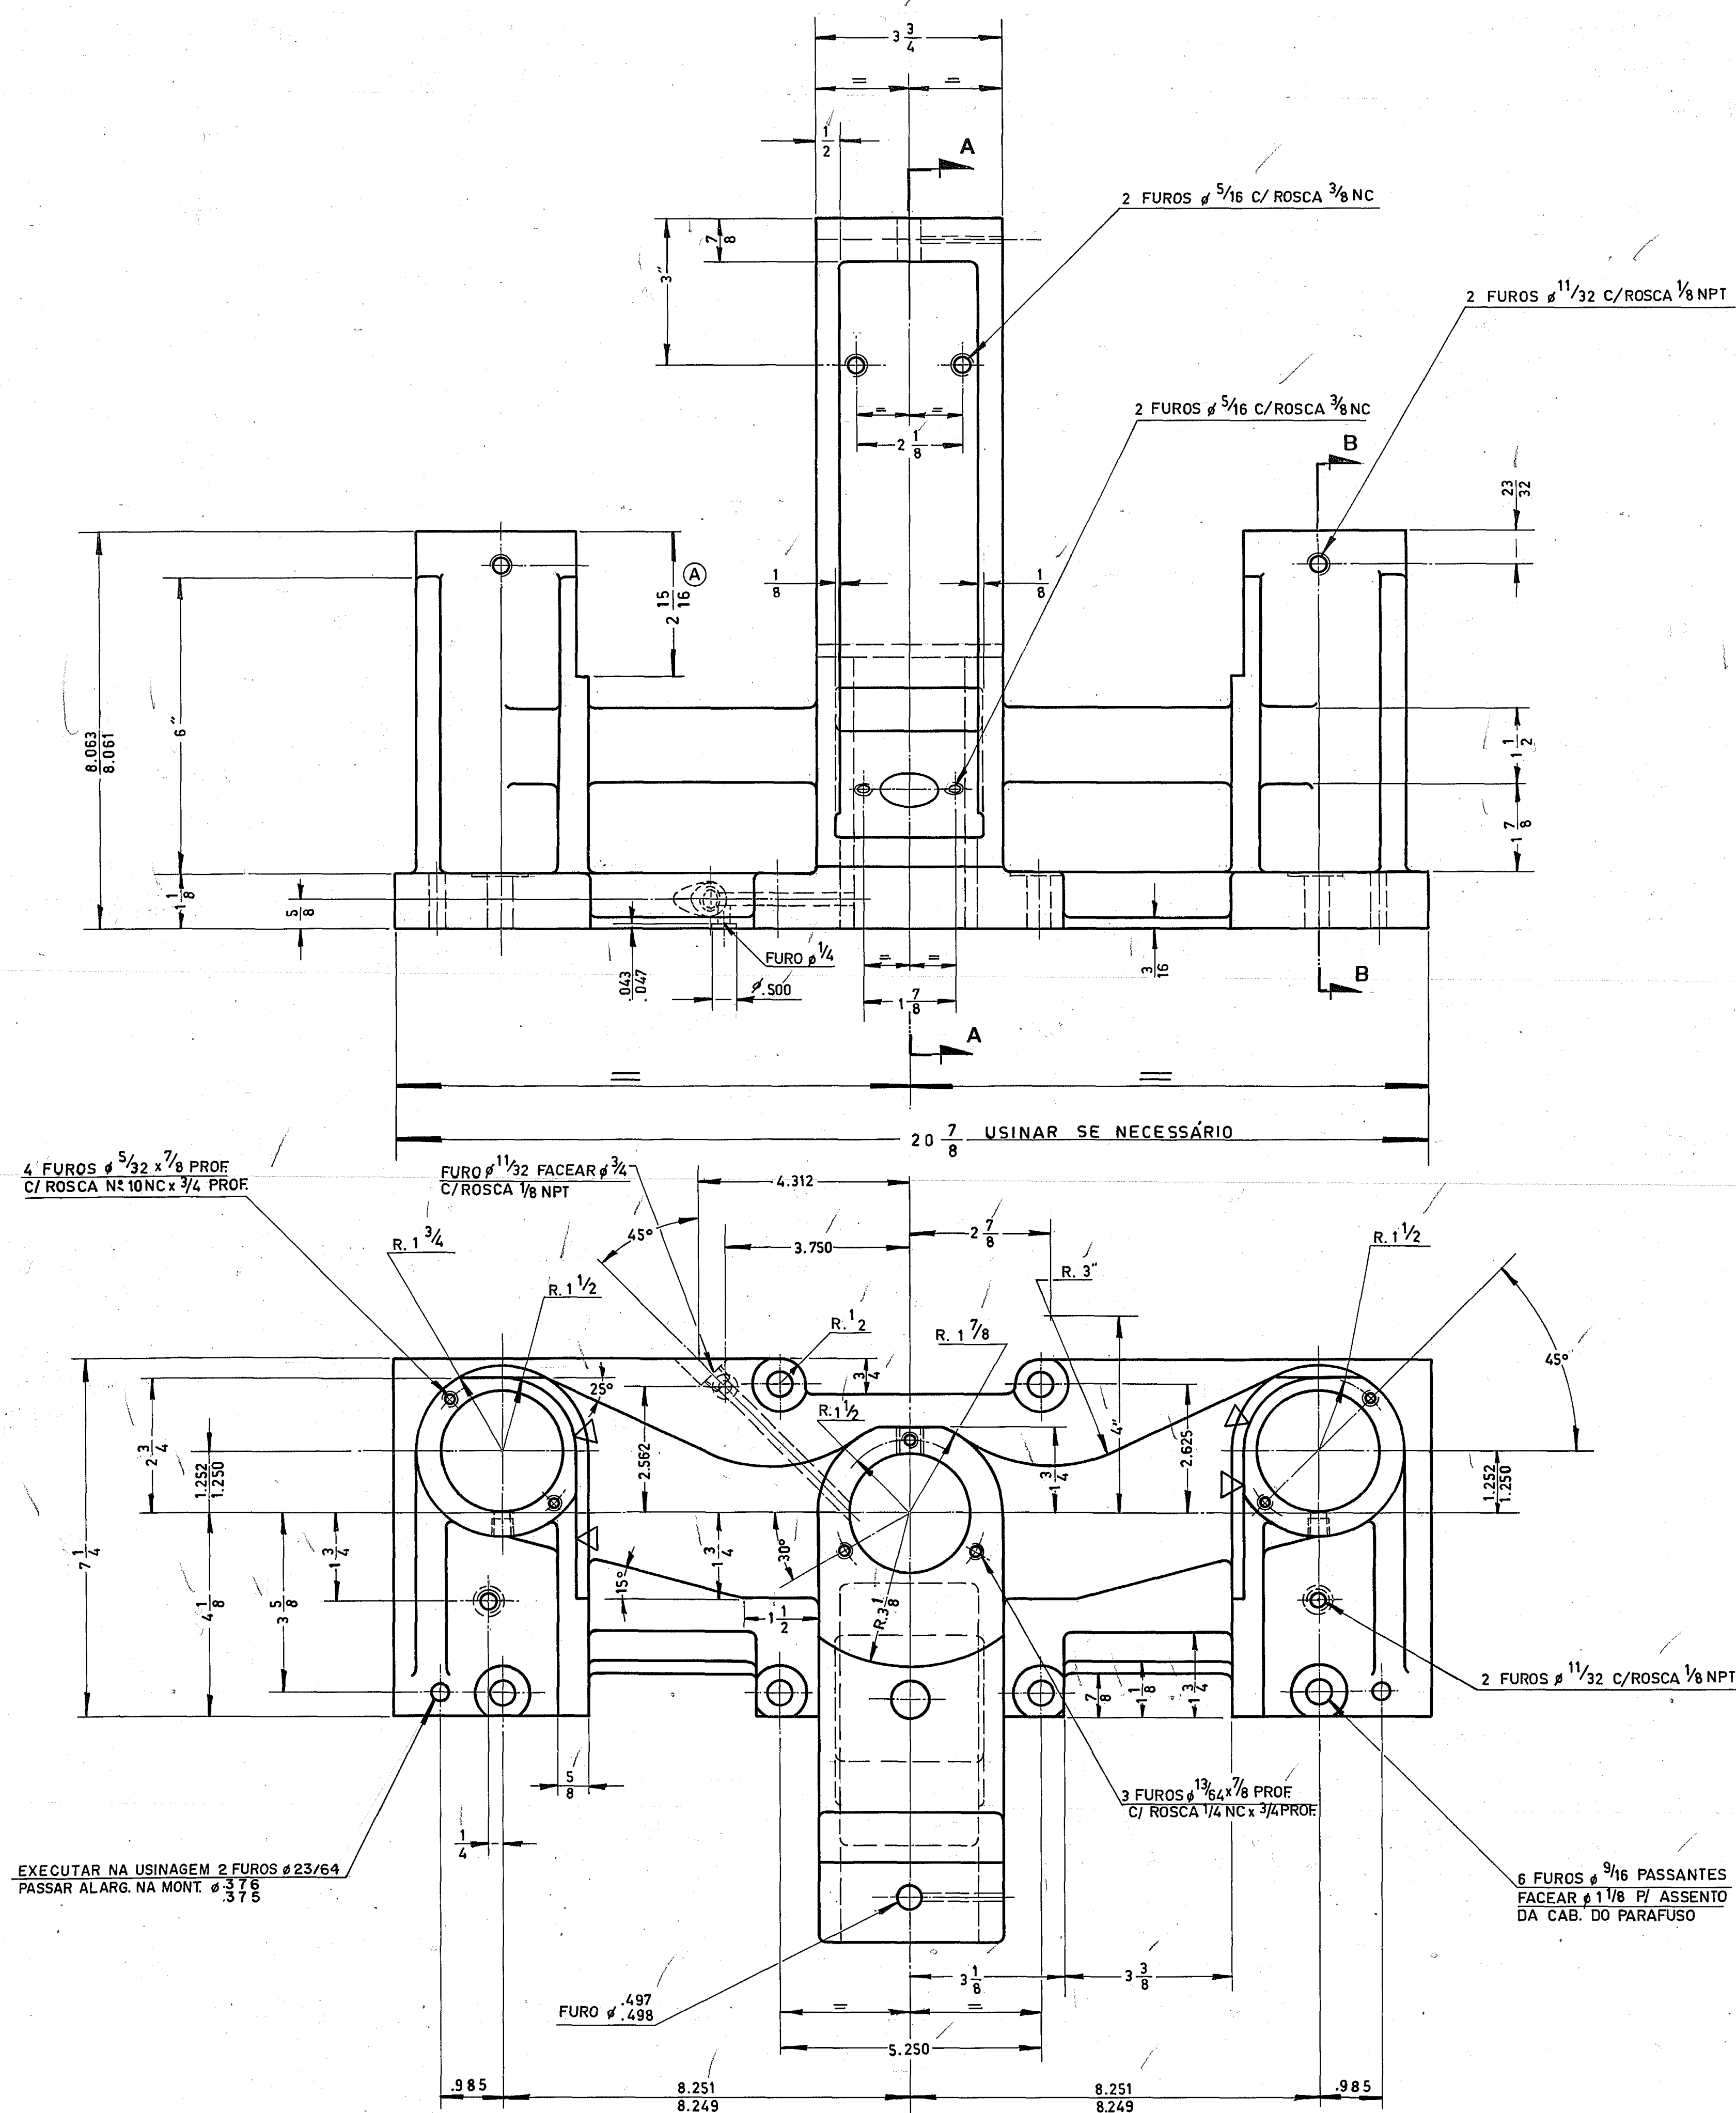

D-1A-11-03-85		VIDROS VITON LTDA.		DES. <i>Pravins</i>
TOLERANCIAS STANDARD PARA SUPERFICIES UNIDADES SEM TOLERANCIA INDICADA		MAT. FERRO FUND. SAE 114		APROV.
DEGRADAL ± 0.05 "		M. ANTIDEFLECTION BLANK MOLD BRACKET		N.º DO PROJ. WM-262
FRAÇÃO DE 0" ATÉ 5" $\pm 1/64$ DE 5" ATÉ 24" $\pm 1/32$ ACIMA DE 24" $\pm 1/16$		BLANK BRACKET 5 C.C.		N.º DA 5000-552-PEÇA 512-1
ESCALA 1/2		N.º DO DES.		