

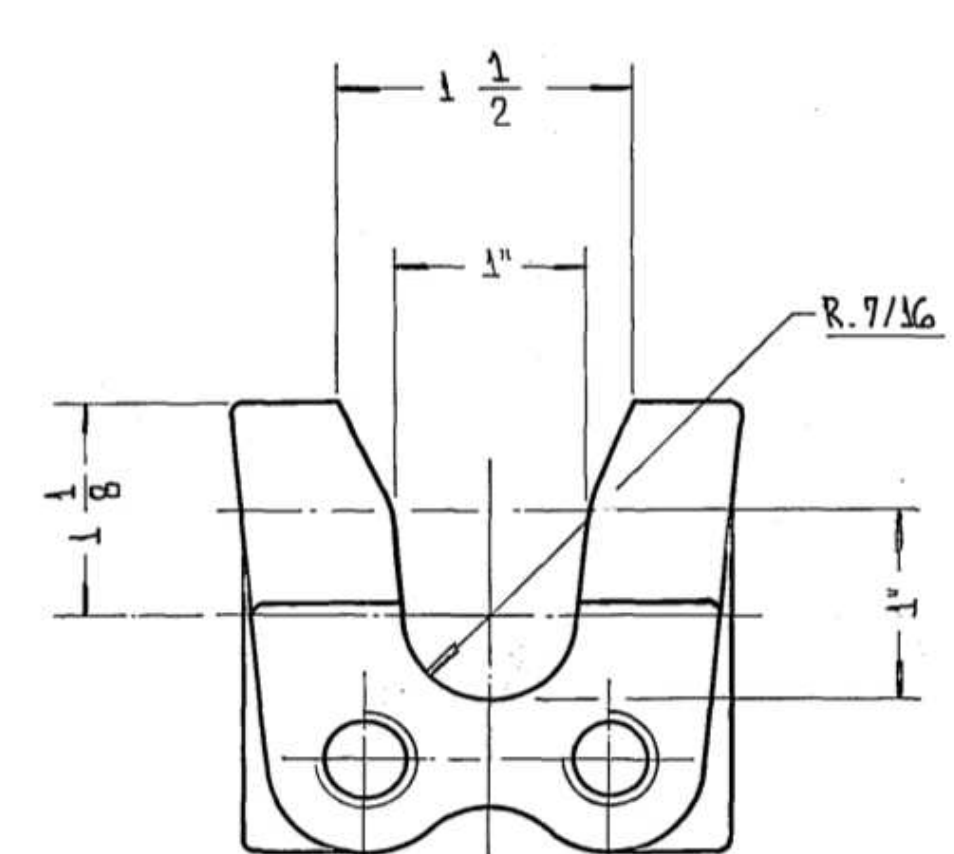
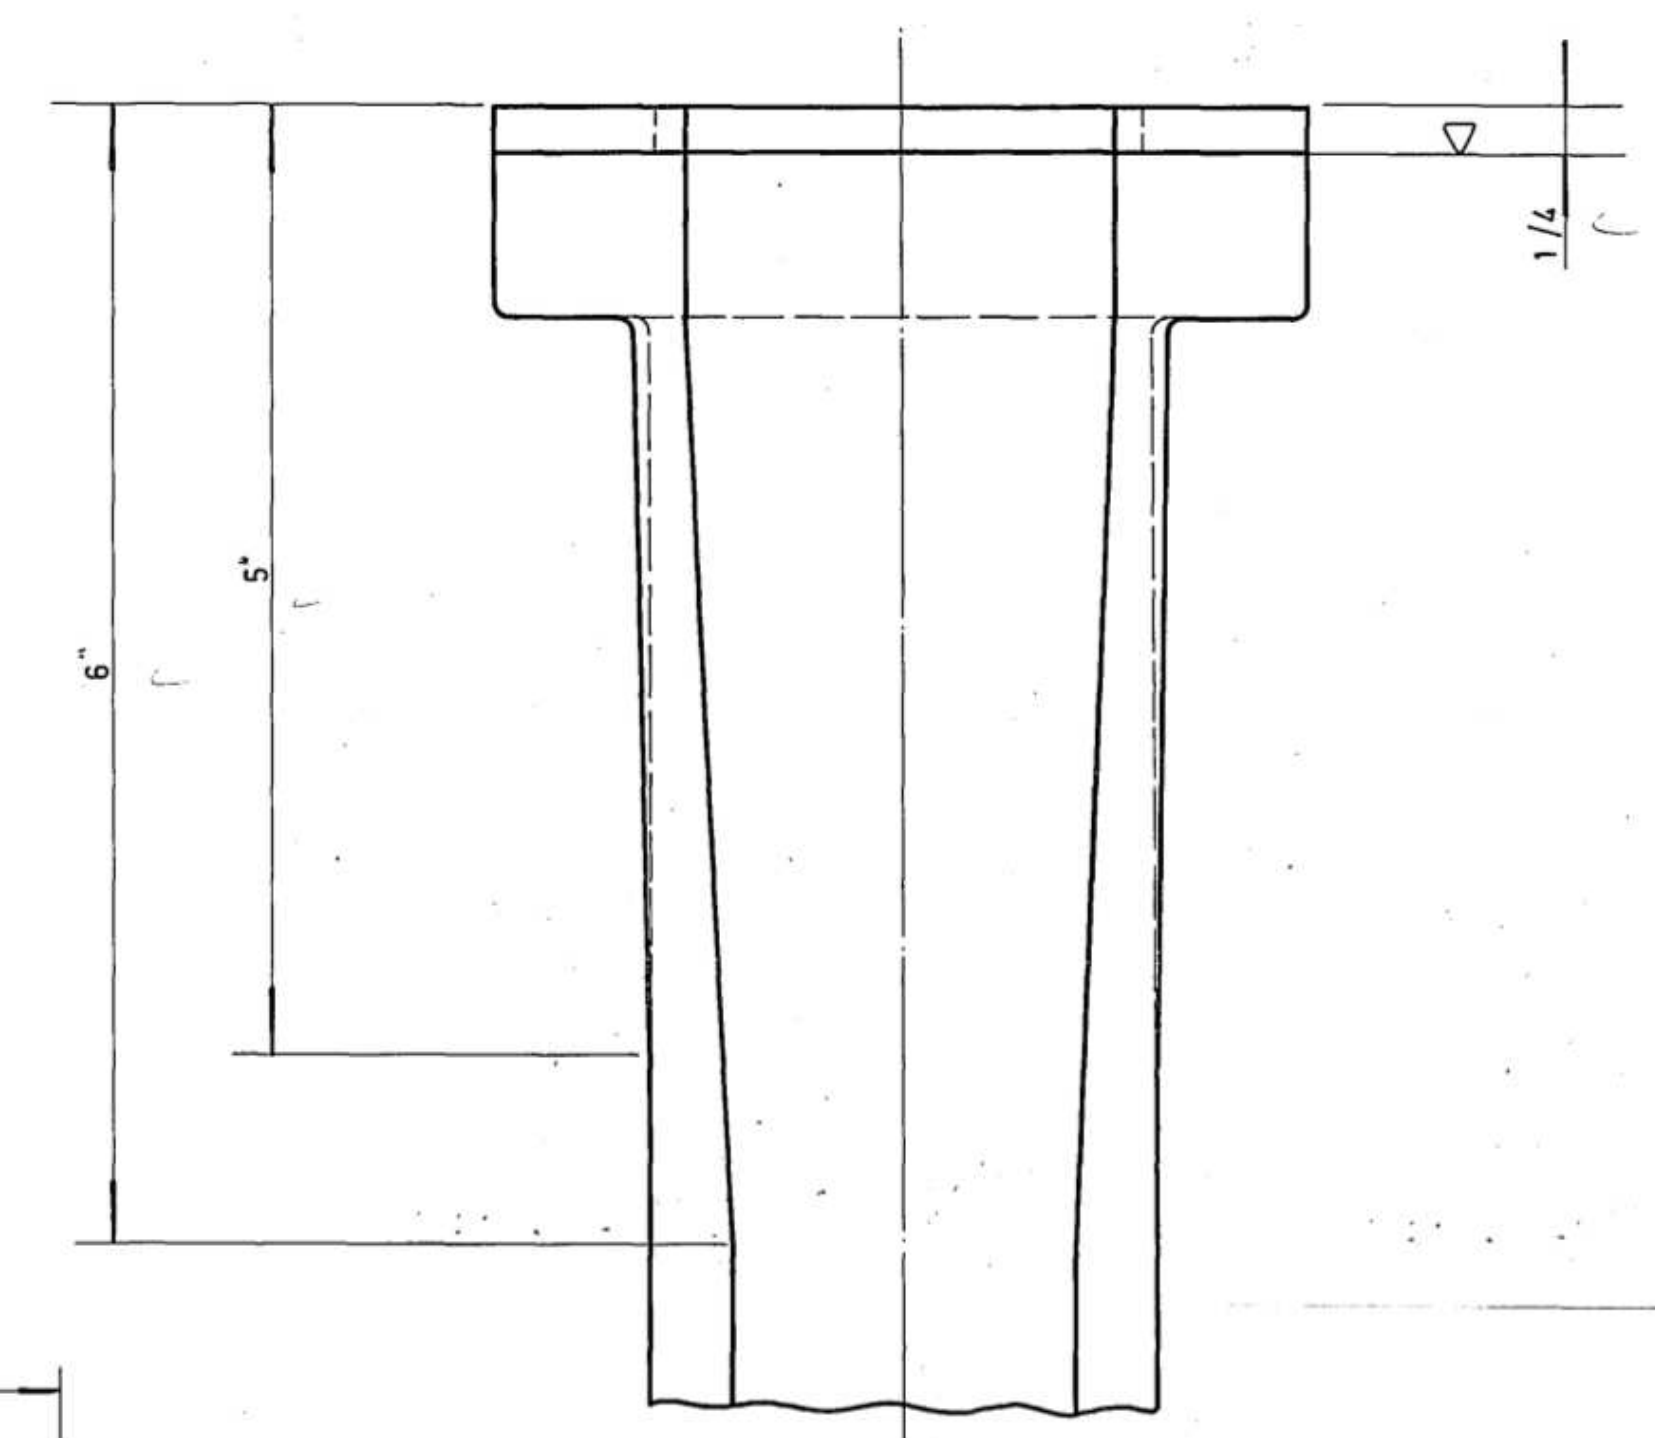


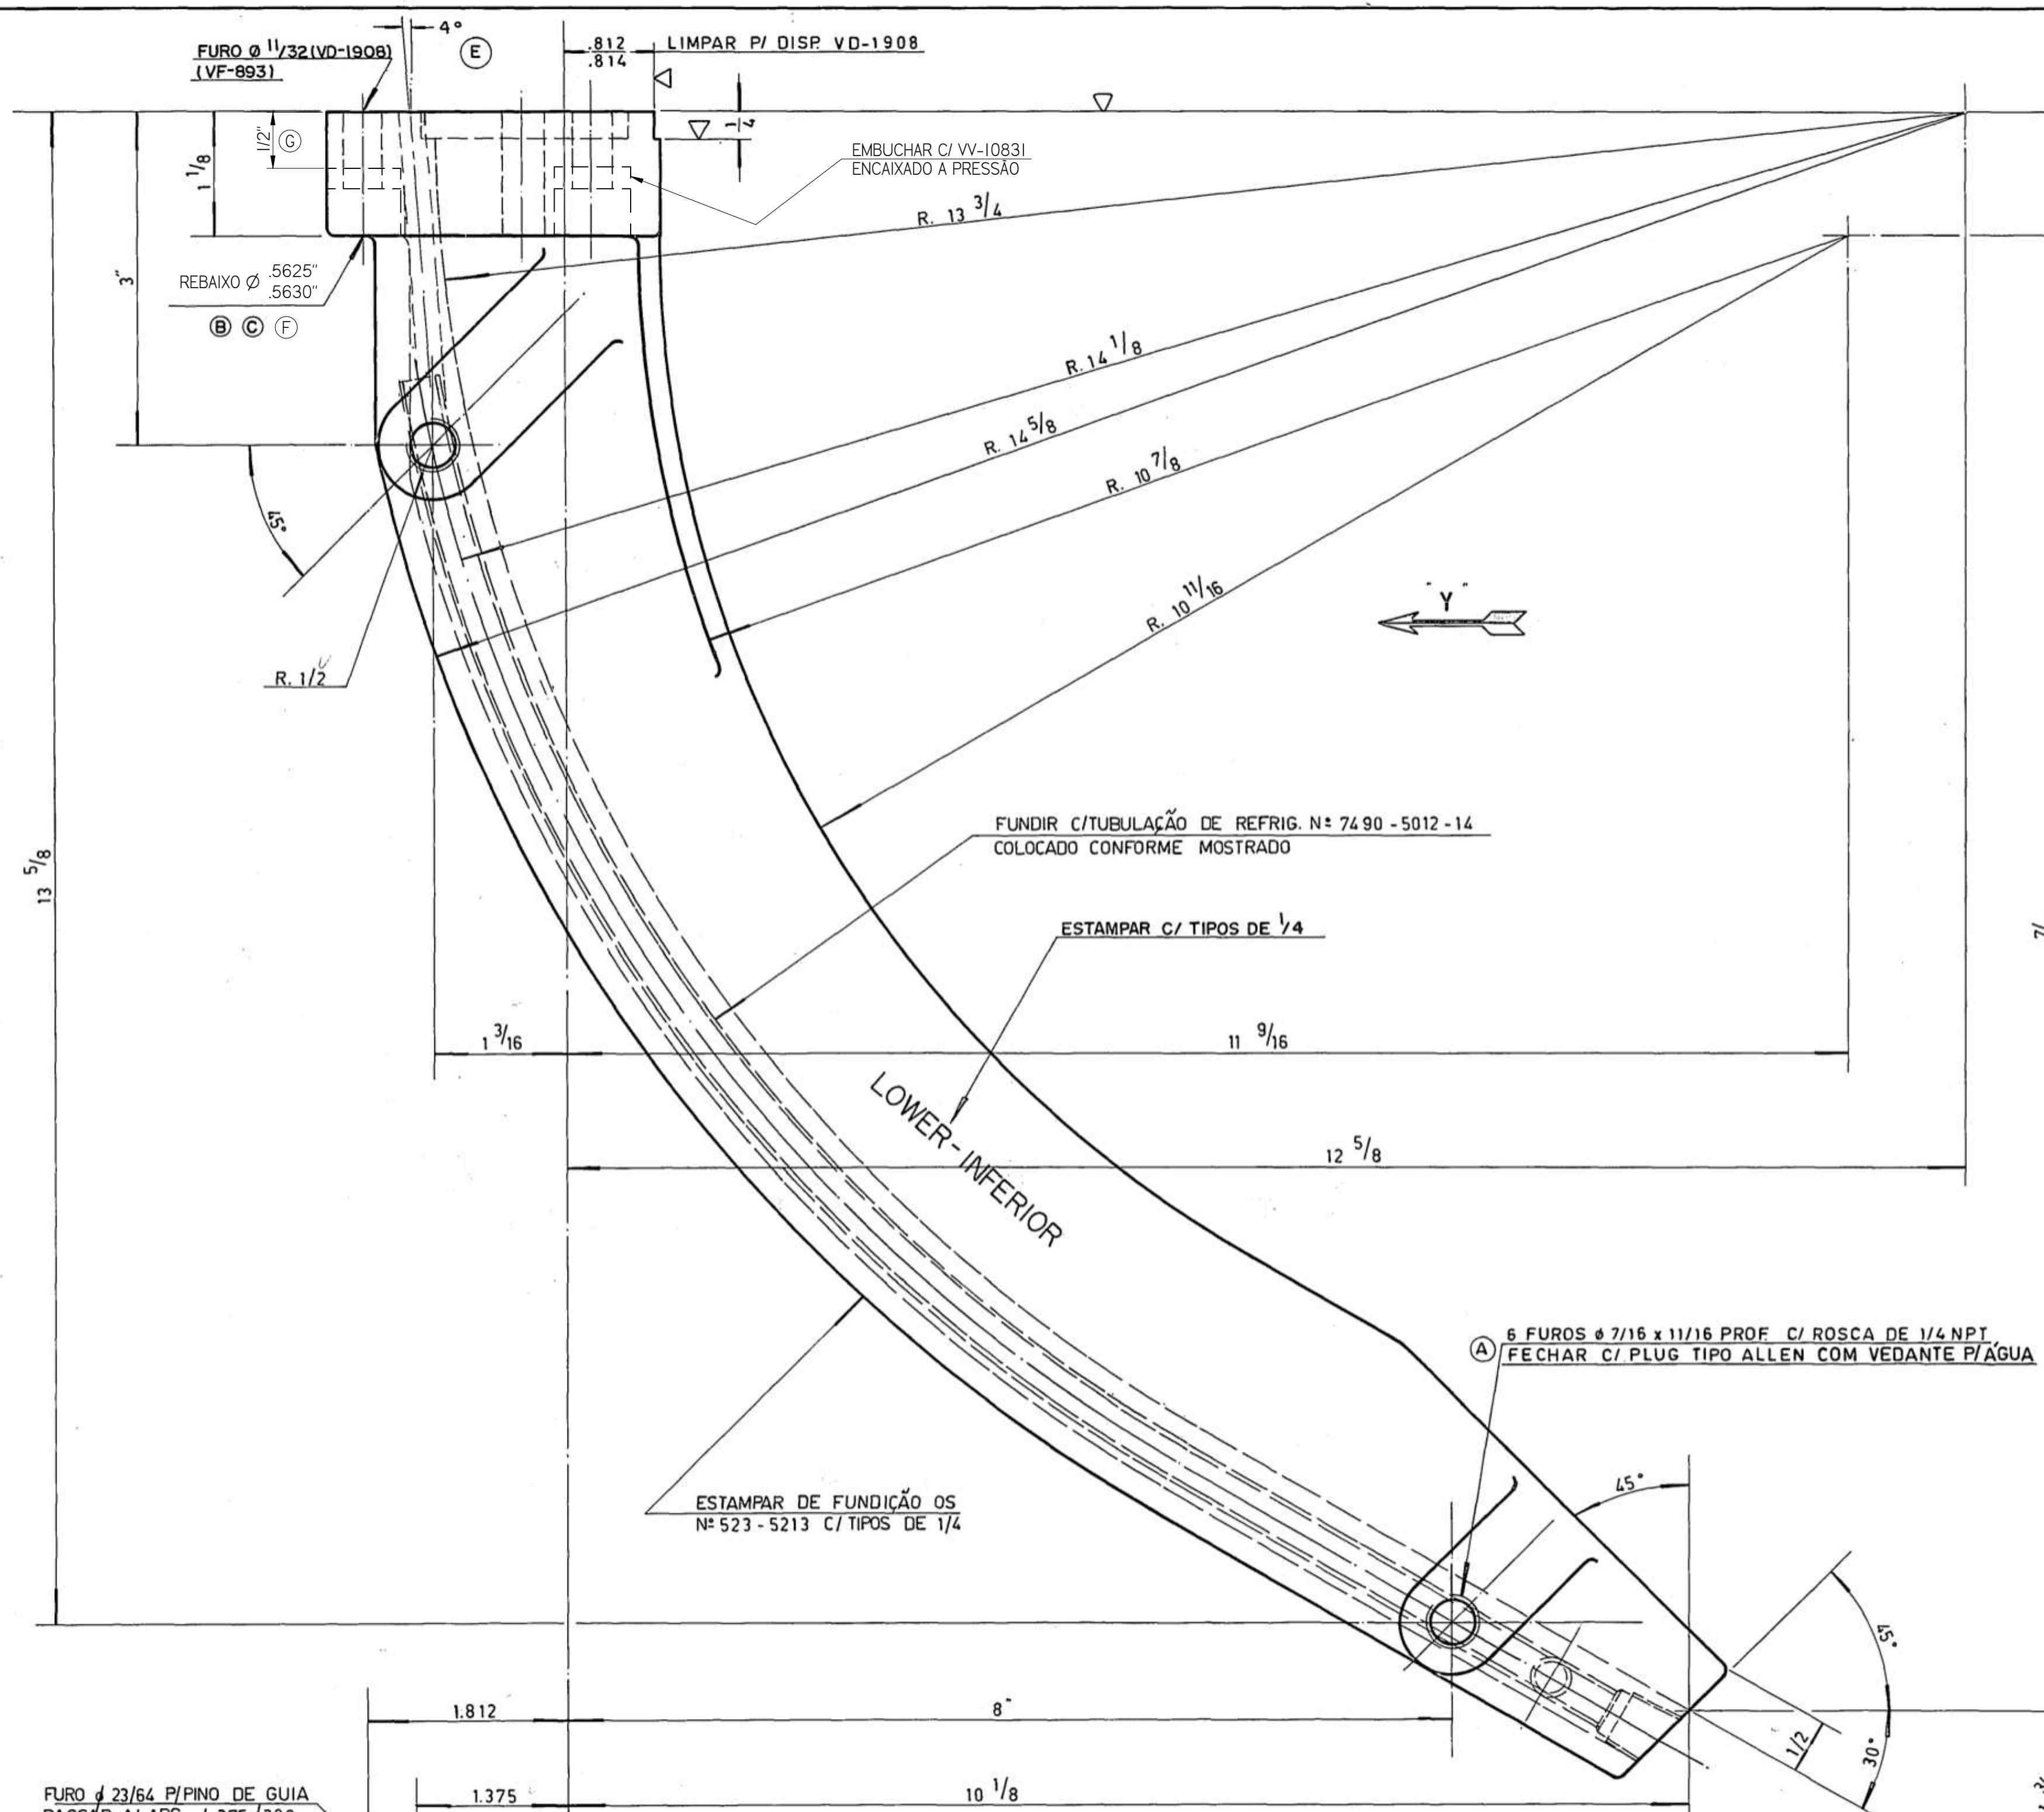


VISTA P' X1
PARA PEÇA Nº 523-5213-7/8
USAR ESTA VISTA

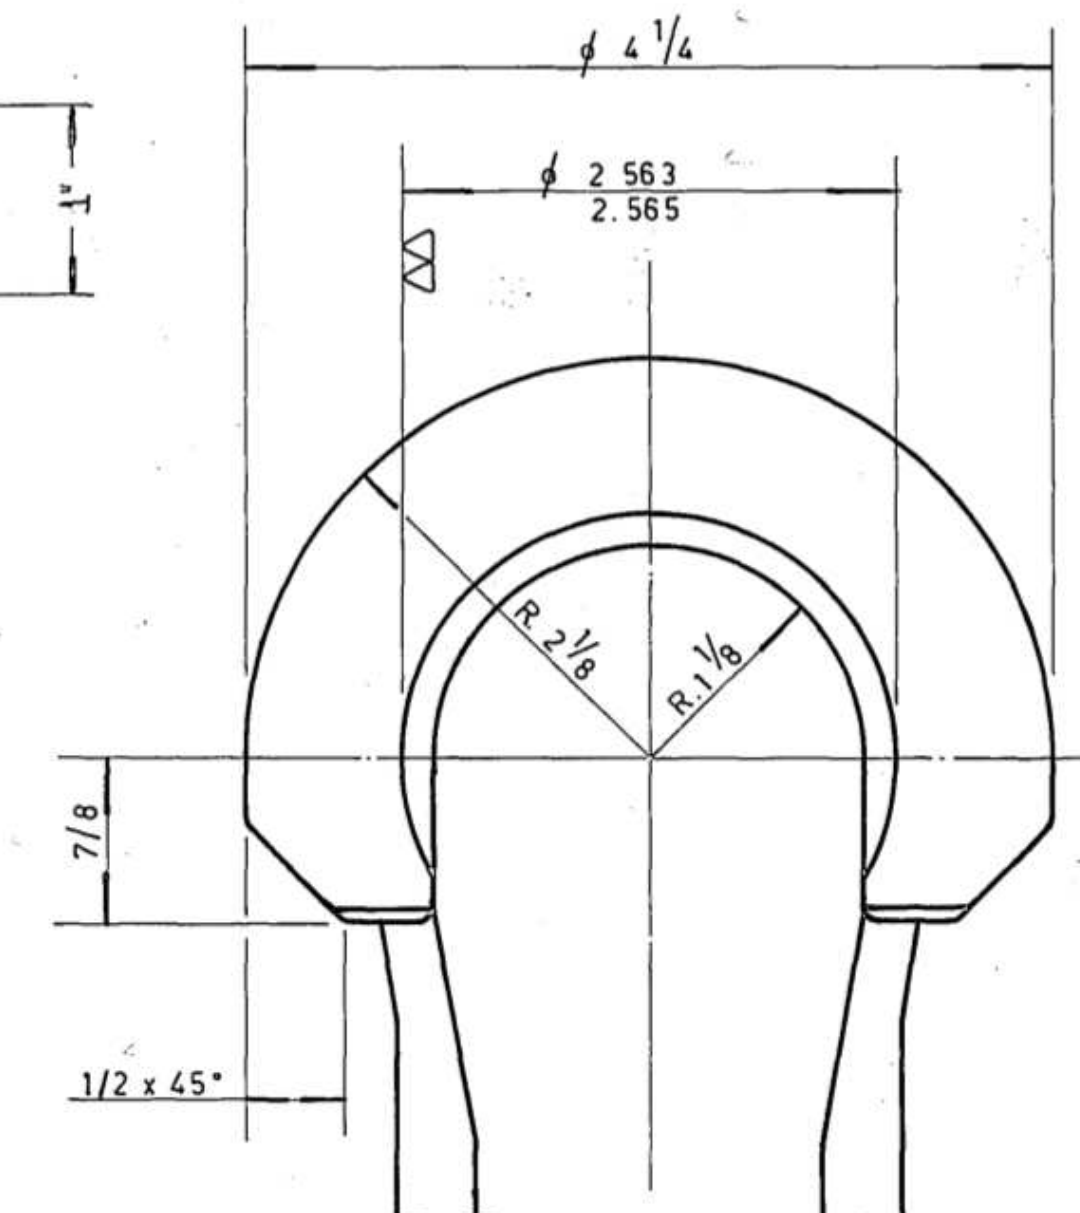


NOTA P/ MODELAÇÃO
NÃO ACRESCENTAR MATERIAL P/ USINAGEM
ESTAS SUPERFÍCIES INTERNAS DEVEM SER
PERFEITAMENTE LISAS DE FUNDIÇÃO.
(P/ ACEITAR SOMENTE POLIMENTO)

523-5213-7/8	X1
523-5213	X
PEÇA Nº	VISTA

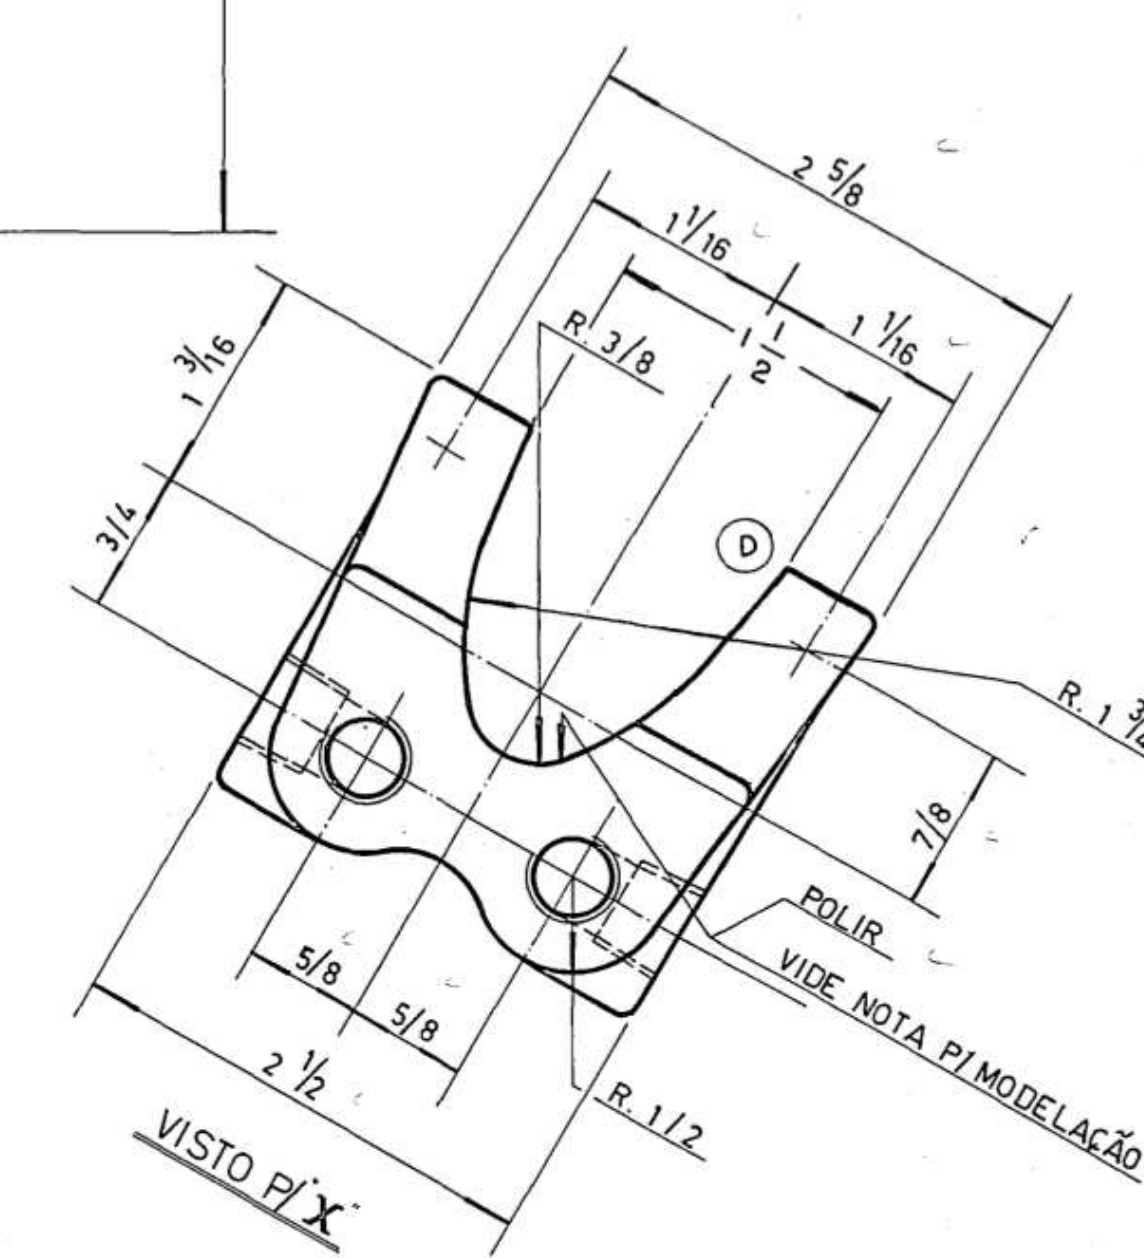

PARA PEÇA Nº 523-5213
USAR ESTA VISTA

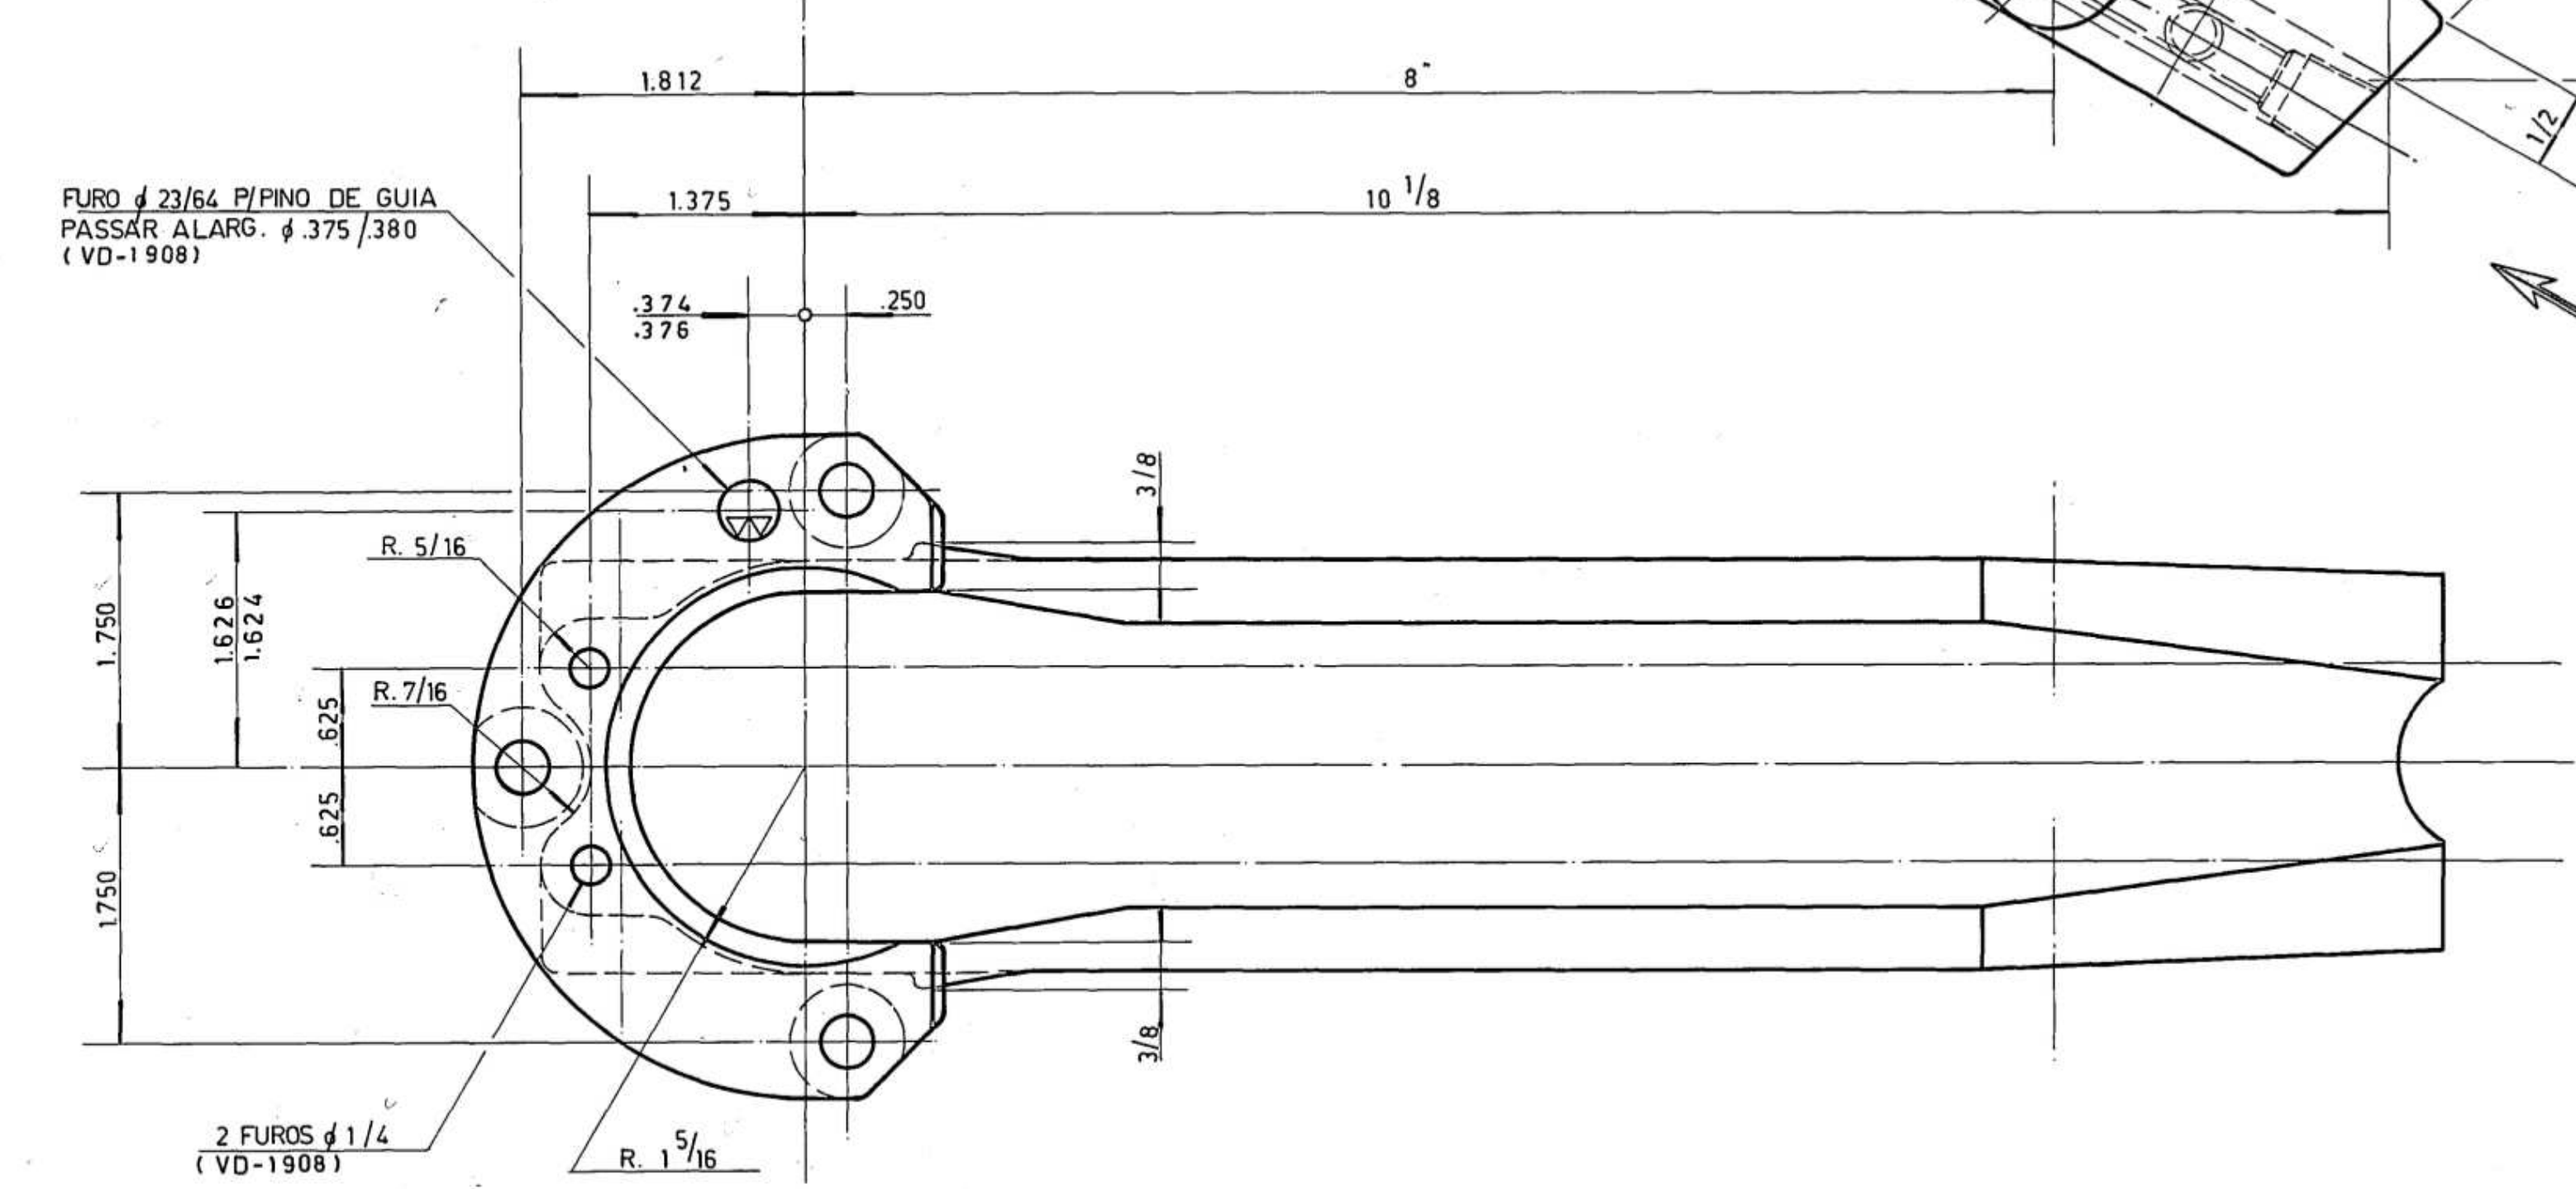

Q	F	E	D	C	B	A	REVISÃO	DATA	29-11-85	VIDROS VITON LTDA.	DES. <i>[Signature]</i>
RODRIGO	RODRIGO	RODRIGO	RODRIGO	RODRIGO	RODRIGO	RODRIGO	RODRIGO	RODRIGO	RODRIGO	ALUMINIO FUNDIDO A-356-T6	AFROV. <i>[Signature]</i>
01/23/85	01/23/85	01/23/85	01/23/85	01/23/85	01/23/85	01/23/85	01/23/85	01/23/85	01/23/85	DELIVERY EQUIPMENT D.G.	Nº DO PROJ. 191-6613
01/23/85	01/23/85	01/23/85	01/23/85	01/23/85	01/23/85	01/23/85	01/23/85	01/23/85	01/23/85	8 SECT. IN LINE I.S. MACH.	Nº DA DES. 191-6613
01/23/85	01/23/85	01/23/85	01/23/85	01/23/85	01/23/85	01/23/85	01/23/85	01/23/85	01/23/85	SCOOP LOWER Nº 0 & 2	Nº DO DES. 191-6613
01/23/85	01/23/85	01/23/85	01/23/85	01/23/85	01/23/85	01/23/85	01/23/85	01/23/85	01/23/85	1:1	Nº DO DES. 191-6613