


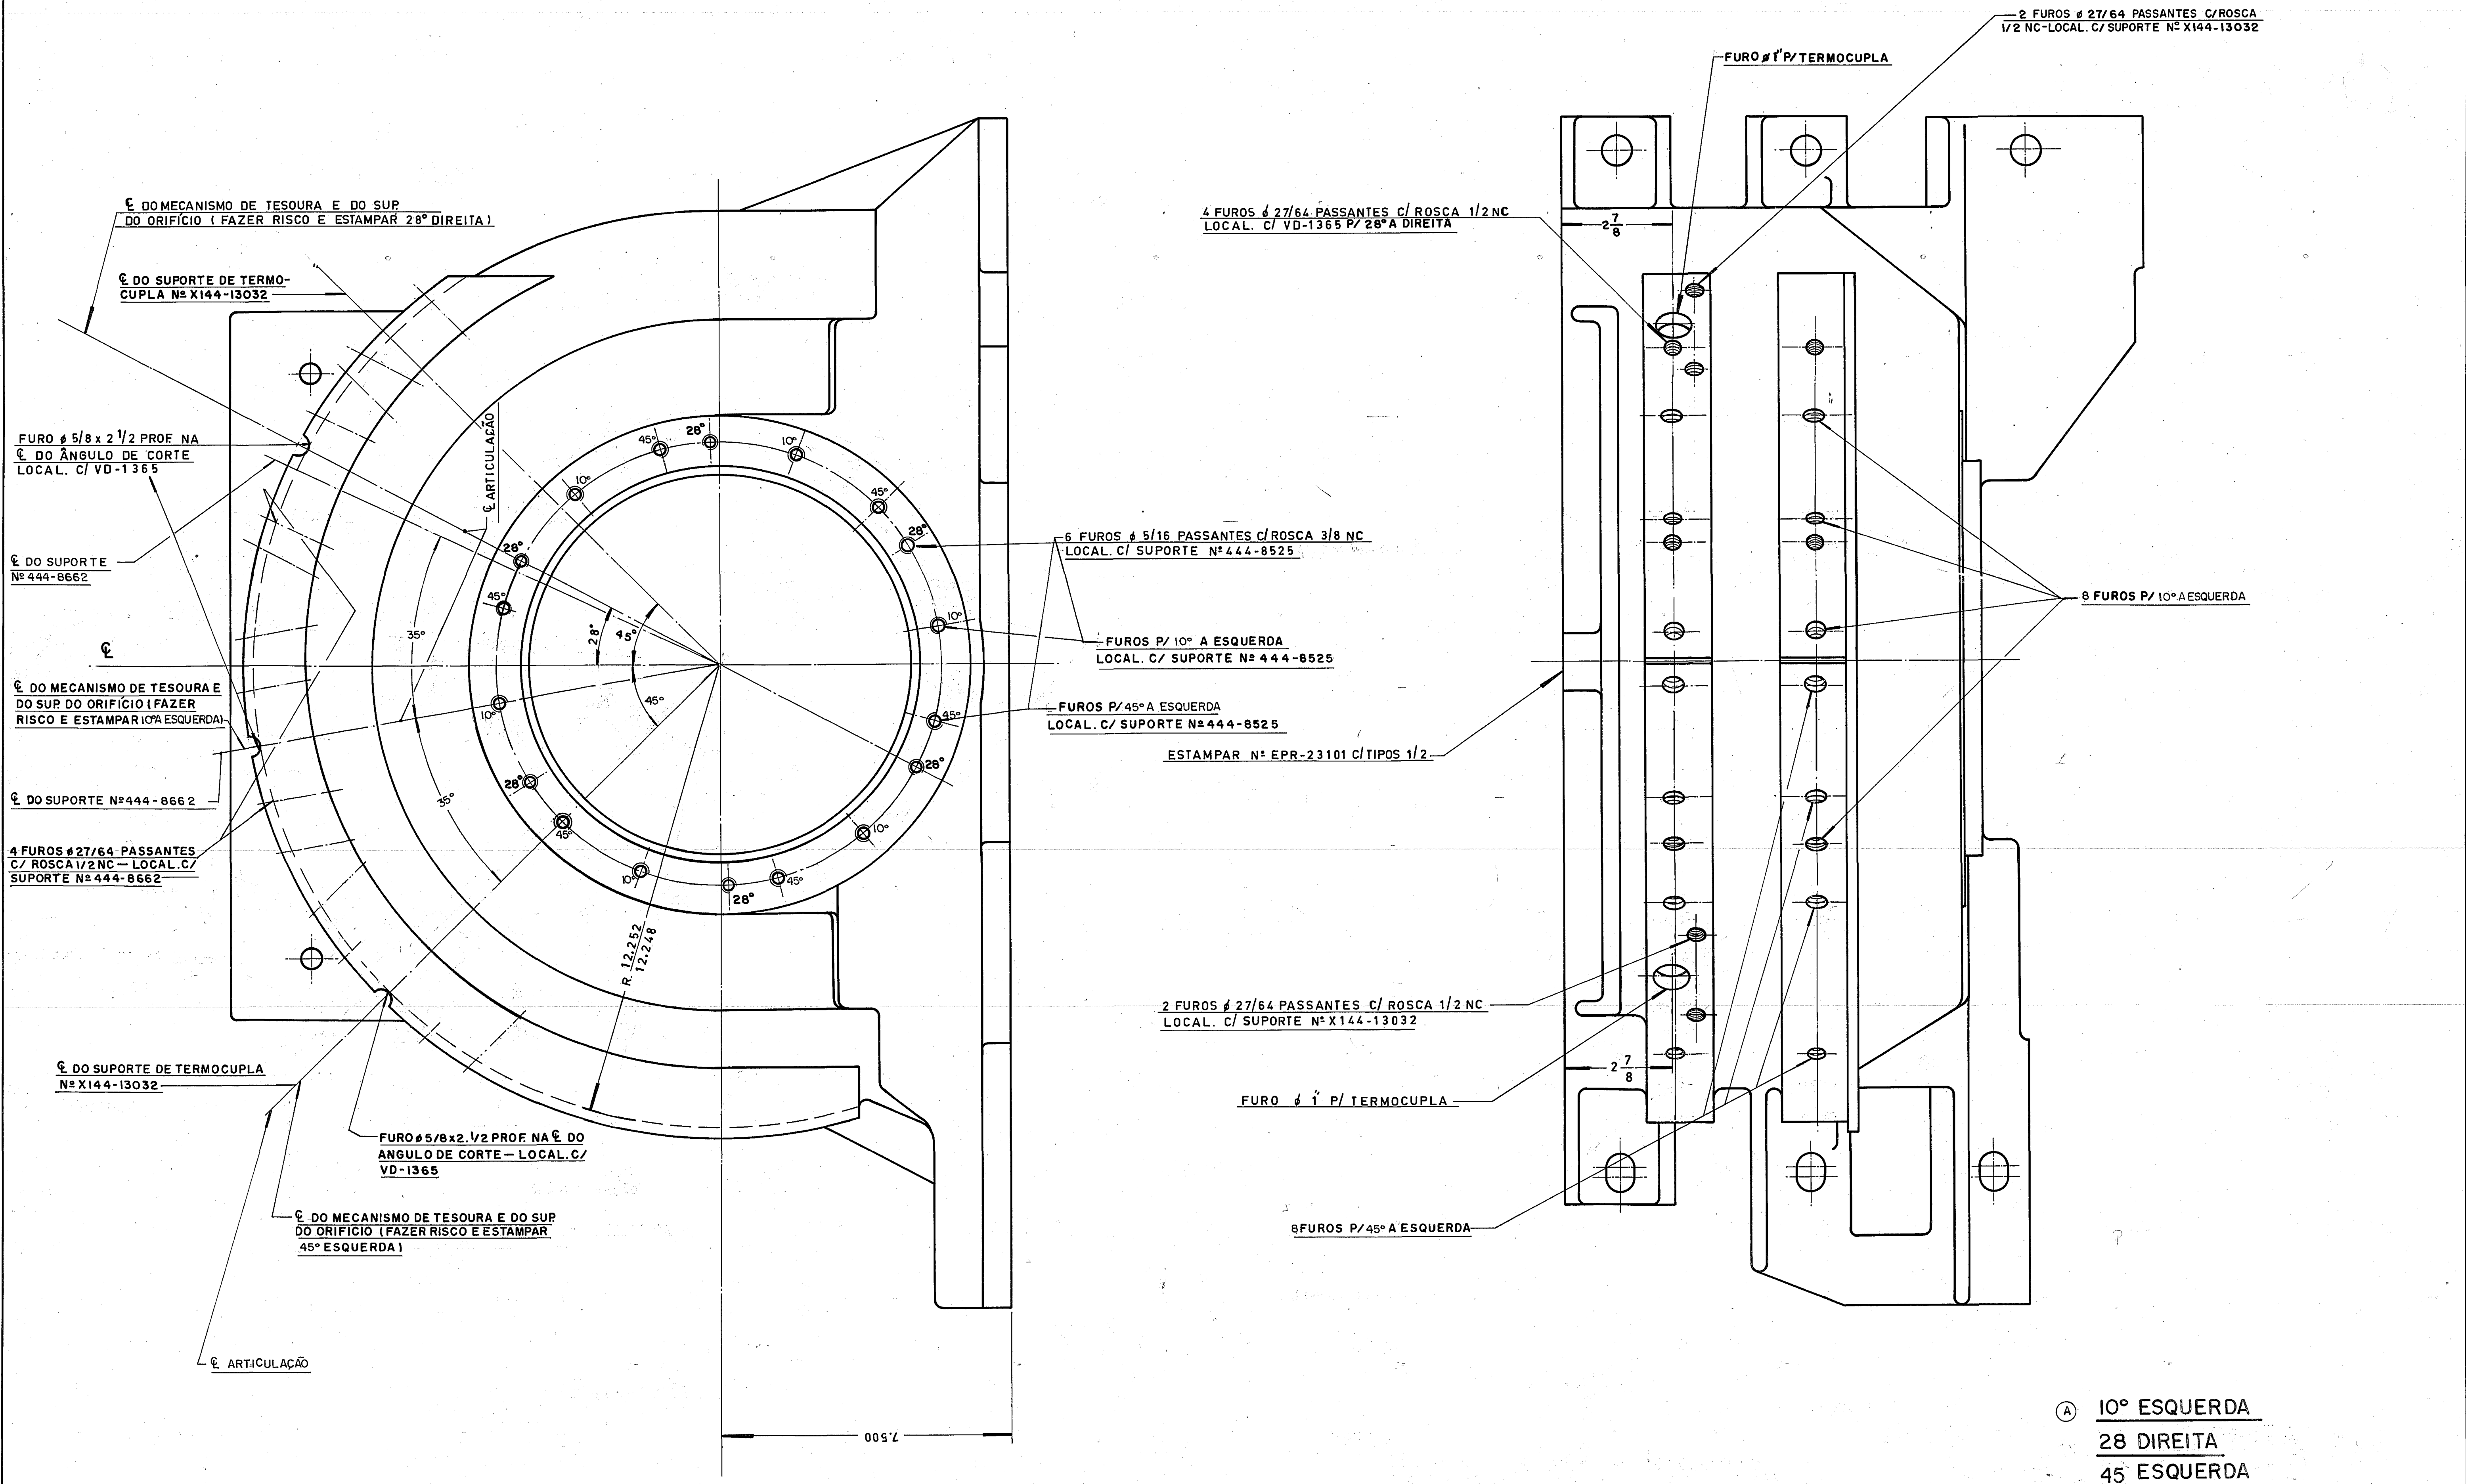

(A) 10° ESQUERDA
28 DIREITA
45 ESQUERDA

REVISÃO	DATA	24-9-87	VIDROS VITON LTDA.		DES.	
	REVISÃO	1	TOLERÂNCIAS STANDARD PARA SUPERFÍCIES USINADAS SEM TOLERÂNCIA INDICADA		VER.	
	DATA	27/10/88	MAT. USAR PEÇA PRONTA Nº 444-8637		APROV.	
	REVISÃO	2	TOLERÂNCIA INDICADA		N.º DO COM.	
DIMENSÃO EN-			DECIMAL ± 0.05"		N.º DO COM.	
			FRAÇÃO		N.º DO COM.	
			DE 0" ATÉ 0" ± 1/64		N.º DO COM.	
			DE 0" ATÉ 24" ± 1/32		N.º DO COM.	
			ACIMA DE 24" ± 1/16		N.º DO COM.	
			TRAT.		N.º DO COM.	
			TERM.		N.º DO COM.	
			ESCALA	1:2	N.º DO COM.	