
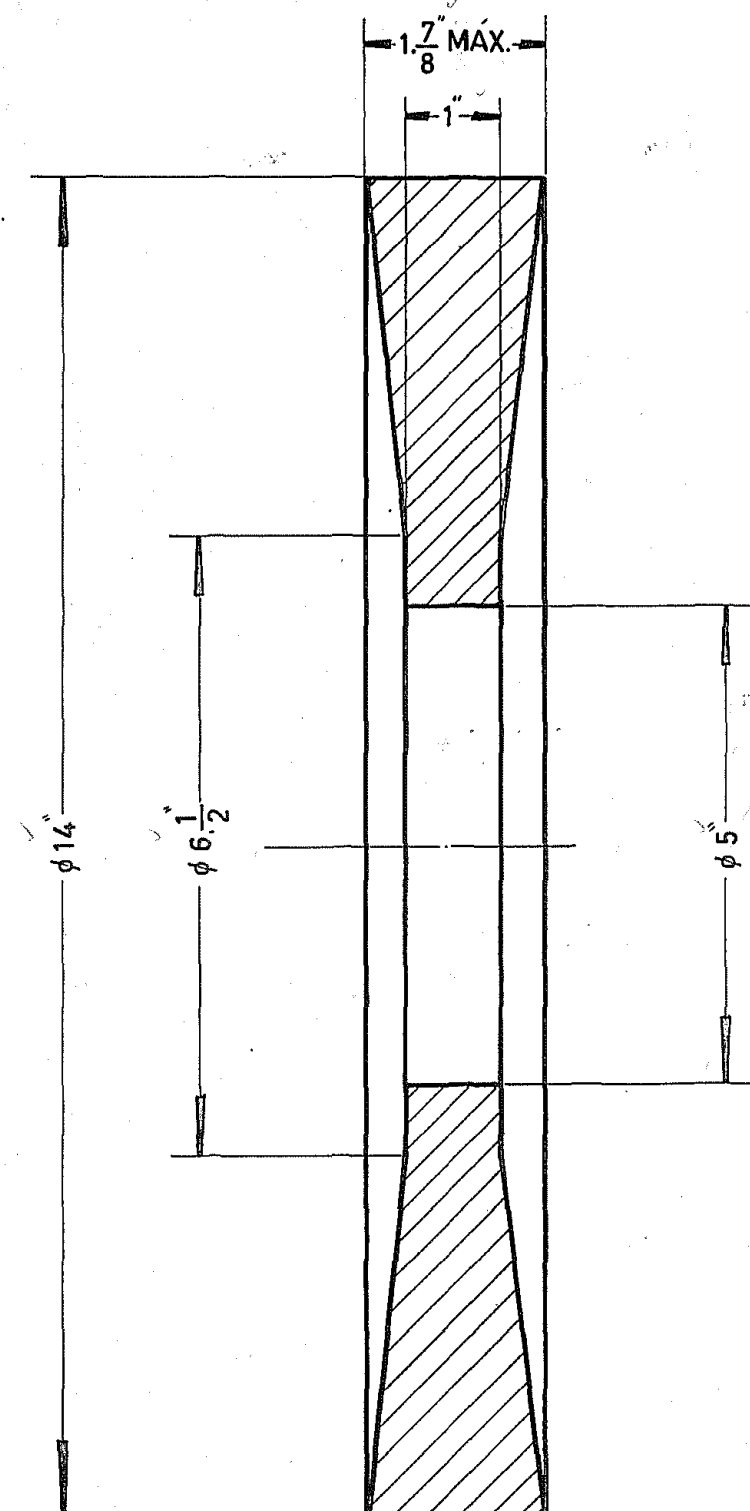


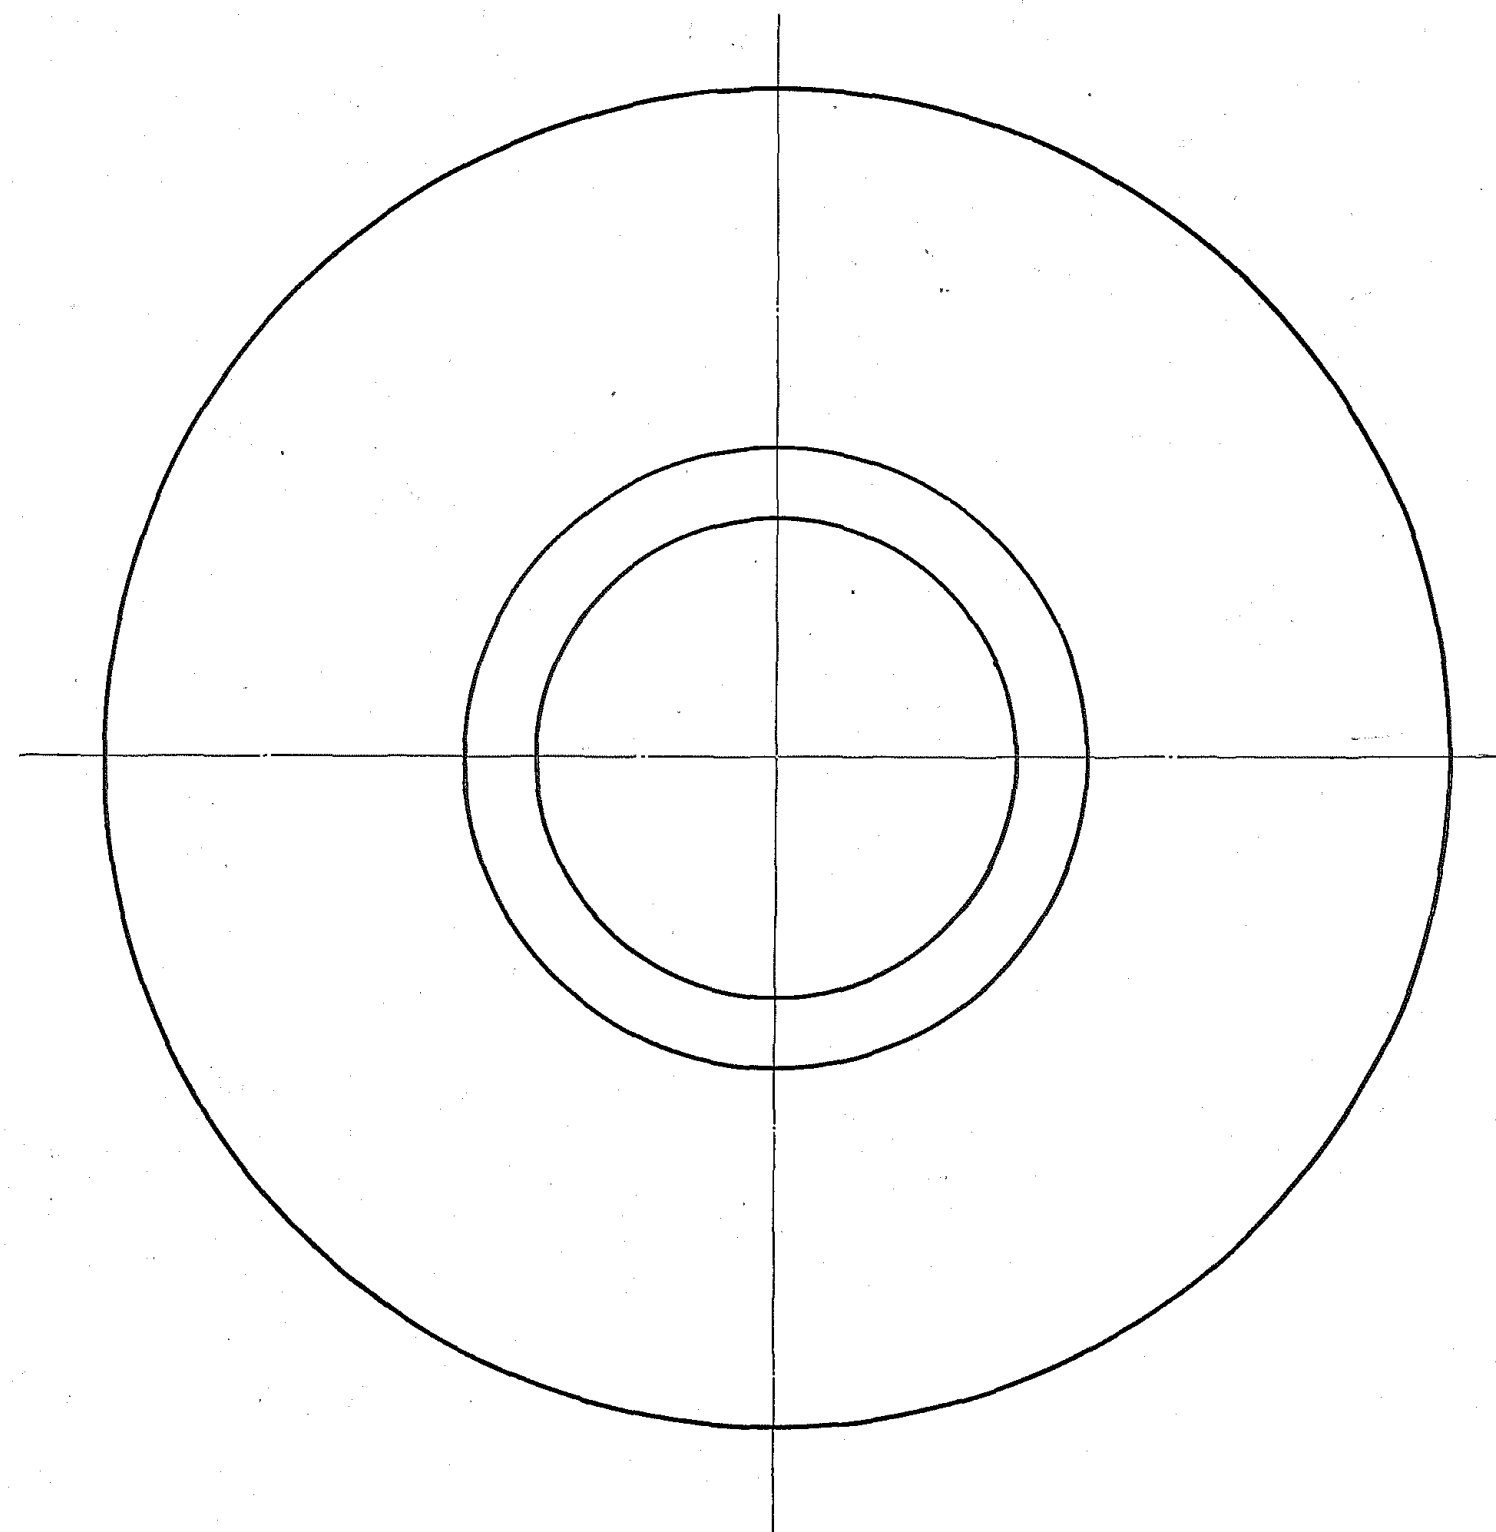

DATA	REVISÃO	ITEM	DATA 8-6-79	DES. <i>Paulo</i>
			TOLEFÂNCIAS STANDARD PARA SUPERFÍCIES USINADAS SEM TOLEFÂNCIA INDICADA	VER. <i>Galvão</i>
			DE: IMAL $\pm 005''$	APROV.
			FRAÇÃO	N.º DO CONJ.
			DE 0" ATÉ 5 $\pm 1/64$	N.º DA PEÇA
			DE 5" ATÉ 24" $\pm 1/32$	VE-1180
			ACIMA DE 24" $\pm 1/16$	N.º DO DES.
			VIDROS VITON LTDA.	
			MAT. GRANA 46 P/MAT. MOLE (AÇO)	
			NOME DO CONJ.	
			NOME DA PEÇA	
			REBÔLO	
			TRAT. TERM.	
			ESCALA 1/2	