


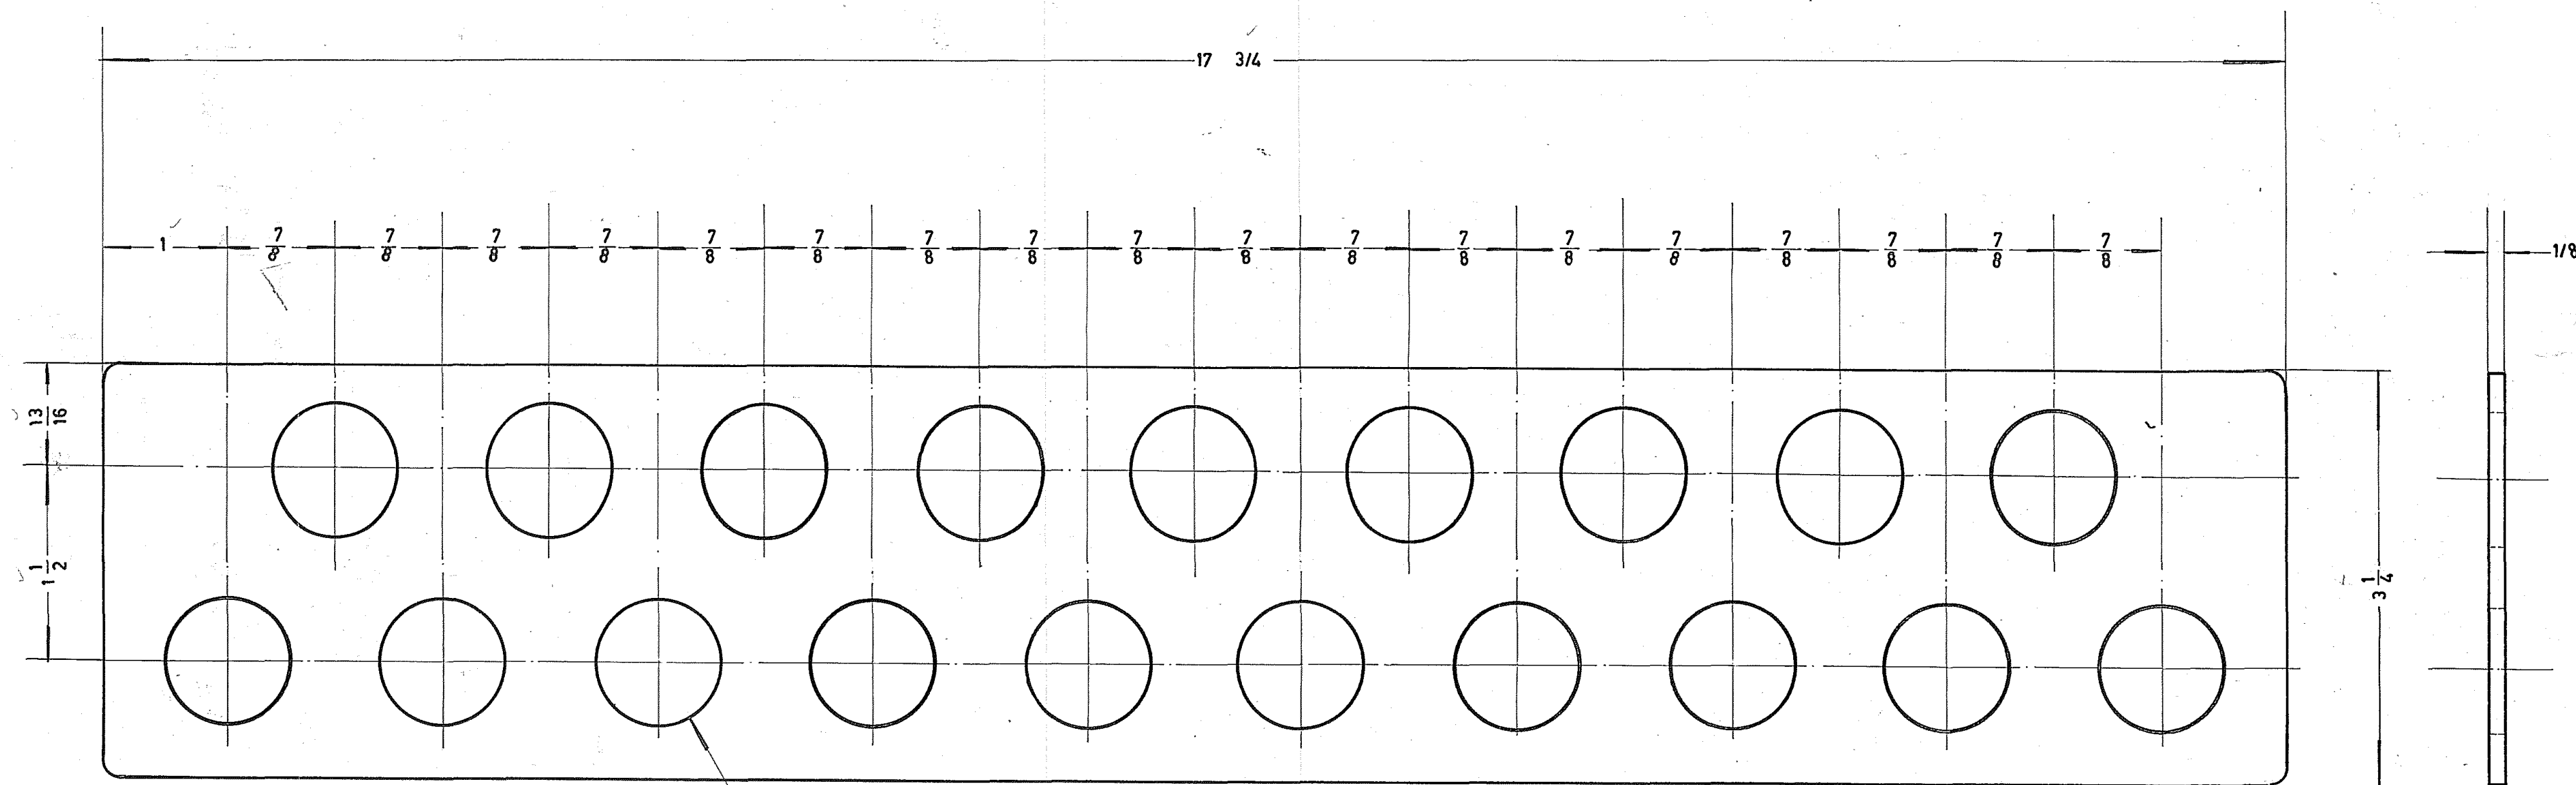

19 Furos Ø 1"

DATA	REVISÃO	Nº	DATA 19/09/79	VIDROS VITON LTDA.		DES. <i>Paulo</i>
			TOLE. ANCIAS STANDARD PARA SUPERFÍCIES USINADAS SEM TOLE. ANCIA INDICADA		VER. <i>Galvão</i>	
			MAT. CHAPA AÇO SAE 1020 - 1/8 ESP.		APROV.	
			NOME DO CONJ.		N.º DO CONJ.	
			NOME CHAPELONA P/ CONTROLAR A DA PEÇA FURAÇÃO DA PC 191-4101		N.º DA PEÇA VE-1195	
			TRAT.		N.º DO DES.	
			TERM.			