


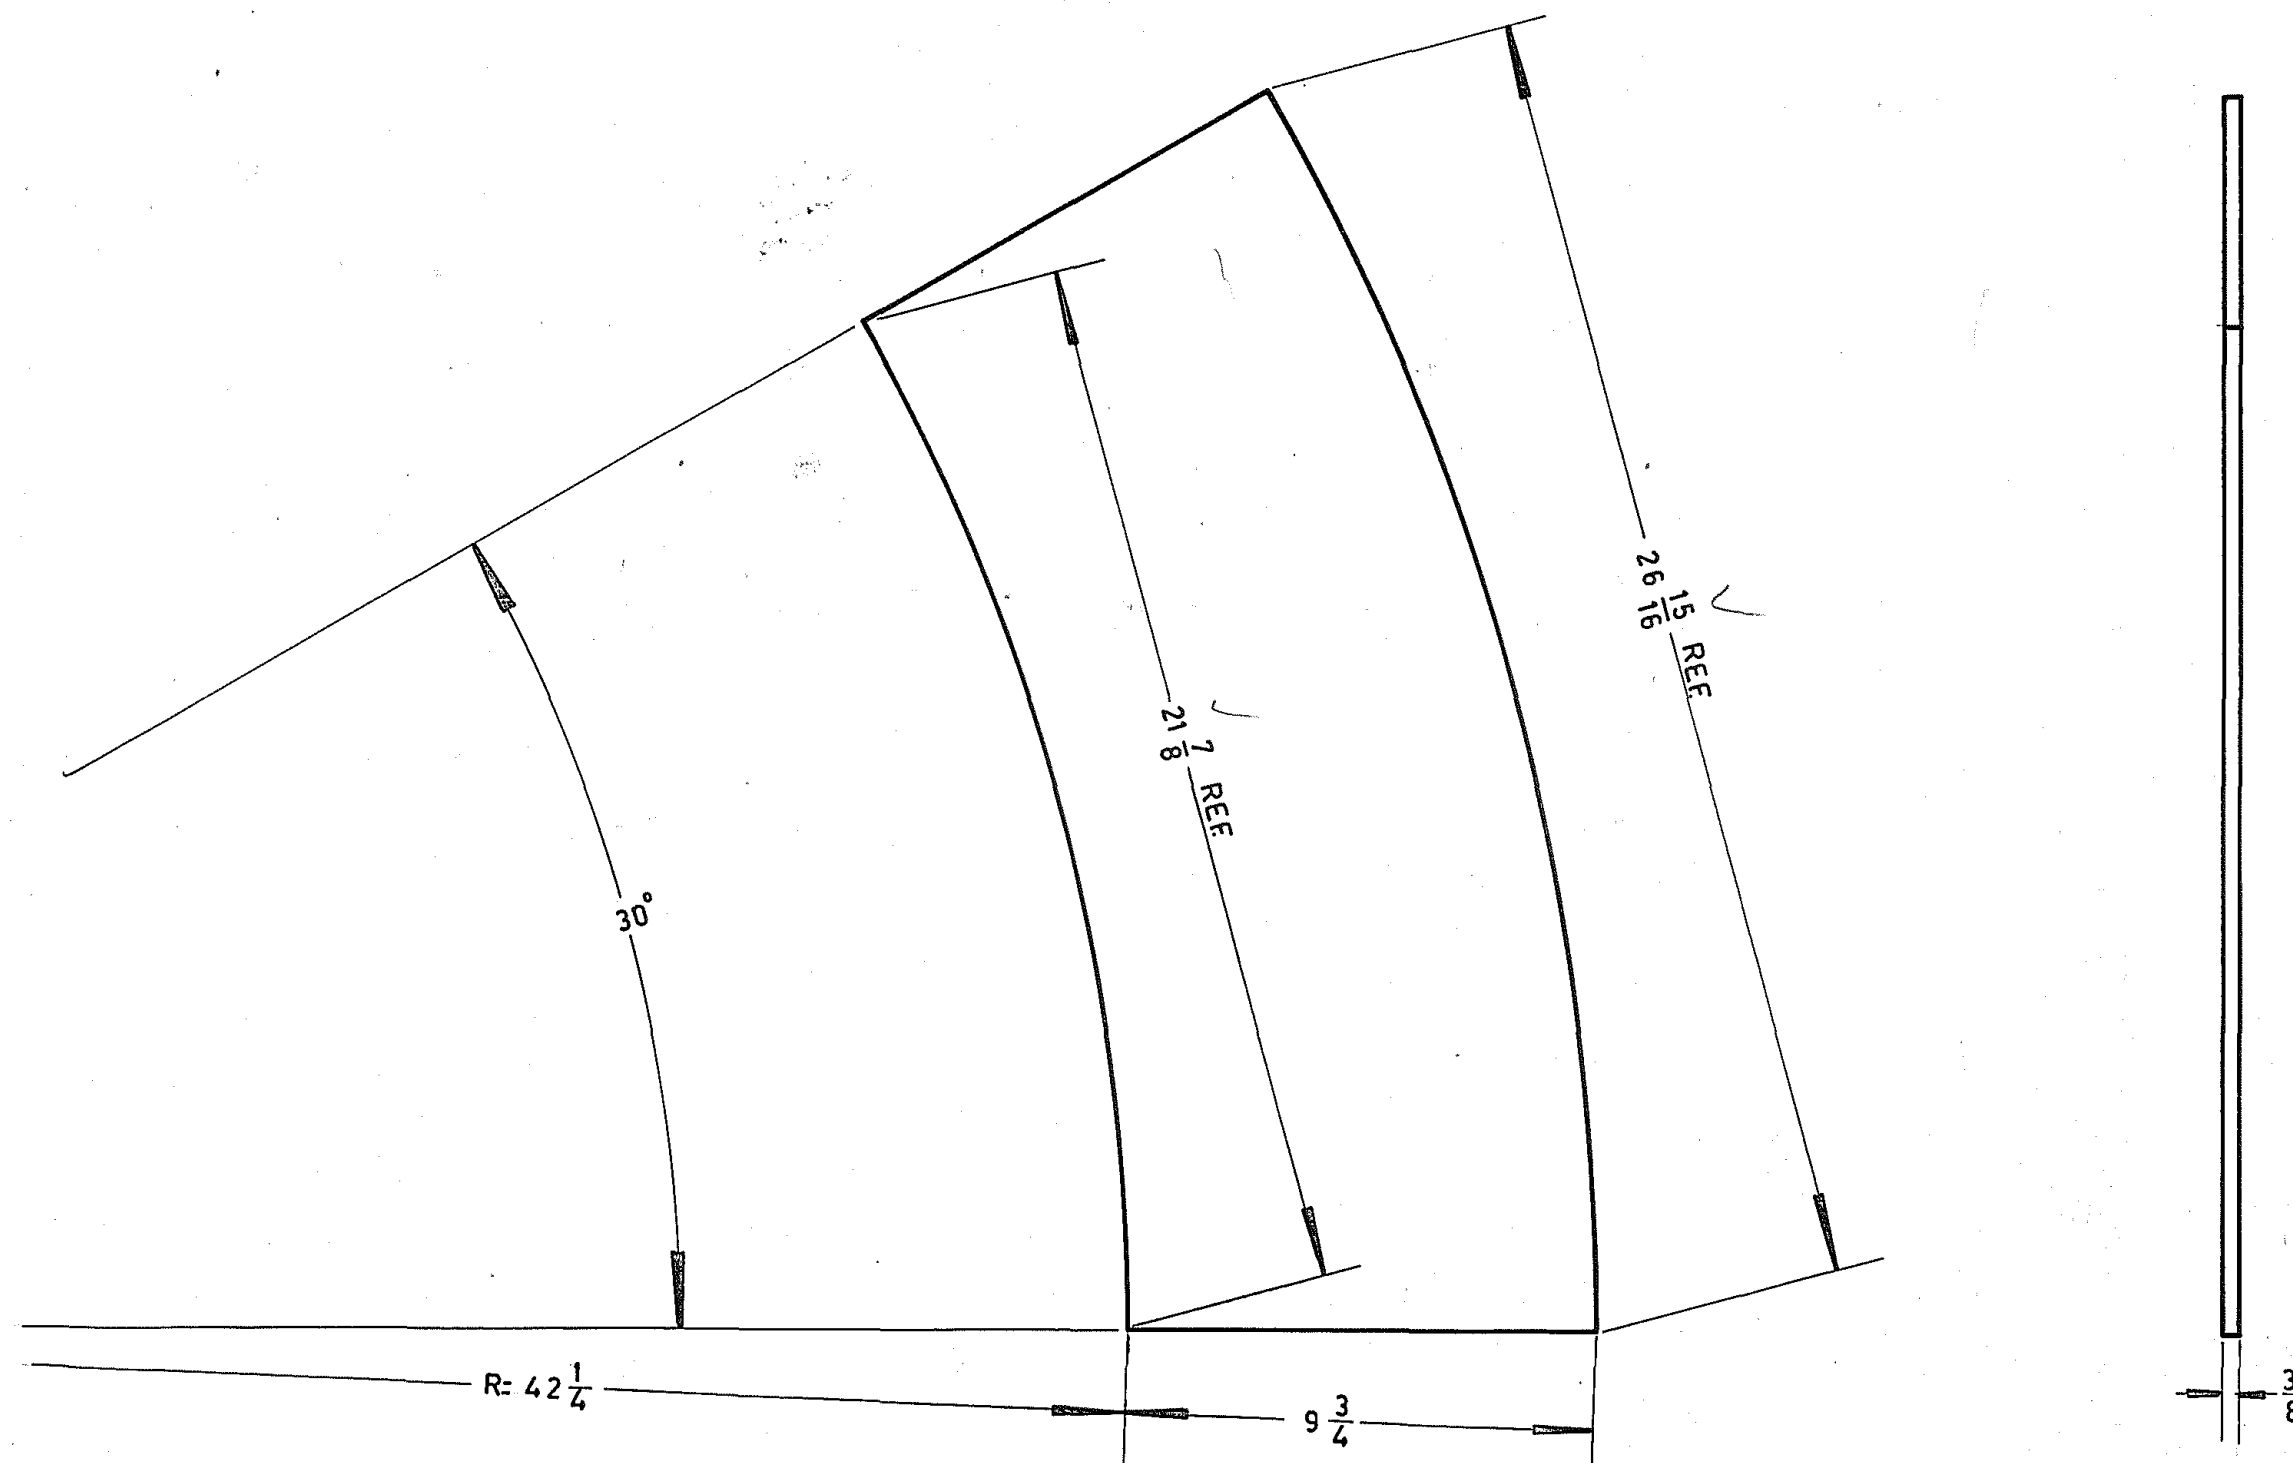

20-08-82		VIDROS VITON LTDA.	
TOLERÂNCIAS STANDARD PARA SUPERFÍCIES USINADAS SEM INDICAÇÃO INDICADA		CHAPA DE AÇO SAE 1020	
DE 0" A 1" ± 0.05"		ESTEIRA CURVA	
DE 1" A 2" ± 0.005"		DETALHE P/CORTAR A MAÇARI- CO AUTOMÁTICO PEÇAVME253-2	
DE 2" A 5" ± 0.005"		VME-253	
DE 5" A 24" ± 1/32		VE-1425	
ACIMA DE 24" ± 1/16		1/4	