


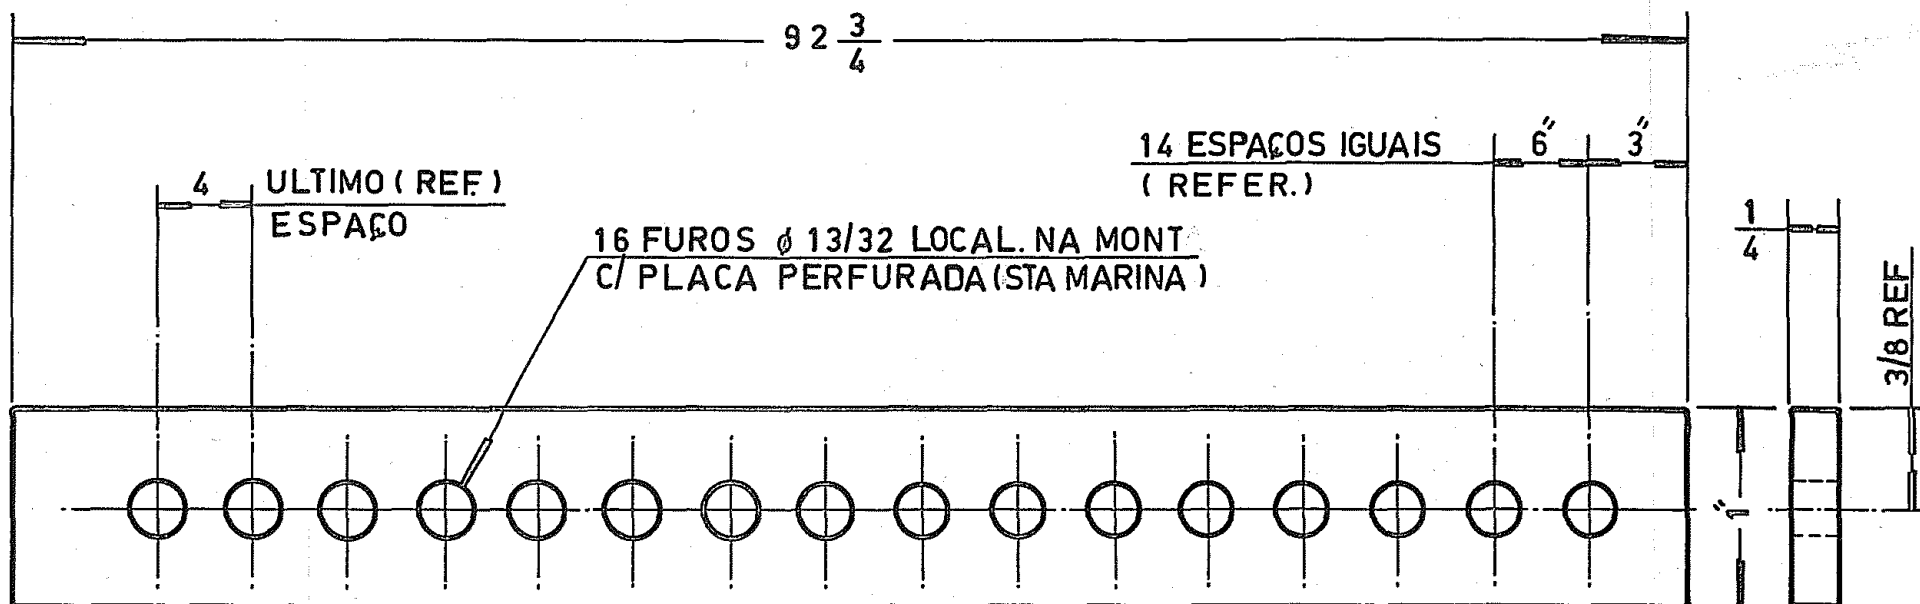

DATA: 26-01-89		VIDROS VITON LTDA.		DES. <i>Adilson</i>
TOLERÂNCIAS STANDARD PARA SUPERFÍCIES USINADAS SEM TOLERÂNCIA INDICADA		MAT.		<i>Adilson</i>
DECIMAL $\pm 0.05''$		NOME DO CONJ. EXT. DA EST. X117 MAQ. I.S. 8 SEC.(STA MARINA)		N.º DO CONJ.
FRAÇÃO		NOME DA PEÇA CALÇO P/ PLACA PERF DA EST. DA MAQ. STA MARINA		N.º DA PEÇA VE-1955
DE 0'' ATÉ 5'' $\pm 1/64$		TRAT. TERM.		ESCALA S/E
DE 5'' ATÉ 24'' $\pm 1/32$				
ACIMA DE 24'' $\pm 1/16$				N.º DO DES.