


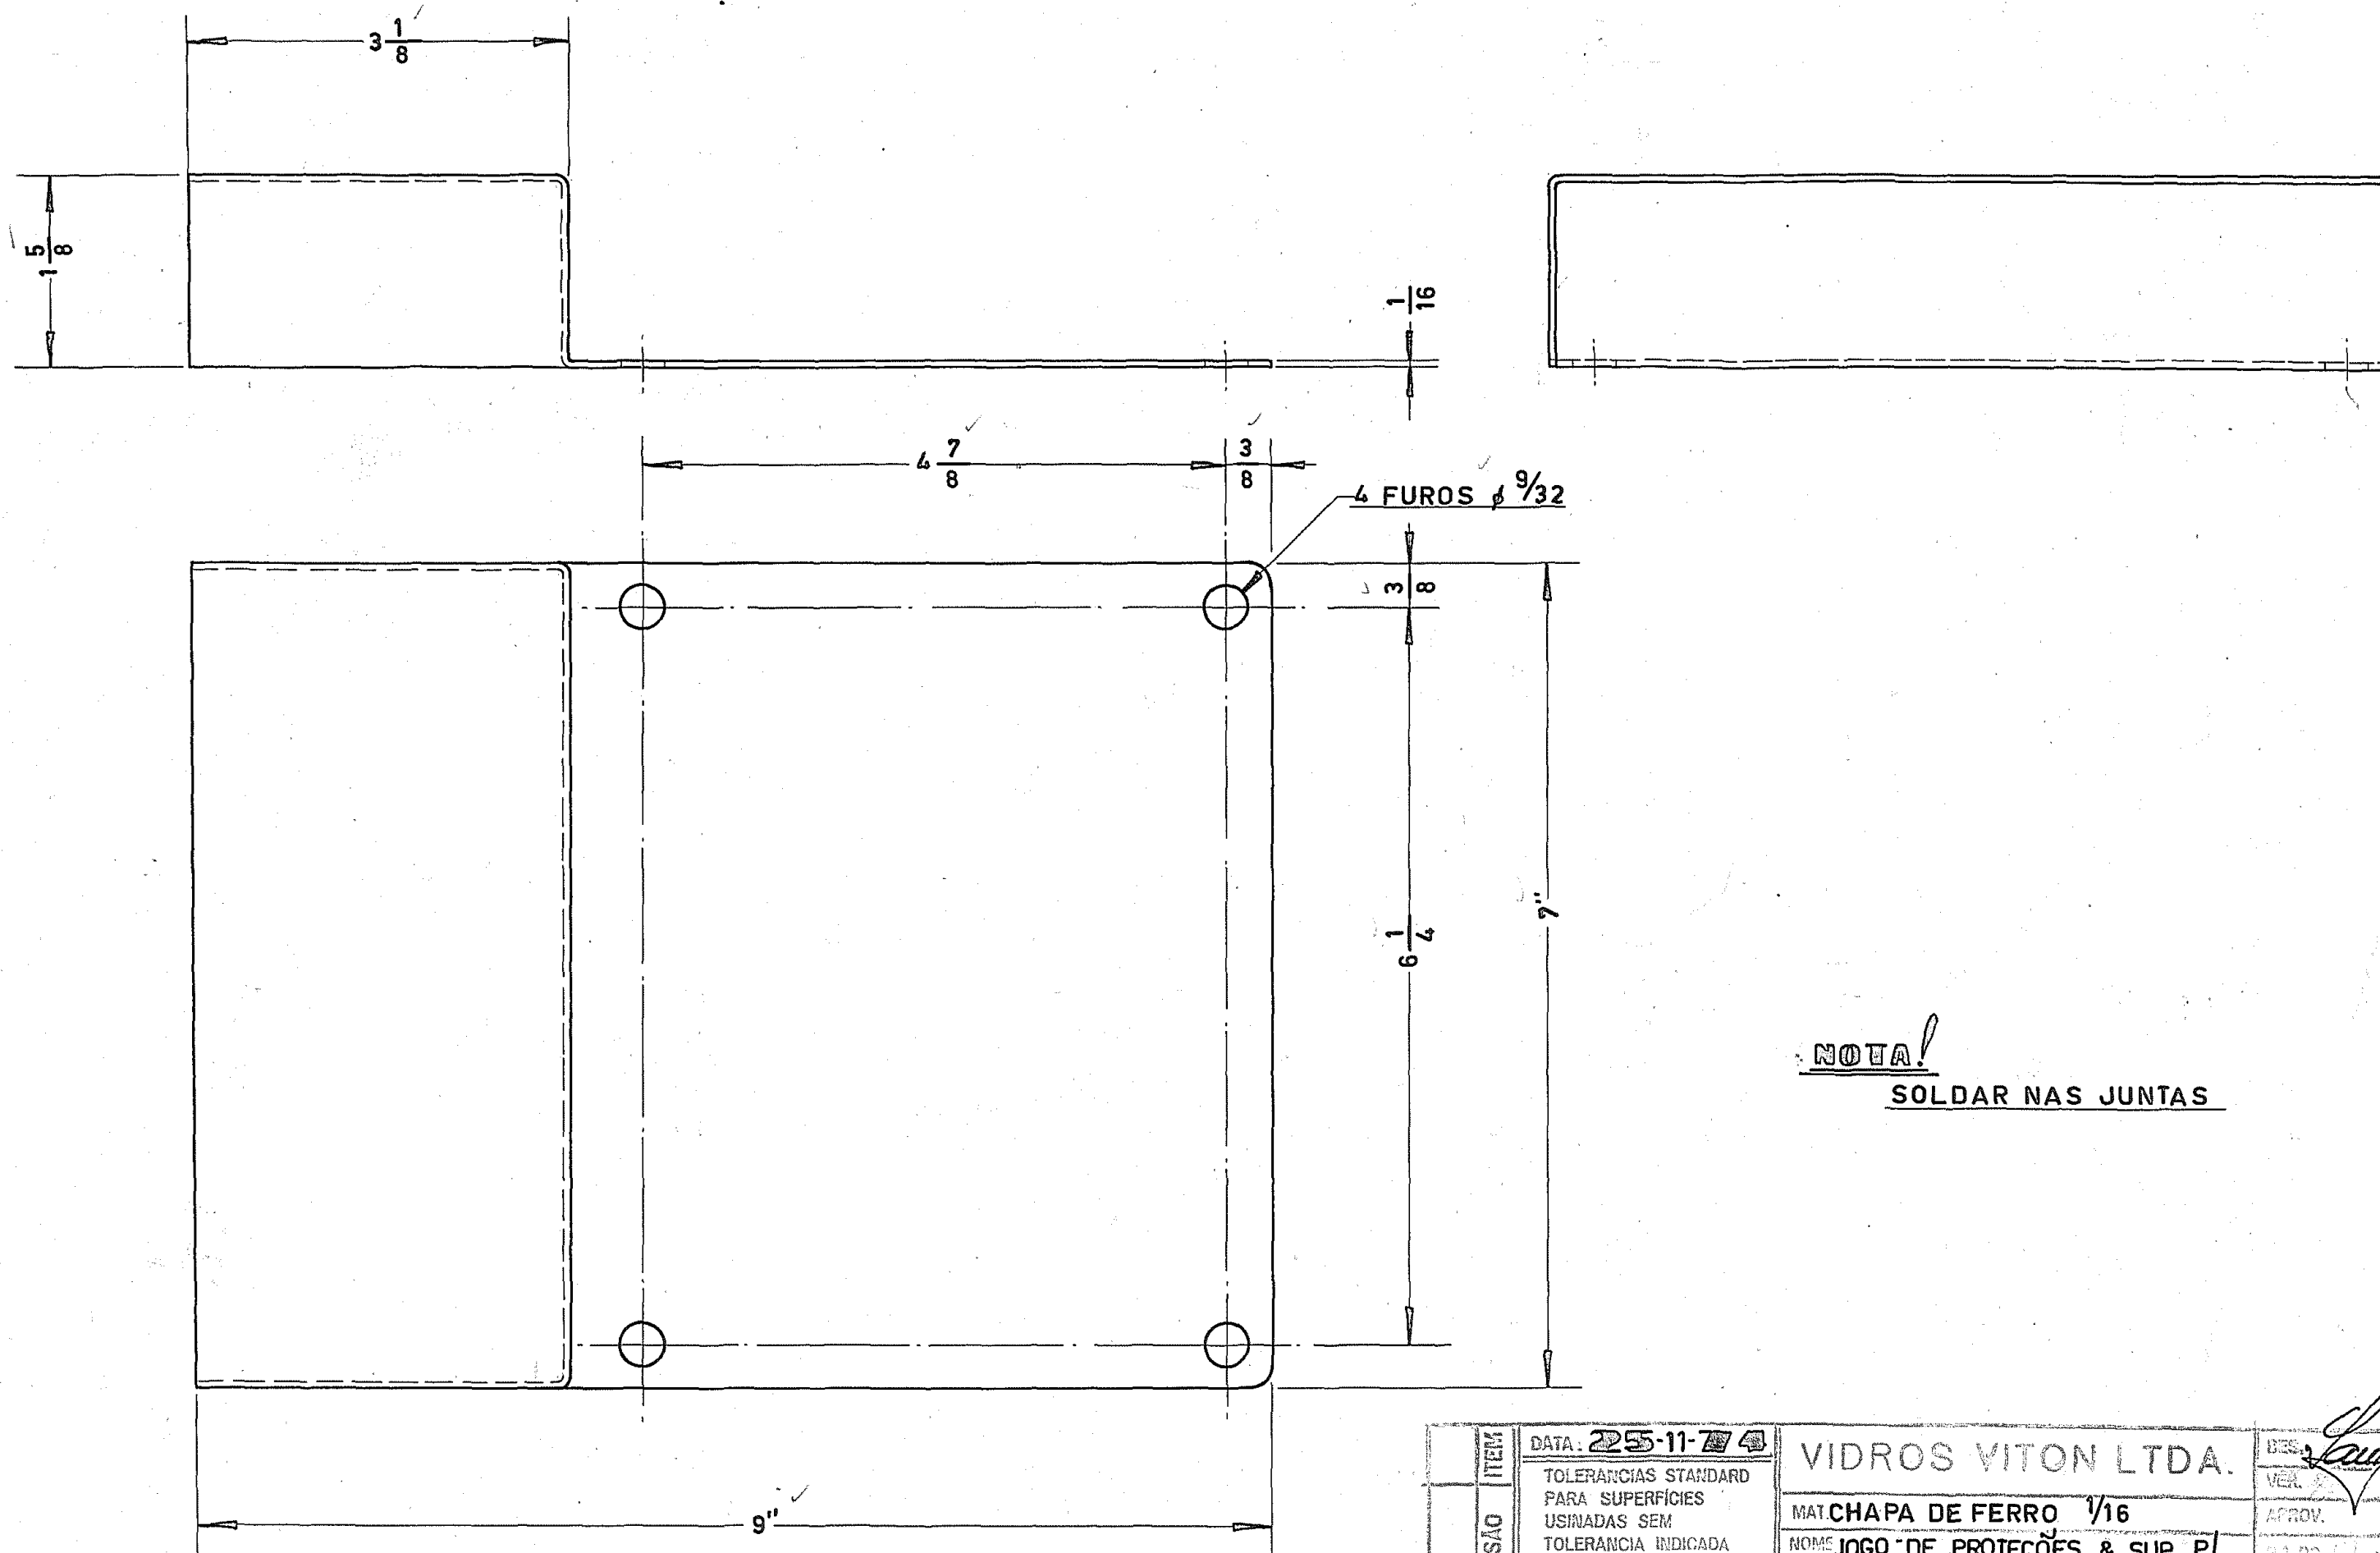

DATA: 25-11-74	VIDROS VITON LTDA.	DES. <i>[Signature]</i>
TOLERANCIAS STANDARD PARA SUPERFÍCIES USINADAS SEM TOLERANCIA INDICADA	MAT. CHAPA DE FERRO 1/16	VER. <i>[Signature]</i>
DECIMAL $\pm$ 005"	NOME DO PROJ. JOGO DE PROTEÇÕES & SUP. P/ LUBRIF. AUTOM. DA MAQ. I.S.	APROV. <i>[Signature]</i>
FRAÇÃO	NOME DA PEÇA PROTEÇÃO	N.º DA PEÇA VV-105
DE 0" ATÉ 5" $\pm$ 1/64	TRAT. TERM.	N.º DO DES. VE-714
DE 5" ATÉ 24" $\pm$ 1/32	ESCALA 3/4	
ACIMA DE 24" $\pm$ 1/16		