


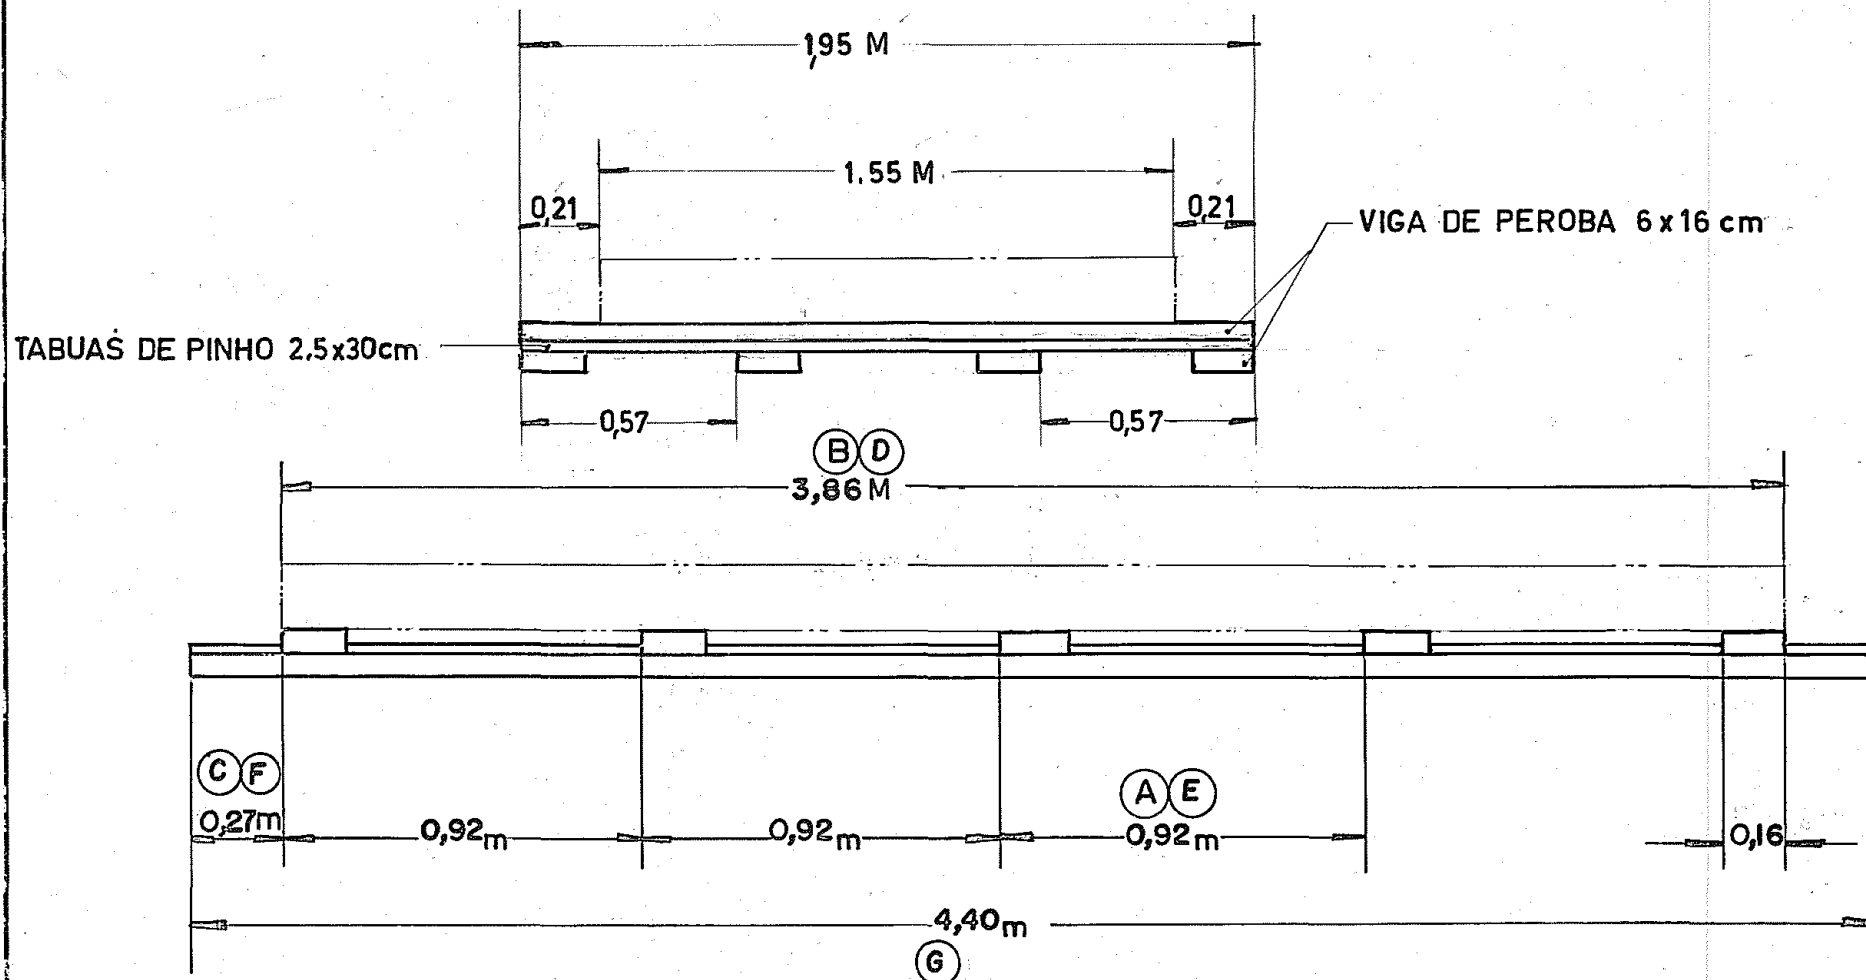

	G	F	E	C	C	B	A
	ERA: 4,50M	ERA: 0,30M	ERA: 0,84M	ERA: 3,90M	ERA: 0,25m	ERA: 4,00m	ERA: 0,96m
Adilson	22.4.91	Adilson	22.4.91	Adilson	22.4.91	2.2.88	2.2.88
DATA	REVISÃO						

DATA 14-10-75

TOLERANCIAS STANDARD
PARA SUPERFICIES
USINADAS SEM
TOLERANCIA INDICADA

DECIMAL $\pm 0.05"$

FRAÇÃO

DE 0" ATÉ 5" $\pm 1/64$

DE 5" ATÉ 24" $\pm 1/32$

ACIMA DE 24" $\pm 1/16$

EMPENSAO EM:

VIDROS VITON LTDA.

MAI VIDE A NOTAÇÕES

NOME
DO
CORR.

NOME
DA
PEÇA

TRAT.
TÉCNICA

BASE DE MAD. P/MAQ. I-S (6 SEQ.)

ESCALA
1:20

DES. Carlos A. Demetrio

VEN.

APROV.

N.º DO

CONJ.

N.º DA

PEÇA

N.º DO
DES.

VE-811