
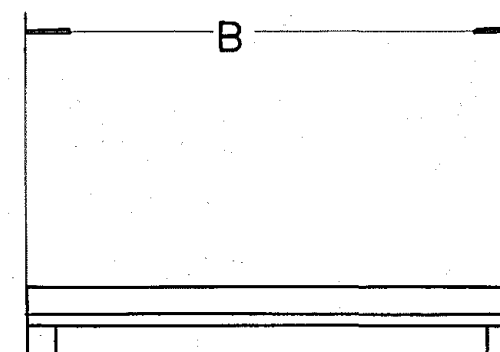


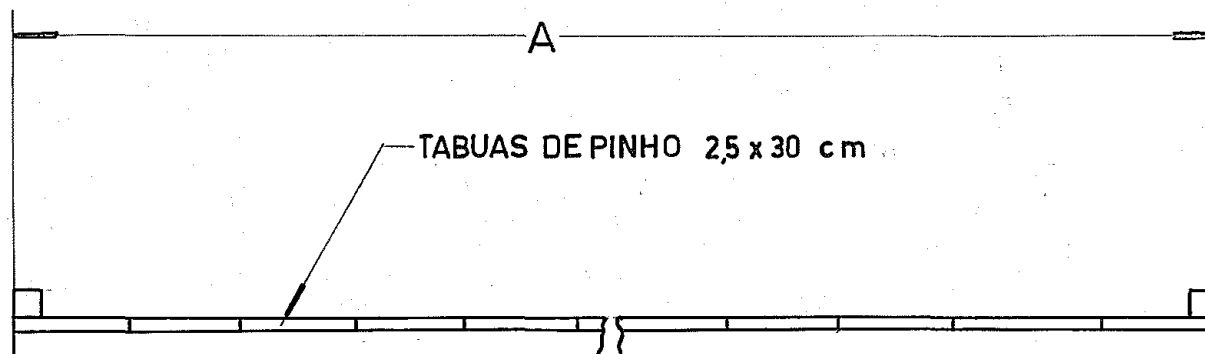

TABUAS DE PINHO 2,5 x 30 cm

CAIBRO DE PINHO 7,5 x 75 cm

MADEIRA NECESSÁRIA P/ COMPLETAR 1 CAIXA

CAIBRO PINHO 3" x 3" = 100 m²

TABUAS PINHO 1" x 12" = 110 m²

RIPAS PINHO 1/2" x 2" = 50 m²

PAPELÃO PIXADO DE 1 m LARG. 15 m

VIGA	A	B
STANDARD	4,25 m	1,40 m
ESPECIAL 4 ³ /8 C.C.	4,25 m	1,75 m (A)

5.6.91	ERA: 1,95	A	DATA 14-10-75	VIDROS VITON LTDA.	DES. <i>Carlo A. Damasceno</i>
			TOLEPANCILLO STANDARD PARA SUPERFICIES USINADAS SEM TOLERANCIA INDICADA	MAT VIDE ANOTAÇÕES	VER. <i>Tabellera</i>
			DECIMAL ± 005"	NOME DO CONJ.	APR. <i>...</i>
			FRAÇÃO DE 0" ATÉ 5" ± 1/64 DE 5" ATÉ 24" ± 1/32 ACIMA DE 24" ± 1/16	BASE DE MADEIRA P/ ENCAIXOTAR AS VIGAS DOS SCOOPS (6 SEC)	1.º DO CONJ.
			ESCALA 1:20	2.º DA FICHA	VE-813