


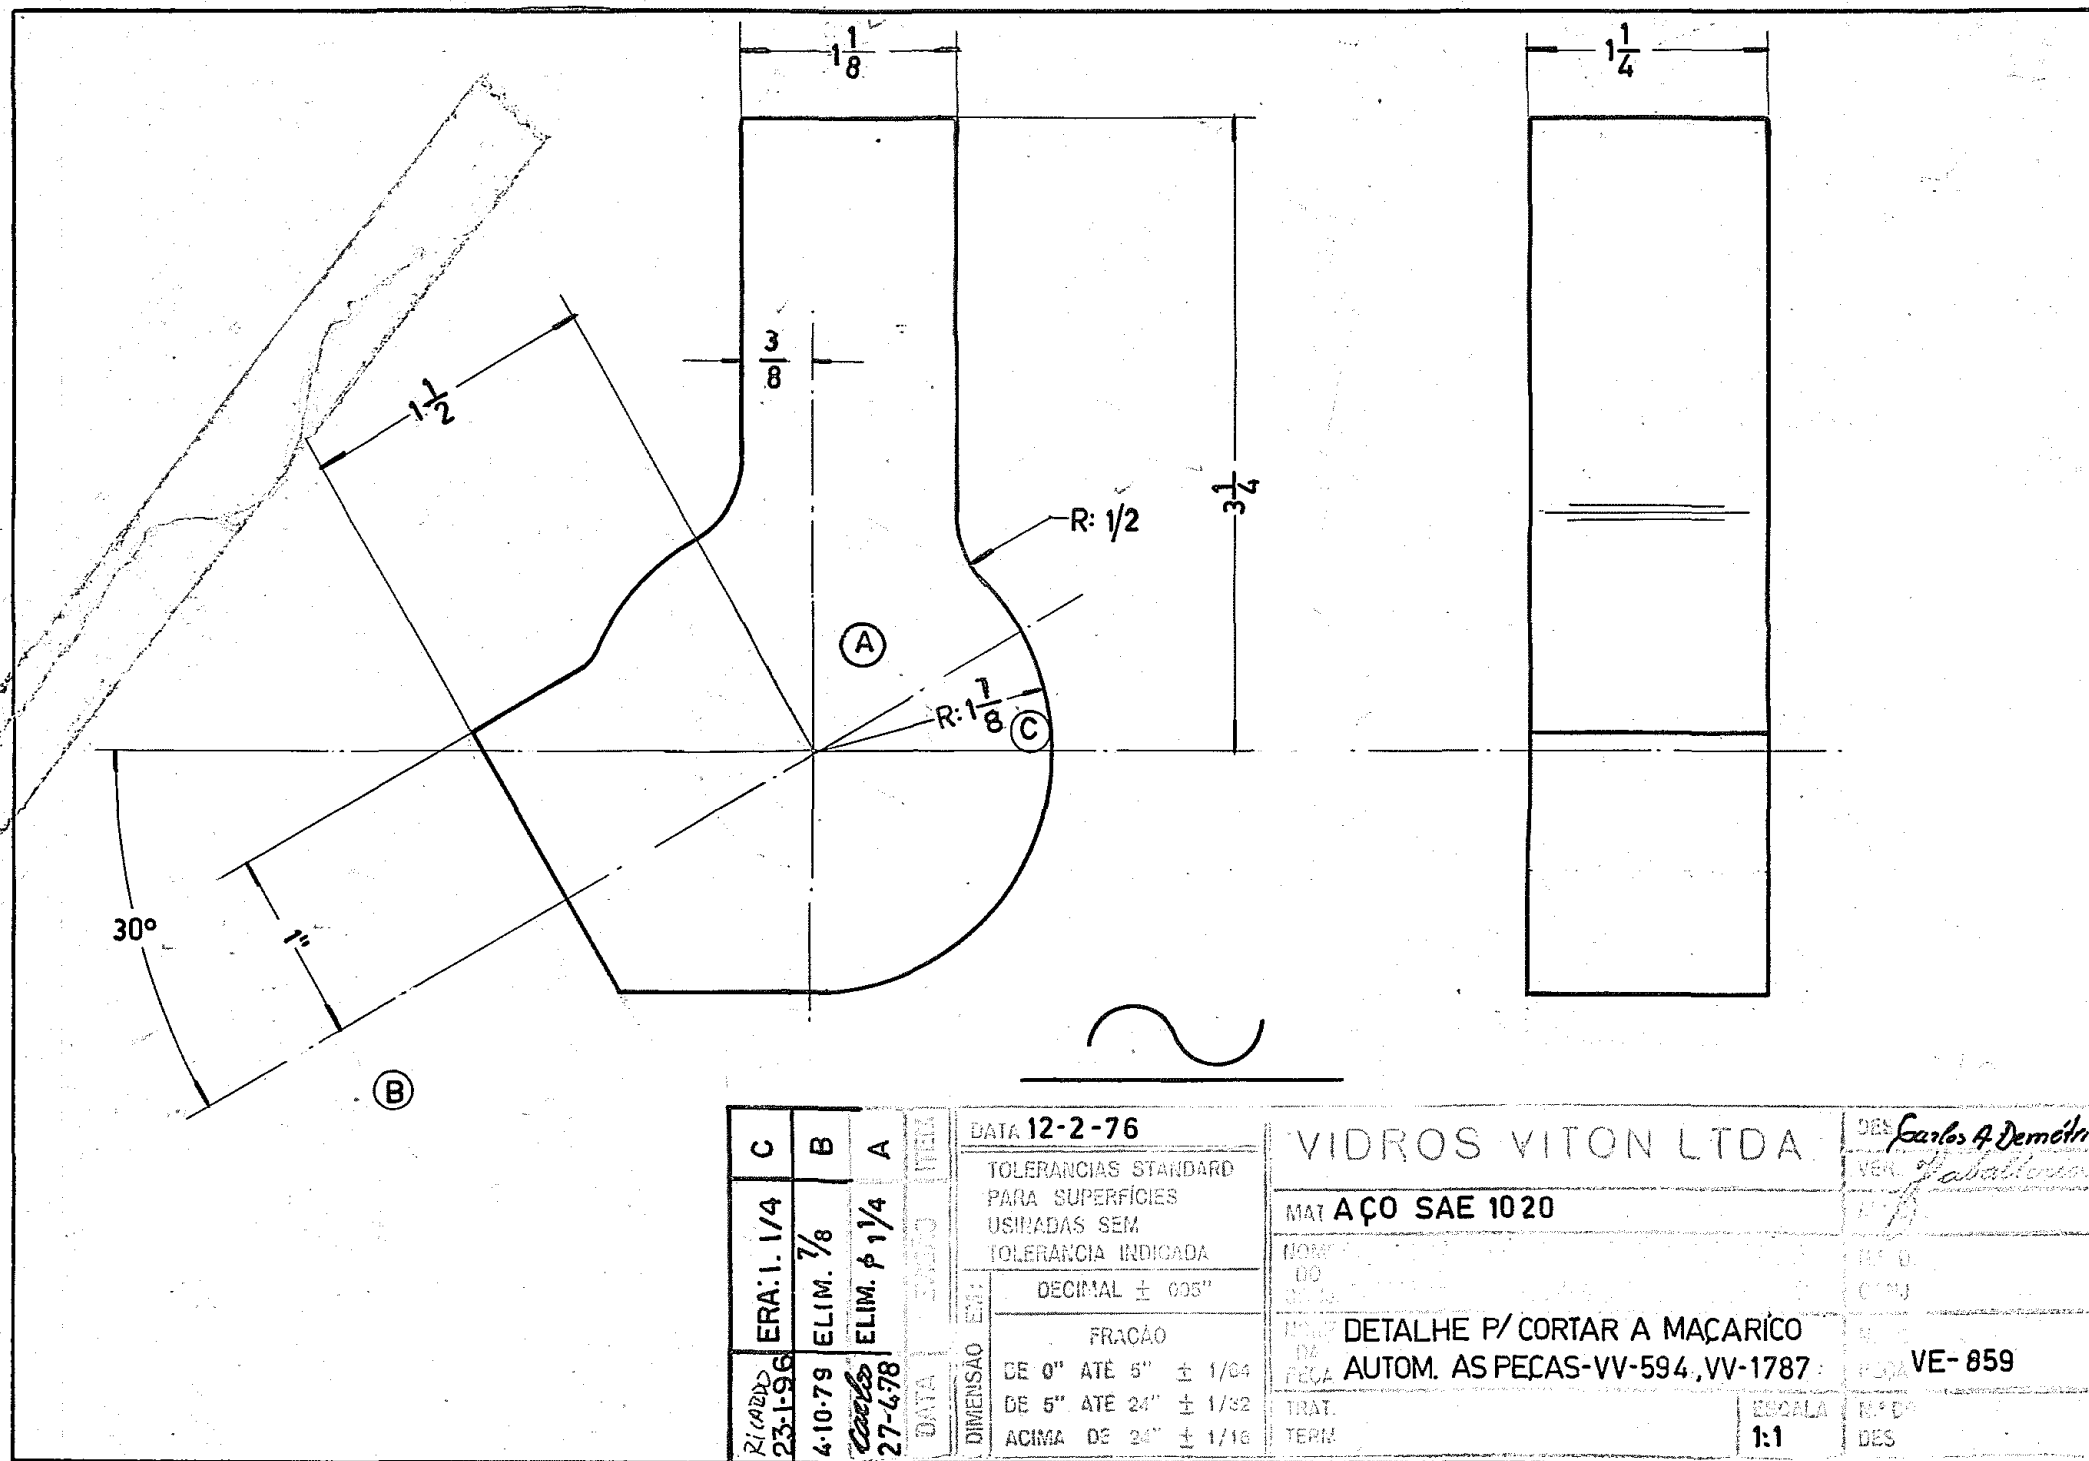

RIZADO	ERA	ELIM.	ELIM.	DATA	DE
23-1-96	1. 1/4	7/8	1 1/4	12-2-76	VE
4-10-79					
27-4-78					

DATA	12-2-76
TOLERANCIAS STANDARD PARA SUPERFÍCIES USINADAS SEM TOLERANCIA INDICADA	
DECIMAL	± 0.05"
FRAÇÃO	
DE 0" ATÉ 5"	± 1/64
DE 5" ATÉ 24"	± 1/32
ACIMA DE 24"	± 1/16

VIDROS VITON LTDA.	DES. Carlos A. Demétrio
MAT AÇO SAE 1020	VER. Fabellon
NOM. 00	DE 0
DE 00	DE 0
DE 00	DE 0
DETALHE P/ CORTAR A MAÇARICO AUTOM. AS PEÇAS-VV-594, VV-1787	VE- 859
TRAT.	ESCALA 1:1
TERM.	DES