


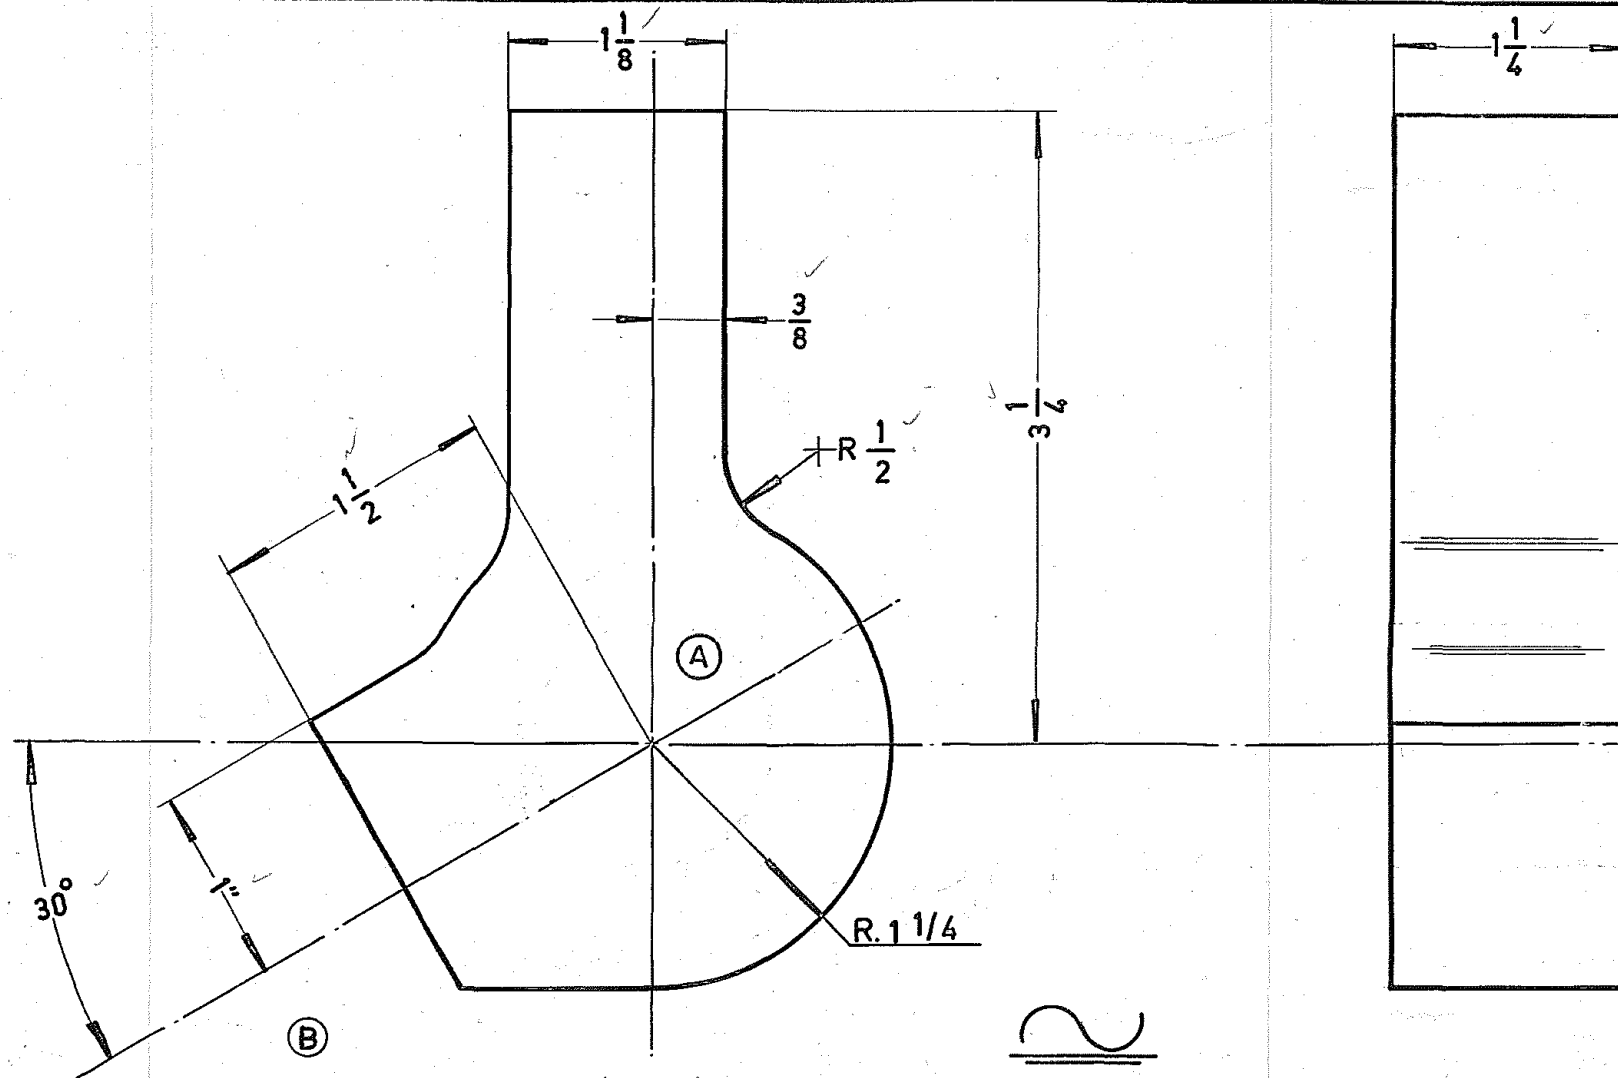

|         | B                   | A                         |
|---------|---------------------|---------------------------|
|         | ELIM. $\frac{7}{8}$ | ELIM. $\phi 1\frac{1}{4}$ |
| 4-10-79 |                     |                           |
| 27-4-78 |                     |                           |

DATA 4-5-1976

COLEÇÃO'S STANDARD  
PARA 9 CALIBRES  
UNIDADE 100

ELIMINAR O P/10  
O P/10  $\pm 1/100$

ELIMINAR O P/10  
O P/10  $\pm 1/100$   
O P/10  $\pm 1/100$   
O P/10  $\pm 1/100$

VIDROS YITON LTDA.

CHAPA DE AÇO SAE 1020

DETALHE P/ CORTAR A MAÇARICO  
AUTOM. PEÇA N° VV- 507

1:1

DES. *Pereira*  
VER. *Faballeria*

VE-898