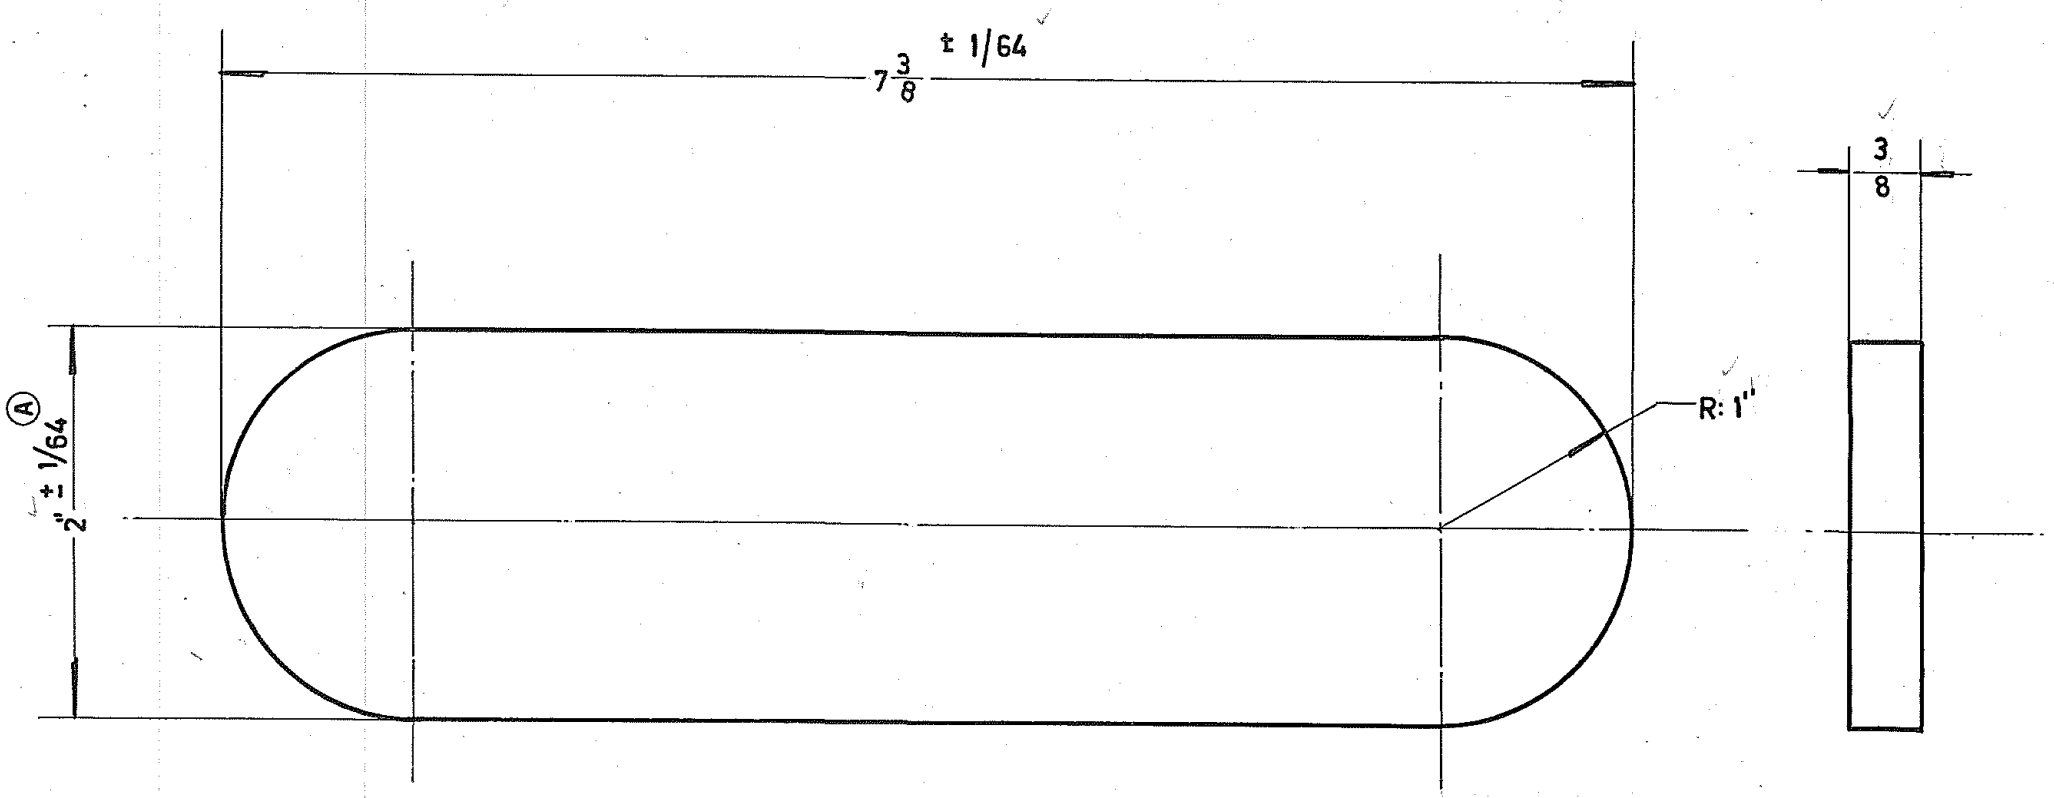

NOTA!
USAR CHAPELONA DO DES. VE-842

13-4-77 ACRESC. TOLERAN. A	DATA 9-11-76	VIDROS VITON LTDA.	DES. Carlos
	TOLERANCIAS STANDARD PARA SUPERFICIES USINADAS SEM TOLERANCIA INDICADA	CHAPA DE AÇO SAE 1020	VER. J. Caballeira
	DECIMAL ± 005"		
	FRAÇÃO DE 0" ATÉ 6" ± 1/64 DE 6" ATÉ 24" ± 1/32 ACIMA DE 24"	DETALHE P/CORTAR A MAÇARICO AUT. APEÇA 111-6727	VE-990
			1:1

FOLHA 236