


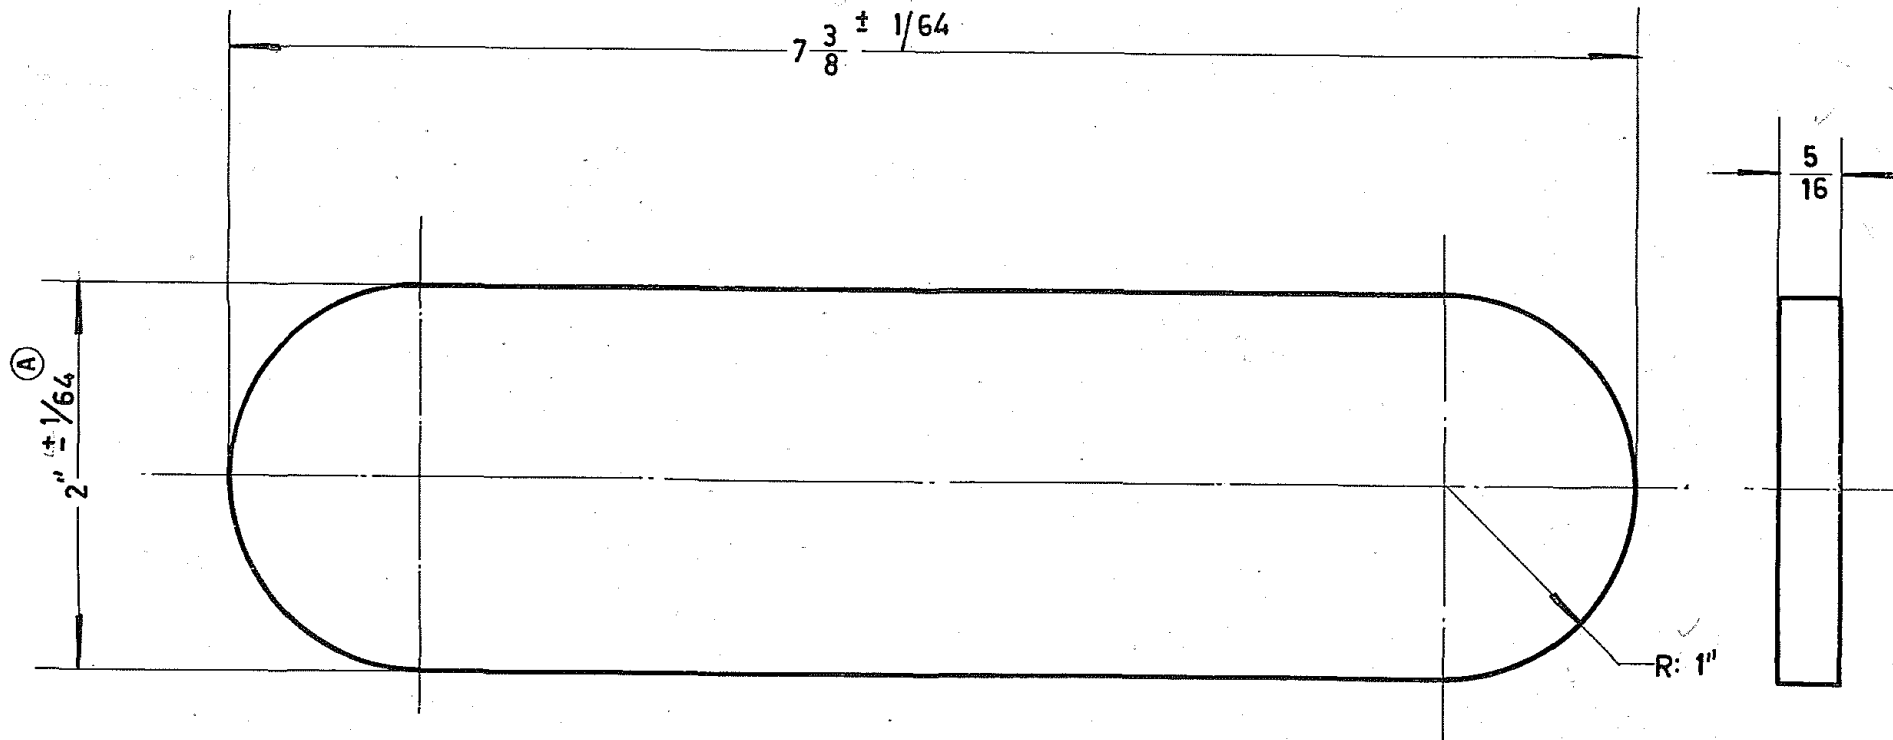

NOTA!

USAR CHAPELONA DO DES.VE-842

13-4-77 ACRES. Pecis TOLERAN.	A	DATA	9-11-76	VIDROS VITON LTDA.	DES.	Carlos
		TOLERANCIAS STANDARD PARA SUPERFICIES USINADAS SEM TOLERANCIA INDICADA			VER.	de Abalho
		DE 0" ATÉ 5" $\pm \frac{1}{64}$			ATE	
		DE 5" ATÉ 24" $\pm \frac{1}{32}$			Nº DO	
ACIMA DE 24" $\pm \frac{1}{16}$		DETALHE P/CORTAR A MAÇARICO AUT. A PEÇA 111-6728		COM.		
		Escala		1:1	Nº DA PEÇA	VE-991