


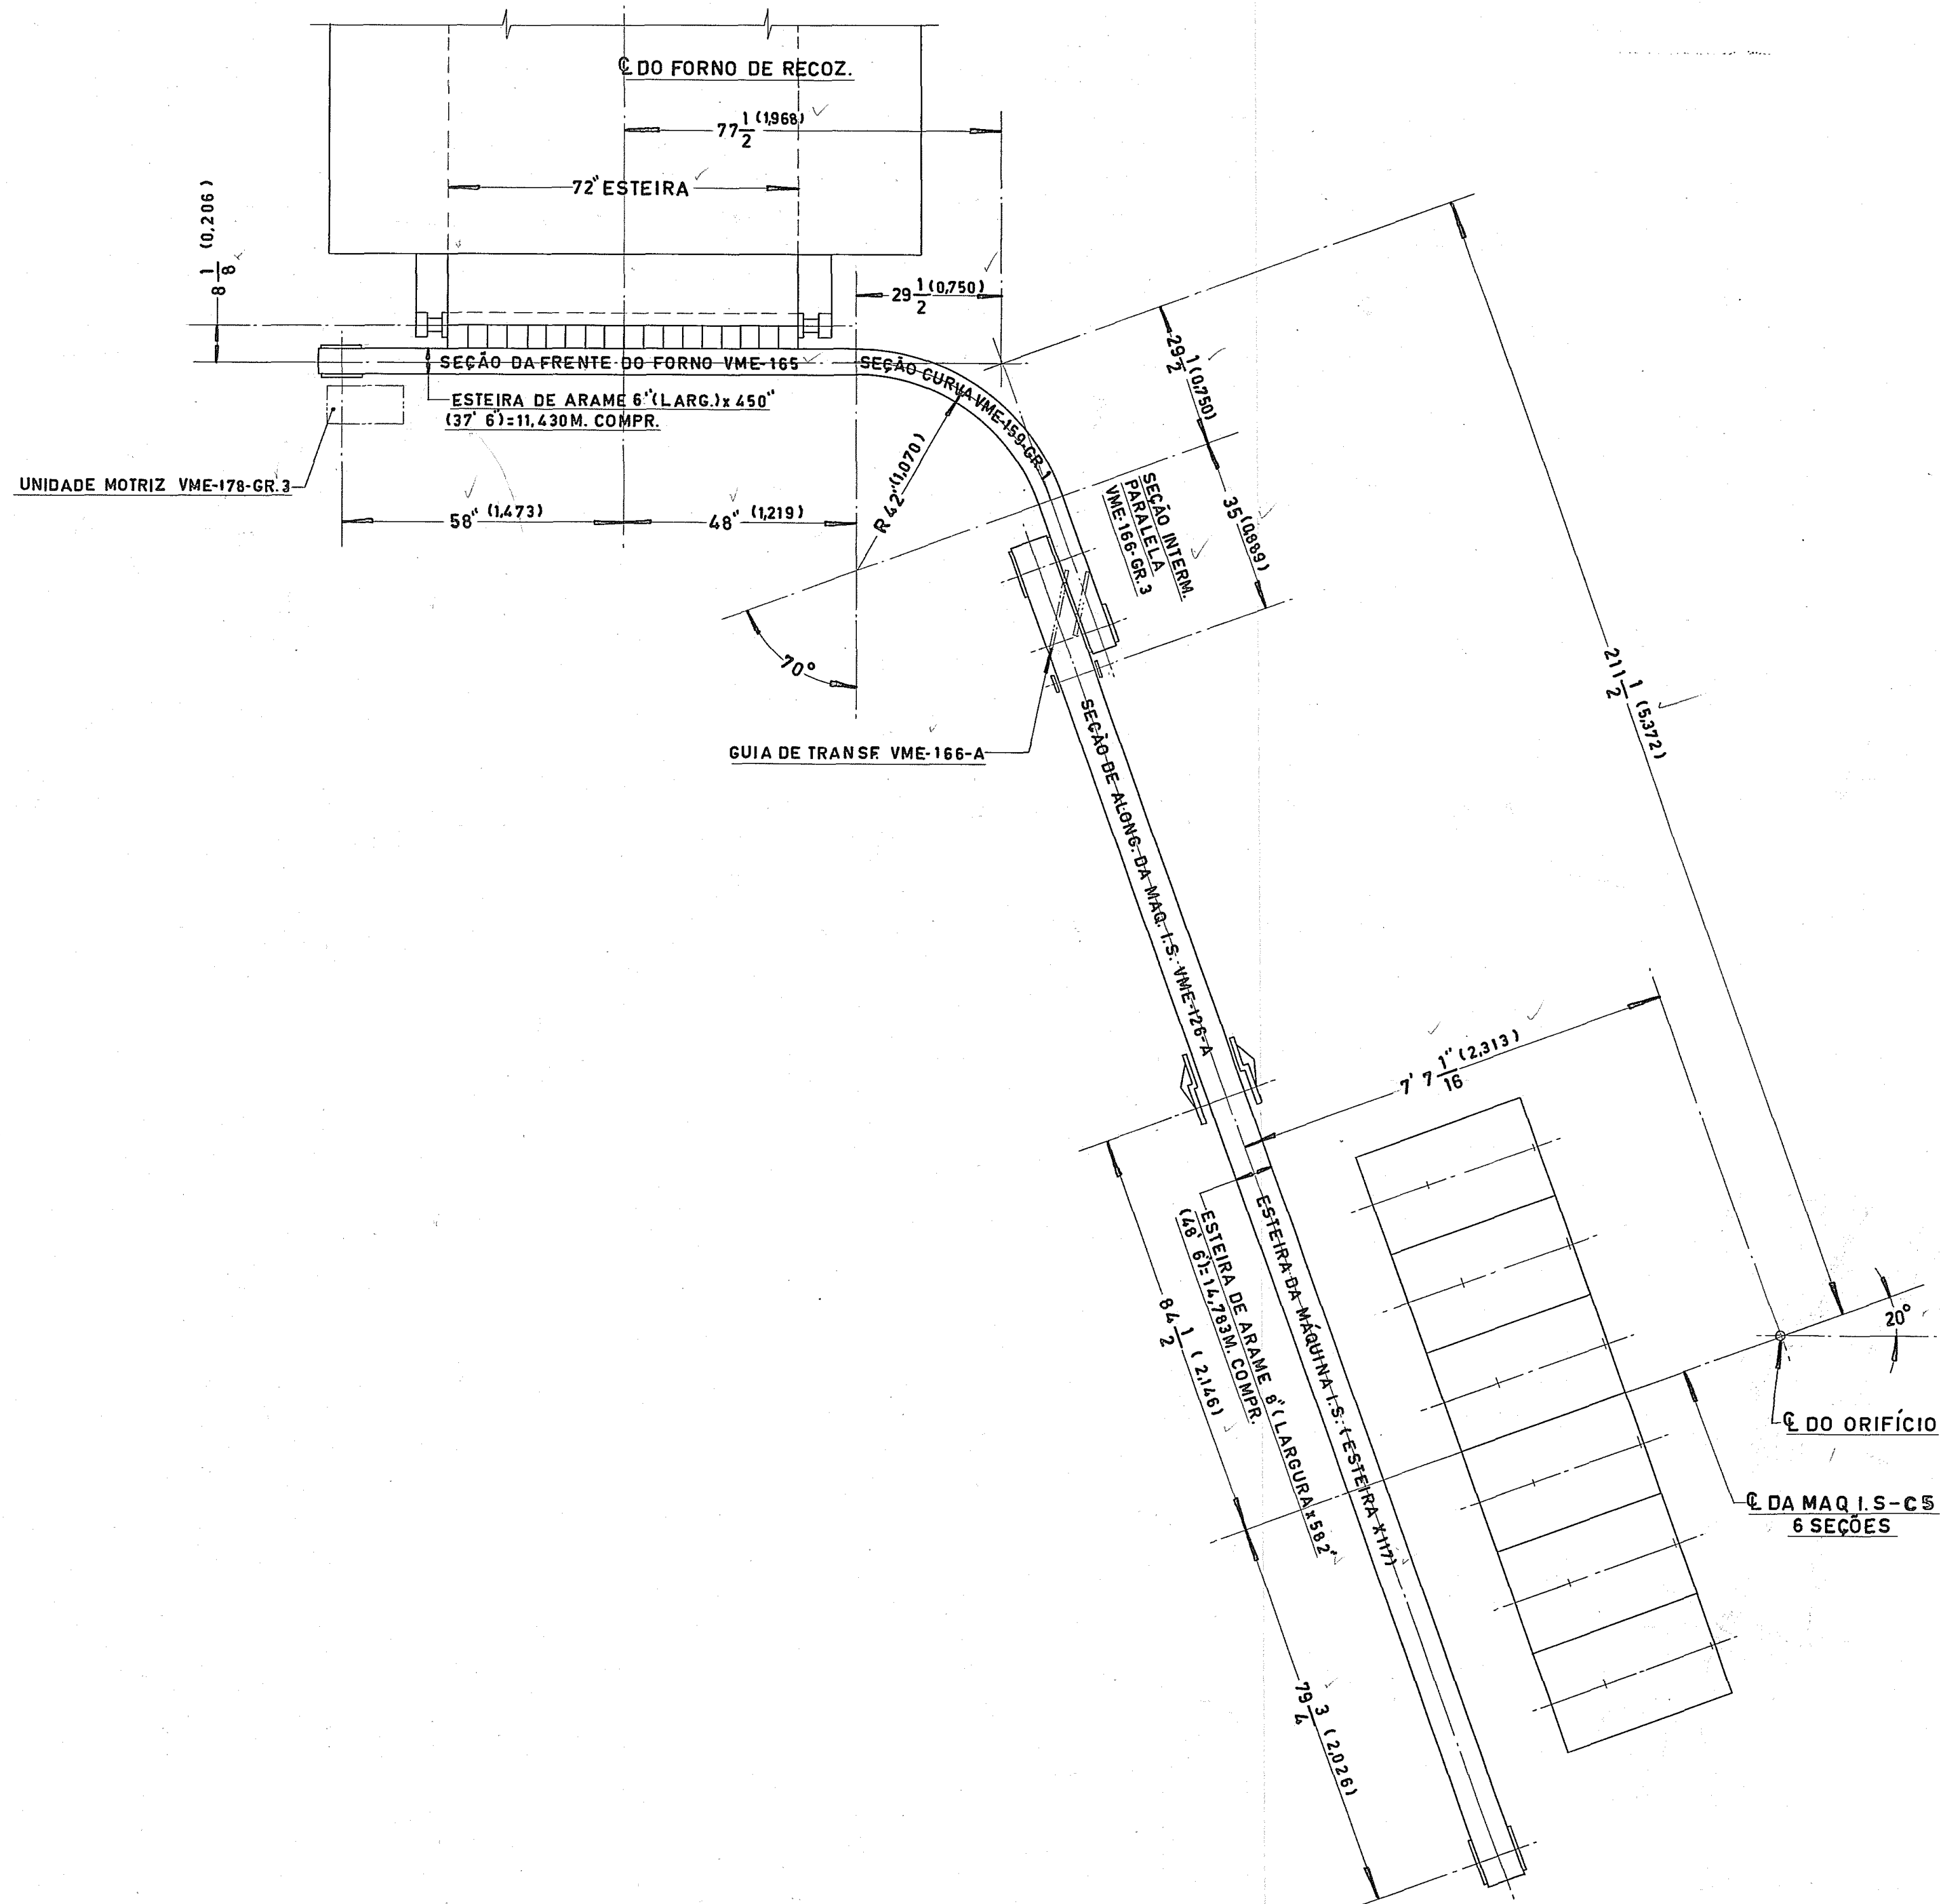

Seq.	VIDROS VITON LTDA.	Data	26-01-76
Pag.		Des.	
Mat.		Escala	1:25
Conjunto	MÁQUINA I.S. 6 SEÇÕES WHEATON-C 5	Ver.	
Nome da Peça	ESQUEMA P/ INSTALAÇÃO DA ESTEIRA CURVA	Subst.	
Tratam. Térmico		N.º da Peça	VP-164
		N.º do Desenho	