


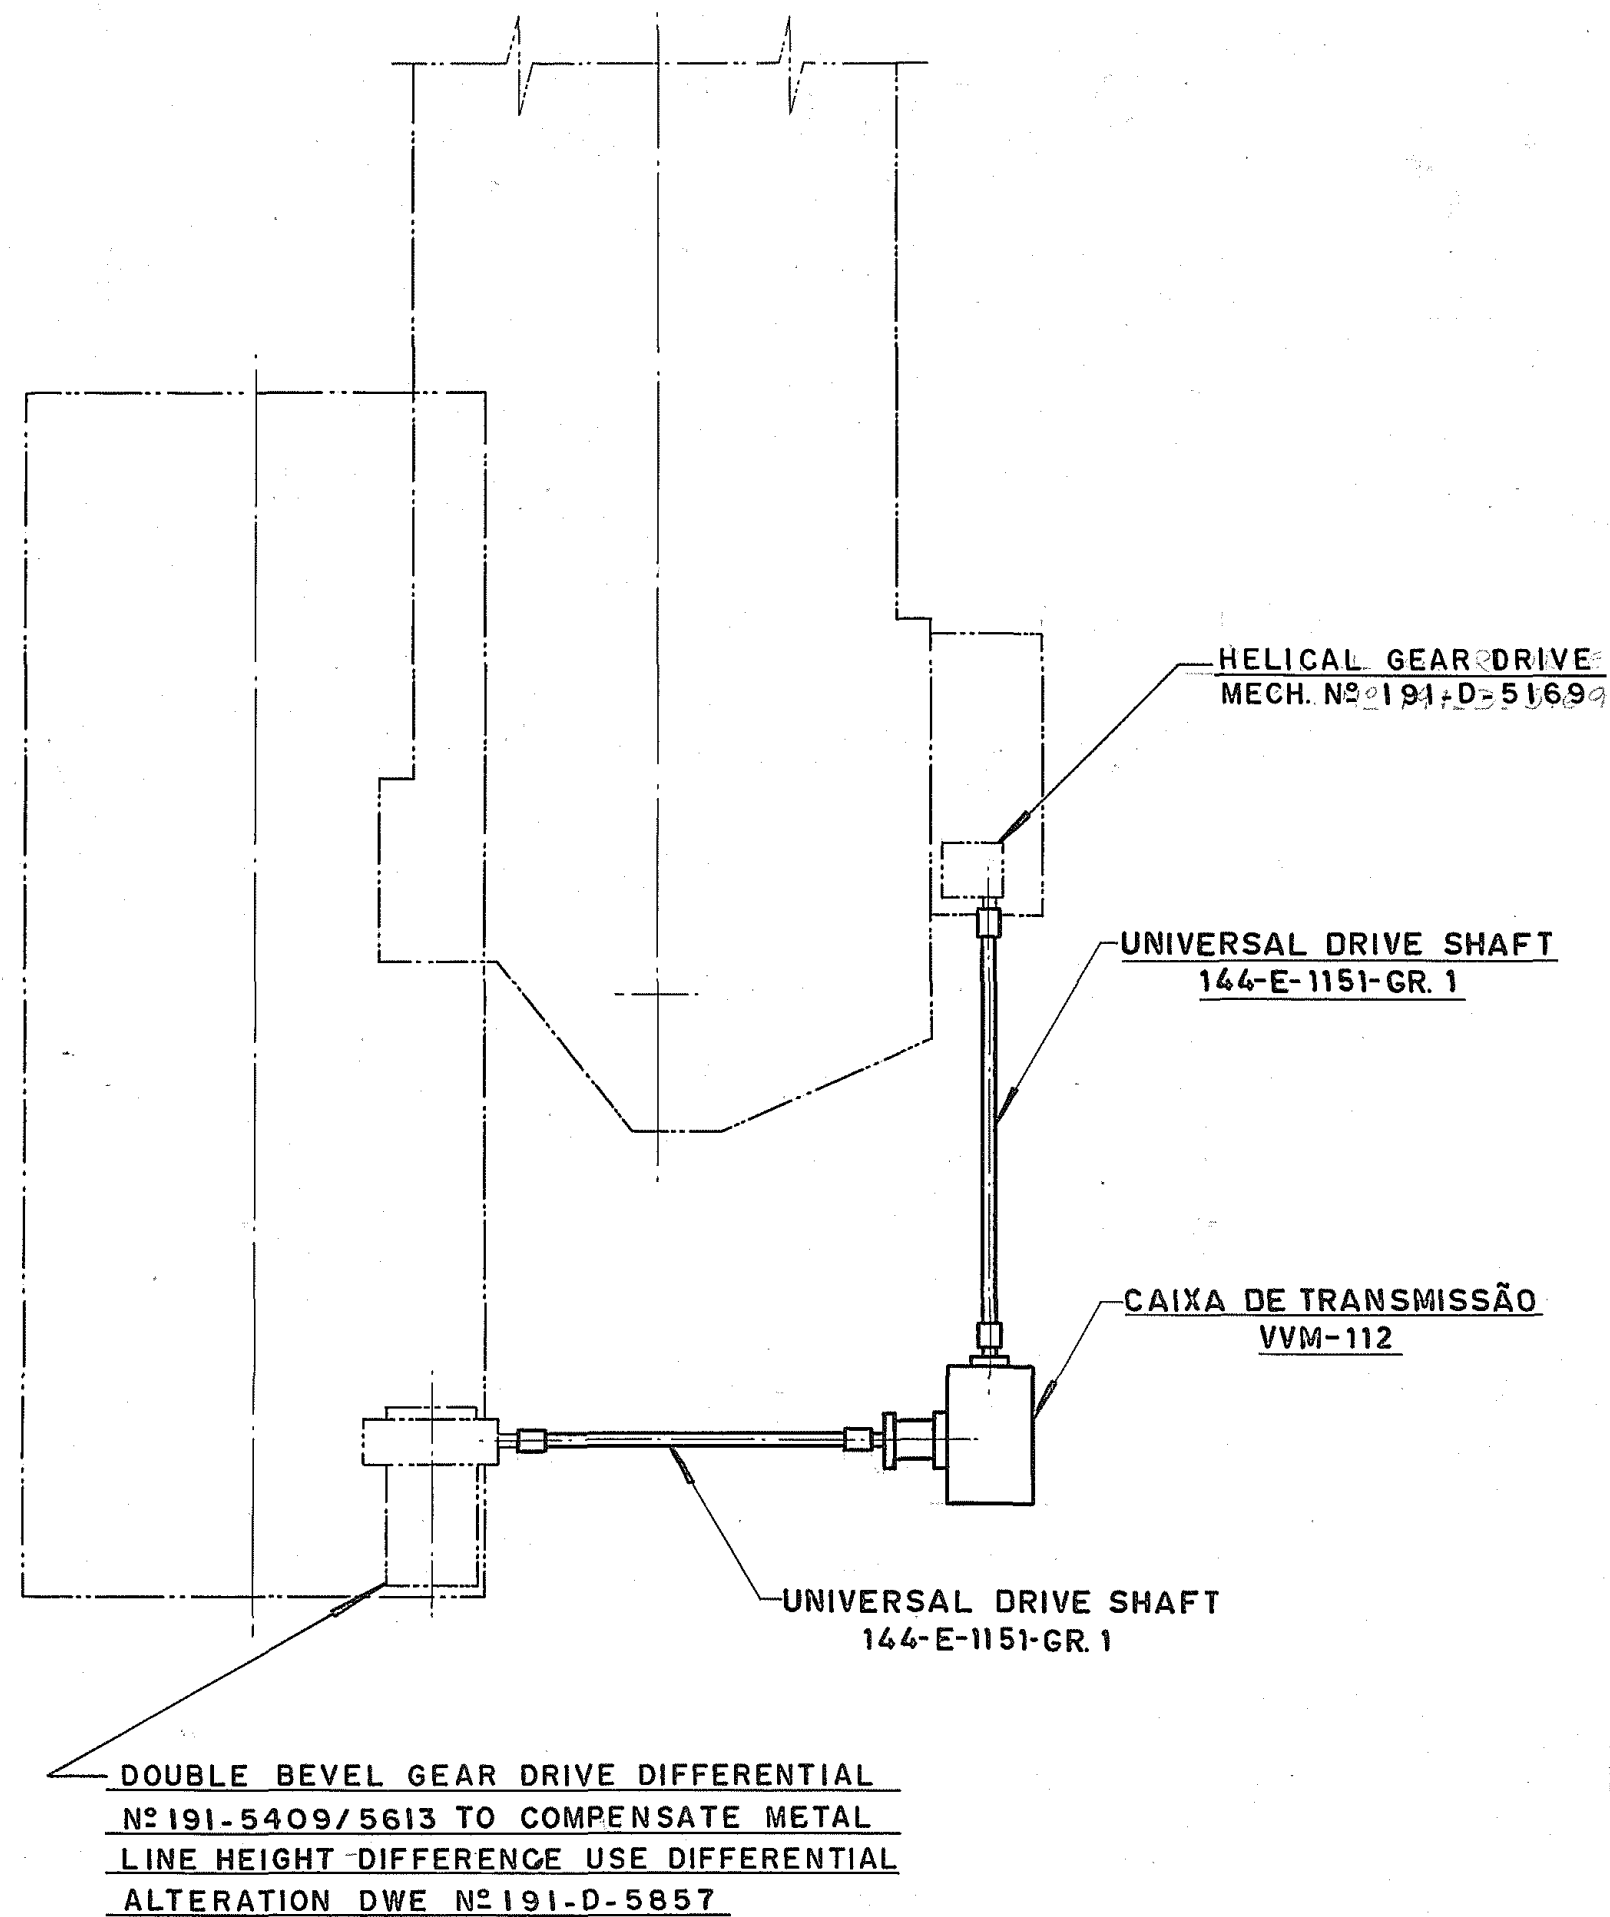

Sec.	VIDROS VITON LTDA.	Data	19-03-76
Pag.		Des.	Ver. 19-03-76
Mat.		Escala	Cop.
Conjunto		0:25	Ver. 19-03-76
Nome da Peça	ESQUEMA P/LIGAÇÃO DE UMA MAQ.I.S. INSTALADA A 90°A ESQUERDA (COMPANHIA NACIONAL DE VIDRIOS-SA)		N.º da Peça VP-165
Tratam. Térmico		N.º do Desenho	