


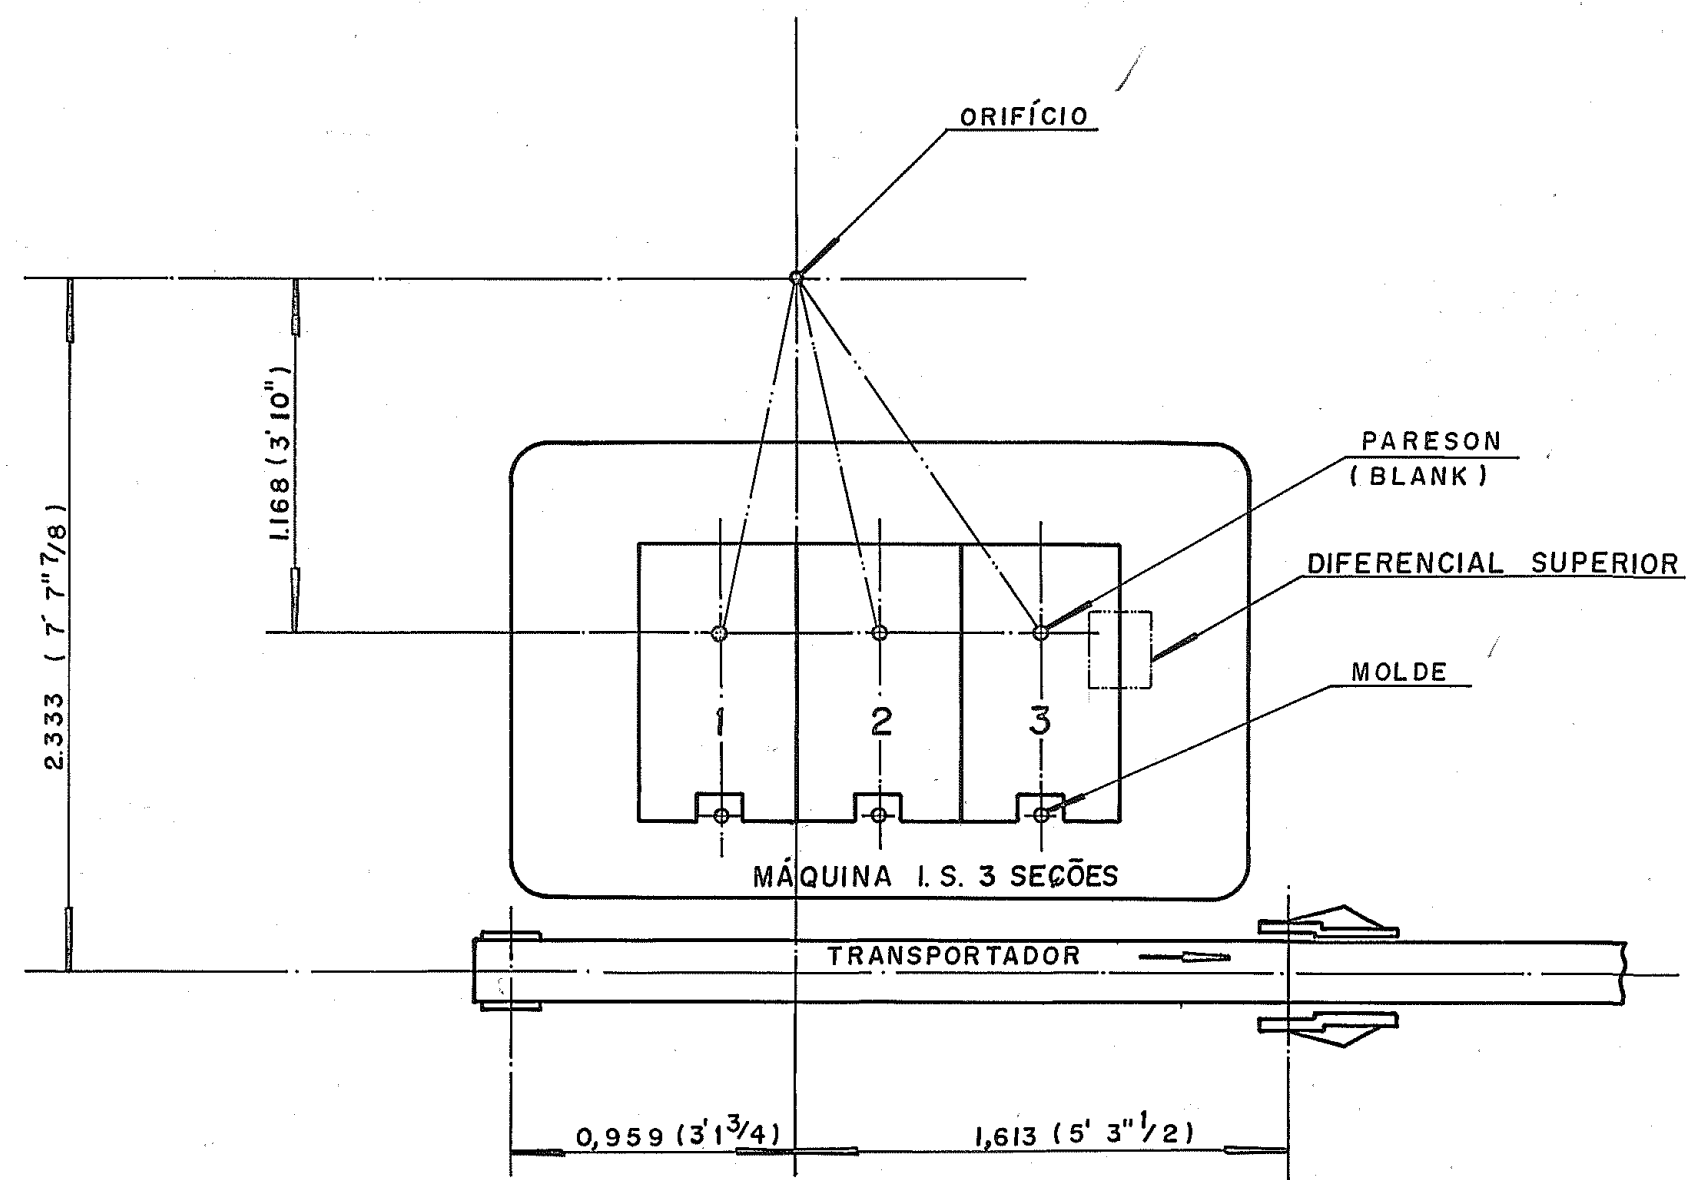

LAS SECCIONES 1 - 2 - 3 CORRESPONDEM
A LAS SECCIONES 3 - 4 - 5 DE LA
MÁQUINA I. S. 6 SECCIONES

VIDROS VITON LTDA.		DES.	<i>[Signature]</i>
		VER.	<i>[Signature]</i>
MAT:		DATA	30-09-92
PLANTA DE UMA MÁQUINA I.S.		N.º DO PROJ.	
PEÇA TIPO "E" DE 3 SEÇ. - SAÍDA LADO DIR.		N.º DA PEÇA	VP-227 ✓
TRAT.	ESCALA	N.º DO DES.	
TERM.			