

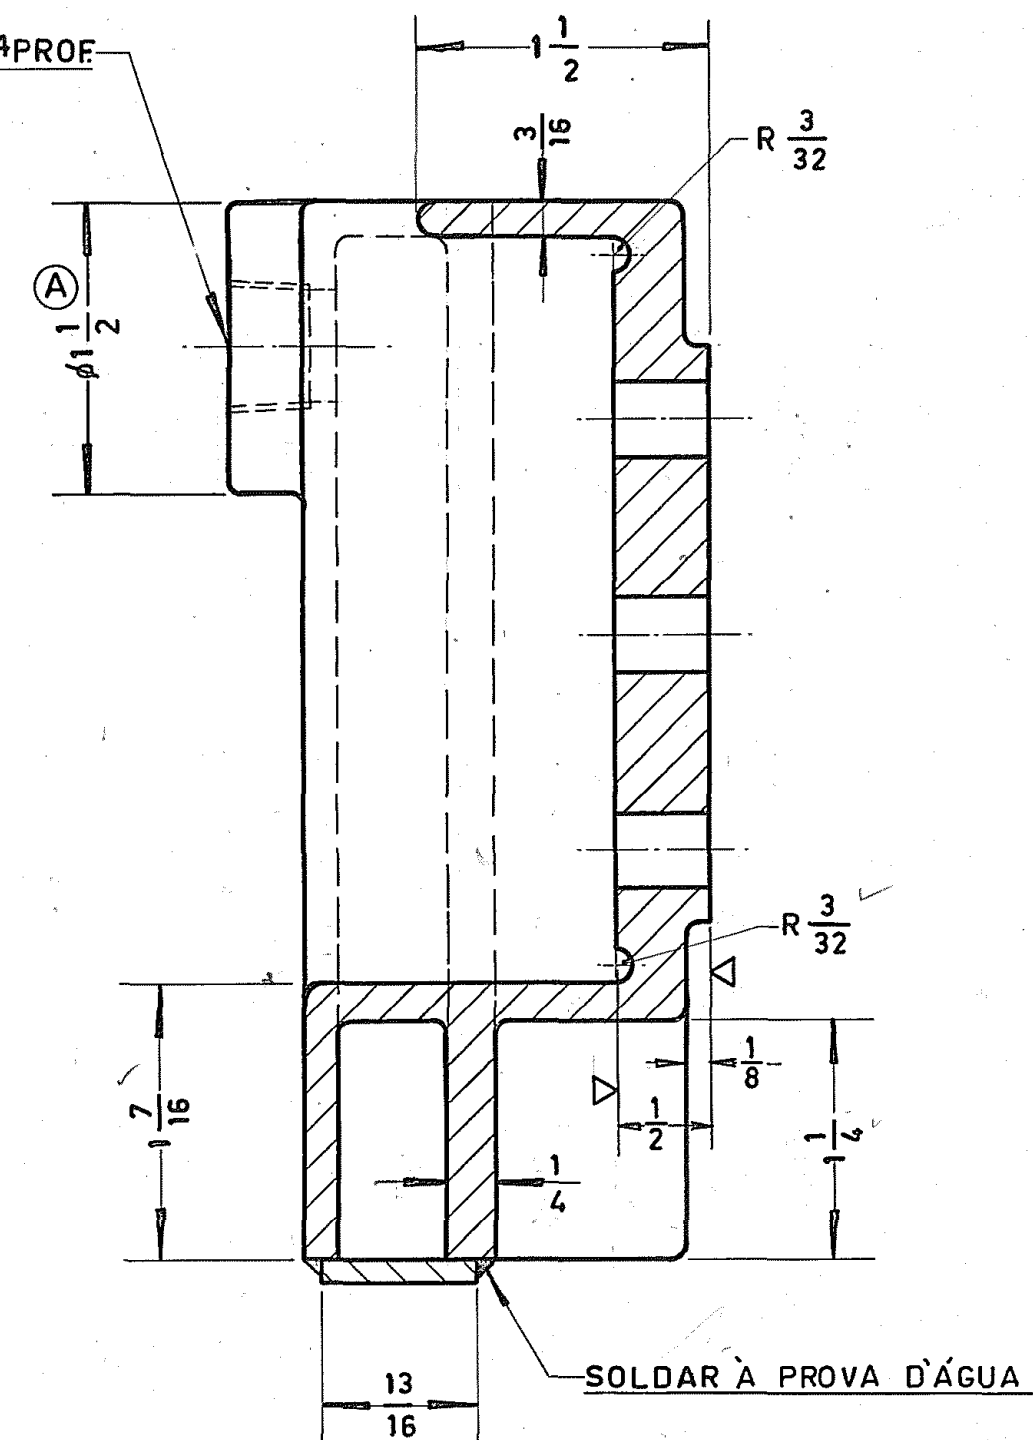
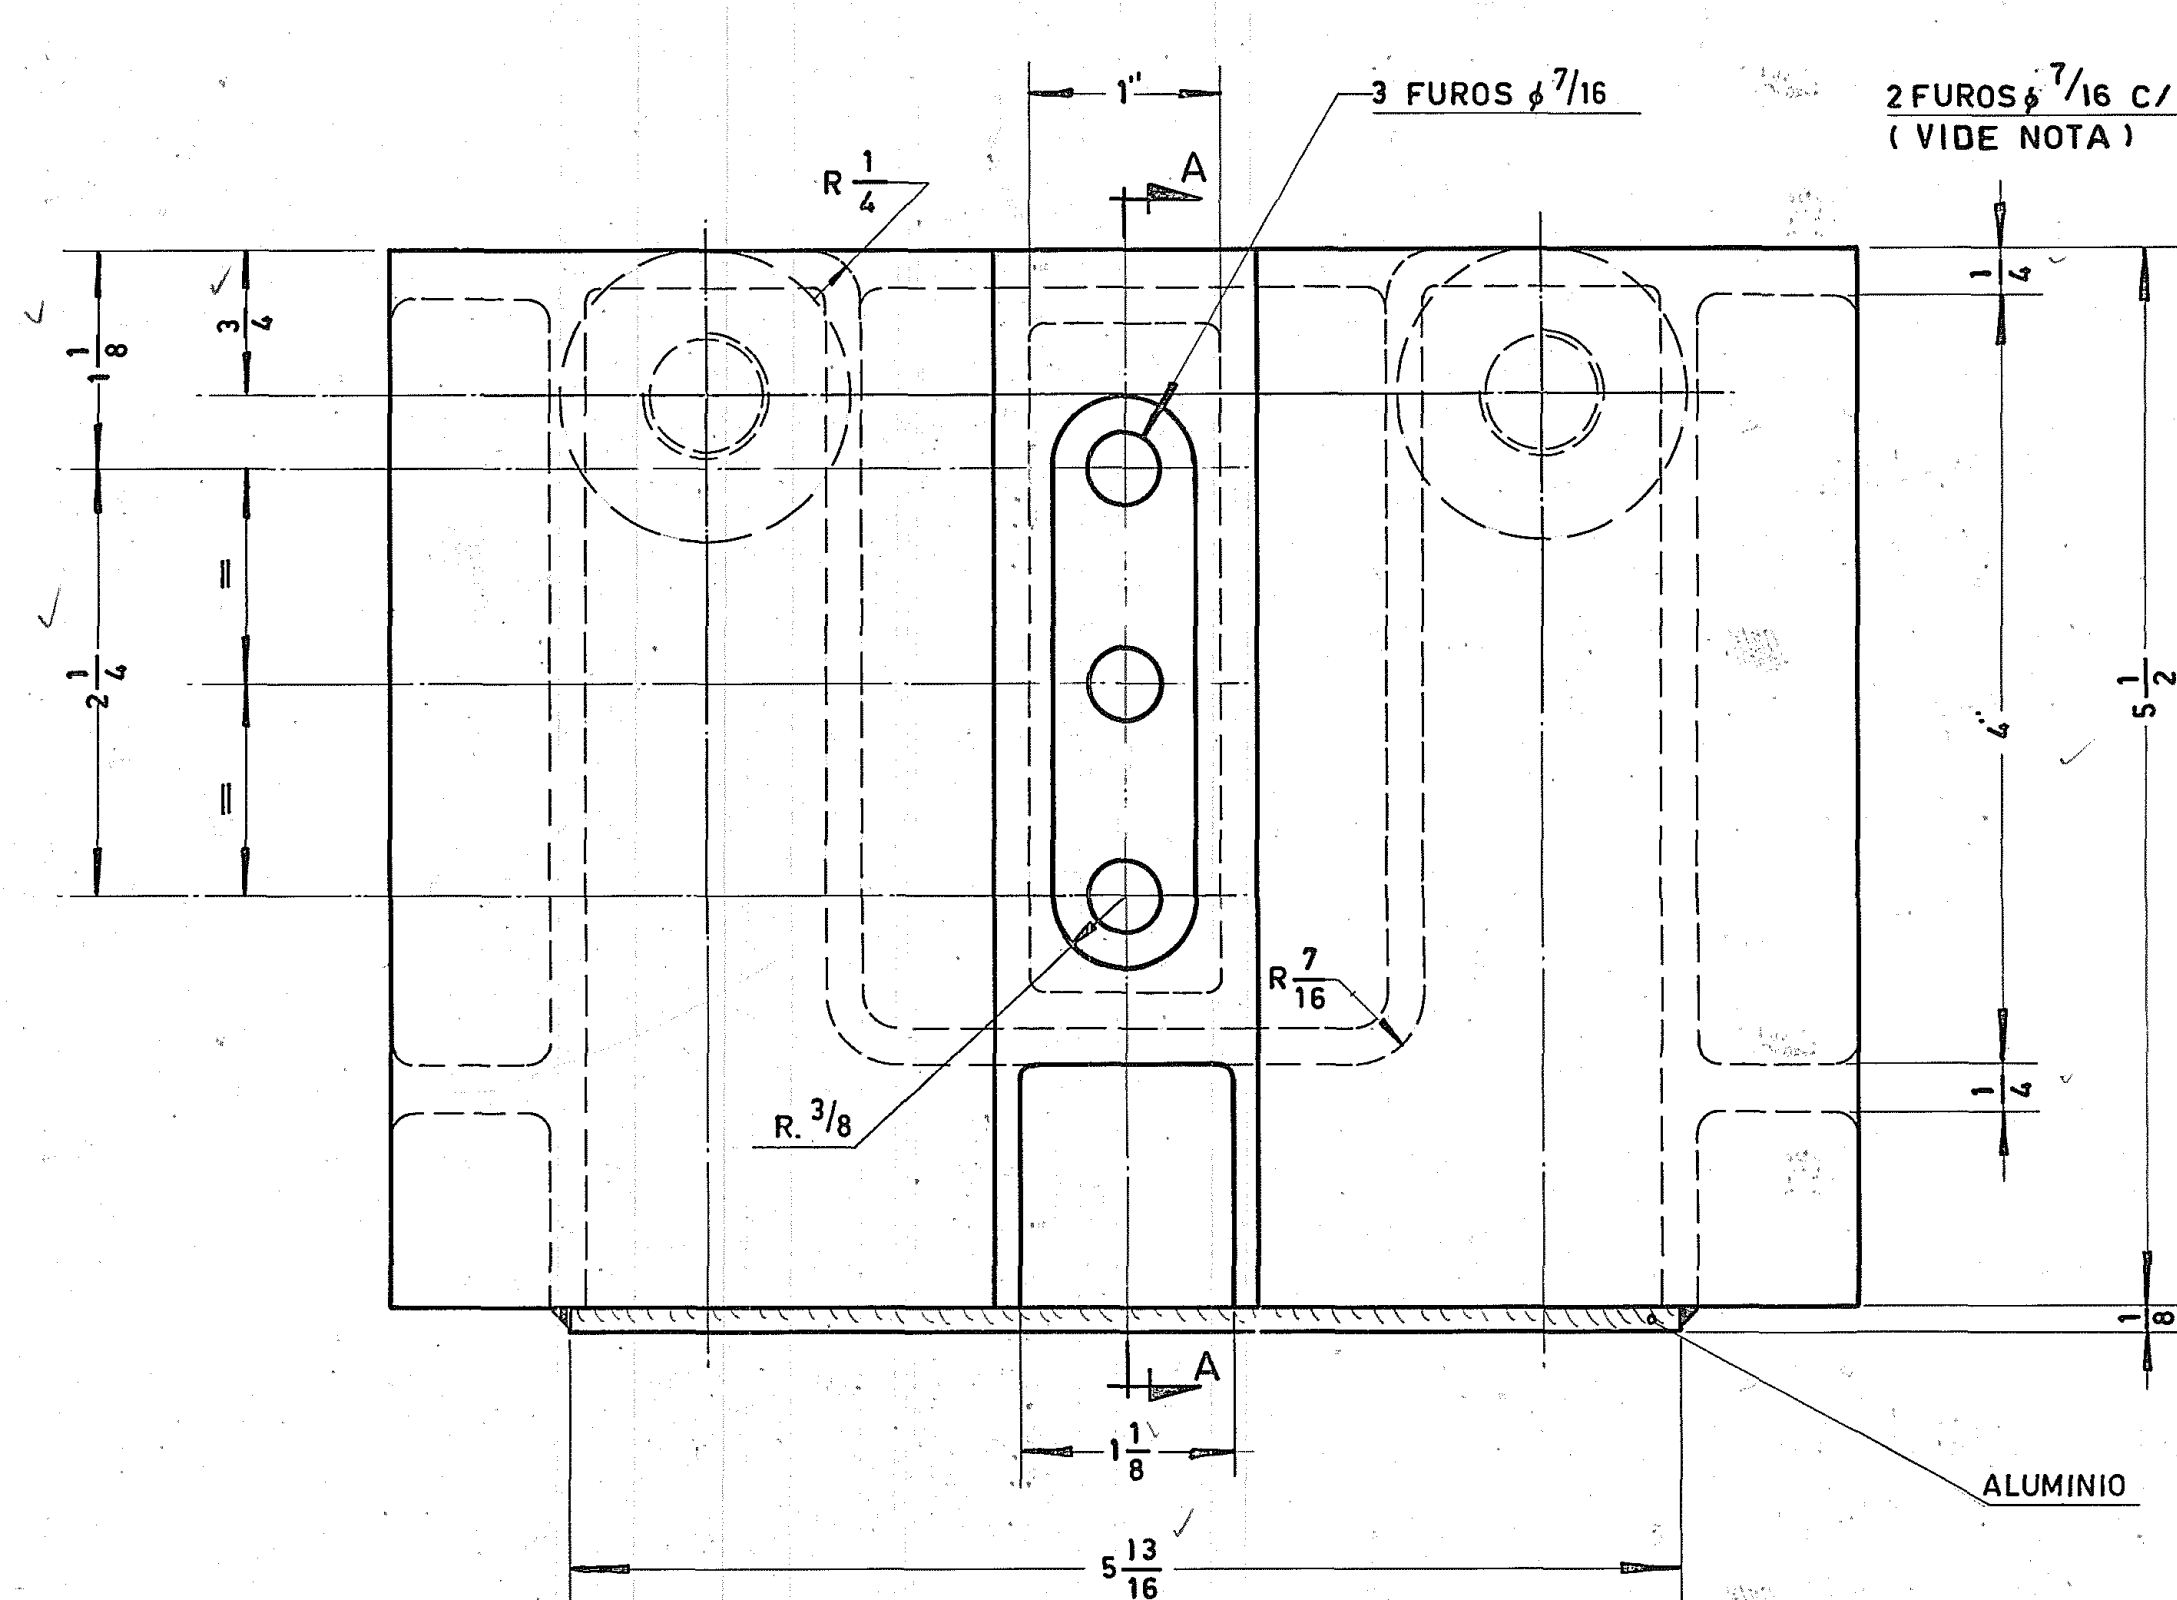


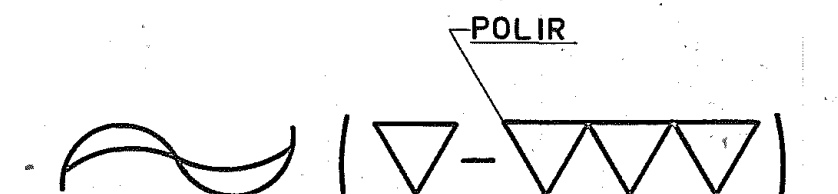

CORTE A-A

NOTA
FAZER TESTE DE PROVA
DE VAZAMENTO C/ ÁGUA,
ANTES DE POLIR

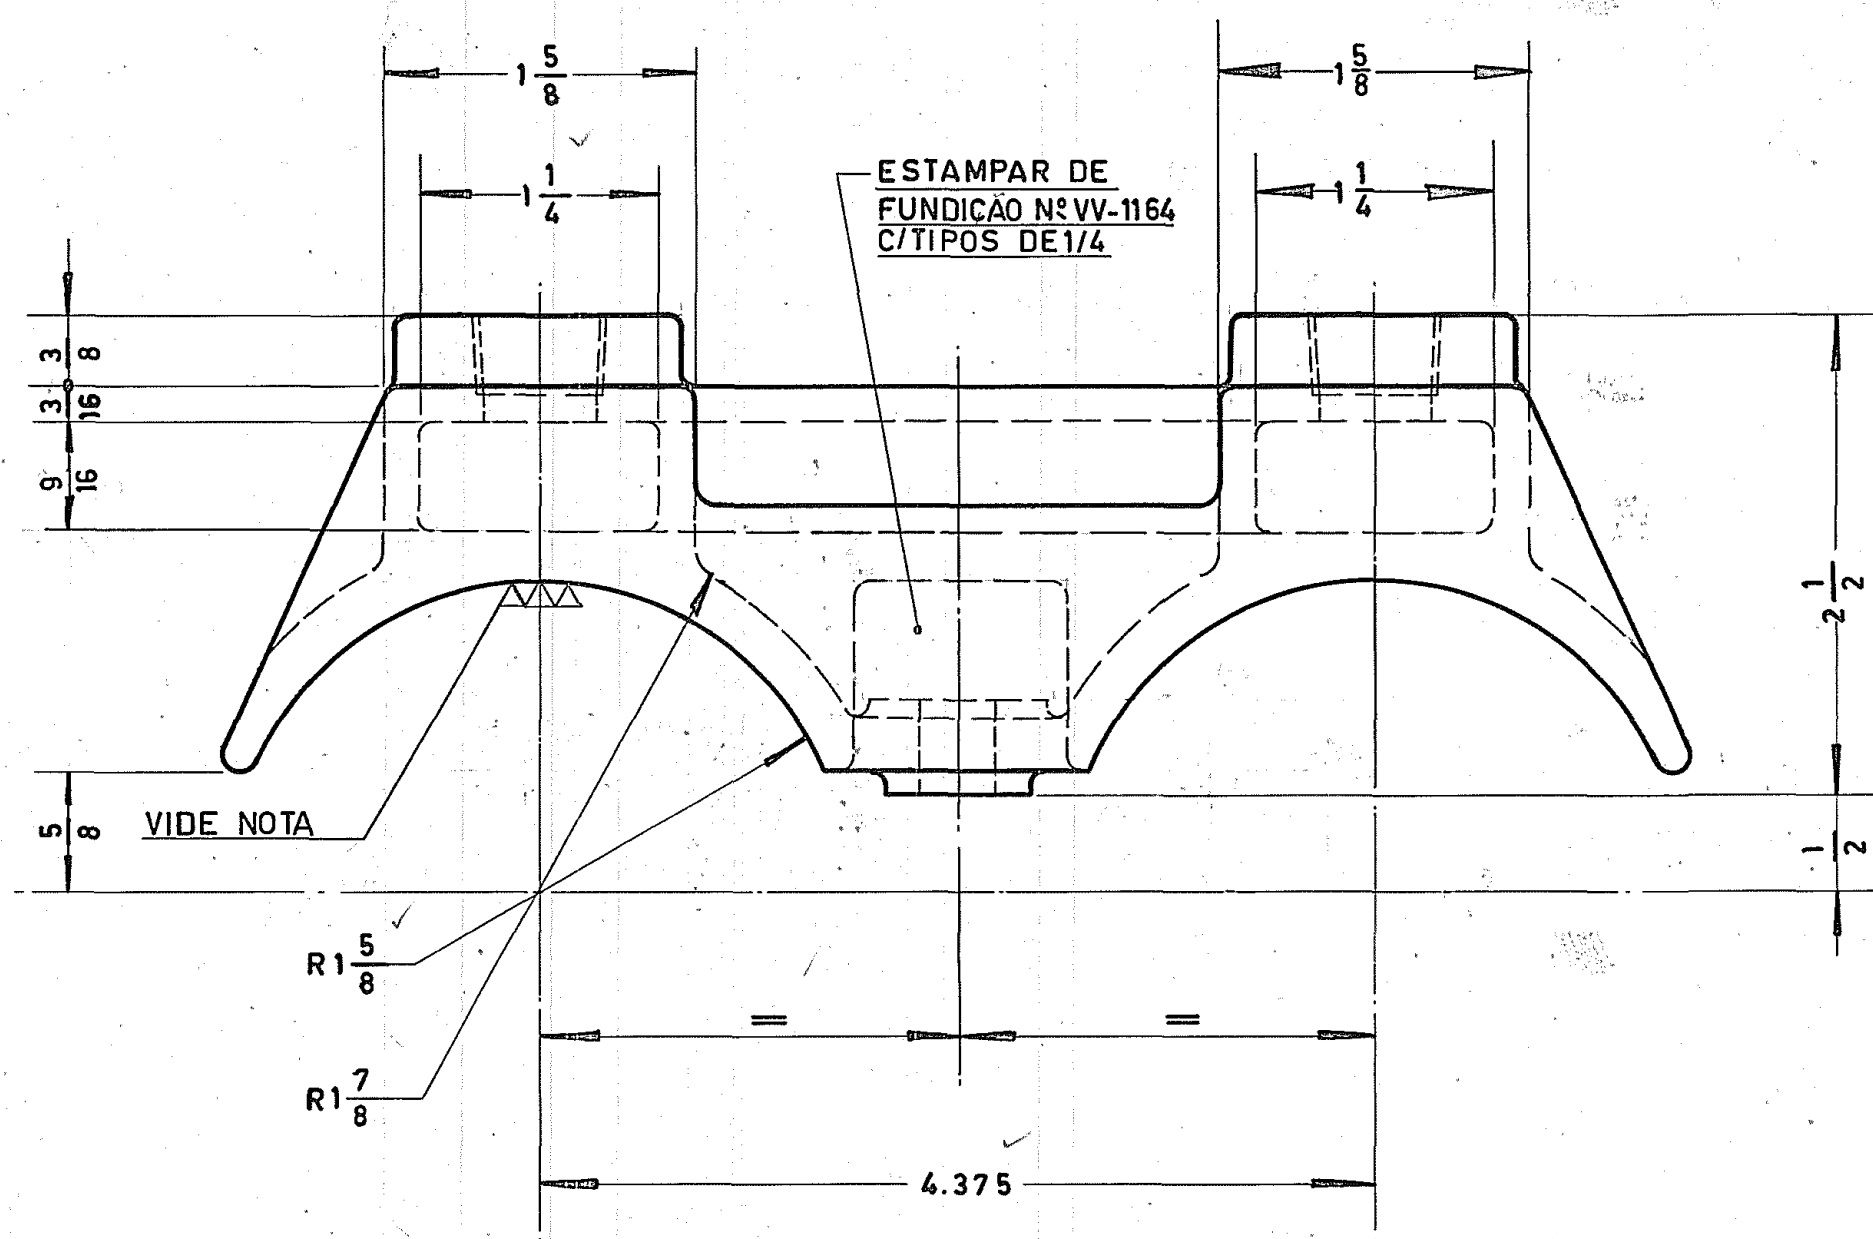

C	B	A	ITEM	DATA: 03-11-81		VIDROS VITON LTDA.		DES. <i>Paulo A. V.</i>
				TOLERANCIAS STANDARD PARA SUPERFICIES USINADAS SEM TOLERANCIA INDICADA		MAT. ALUMINIO FUNDIDO SAE 323 (B)		V.R. <i>Paulo A. V.</i>
ERA FURO 8.11.96 3/8 NPT	ERA 22.6.92 SAE 310	ERA 5.12.88 SAE 310	ERA 5.12.88 SAE 310	DE 0" A 5" ± 0.05 "		GOB INTERCEPTOR		VVM-205
FRAÇÃO				DE 0" ATÉ 5" $\pm 1/64$		GOB GUIDE		VV-1164
DE 5" ATÉ 24" $\pm 1/32$				ACIMA DE 24" $\pm 1/16$		TRAT. TERM.		DES.
ESCALA 1:1				FOLHA 5		(L)		