


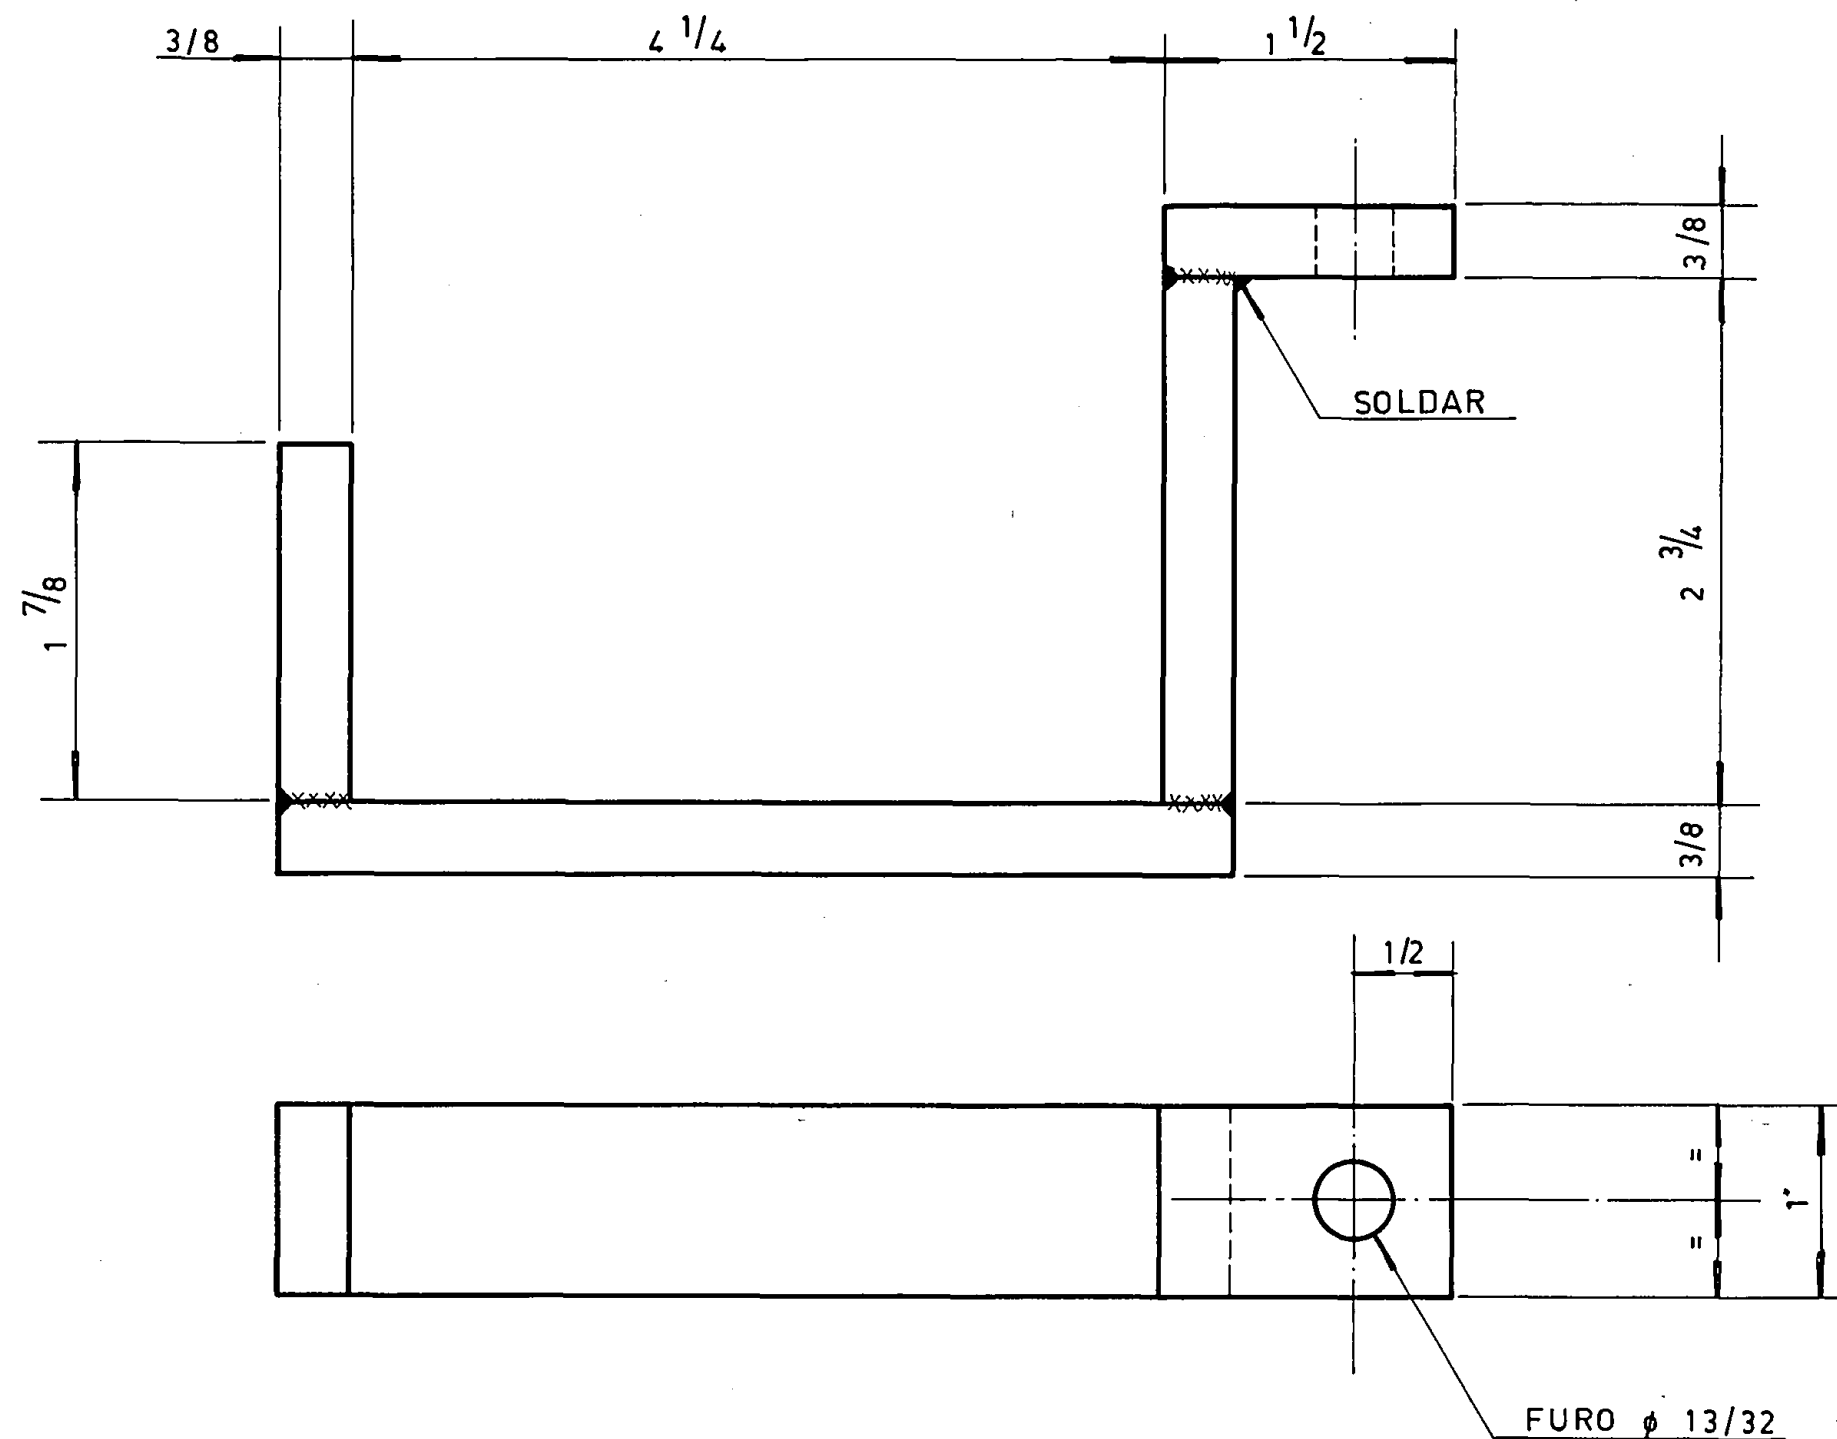

DATA: 08-07-85	VIDROS VITON LTDA.	DES. <i>[Signature]</i>
TOLERANCIAS STANDARD PARA SUPERFICIES		VER. <i>[Signature]</i>
USINA DE SIDA	MAQ. FERRO CHATO DE 3/8 x 1"	
COLUNA DE 100MM	MAQ. I.S. 8 SEC.	
	ENCANAMENTO DE PARADA INDIVIDUAL	
	BLOW HEAD E MOLD	
	SUPORTE DO MANIFOLD	VVM-368
		N.º DA PEÇA VV-1226
		N.º DO DES.