


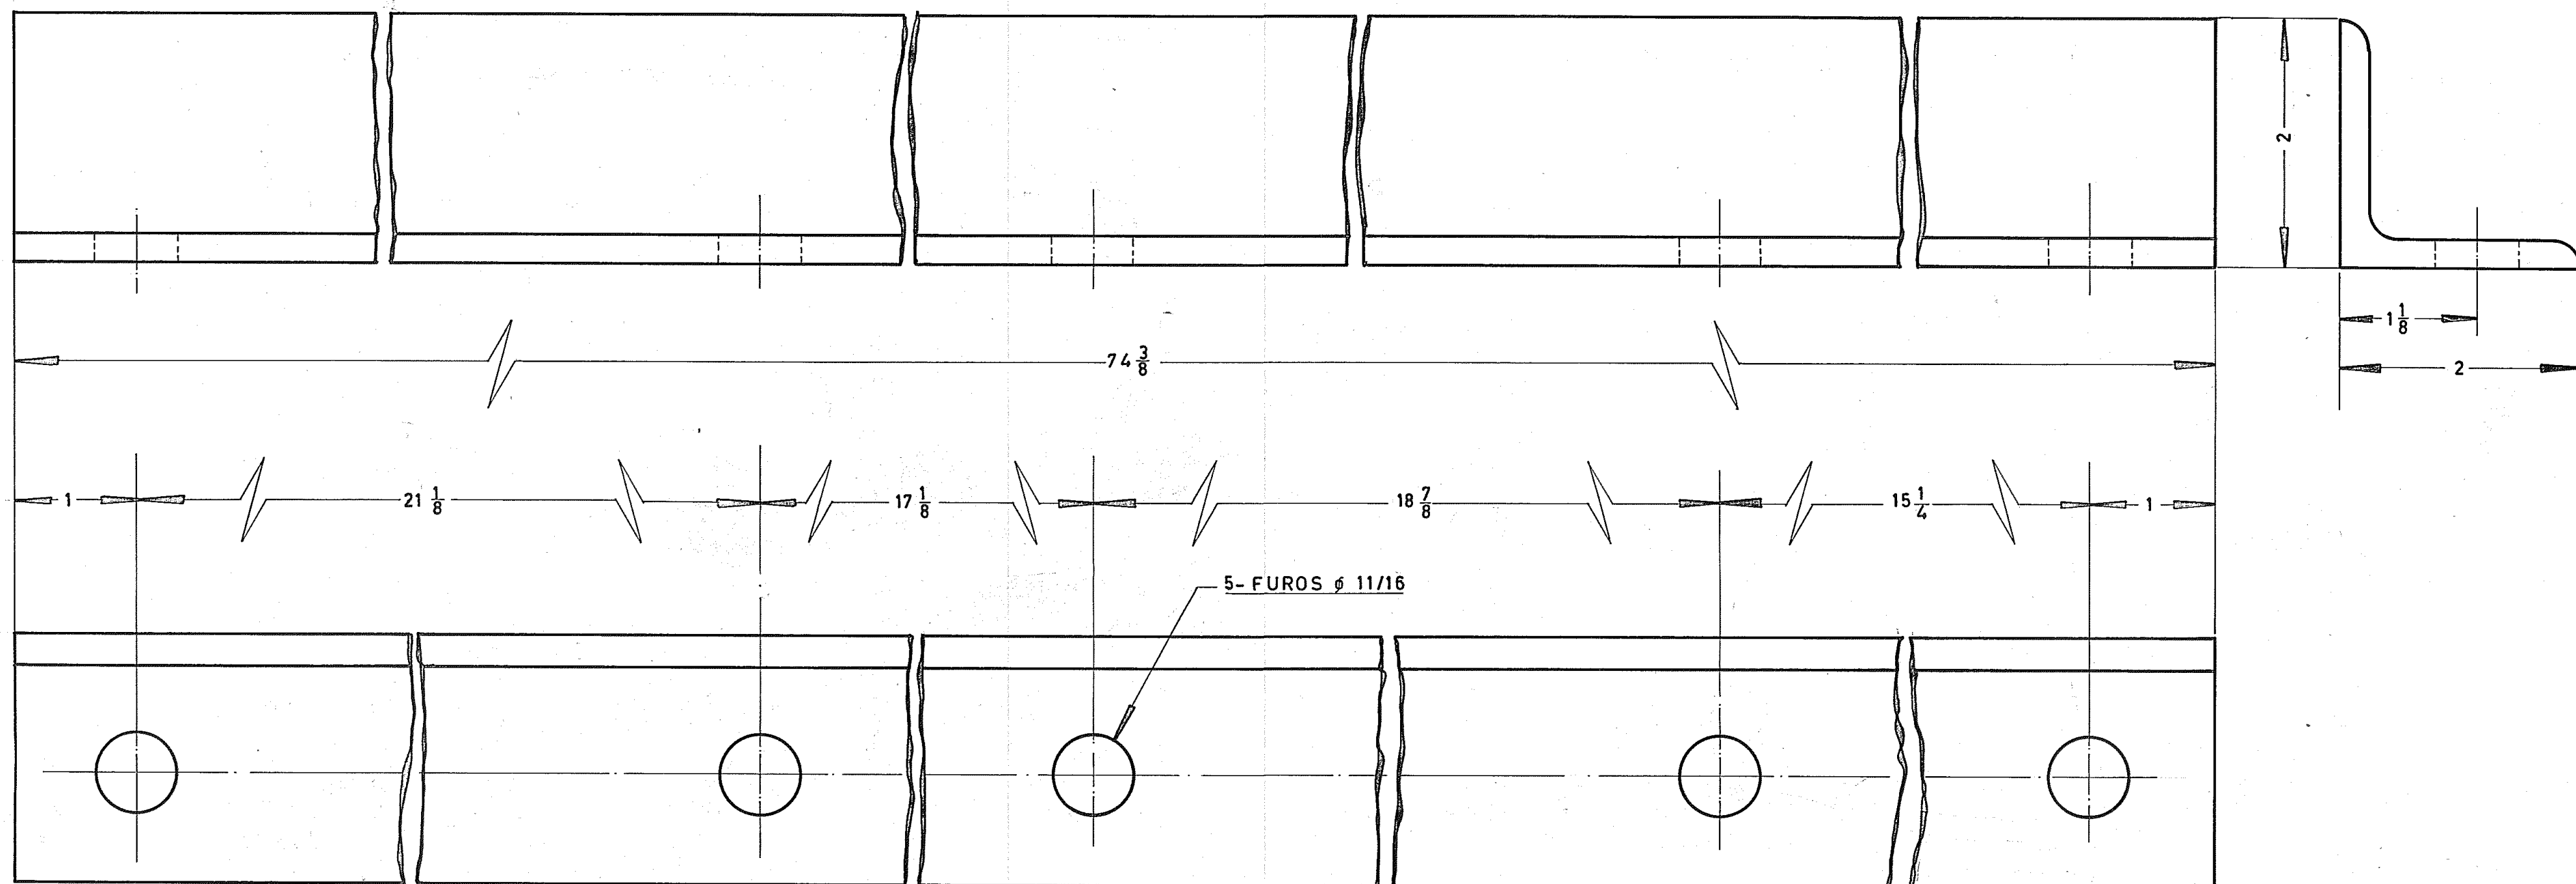

DATA: 22-12-82	DES. <i>W. B. Junior</i>
TOLERÂNCIAS STANDARD PARA SUPERFÍCIES UNIFORMES SEM TOLERÂNCIA INDICADA	VER. <i>W. B. Junior</i>
DE 0" ATE 5" ± 1/64	APR. V. <i>W. B. Junior</i>
DE 5" ATE 24" ± 1/32	N.º DO PROJ. VVM-232
ACIMA DE 24" ± 1/16	N.º DA VV-1365
FEÇA	PEÇA
TRAT. TERM.	ESCALA 1:1
	N.º DO DES.