


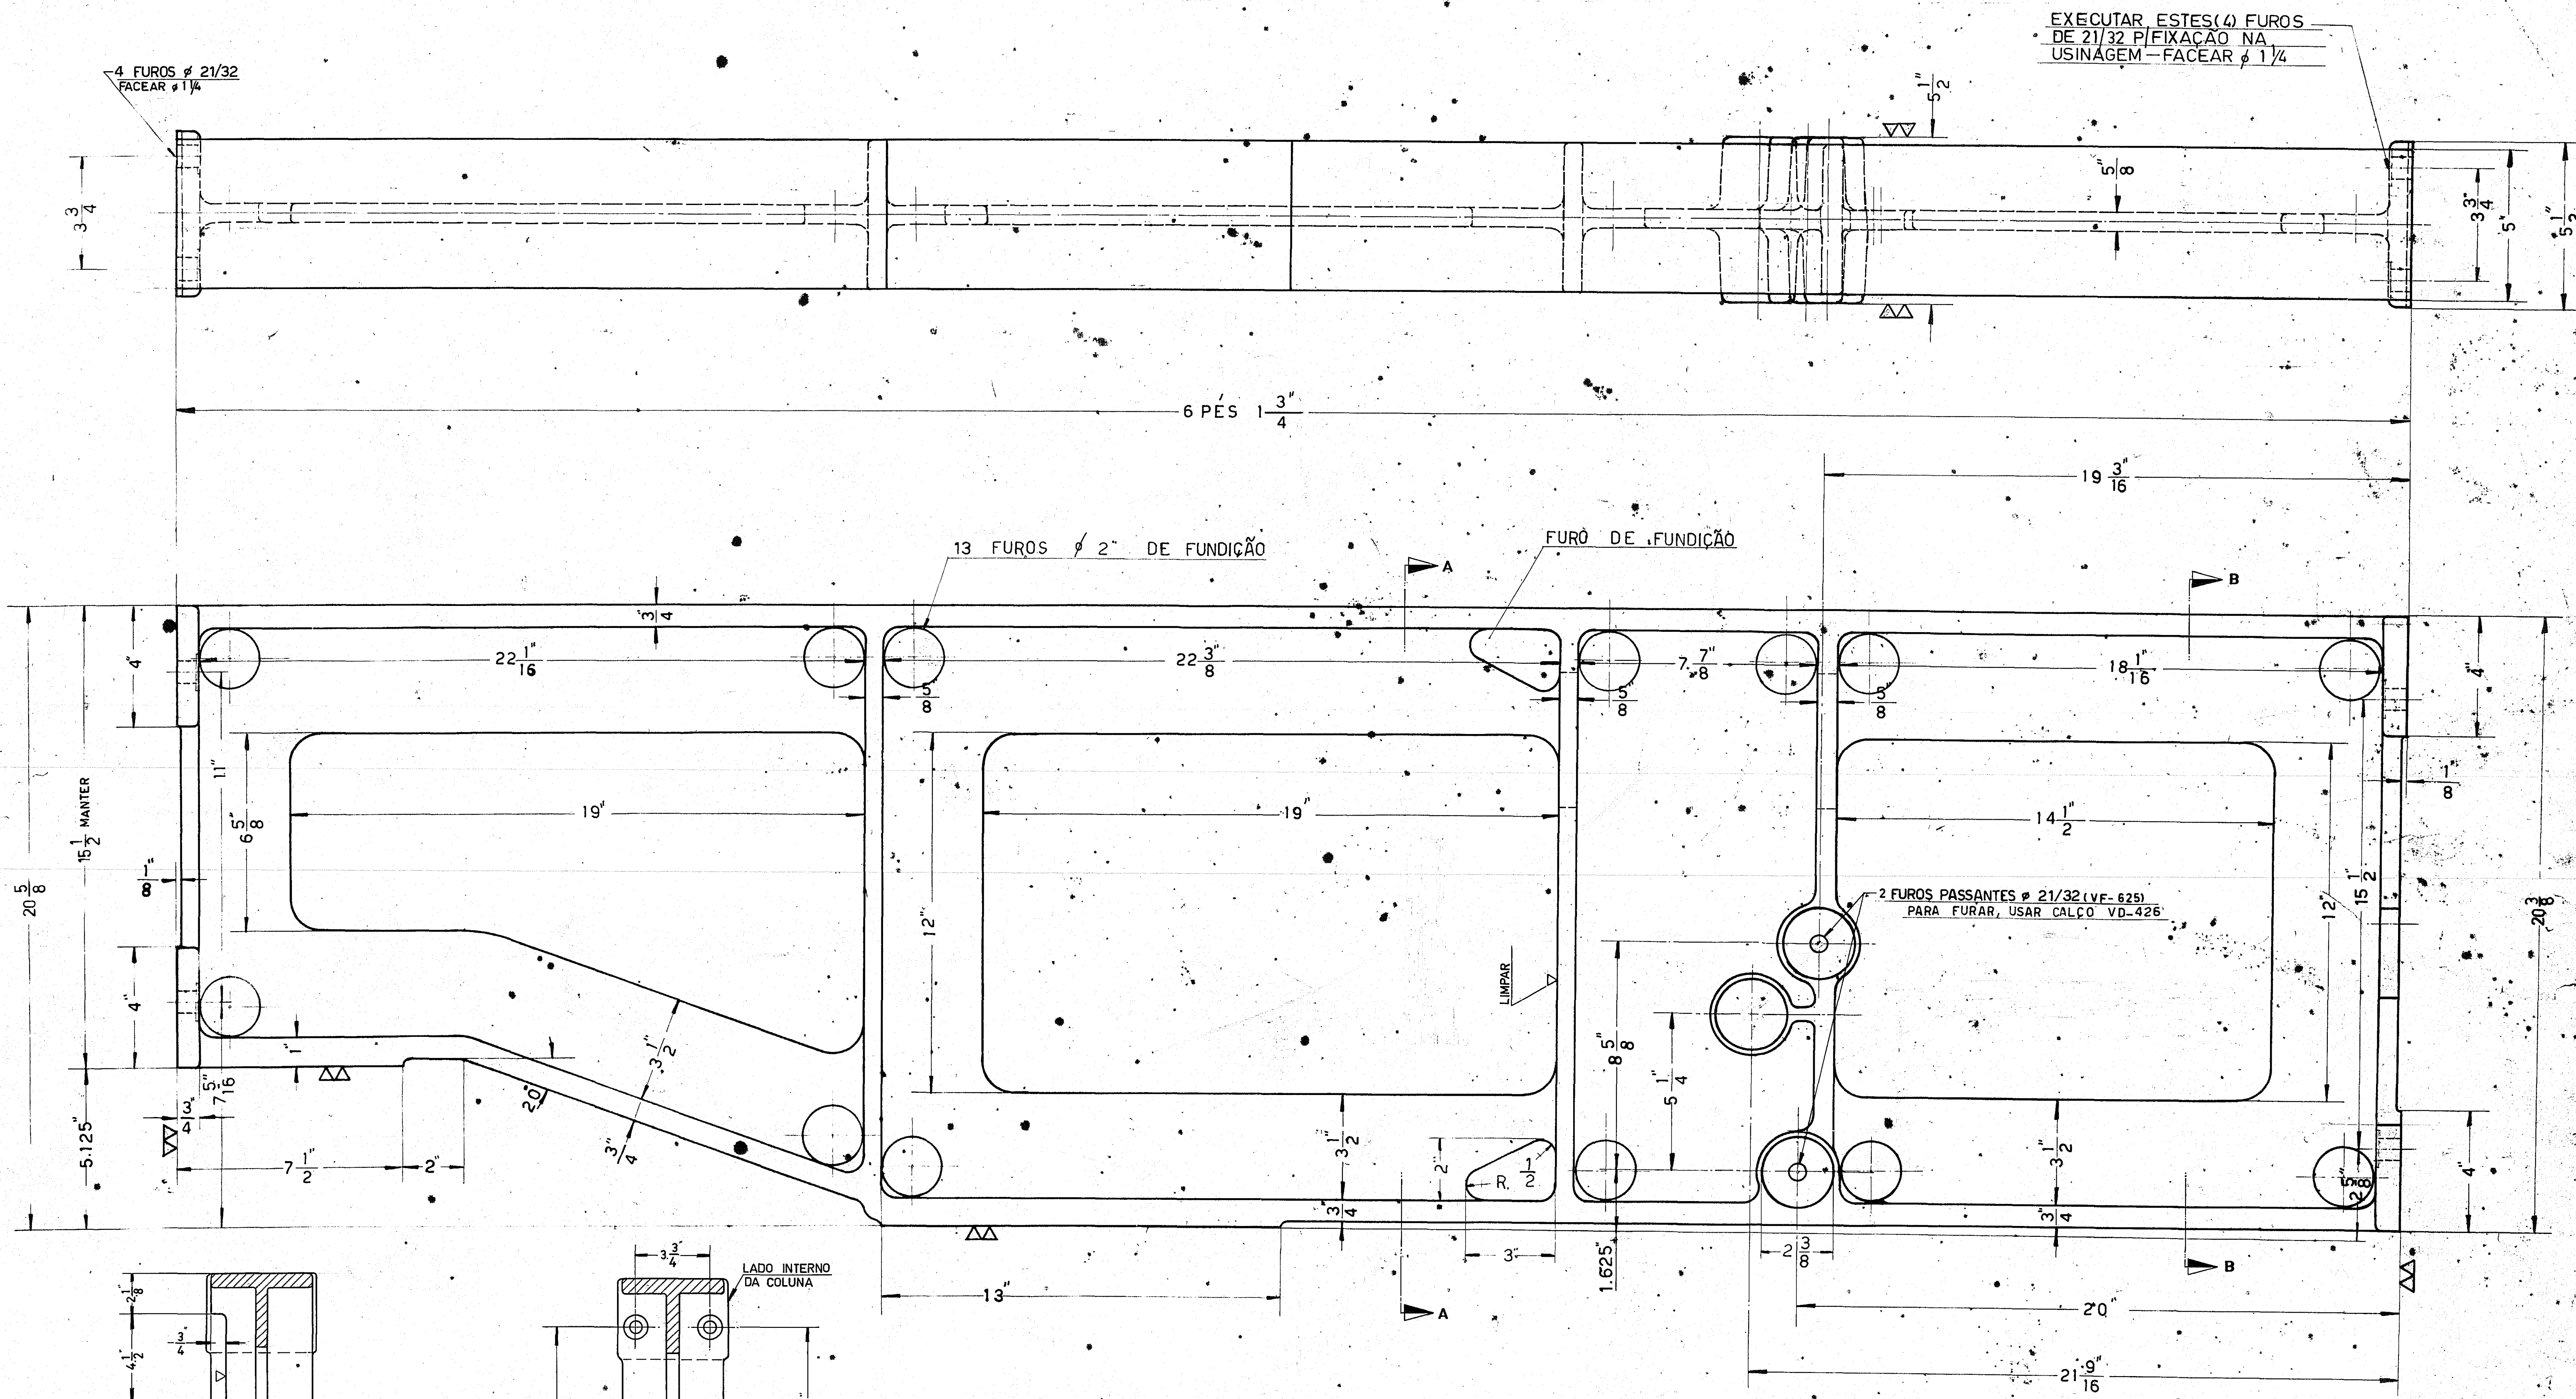

4 FUROS ϕ 21/32
FACEAR ϕ 1 1/4


EXECUTAR ESTES(4) FUROS
DE 21/32 P/FIXAÇÃO NA
USINAGEM - FACEAR ϕ 1 1/4

13 FUROS ϕ 2\" DE FUNDIÇÃO


FURO DE FUNDIÇÃO

2 FUROS PASSANTES ϕ 21/32 (VF-625)
PARA FURAR, USAR CALÇO VD-426

LIMPAR

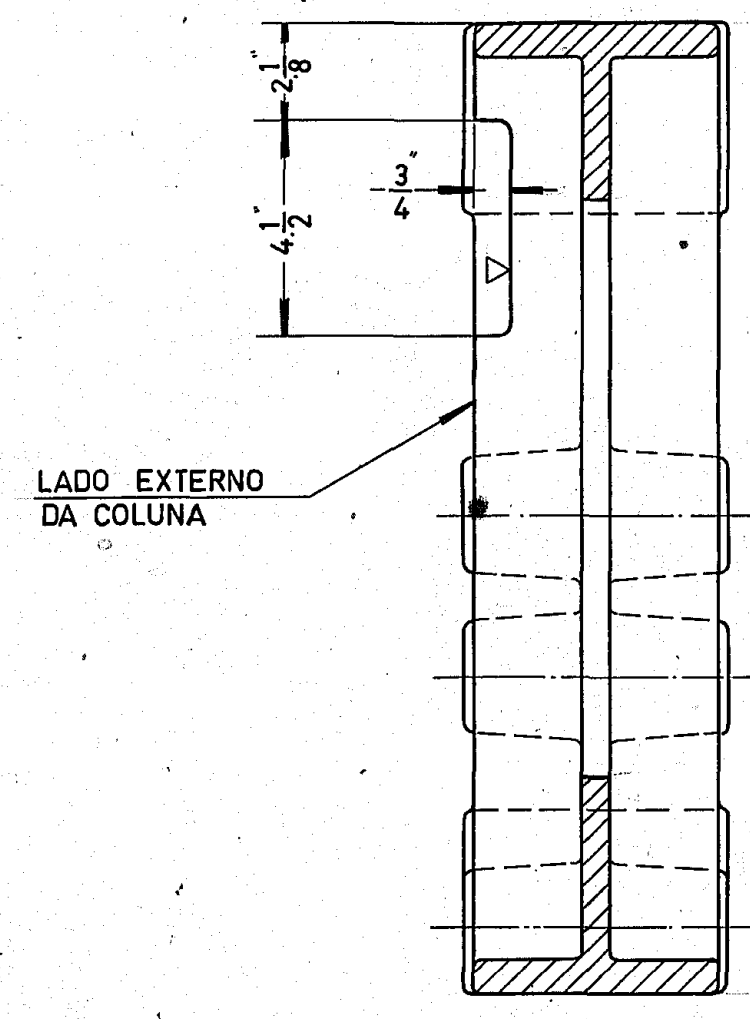

SEÇÃO-AA
ESC. 1/4

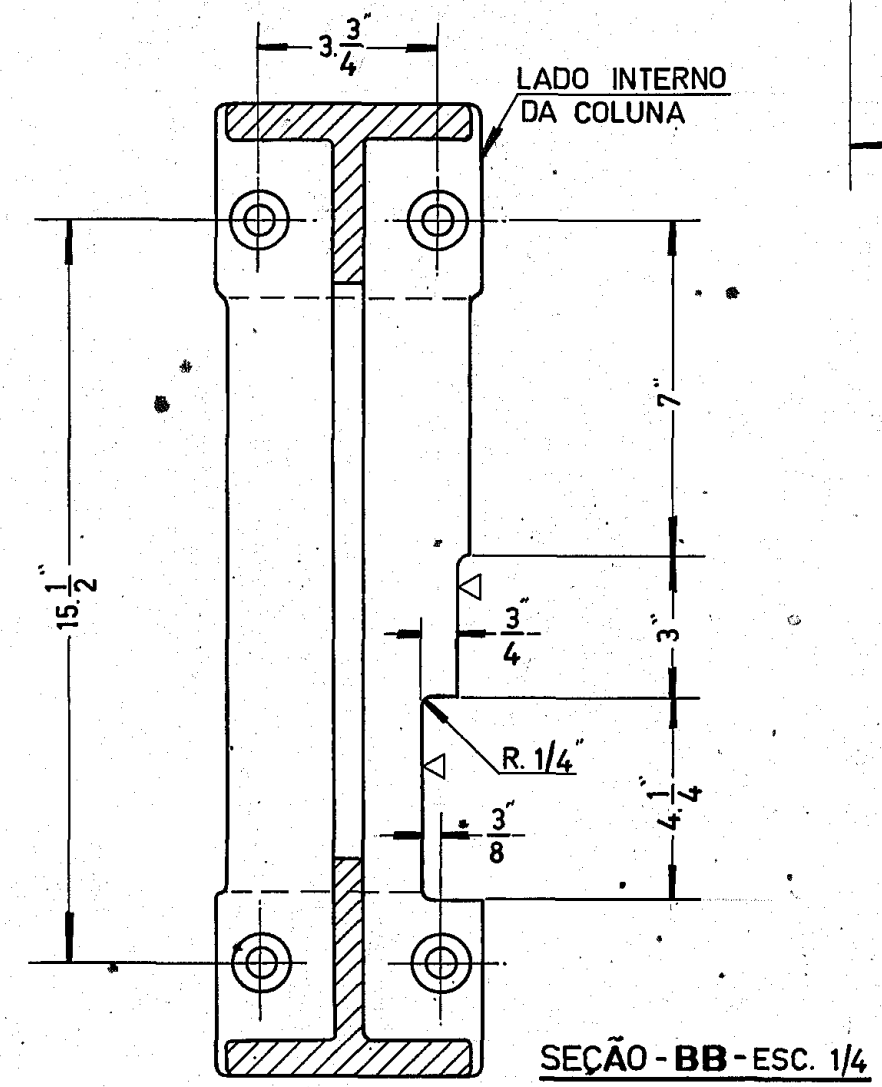

SEÇÃO-BB-ESC. 1/4

SISTEMA MODULAR

USAR PEÇA FUND. EM BRUTO Nº 191-2076

CONJ. 191-5676
VUM. 202
VUM. 362

Ser.	1	21-02-85
Pag.	15	
Mat.	FERRO FUND. CINZENTO	
Condição	DELIVERY SYSTEM MÁQ. I.S. C/ DISTRIB. DE GOTA	1:3/8
Nome da Peça	COLUNA - LADO: ESQUERDO	VV-1735
Tratam.	Nº 40	
Termo	Desenho	