


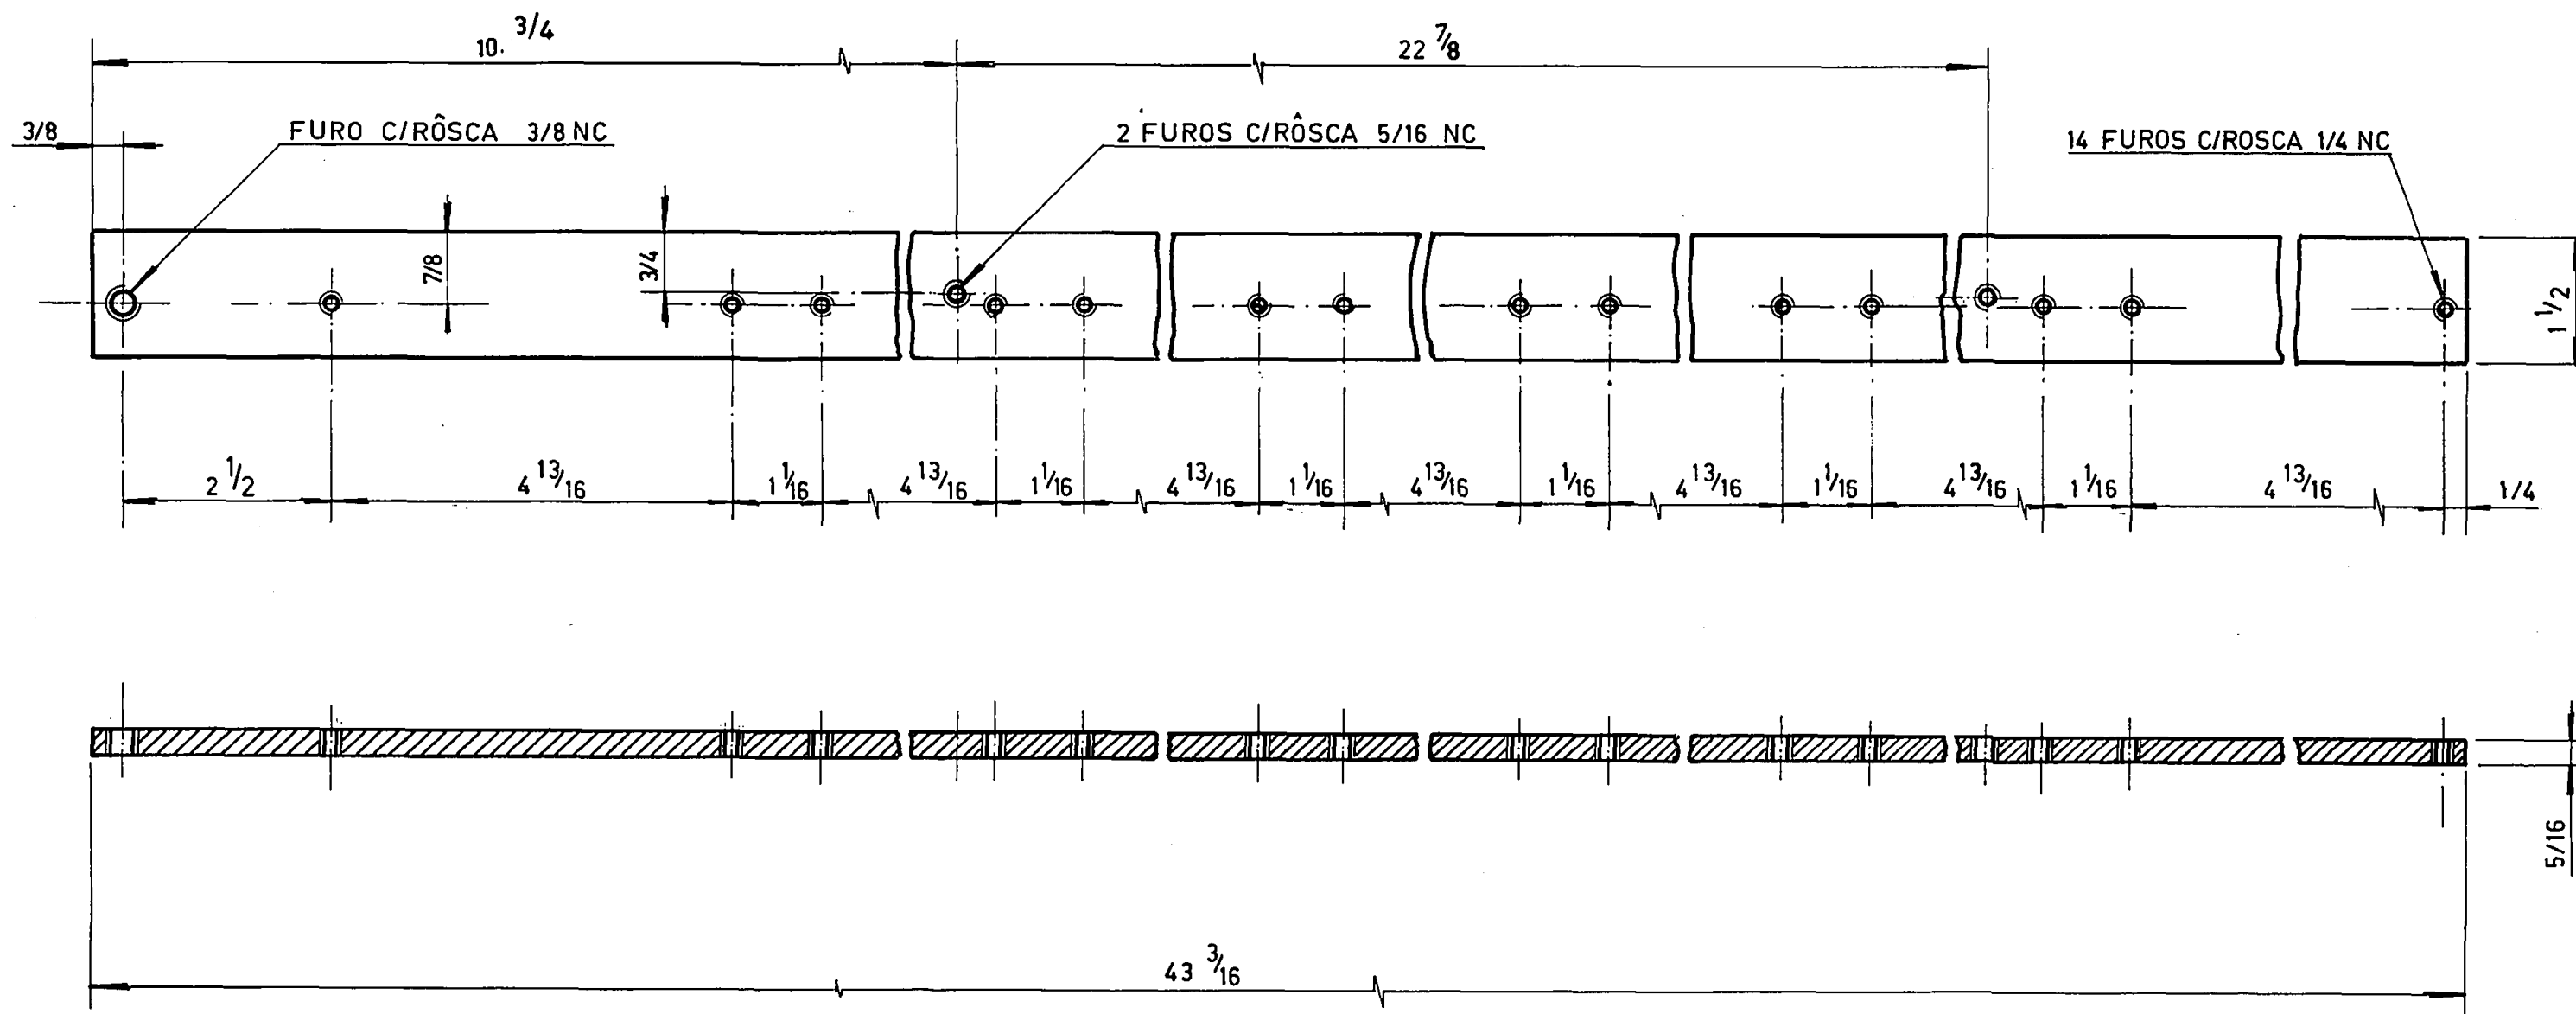

DATA: 05/07/85		VIDROS VITON LTDA.	
TOLERÂNCIAS INDICADAS PARA SUPERFÍCIES USINADAS SEM TOLERÂNCIA INDICADA		FERRO CHATO $5/16 \times 1 \frac{1}{2}$	
DECIMAL ± 0.05		ESQUEMA DOS PAINÉIS DE LUBRIFICAÇÃO (MAQ. I.S. 8 SEC)	
FRAÇÃO		VVL-114	
DE 0" ATE 5" $\pm 1/32$		SOPORTE DOS INJETORES	
DE 5" ATE 24" $\pm 1/32$		VV-1789	
ACIMA DE 24" $\pm 1/16$		ESCALA: 1/2	