


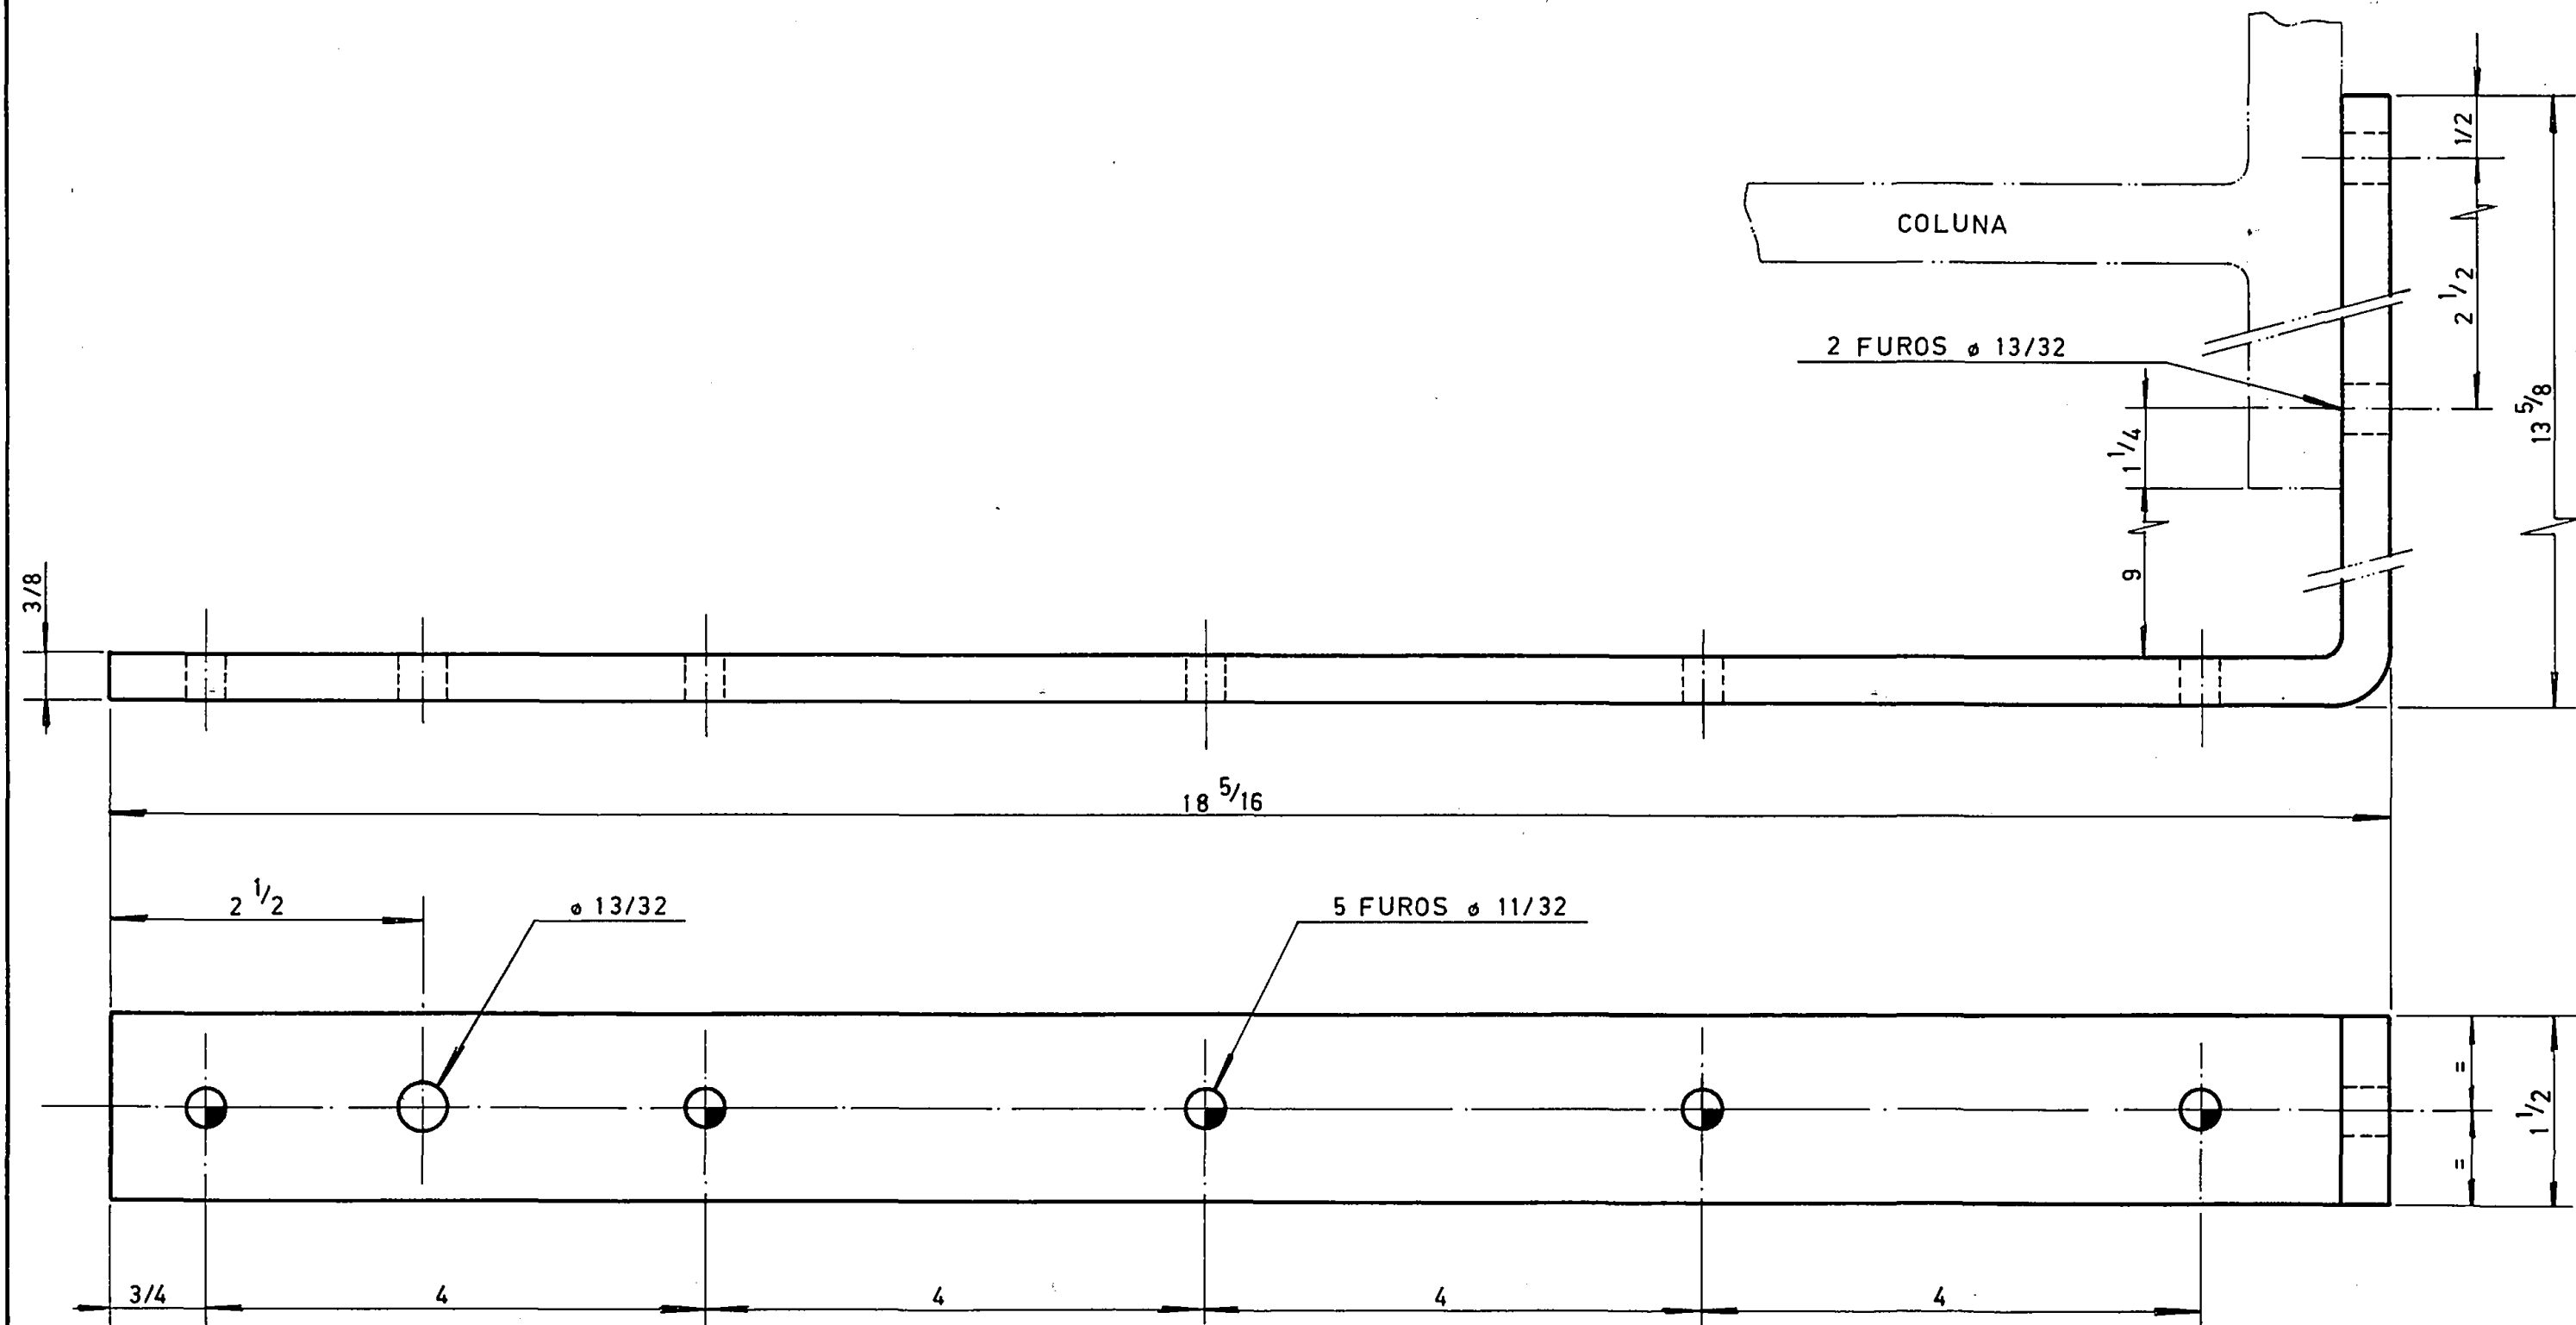

DATA	VER	L	DATA 29-5-85		VIDROS VITON LTDA.		DES. <i>[Signature]</i>
			TOLERANCIAS STANDARD PARA SUPERFICIES USINADAS SEM TOLERANCIA INDICADA		MAT. FERRO CHATO 3/8 x 1 1/2		VER. <i>[Signature]</i>
DATA	VER	L	DE 0" A 5" ± 1/64 DE 5" A 24" ± 1/32 ACIMA DE 24" ± 1/16		ESQUEMA DOS PAINELIS DE LUBRIFICAÇÃO		N.º DO PROJ. VVL-114
			F. ROÇÃO		SUORTE		N.º DA PEÇA VV-1790
					TRAT. TERM.	ESCALA 3/4	N.º DO DES.