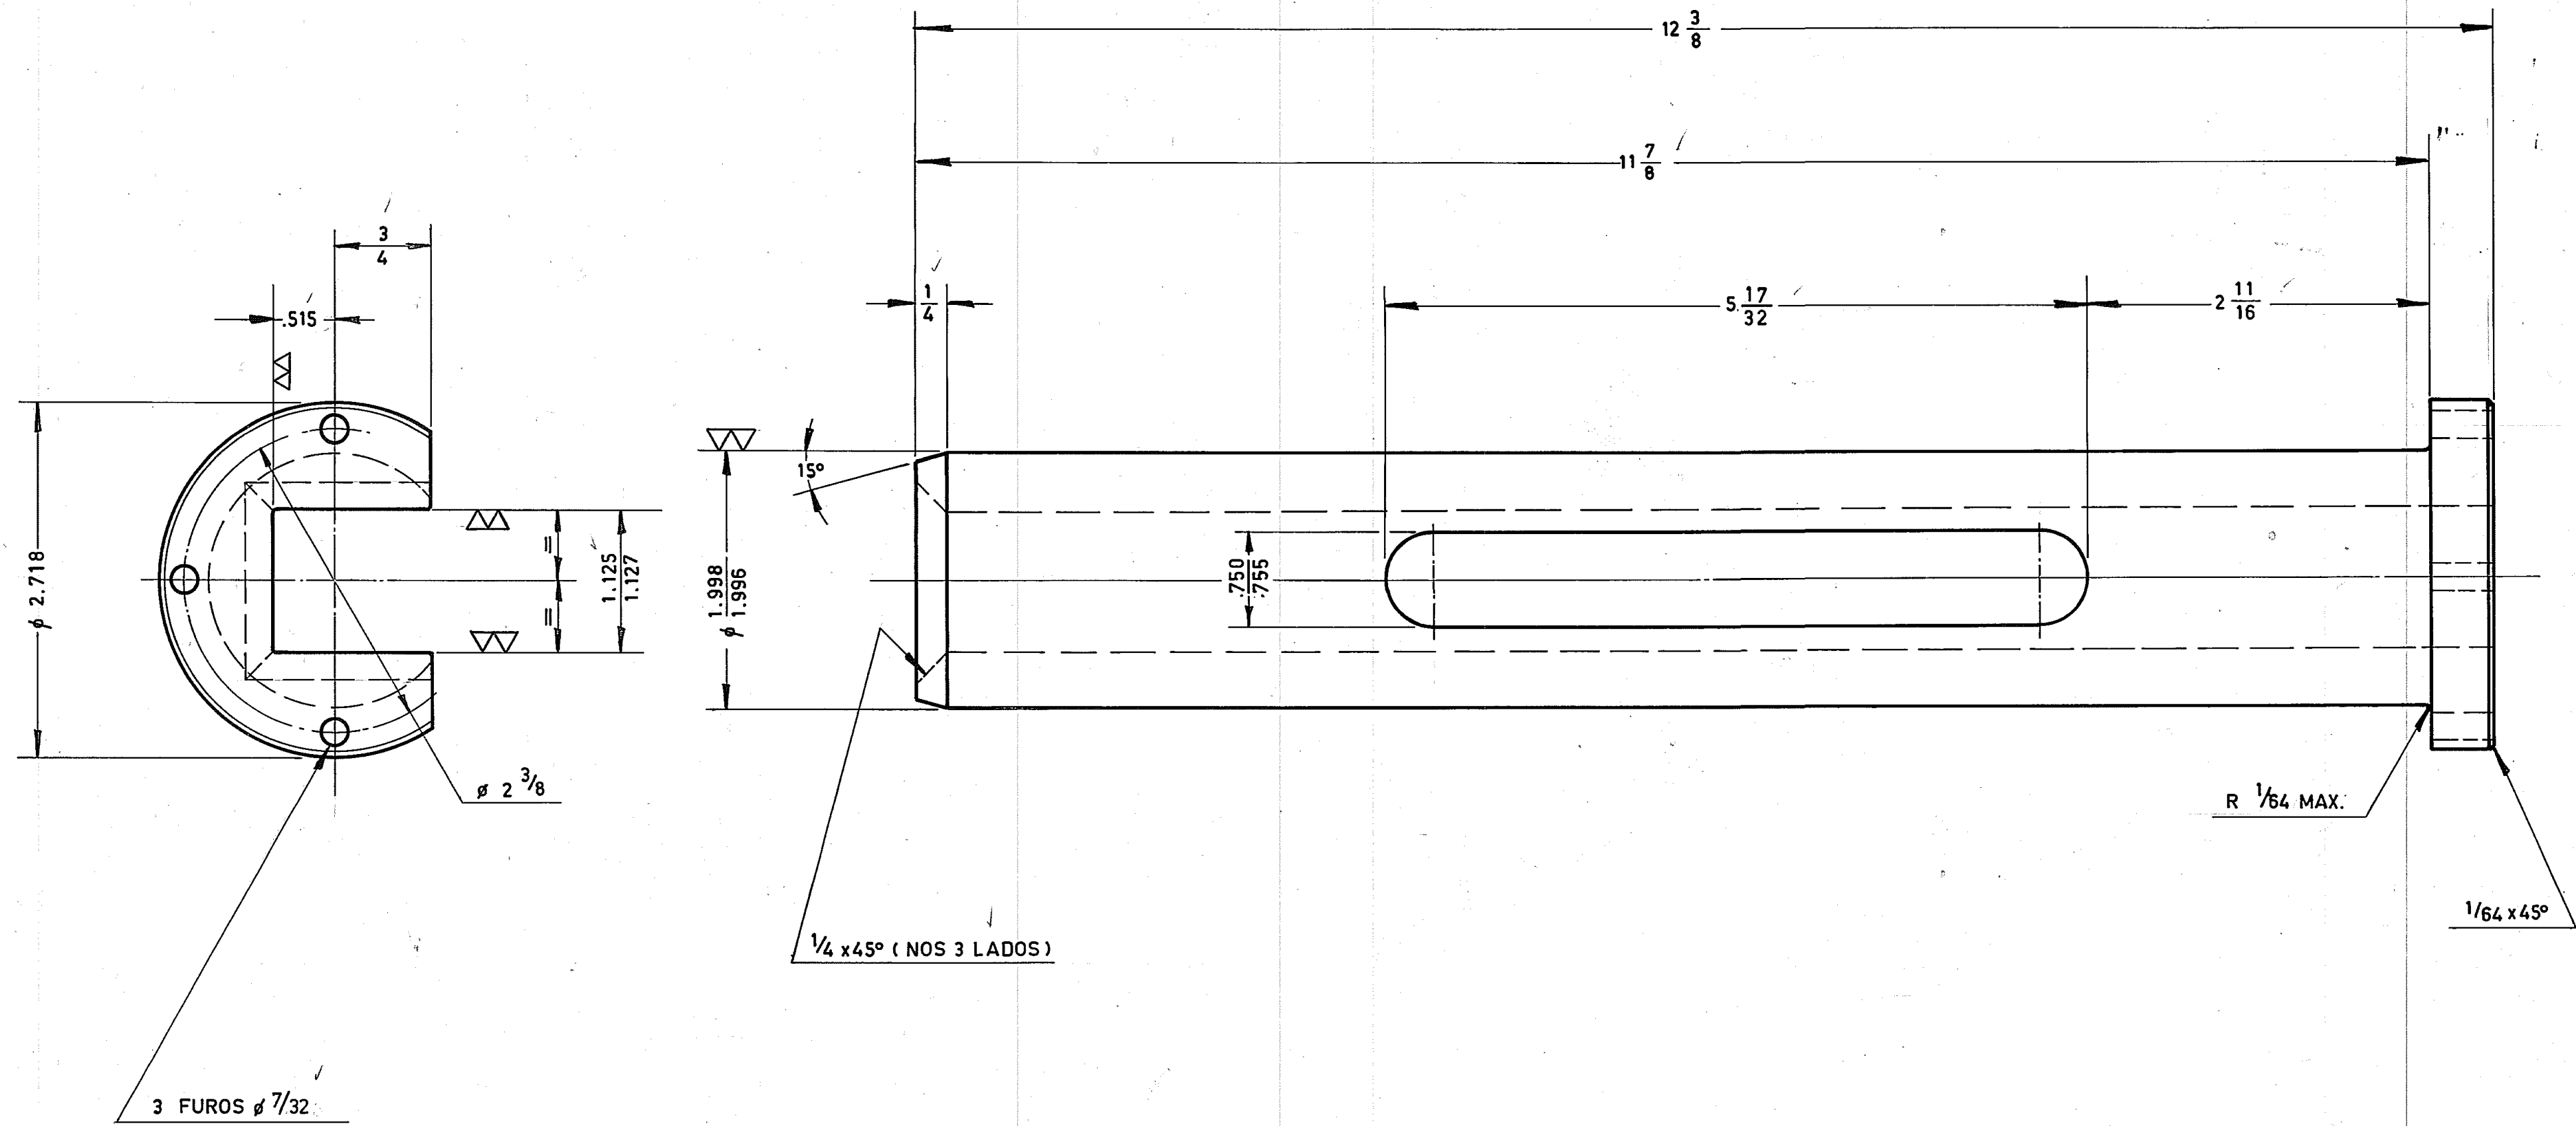


DATA	REVISÃO	ITEM	DATA 28-11-85	DES. <i>Francisco</i>
			TOLERÂNCIAS PARA SUPERFÍCIES USINADAS SEM TOLERÂNCIA INDICADA	VER. <i>00000</i>
			DE 0" A 5" ± 1/64	APR. <i>00000</i>
			DE 5" A 24" ± 1/32	N.º DO PROJ. VVM-310
			ACIMA DE 24" ± 1/16	N.º DA PEÇA VV-1923
			FRACÇÃO	TRAT. TERM.
			DE 0" A 5" ± 1/64	ESCALA 1:1
			DE 5" A 24" ± 1/32	N.º DO DES.
			ACIMA DE 24" ± 1/16	