


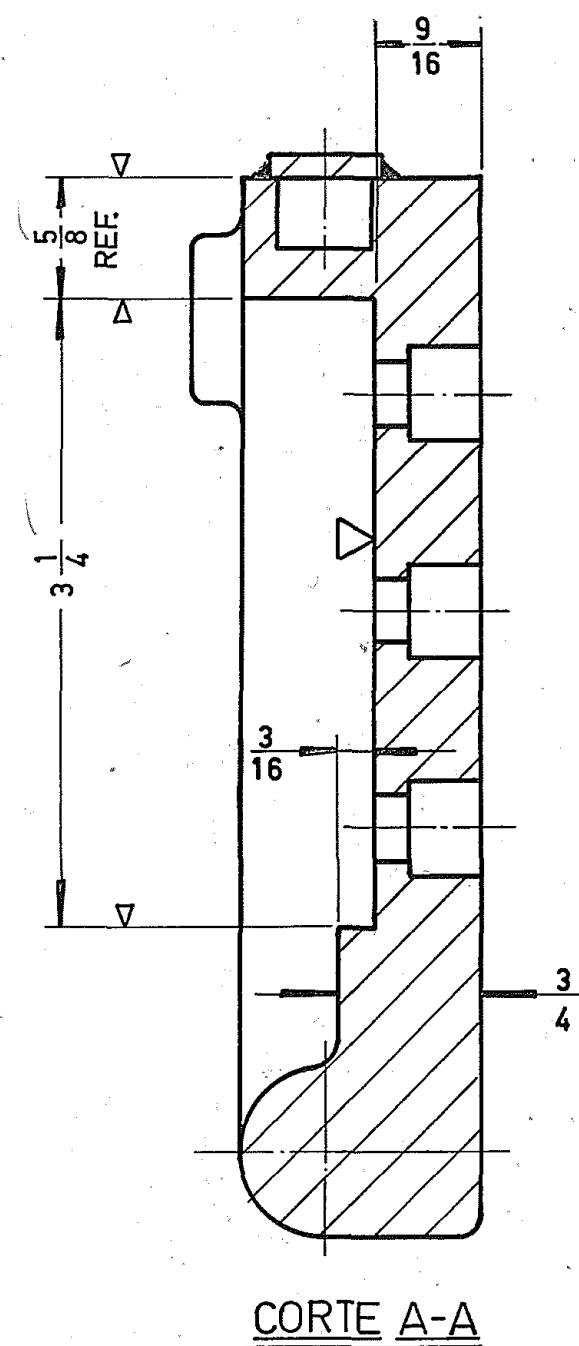


FUNDIR EM ALTO RELEVO
C/ TIPO 1/4 N° VV-1934

2 FUROS $\phi 7/16 \times 3/4$ PROF.
C/ RÔSCA 1/4 NPT-18 FPP


2 FUROS $\phi 7/16 \times 4 3/4$ PROF.

SOLDAR
A PROVA D' ÁGUA

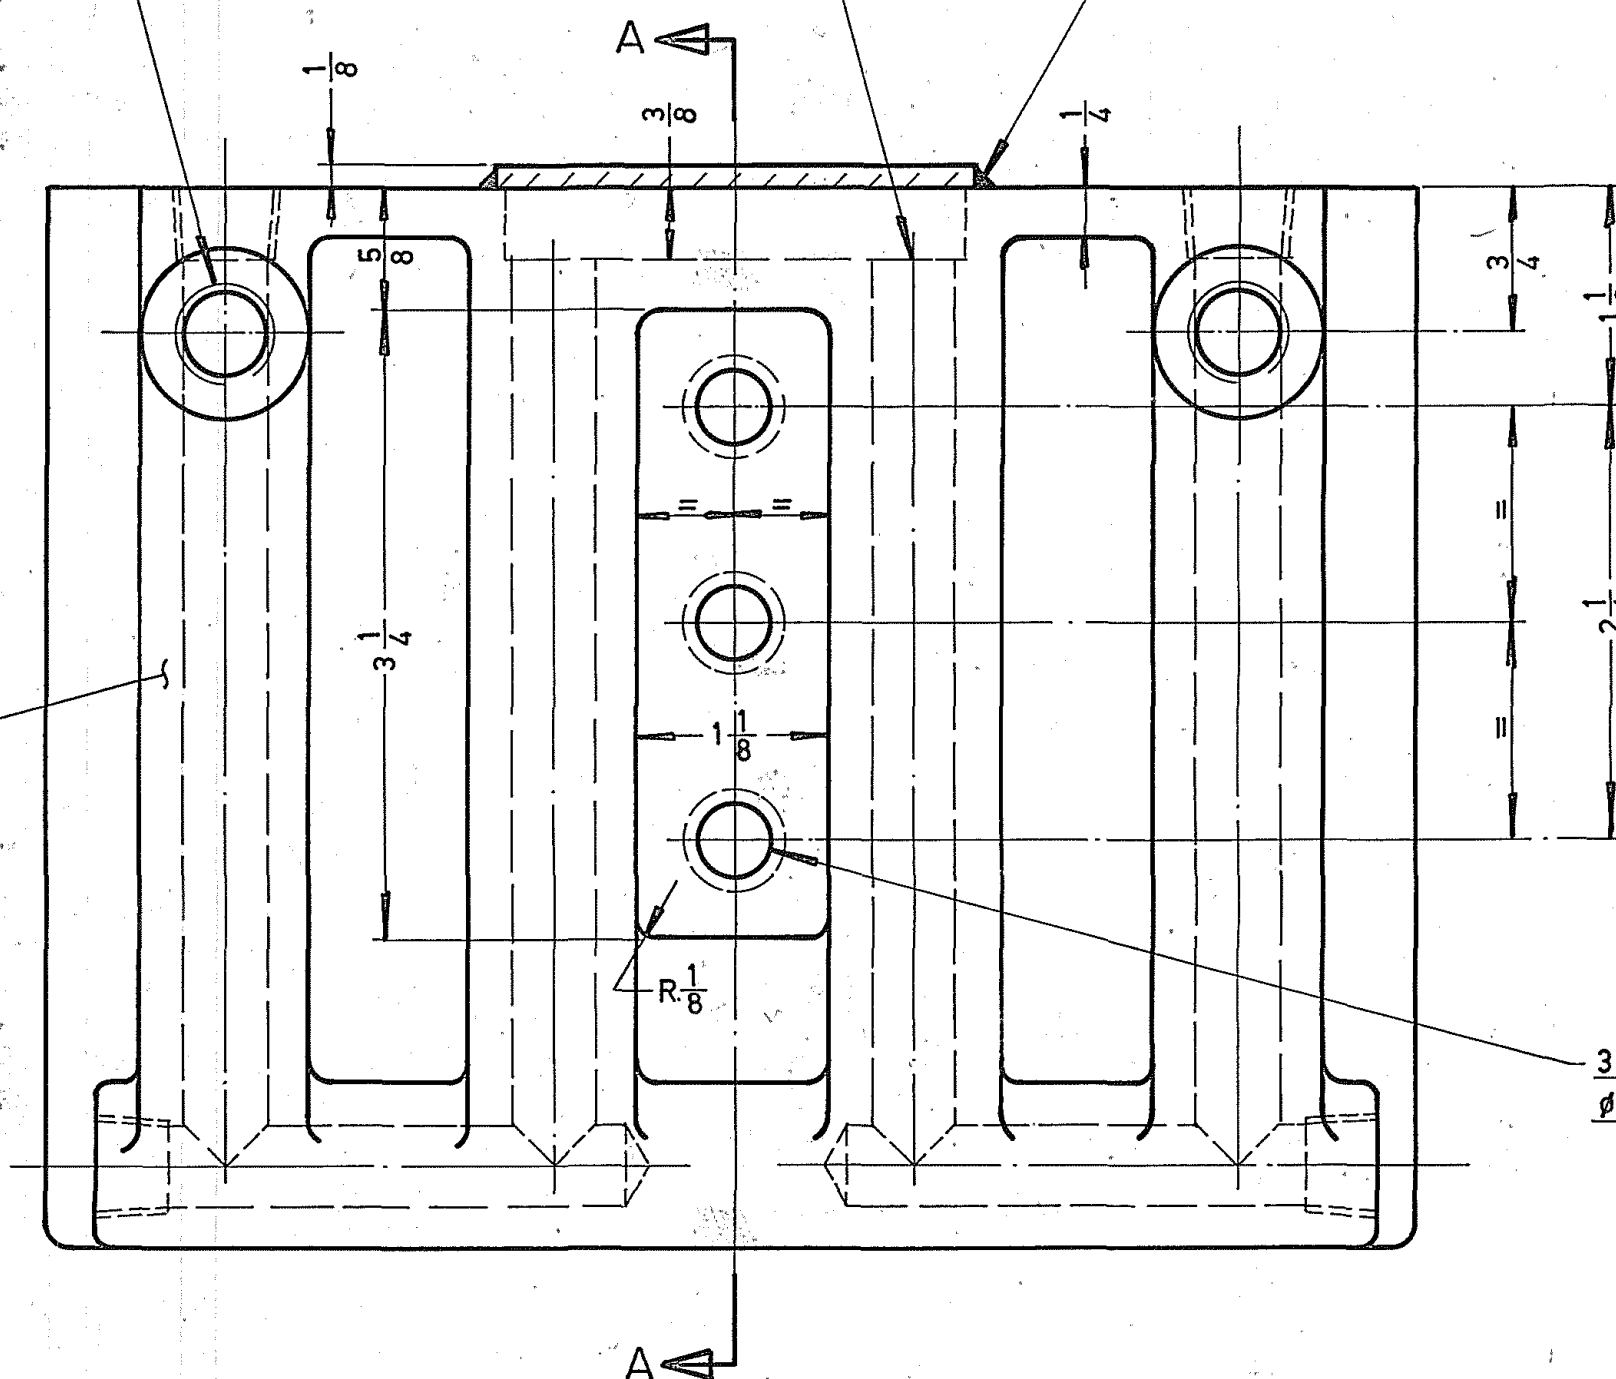


3 FUROS $\phi 11/32$ C/ REB.
 $\phi 1/2 \times 11/32$ PROF.


2 FUROS $\phi 7/16 \times 2 3/4$ PROF.
C/ RÔSCA 1/4 NPT-18 FPP

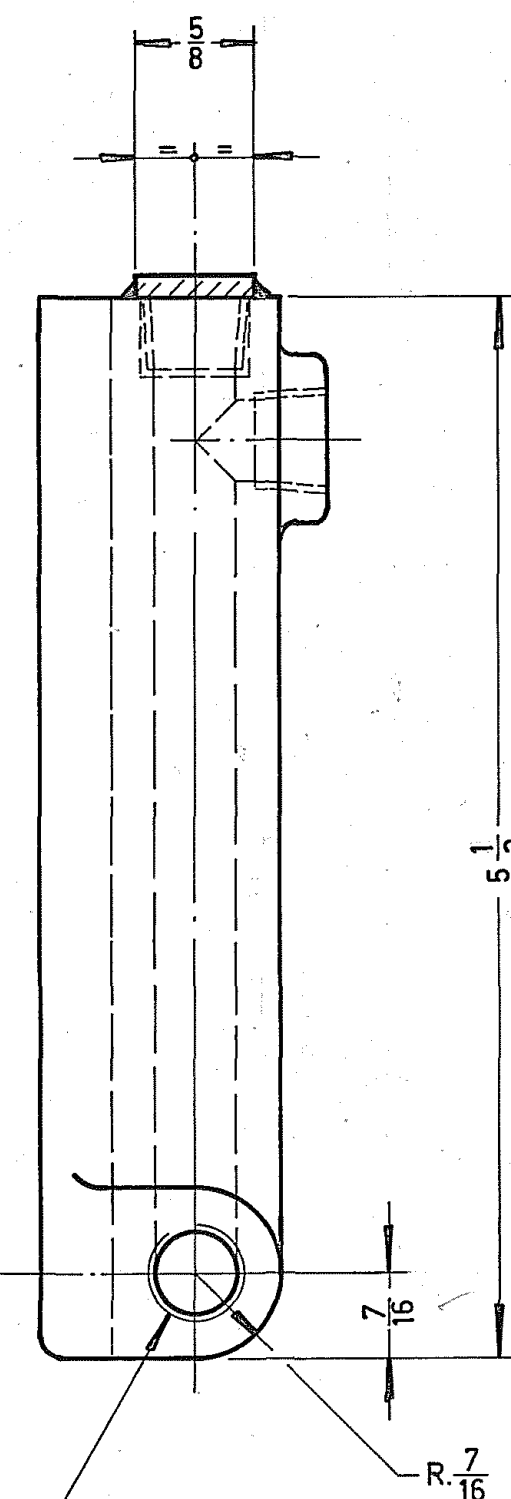

2 FUROS $\phi 7/16 \times 5 1/8$ PROF.
C/ RÔSCA 1/4 NPT-18 FPP

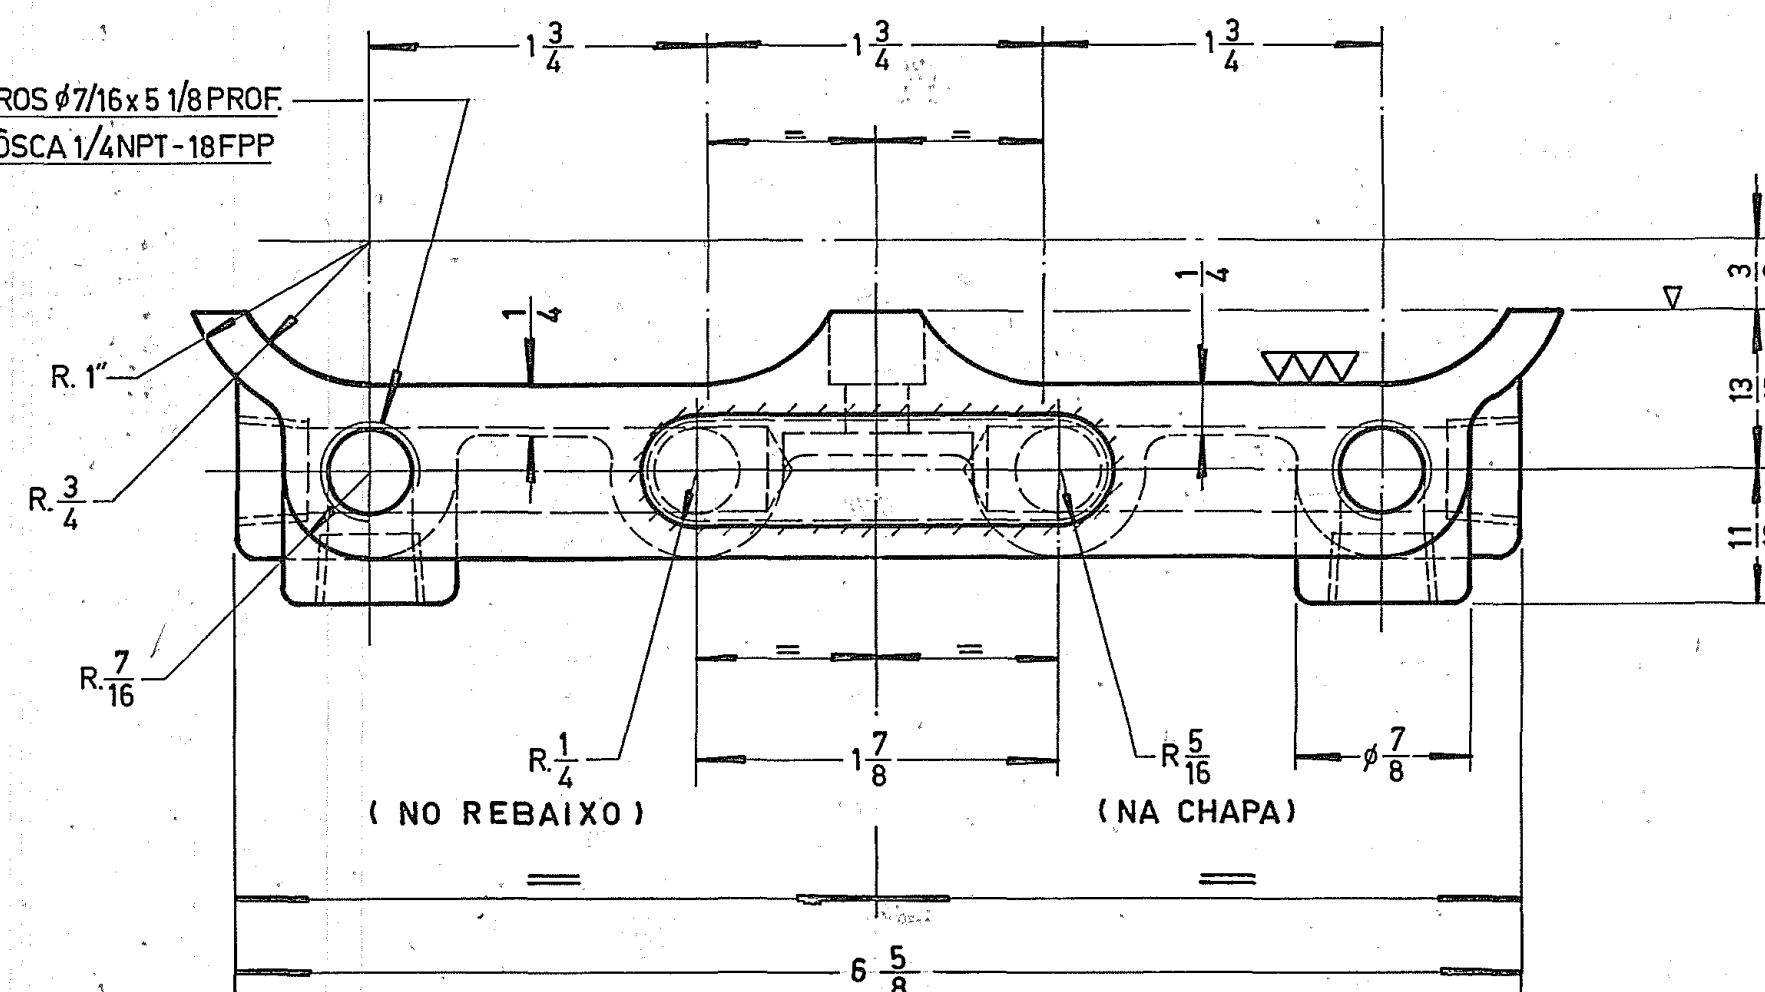

NOTA! RAIOS DE FUNDIÇÃO NÃO COTADOS = 1/8

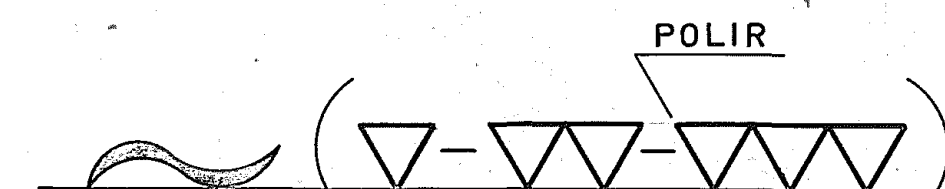

22-6921ERA ALUM. A	DATA	29-01-1986	VIDROS VITON LTDA.		DES. <i>P. P. P.</i>
	REVISÃO	ITEM	ALUMÍNIO FUND. SAE 323 (A)		VER. <i>P. P. P.</i>
	DATA	REVISÃO	INTERCEPTOR DE GOTAS		N.º DO CONJ. VVM-311
	DATA	REVISÃO	GOB GUIDE		N.º DA PEÇA VV-1934
TOLERÂNCIAS PARA SUPERFÍCIES USINADAS SEM TOL. INDICADA			ESCALA 1:1		N.º DO DES.
DE 0" A 1" $\pm 1/64$					
DE 1" A 2" $\pm 1/32$					
ACIMA DE 2" $\pm 1/16$					