


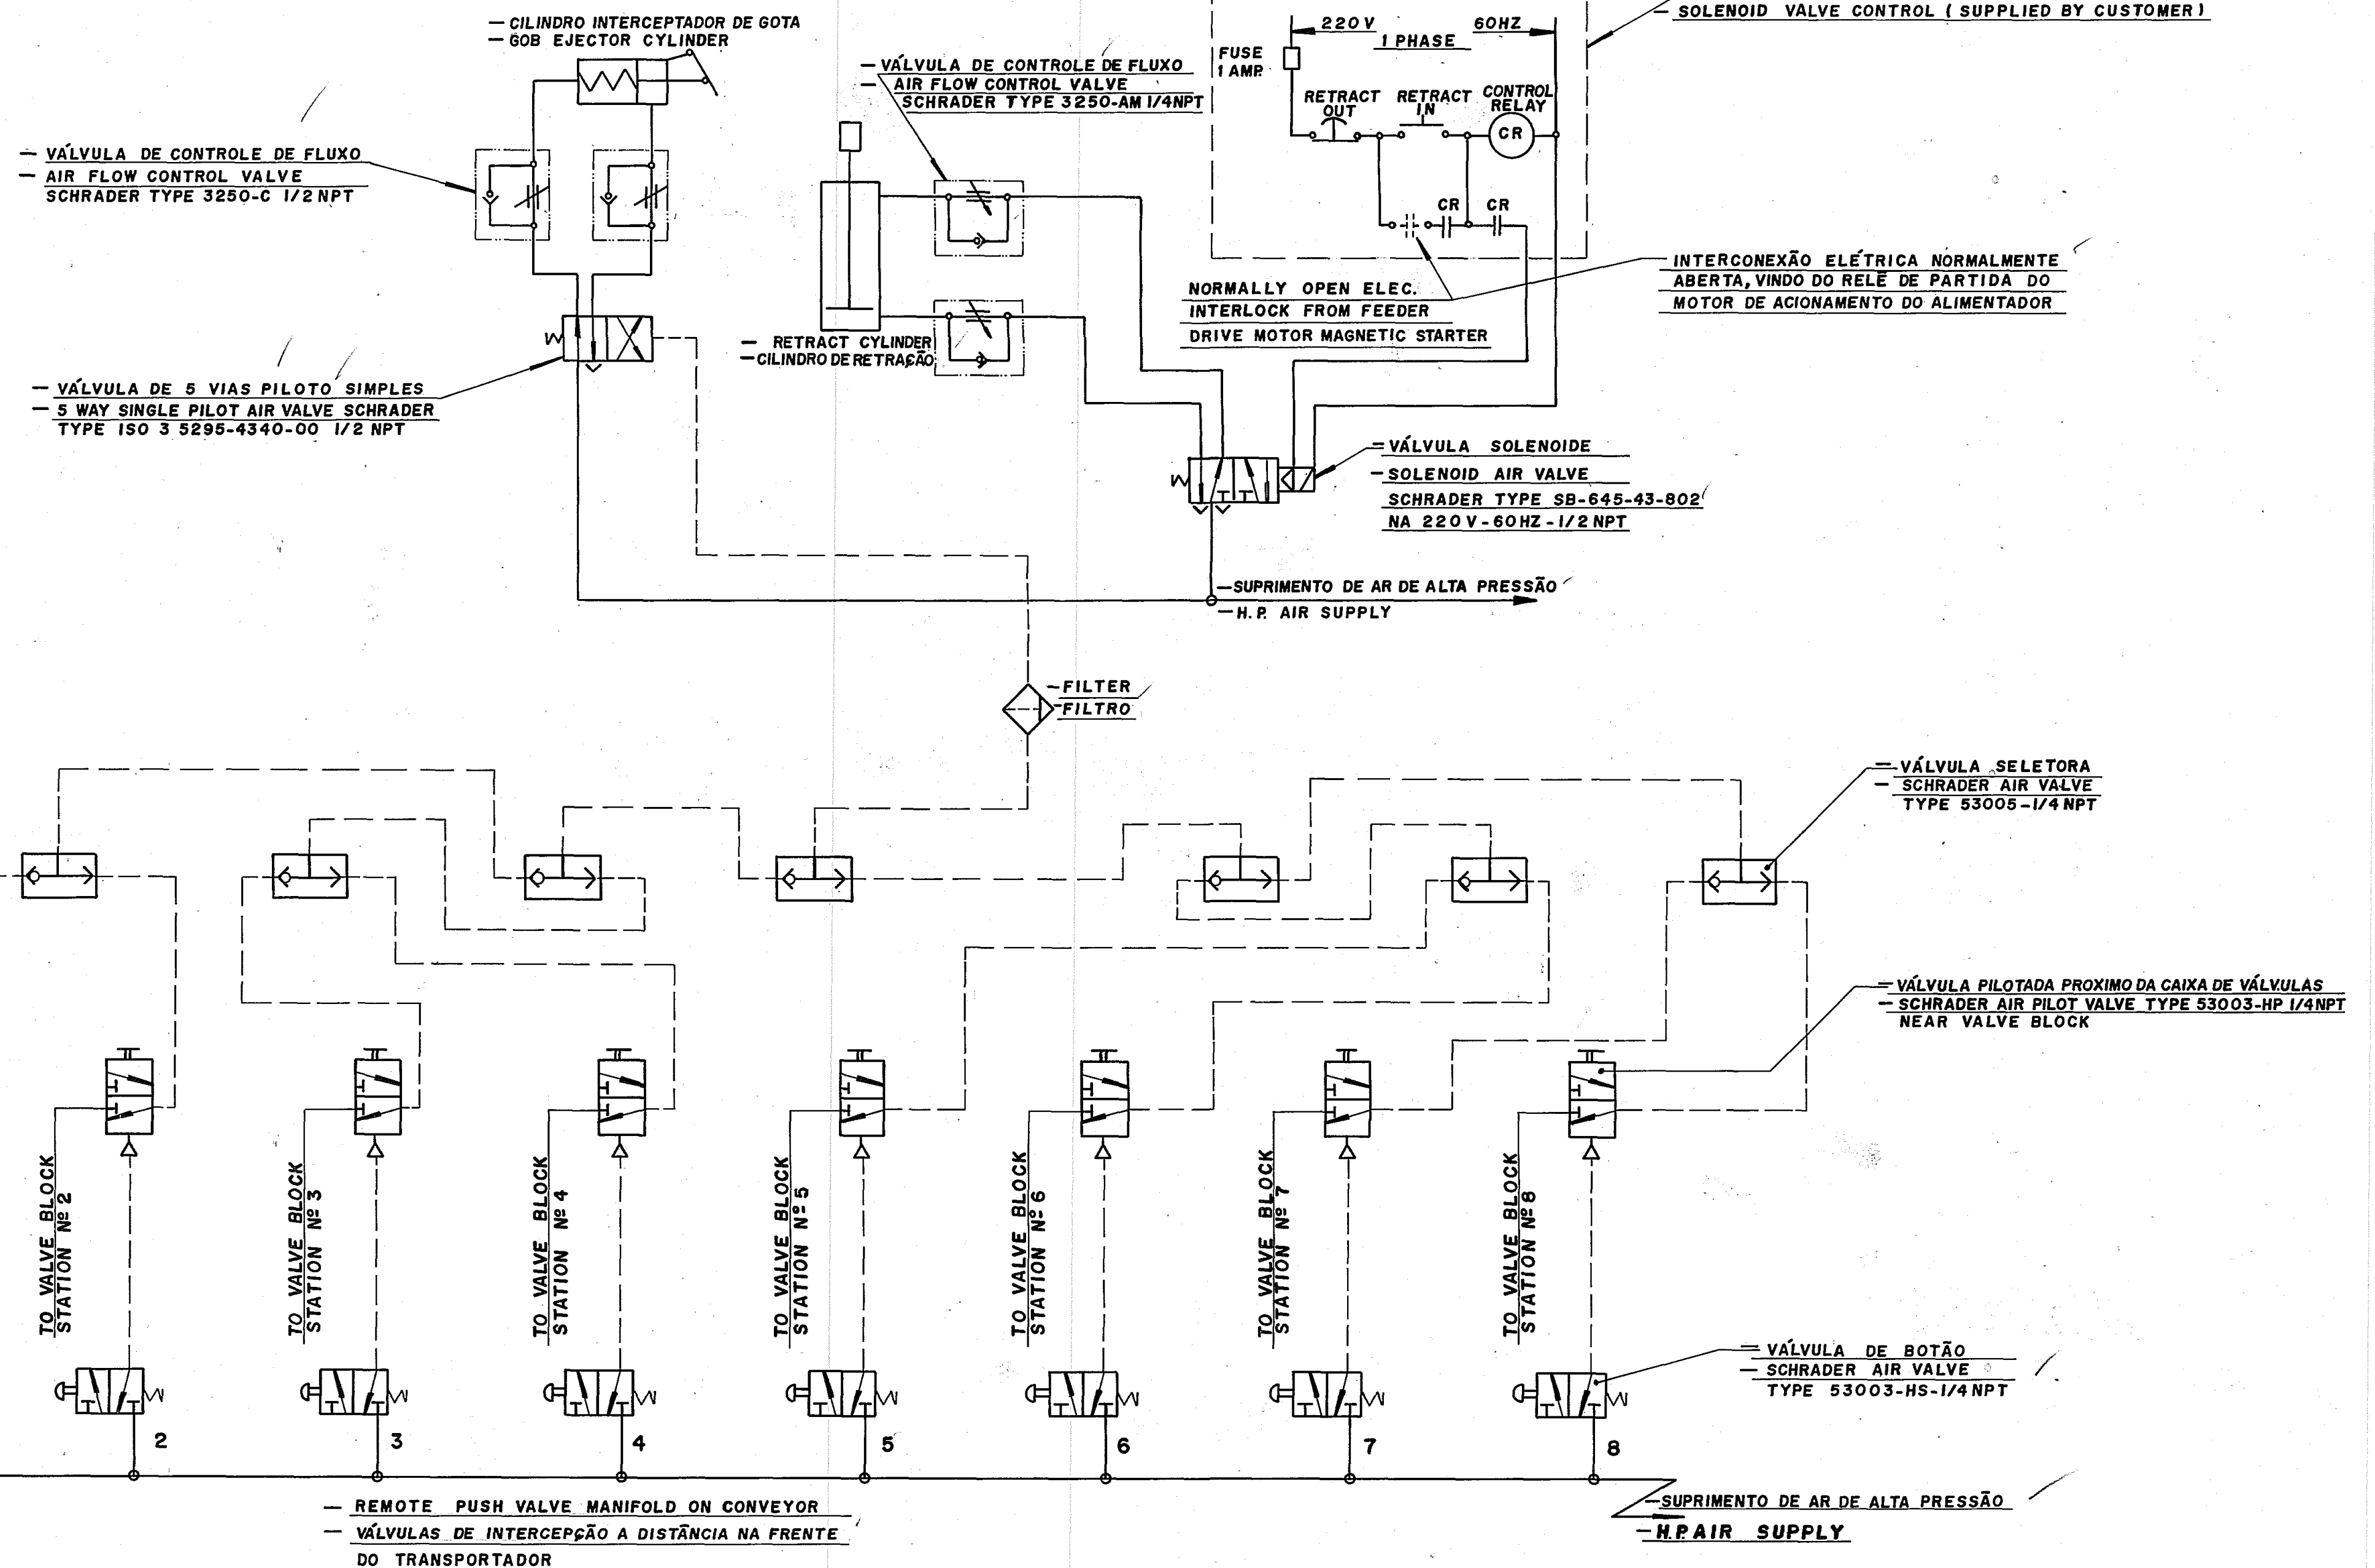

23-05-91	A	REDES.	23-05-91		VITROS VITON LTDA.	
			DIMENSIONES STANDARD PARA SUPERFICIES USADAS SEM TOLERANCIA INDICADA		ENCAN. GERAL DA MAQ. I.S. 8 SEC.	
			DECIMAL ± 0.02"			
			FRAÇÃO			
23-05-91	A	REDES.	DE 0" ATÉ 6" ± 1/32		TRAT. TERM.	ESCALA 1:1
			DE 6" ATÉ 24" ± 1/64			
			ACIMA DE 24" ± 1/16			
						VV-1938