


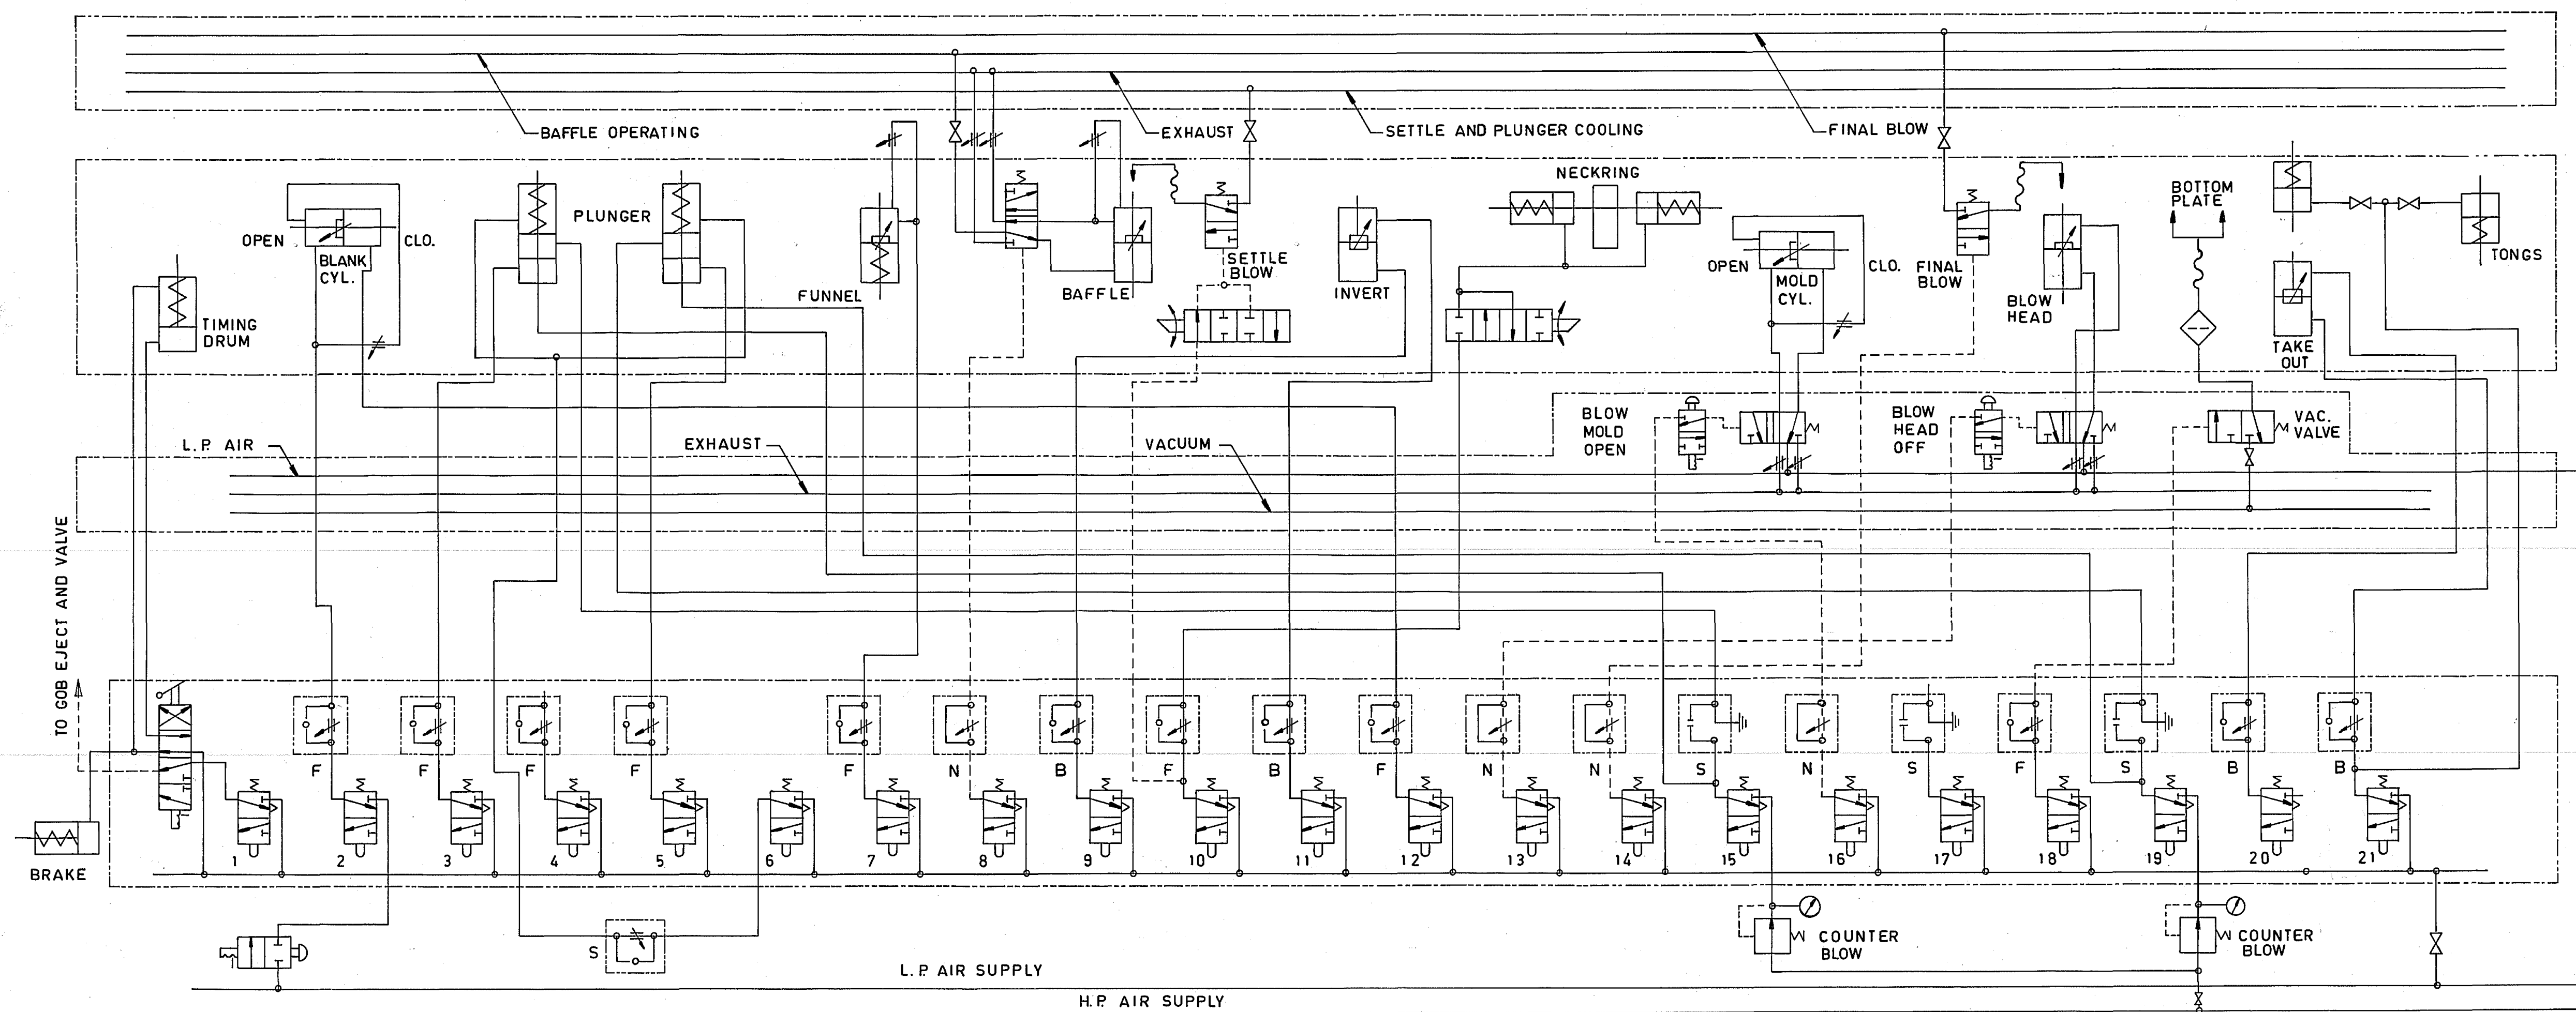

DATA: 13-12-85		VIDROS VITON LTDA.		DES.
REVISÃO	ITEM	TOLERANCIAS STANDARD PARA SUPERFICIES USINADAS SEM TOLERANCIA INDICADA	MAT.	APROV.
		DECIMAL ± 0,05"	N.º DE DOZ.	N.º DO CONJ.
DATA	REVISÃO	FRACAO	NOME SECTION BOX PIPING AND EQUIPMENT DA ARRANGEMENT (FOR BLOW AND PLUNGE OPERATIONS)	N.º DA PEÇA VV-1945
		DE 0" ATE 5" ± 1/64	TRAT.	N.º DO DES.
		DE 5" ATE 24" ± 1/32	TERM.	ESCALA 1:1
		ACIMA DE 24" ± 1/16		