


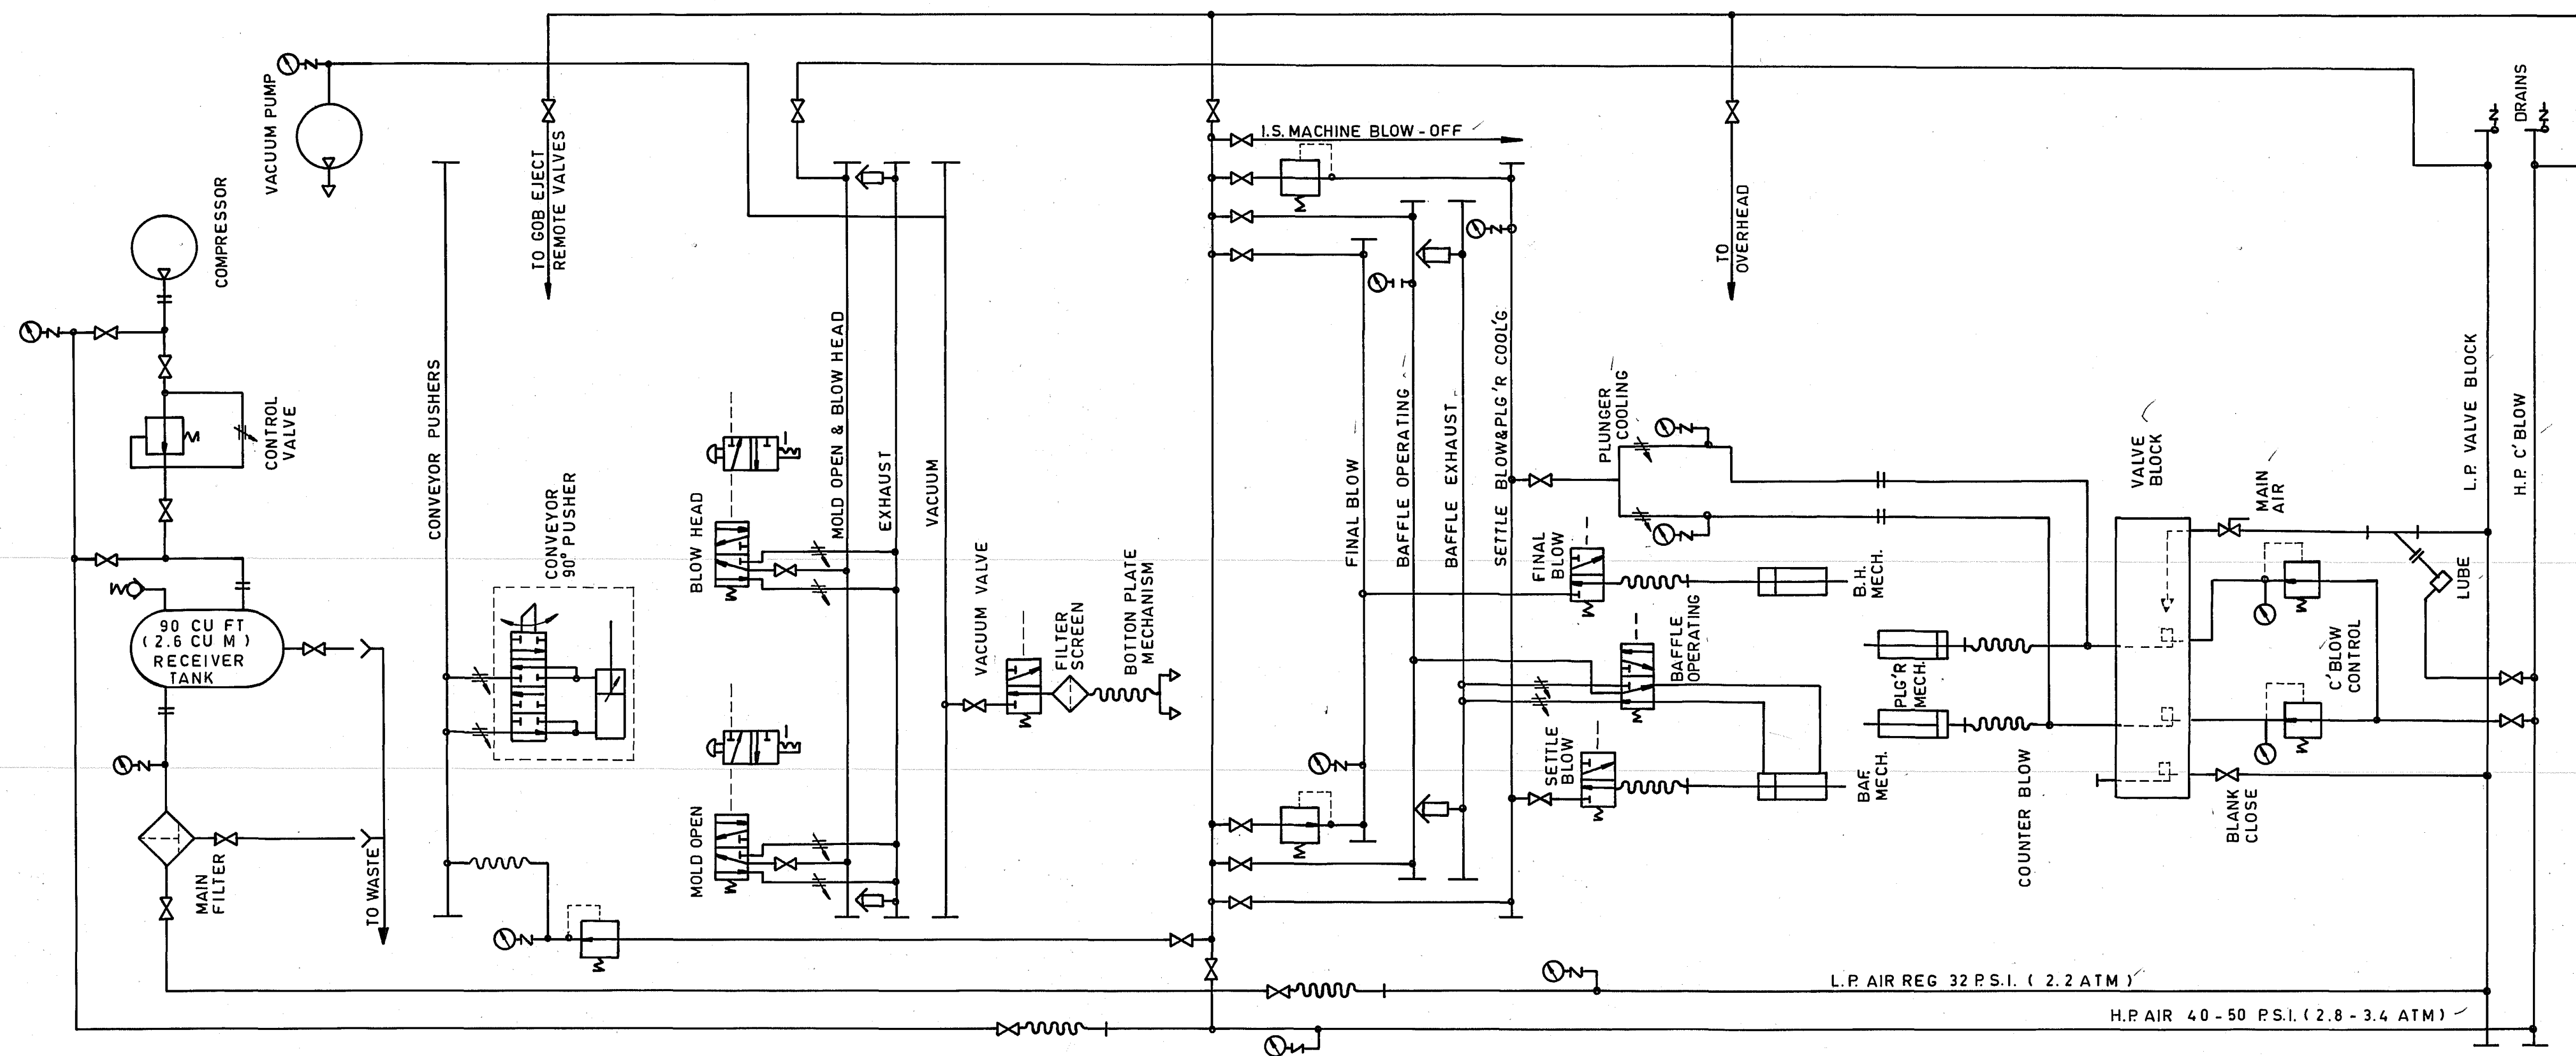

Data: 27-12-85		VIDROS VITON LTDA.		Des. <i>[Signature]</i>
REVISÃO	ITEM	TOLERÂNCIAS STANDARD PARA SUPERFÍCIES USINADAS SEM TOLERÂNCIA INDICADA	Mat.	APROV.
DATA	REVISÃO	DECIMAL ± 0.05"	ENCANAMENTO GERAL DA MAQ. I.S. 8 SEÇÕES	N.º DO PROJ.
FRACAO	DE 0" ATE 5" ± 1/64	DE 5" ATE 24" ± 1/32	ACIMA DE 24" ± 1/16	N.º DA PEÇA
NOTA	SUPPLY AND PROCESS AIR PIPING (TYPICAL EQUIPMENT ARRANGEMENT FOR ONE SECTION)			PEÇA VV-1946
TERM.	ESCALA	N.º DO DES.		