


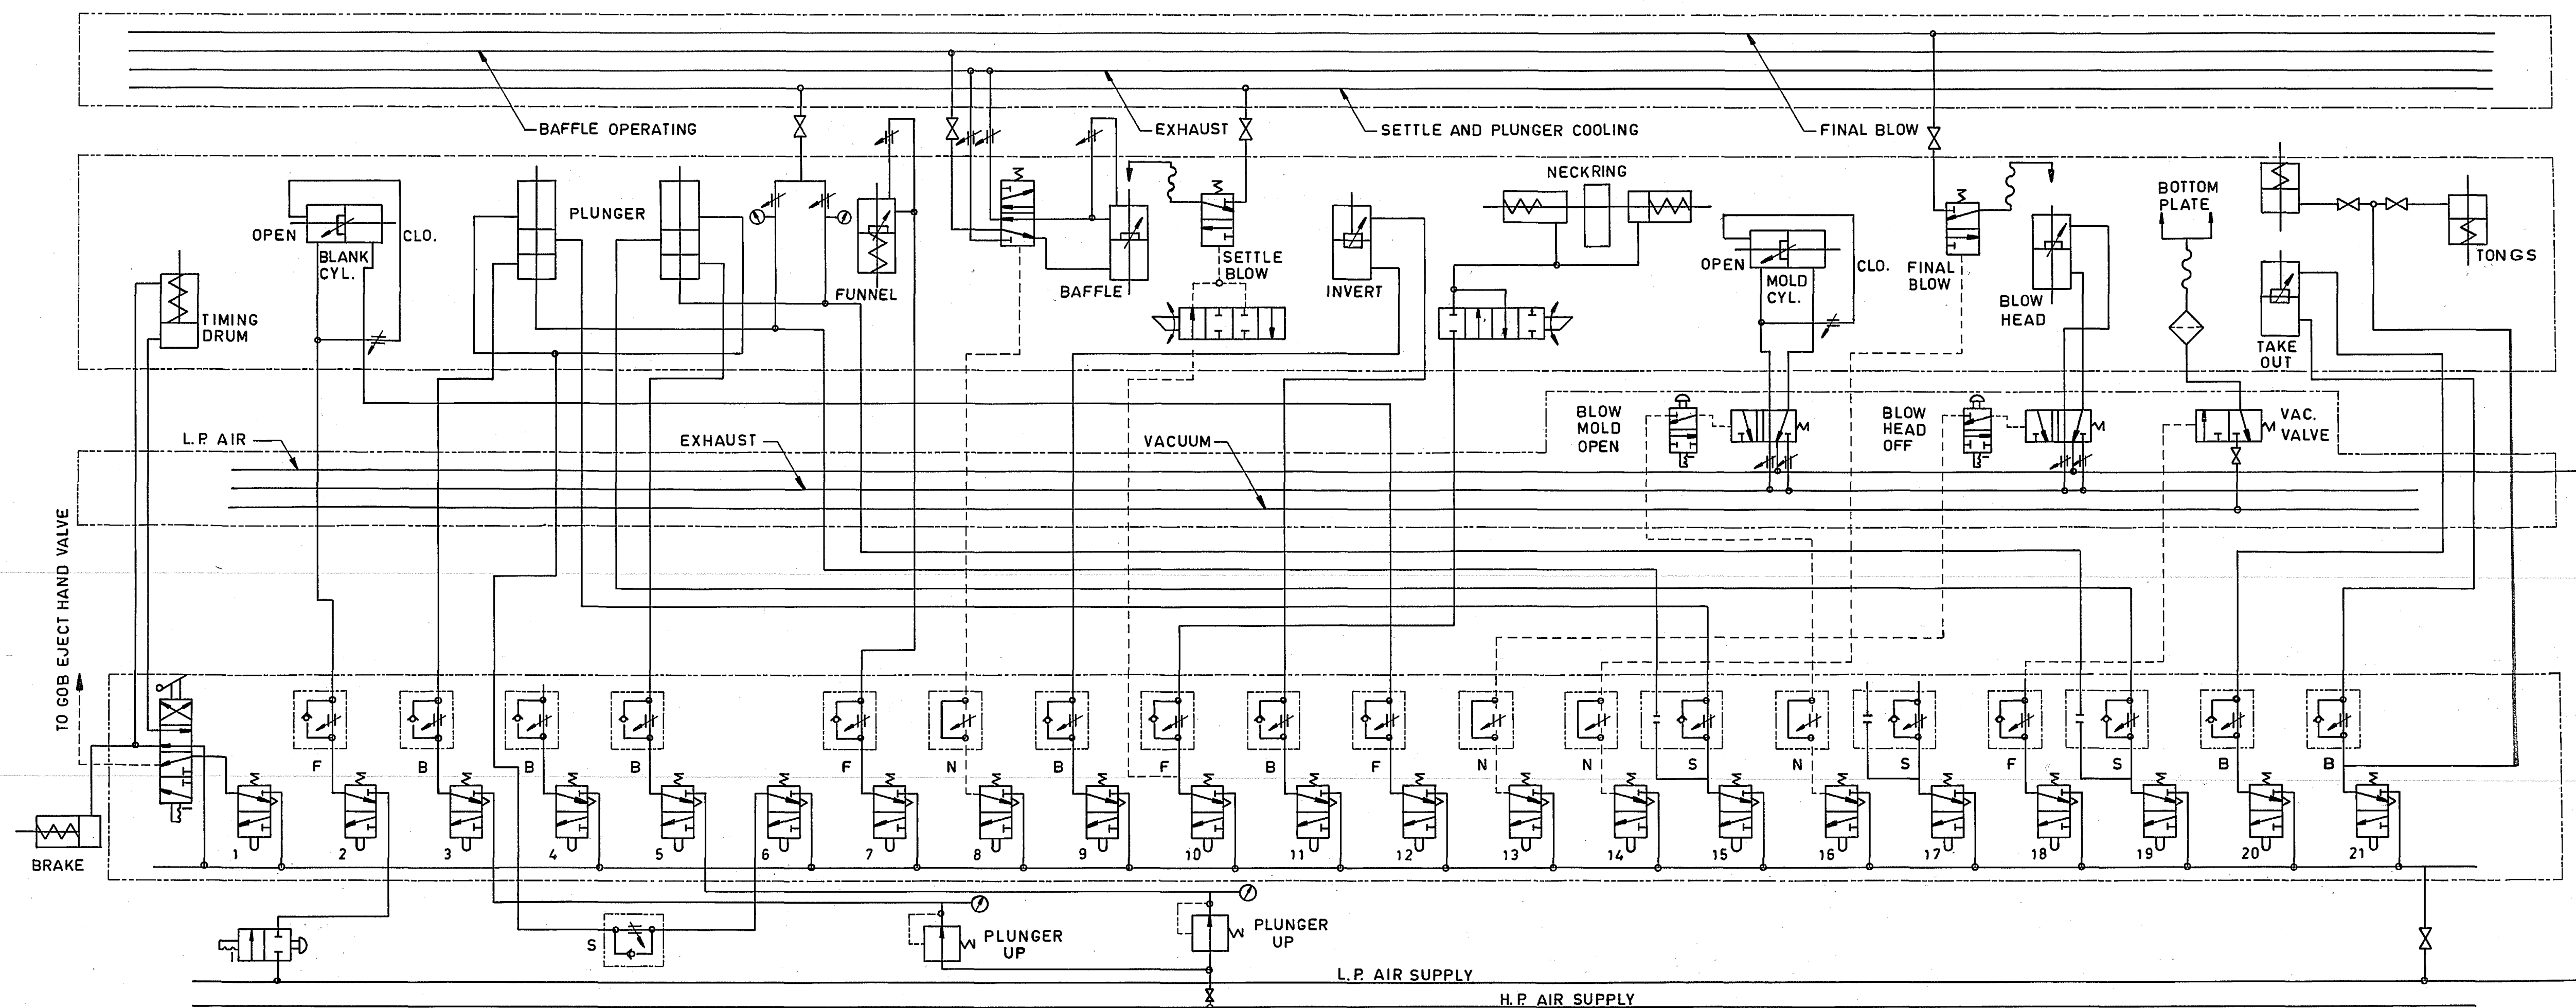

OBS:

SECTION BOX PIPING AND EQUIPMENT ARRANGEMENT
FOR PRESS AND BLOW PLUNGER OPERATIONS ✓

DATA	1 - 1 - 86	DES.	VIDROS VITON LTDA.
REVISÃO		VER.	
ITEM		APROV.	
TOLERÂNCIAS STANDARD PARA SUPERFÍCIES USINADAS SEM TOLERÂNCIA INDICADA		MAT.	
DECIMAL ± 0,05"		ENCANAMENTO GERAL DA MAQ. I.S. 8 SEÇÕES	
FRAÇÃO		NOME	
DE 0" ATÉ 5" ± 1/64		DA PEÇA	
DE 5" ATÉ 24" ± 1/32		TRAT.	
ACIMA DE 24" ± 1/16		TERM.	
		ESCALA	
		N.º DO DES.	
		N.º DA PEÇA VV-1947	