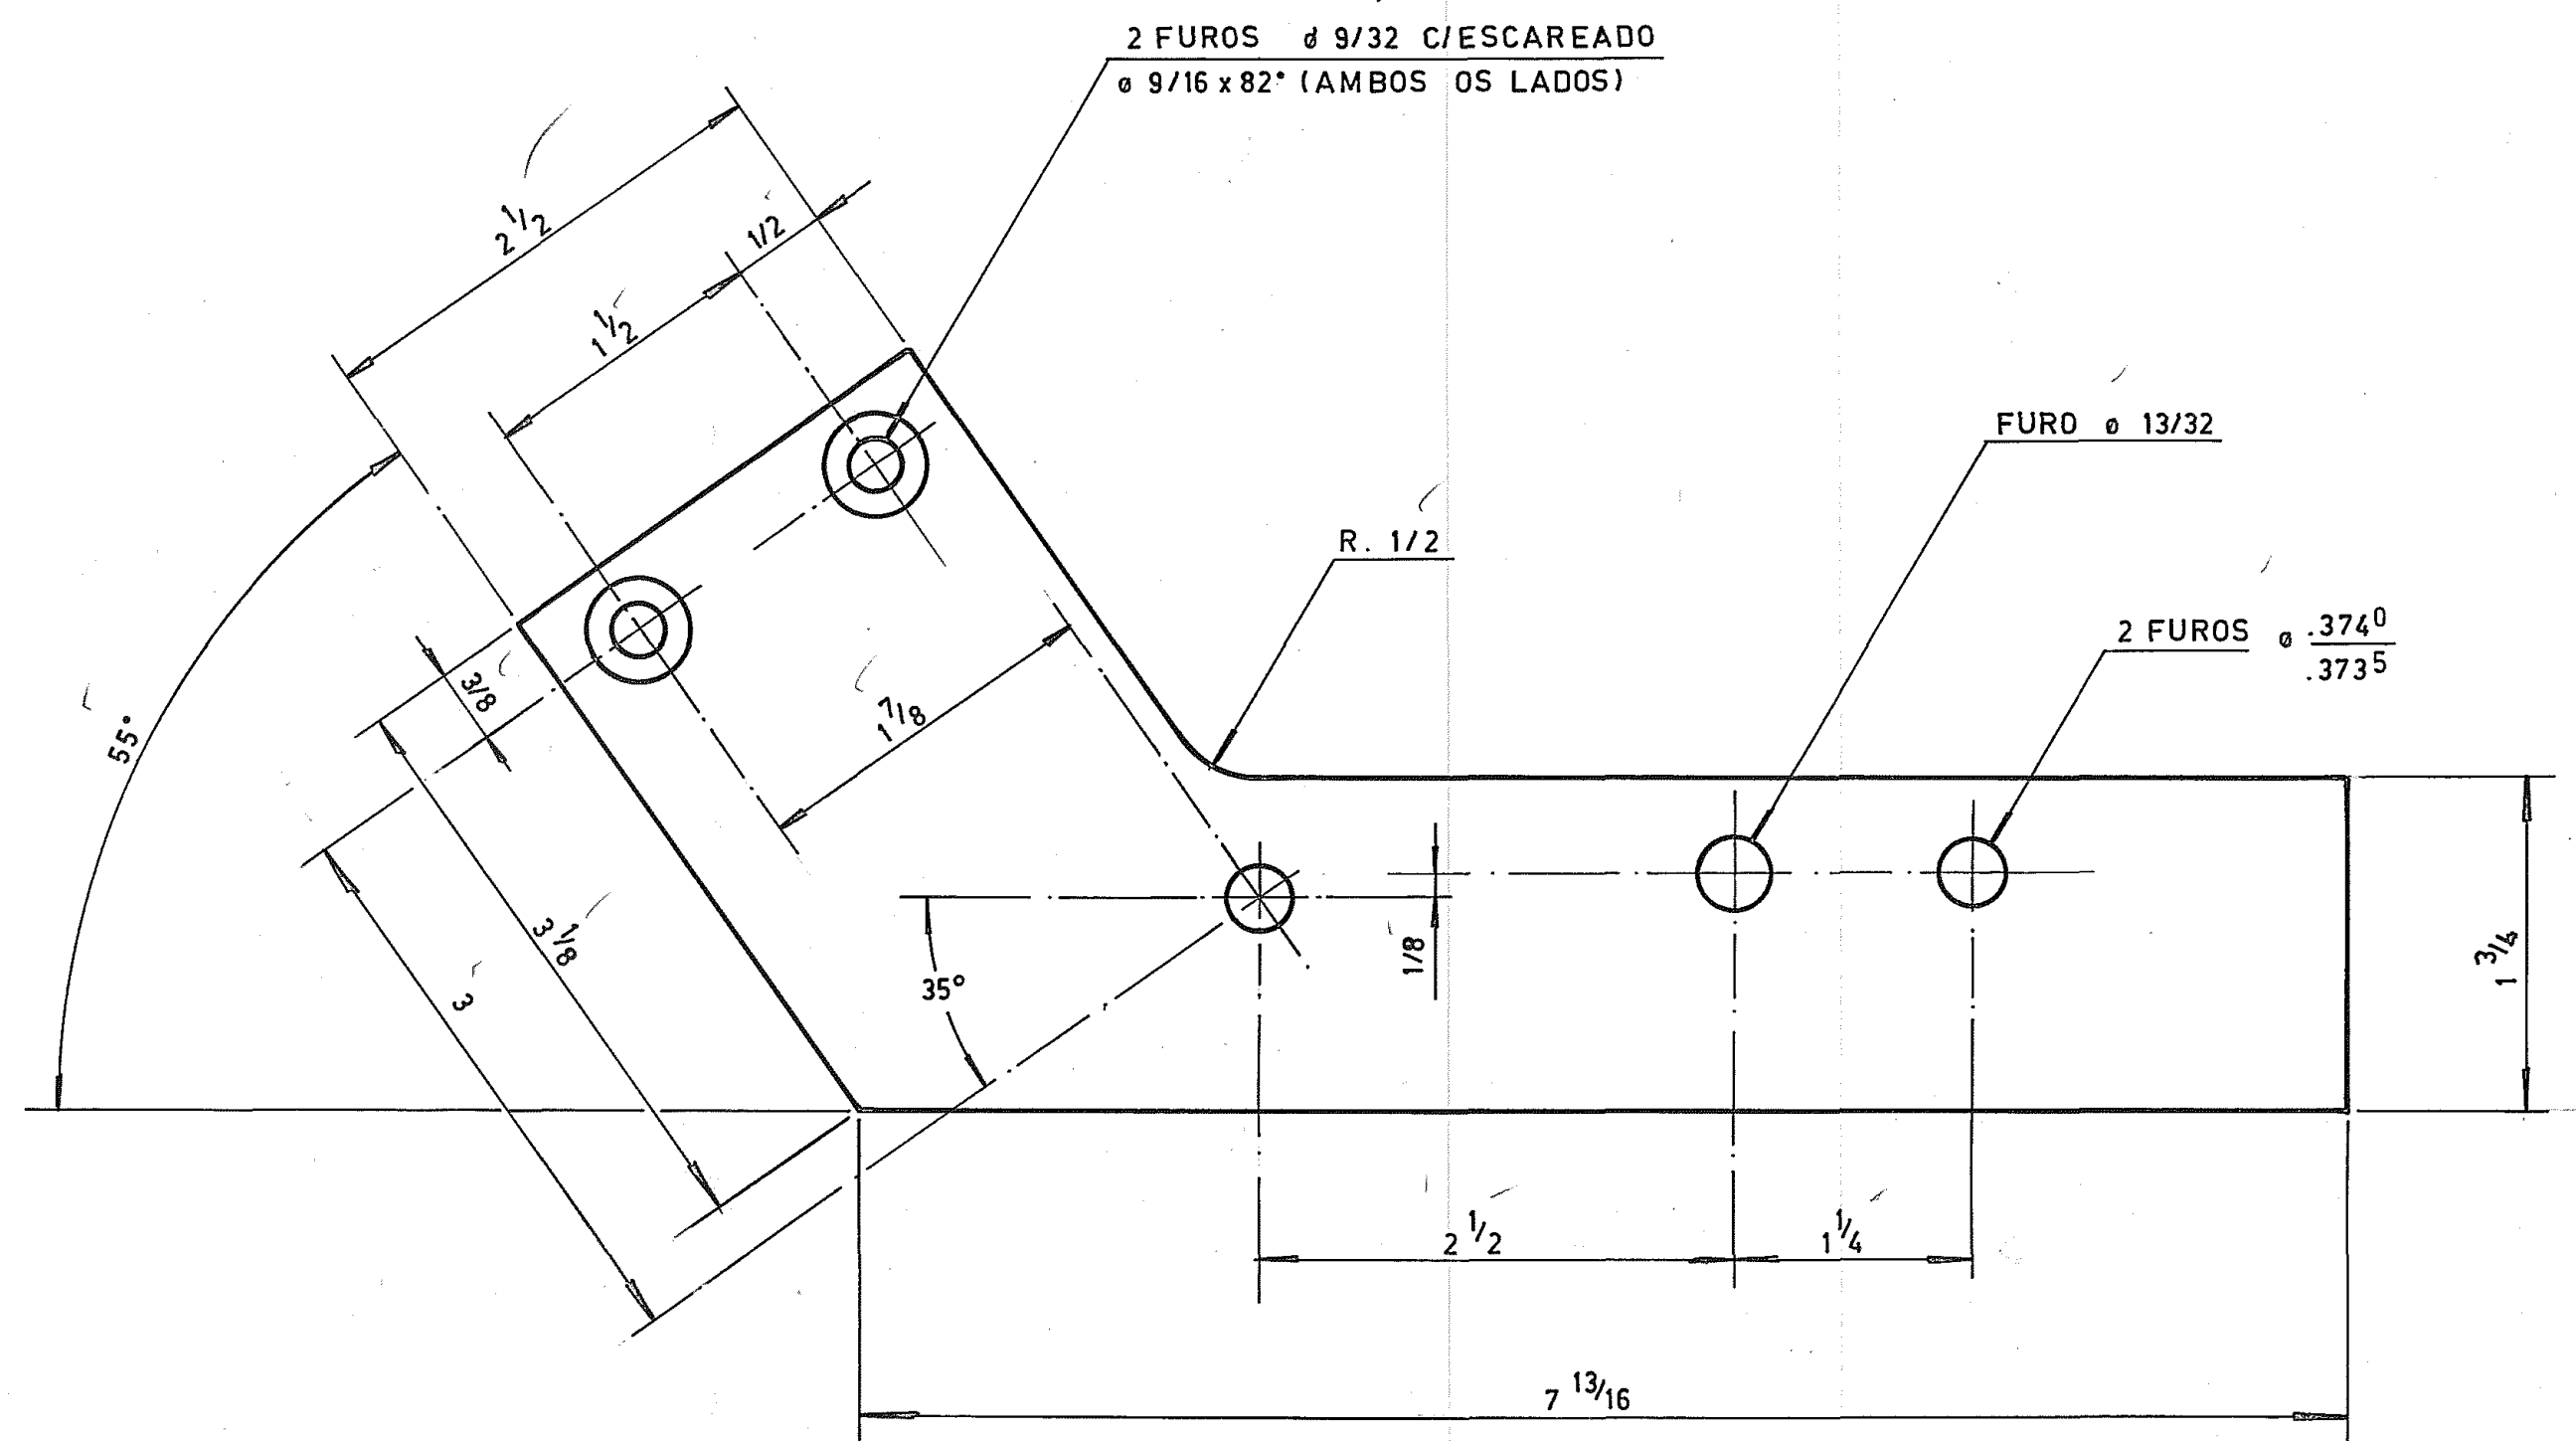


DATA	REVISÃO	ITEMS
31-03-86		
TOLERÂNCIAS STANDARD PARA SUPERFÍCIES USINADAS SEM TOLERÂNCIA INDICADA		
DECIMAL ± DES"		
FRAÇÃO		
DE 0" ATÉ 5" ± 1/64		
DE 5" ATÉ 24" ± 1/32		
ACIMA DE 24" ± 1/16		
TRAT. TERM.		
ESCALA 1:1		

DATA	31-03-86
REVISÃO	
ITEMS	

DES	Paulo José
VER	Wagner
APR	
Nº DO PROJ	VVM-331
Nº DA PEÇA	VV-2133
Nº DO DES	

VIDROS VITON LTDA.
MAT. AÇO SAE 1020
DEFL & TROUGH SUPT SECT.
2 OF 8 SECT. QUAD. 60B.
DEFLECTOR BRACKET