

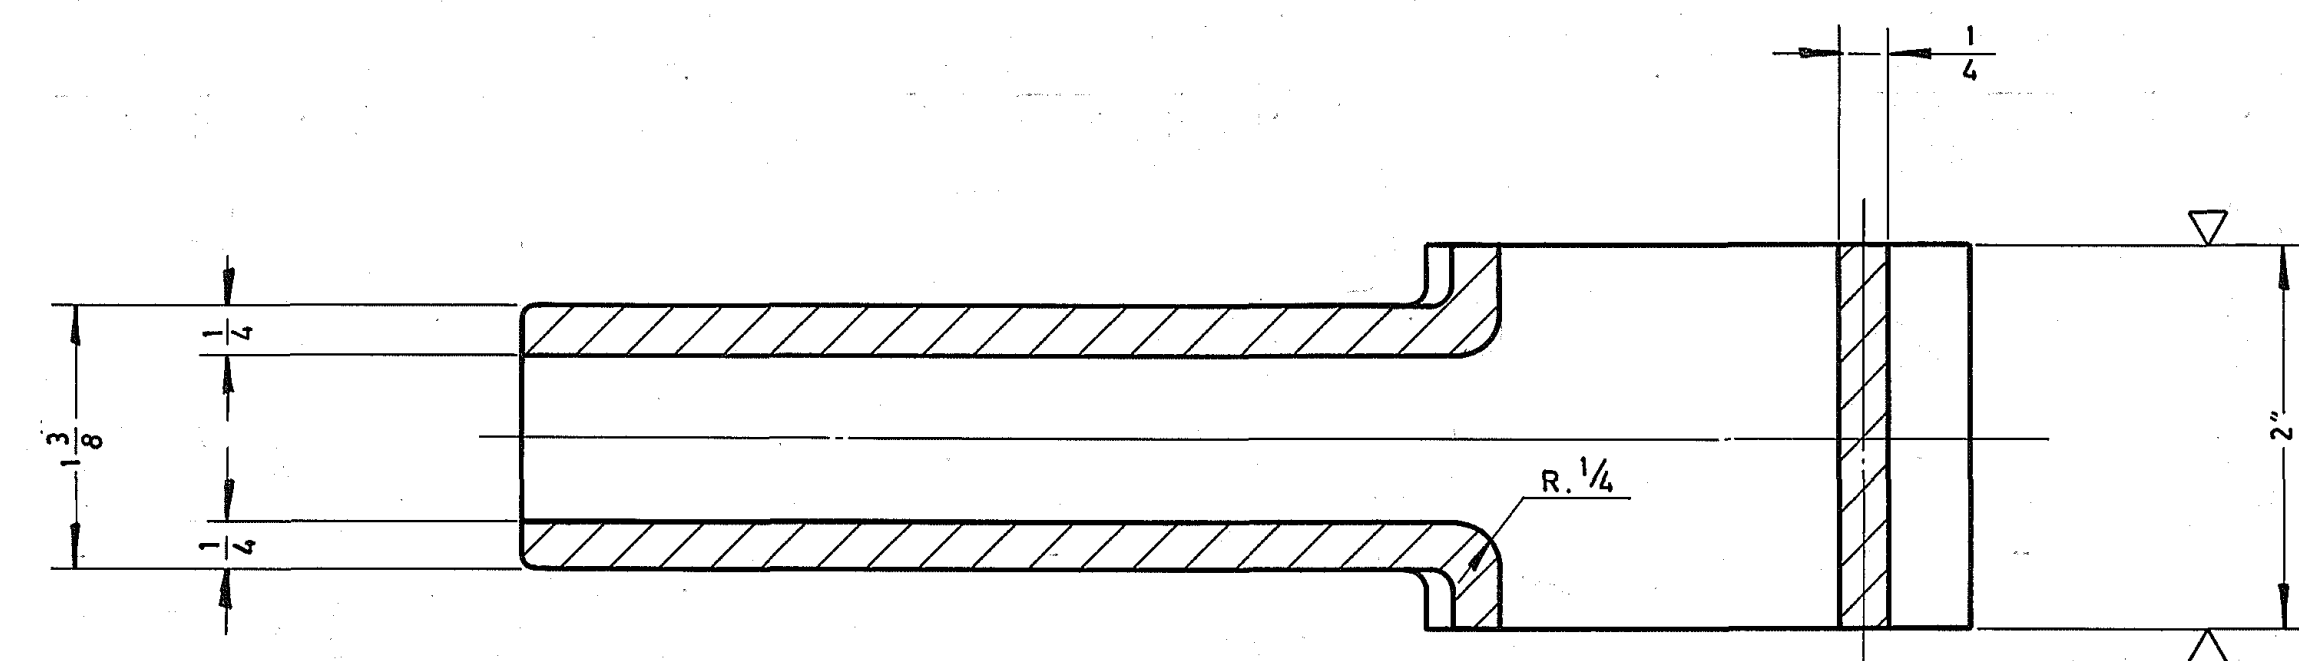


ESTAMPAR DE FUNDIÇÃO (TOP E O Nº VV-2367

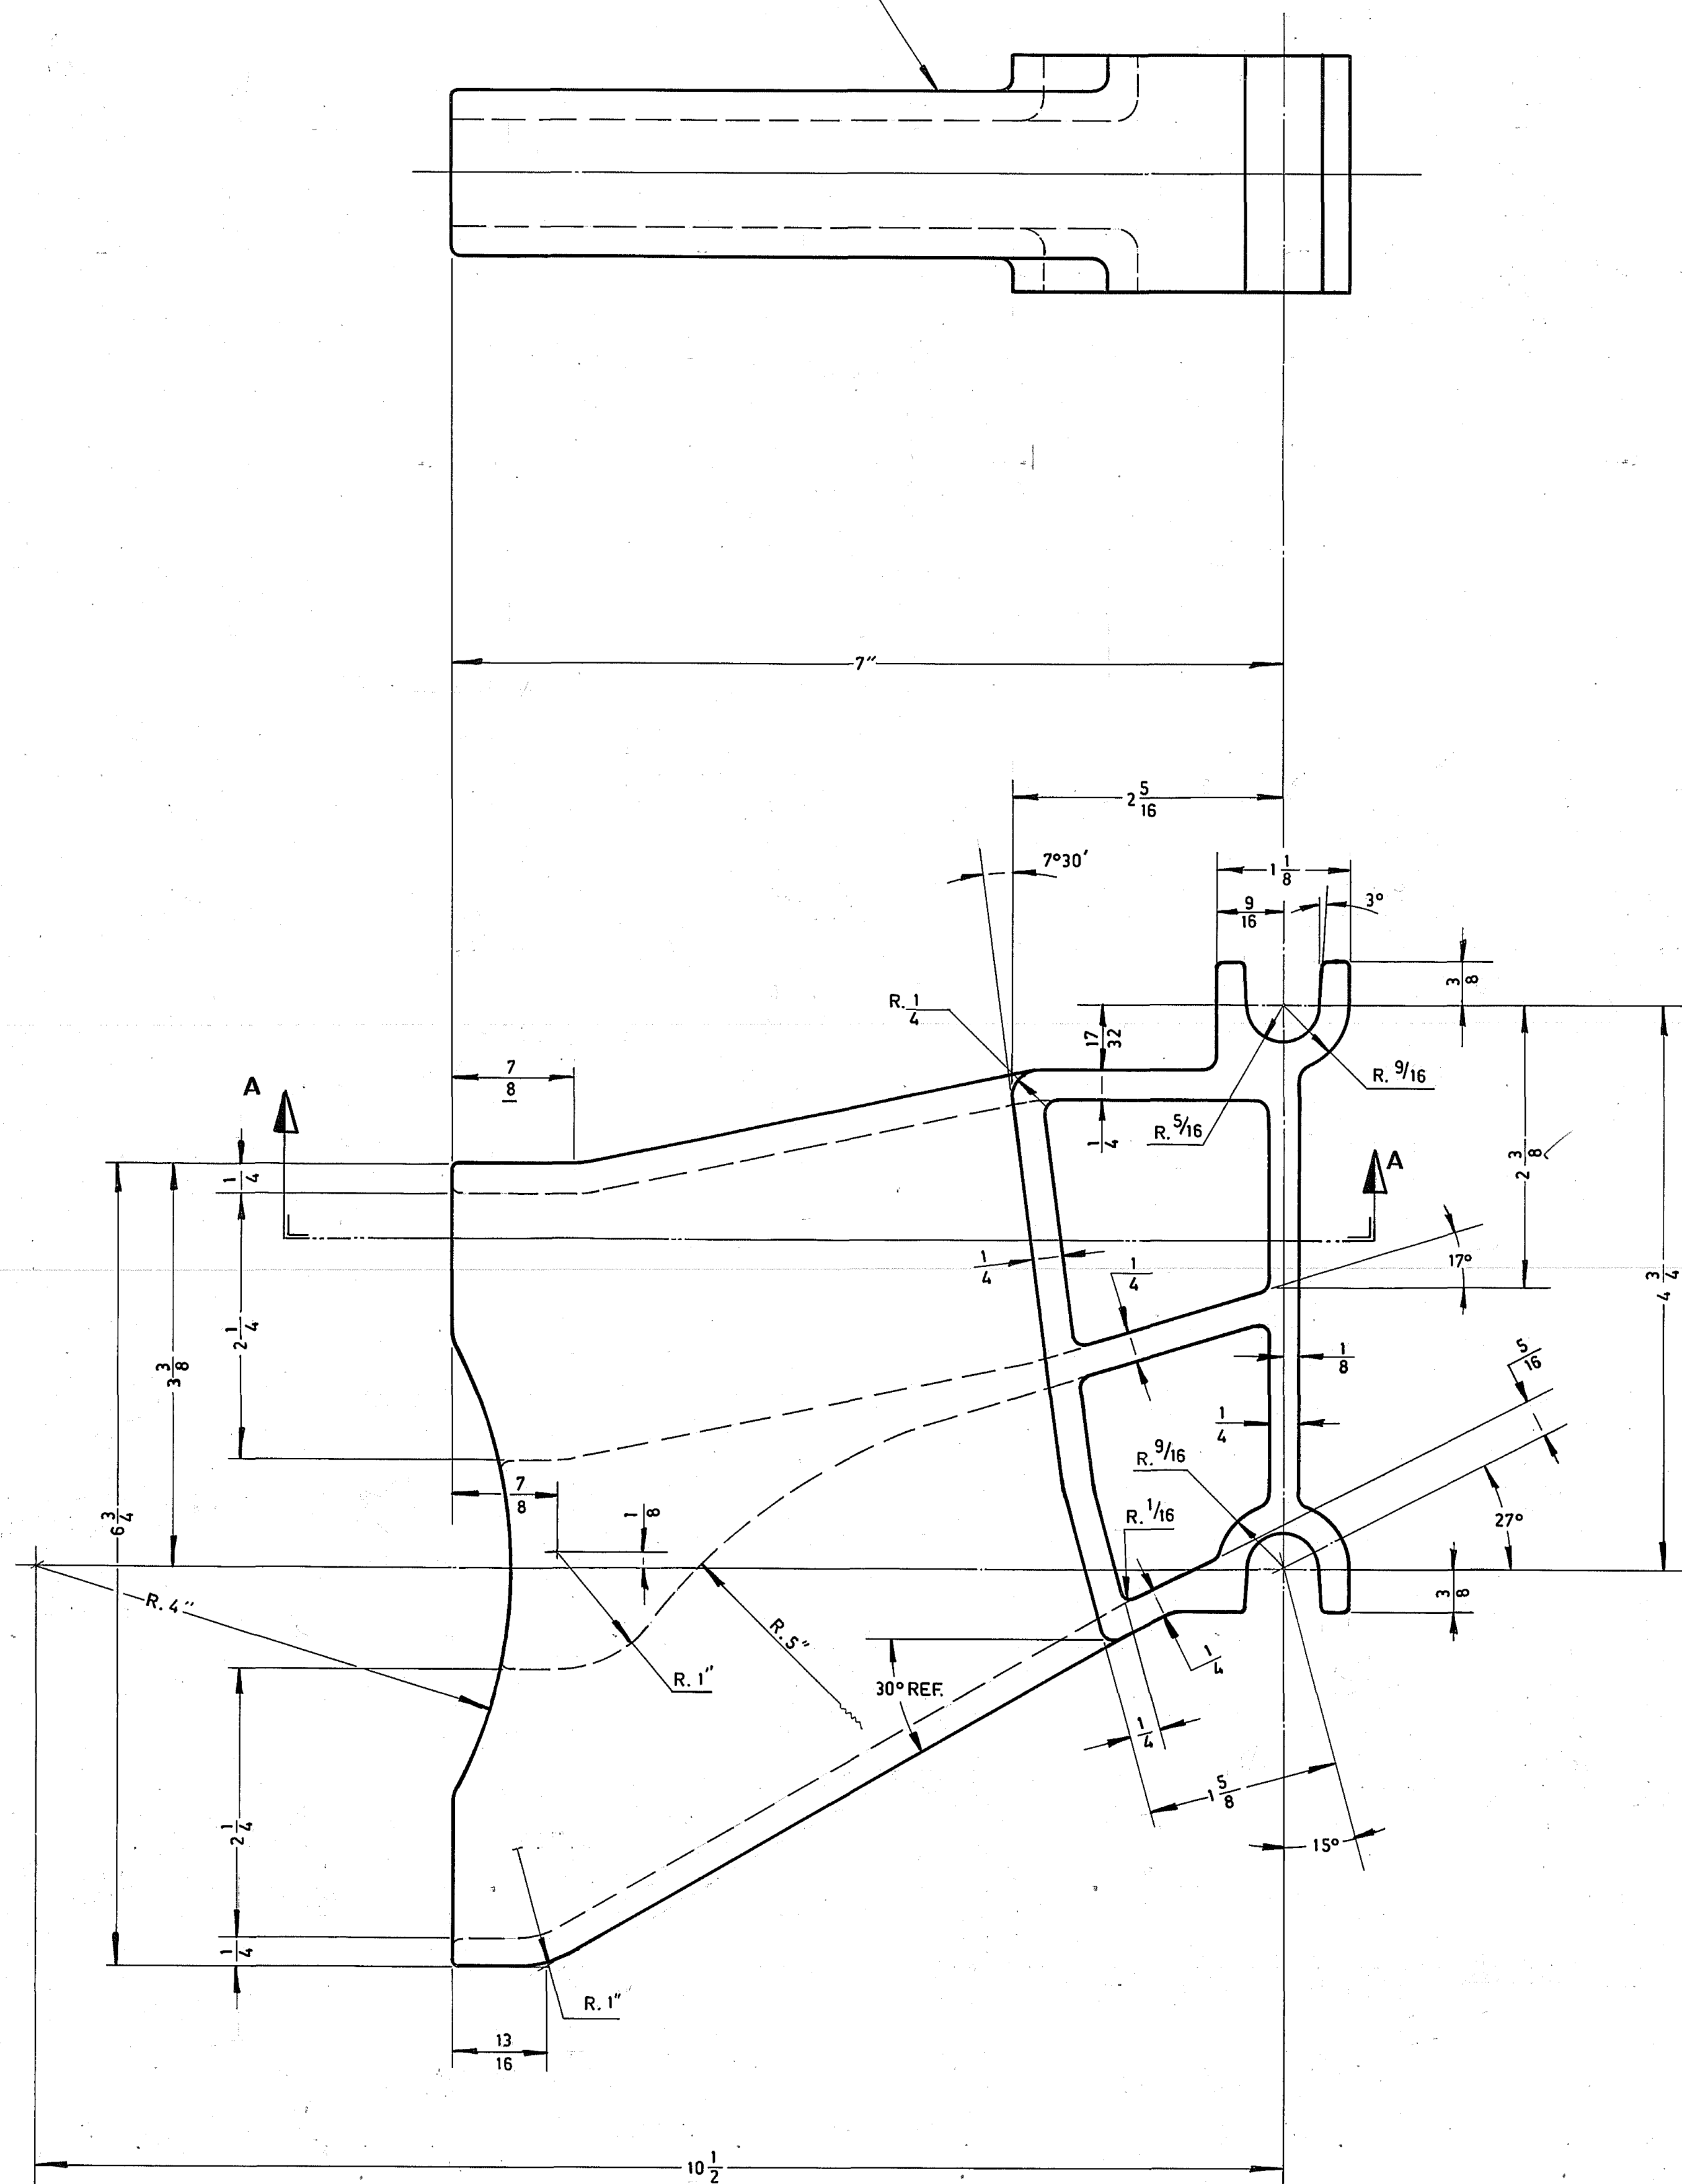

CORTE A-A

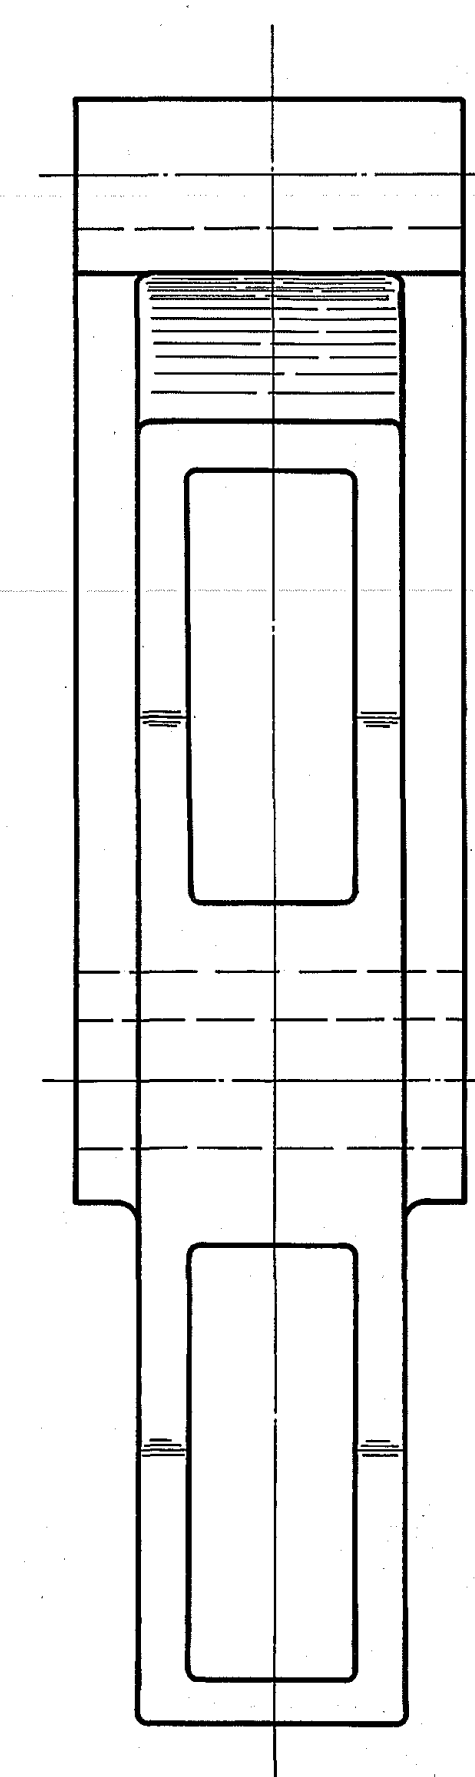

~(▽)