


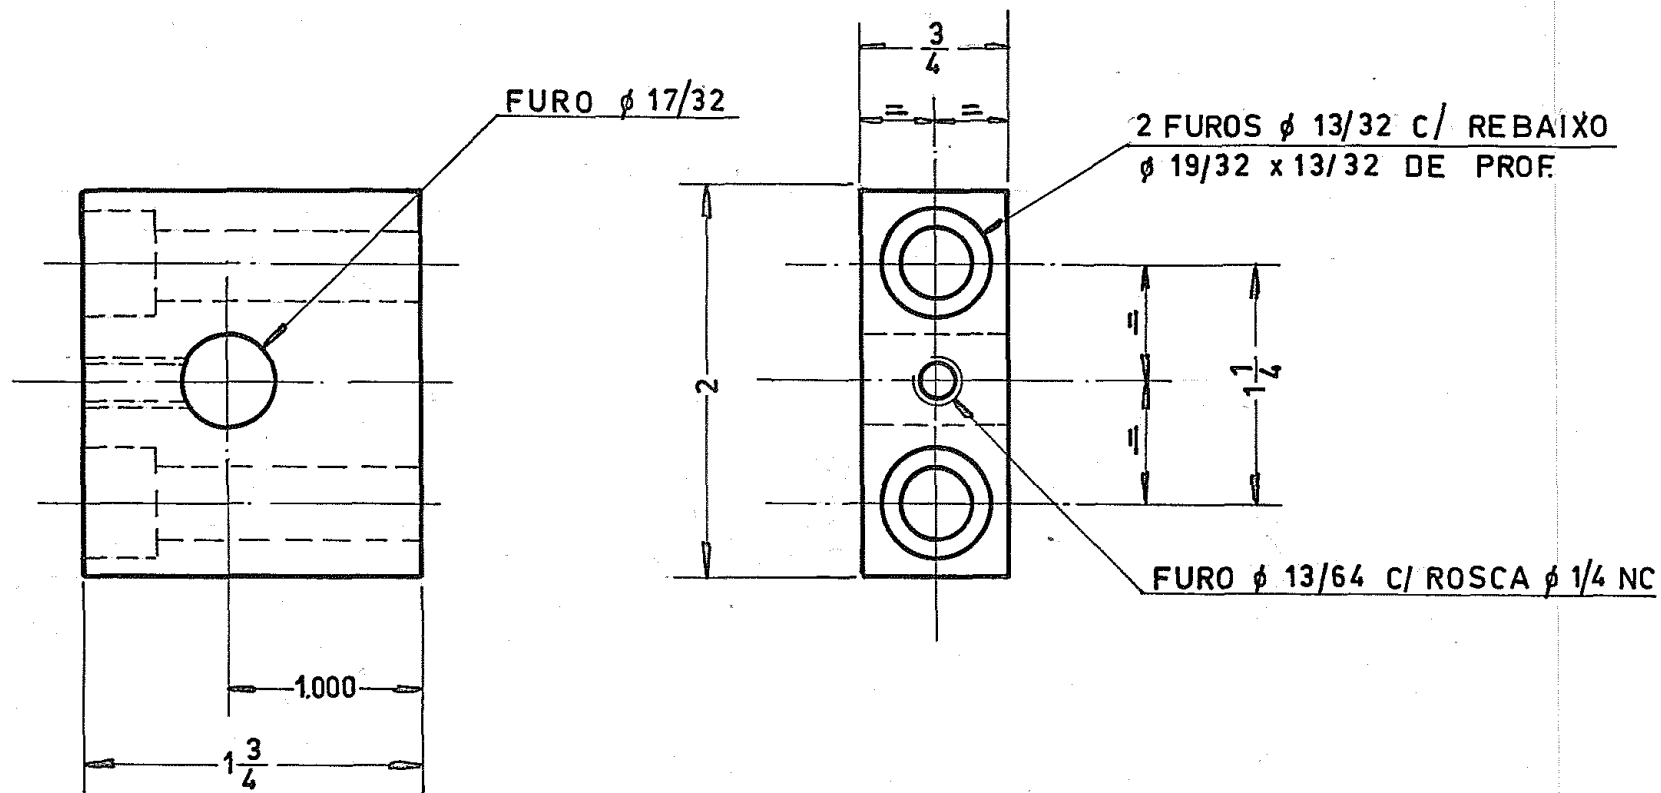

|             |                      |      |                                                                                 |           |                                                    |                           |                          |
|-------------|----------------------|------|---------------------------------------------------------------------------------|-----------|----------------------------------------------------|---------------------------|--------------------------|
| DATA        | REVISÃO              | ITEM | DATA: 16-02-87                                                                  |           | VIDROS VITON LTDA.                                 |                           | DES. <i>Miguel Braga</i> |
|             |                      |      | TOLERANCIAS STANDARD<br>PARA SUPERFICIES<br>USINADAS SEM<br>TOLERANCIA INDICADA |           | MAT. AÇO SAE 1020                                  | VER. <i>Flavio</i>        |                          |
|             |                      |      | DECIMAL ± 005"                                                                  |           | SUPORTE DAS CANALETAS<br>MAQ. I.S. 8 SEÇÕES (S.G.) | APROV. <i>[Signature]</i> |                          |
|             |                      |      | FRAÇÃO                                                                          |           | BLOCO DE FIXAÇÃO                                   | N.º DO CONJ. VVM-350      |                          |
| DIMENSÃO EM | DE 0" ATÉ 5" ± 1/64  |      | TRAT. TERM.                                                                     | ESCALA 11 | N.º DA PEÇA VV-2527                                |                           |                          |
|             | DE 5" ATÉ 24" ± 1/32 |      |                                                                                 |           |                                                    |                           |                          |
|             | ACIMA DE 24" ± 1/16  |      |                                                                                 |           |                                                    |                           |                          |