


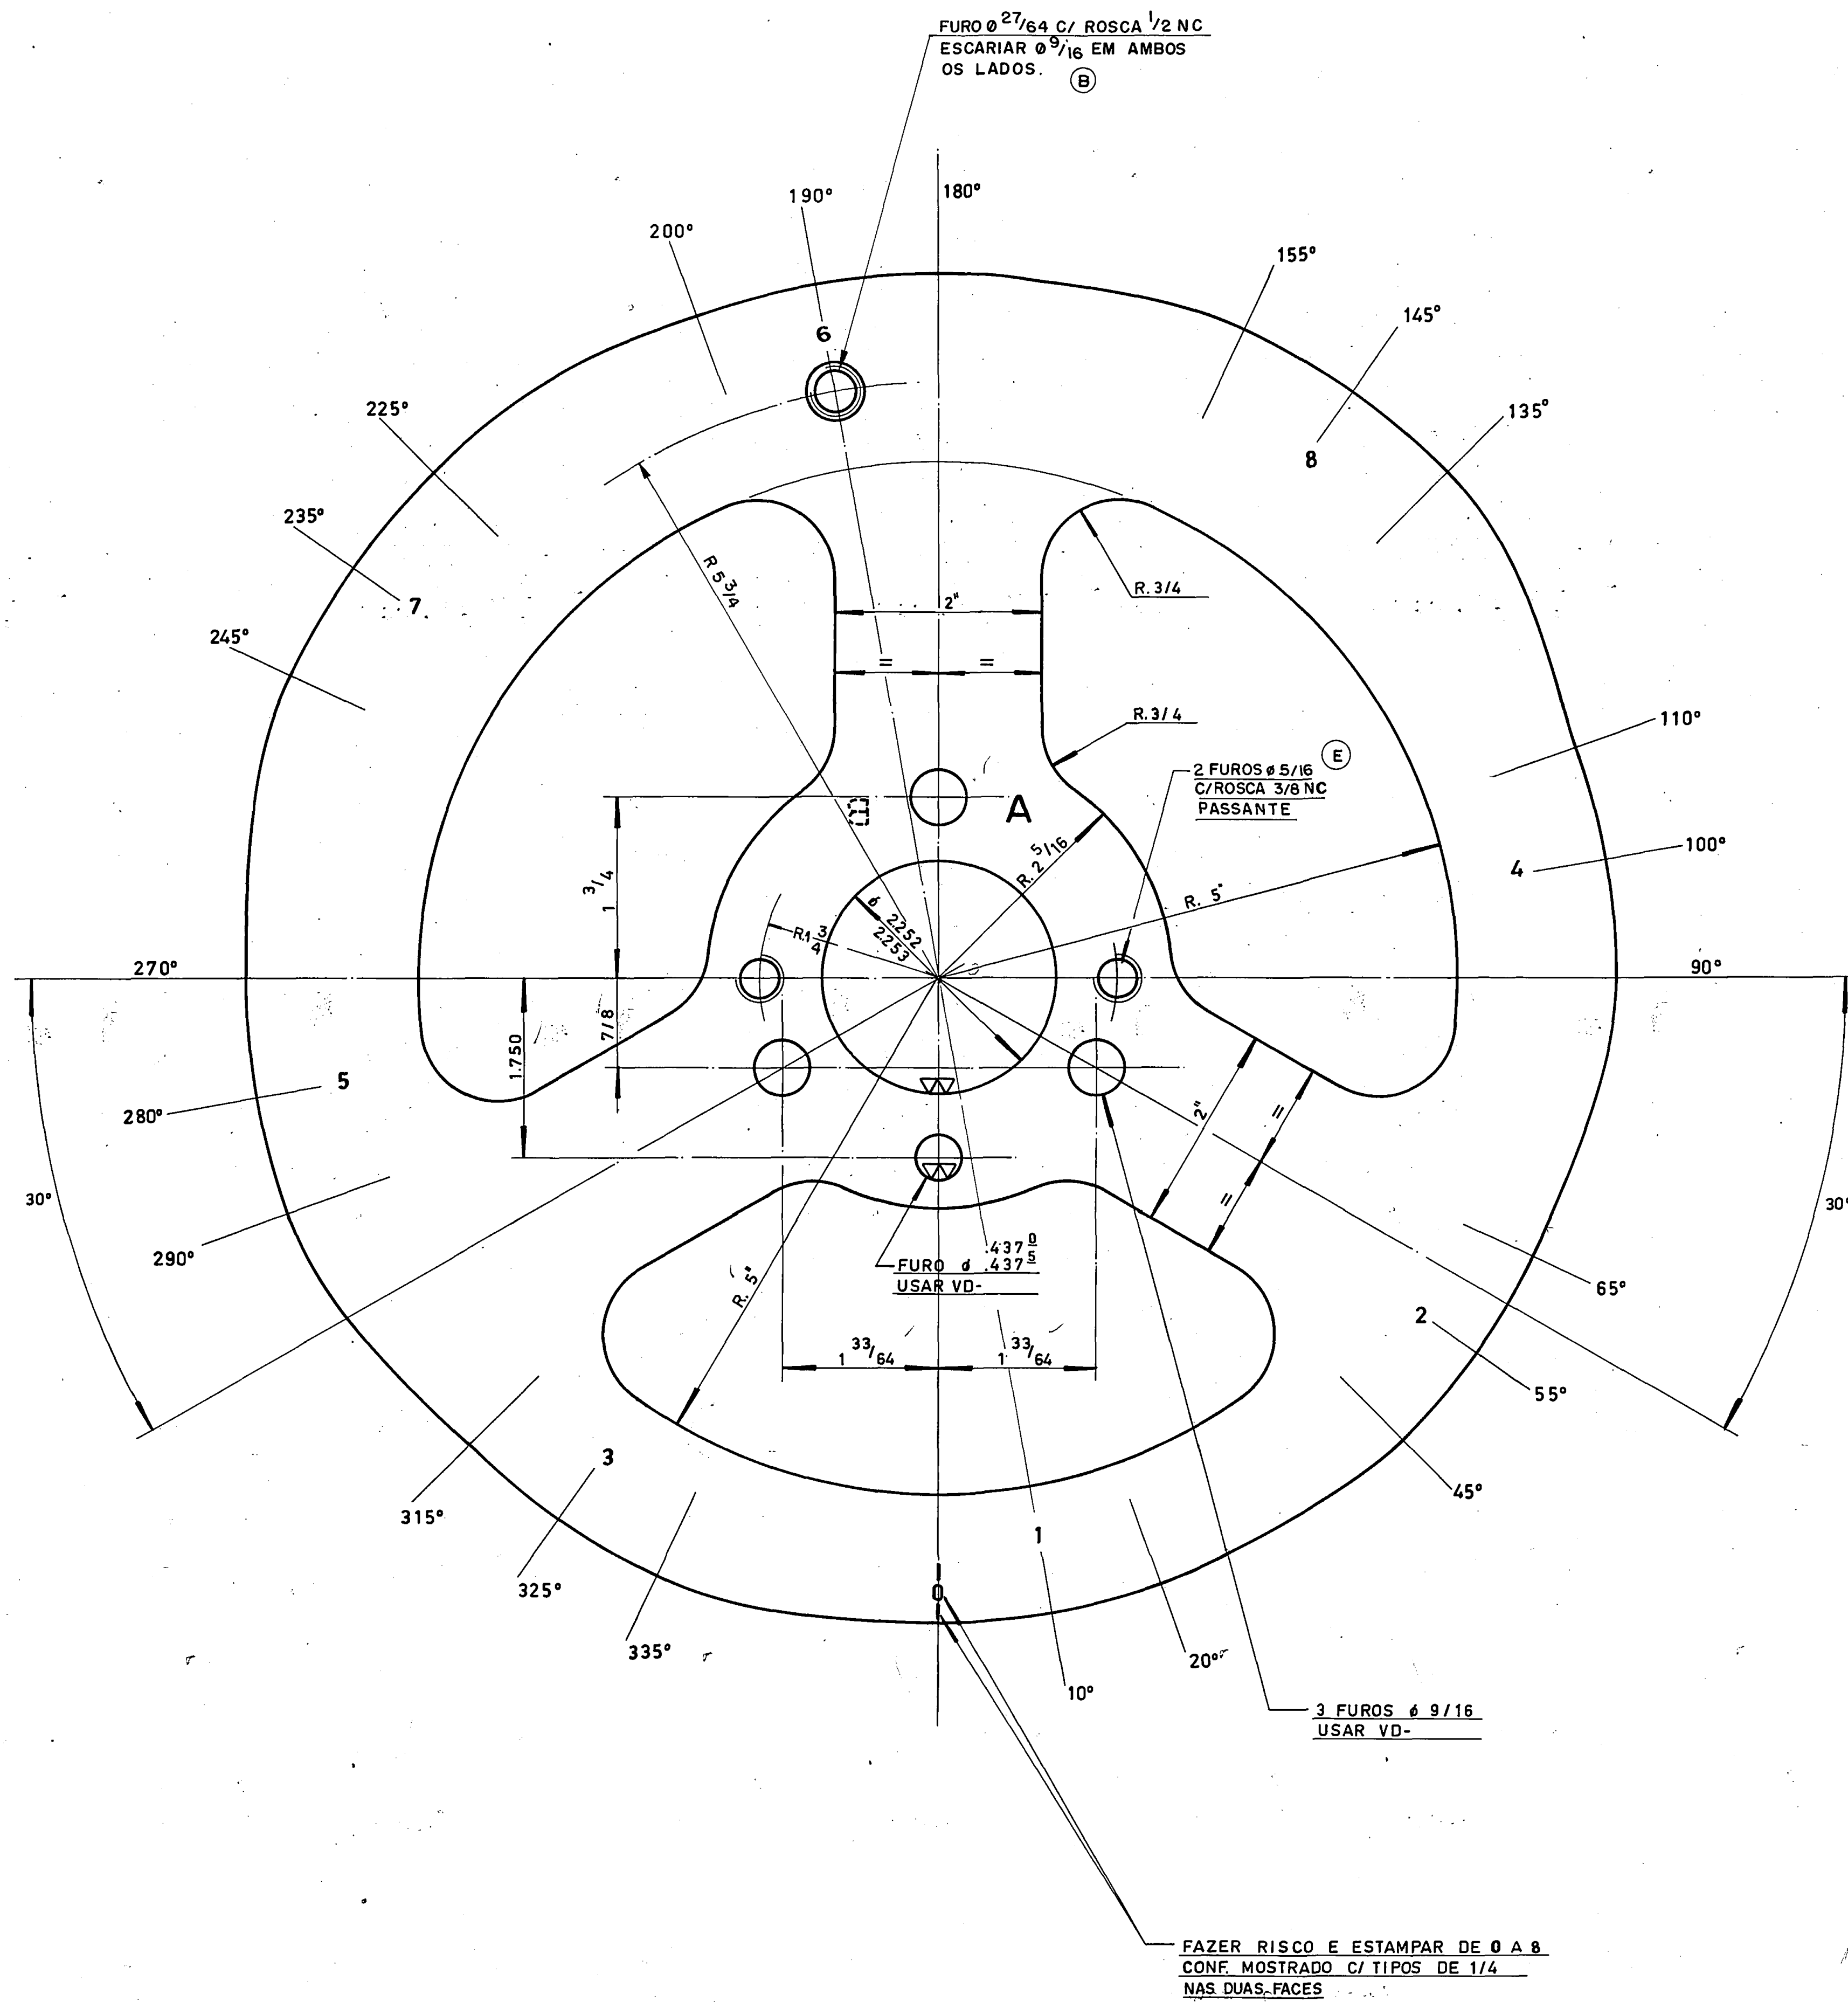

| DIMENSÕES DA PISTA |             |       |
|--------------------|-------------|-------|
| SEQ.               | GRAUS       | RAIO  |
| 1                  | 0° A 20°    | 6.244 |
| 2                  | 45° A 65°   | 6.298 |
| 3                  | 90° A 110°  | 6.302 |
| 4                  | 135° A 155° | 6.317 |
| 5                  | 180° A 200° | 6.345 |
| 6                  | 225° A 245° | 6.349 |
| 7                  | 270° A 290° | 6.385 |
| 8                  | 315° A 335° | 6.392 |

ORDEM DE FOGO:  
R.H. - 1-2-4-8-6-7-5-3  
L.H. - 1-3-5-7-6-8-4-2

RET. VERT.  
▽ (▽-▽▽)

CHAPA DE AÇO SAE 8620  
CORT. A MAÇARICO AUTOM. VE-1898  
ATENÇÃO: ALIVIAR TENSÕES ANTES DE USINAR

| VIDROS VITON LTDA.                                                     |                 | DES.          |
|------------------------------------------------------------------------|-----------------|---------------|
| E                                                                      | ACRESC.         | VER.          |
| D                                                                      | ALTEROU VALORES | APROV.        |
| C                                                                      | ERA TEMP.       | N.º DO        |
| B                                                                      | ACRESC.         | CONJ. VVM-246 |
| A                                                                      | ERA USO         | N.º DA        |
| DATA                                                                   | REVISÃO         | PEÇA          |
| 19/11/87                                                               | 1               | 2804          |
| TOLERÂNCIAS STANDARD PARA SUPERFÍCIES USINADAS SEM TOLERÂNCIA INDICADA |                 | ESCALA        |
| DECIMAL ± 0.05"                                                        |                 | 1:1           |
| FRACÇÃO                                                                |                 | N.º DO        |
| DE 0" ATE 5" ± 1/64                                                    |                 | DES.          |
| DE 5" ATE 24" ± 1/32                                                   |                 |               |
| ACIMA DE 24" ± 1/16                                                    |                 |               |
| NOME DA PEÇA                                                           |                 |               |
| CAM LEVER & REDUCTOR                                                   |                 |               |
| TRAT. CEMENTAR 1/16 PROF. E                                            |                 |               |
| TERM. TEMPERAR 58-62 RC                                                |                 |               |