


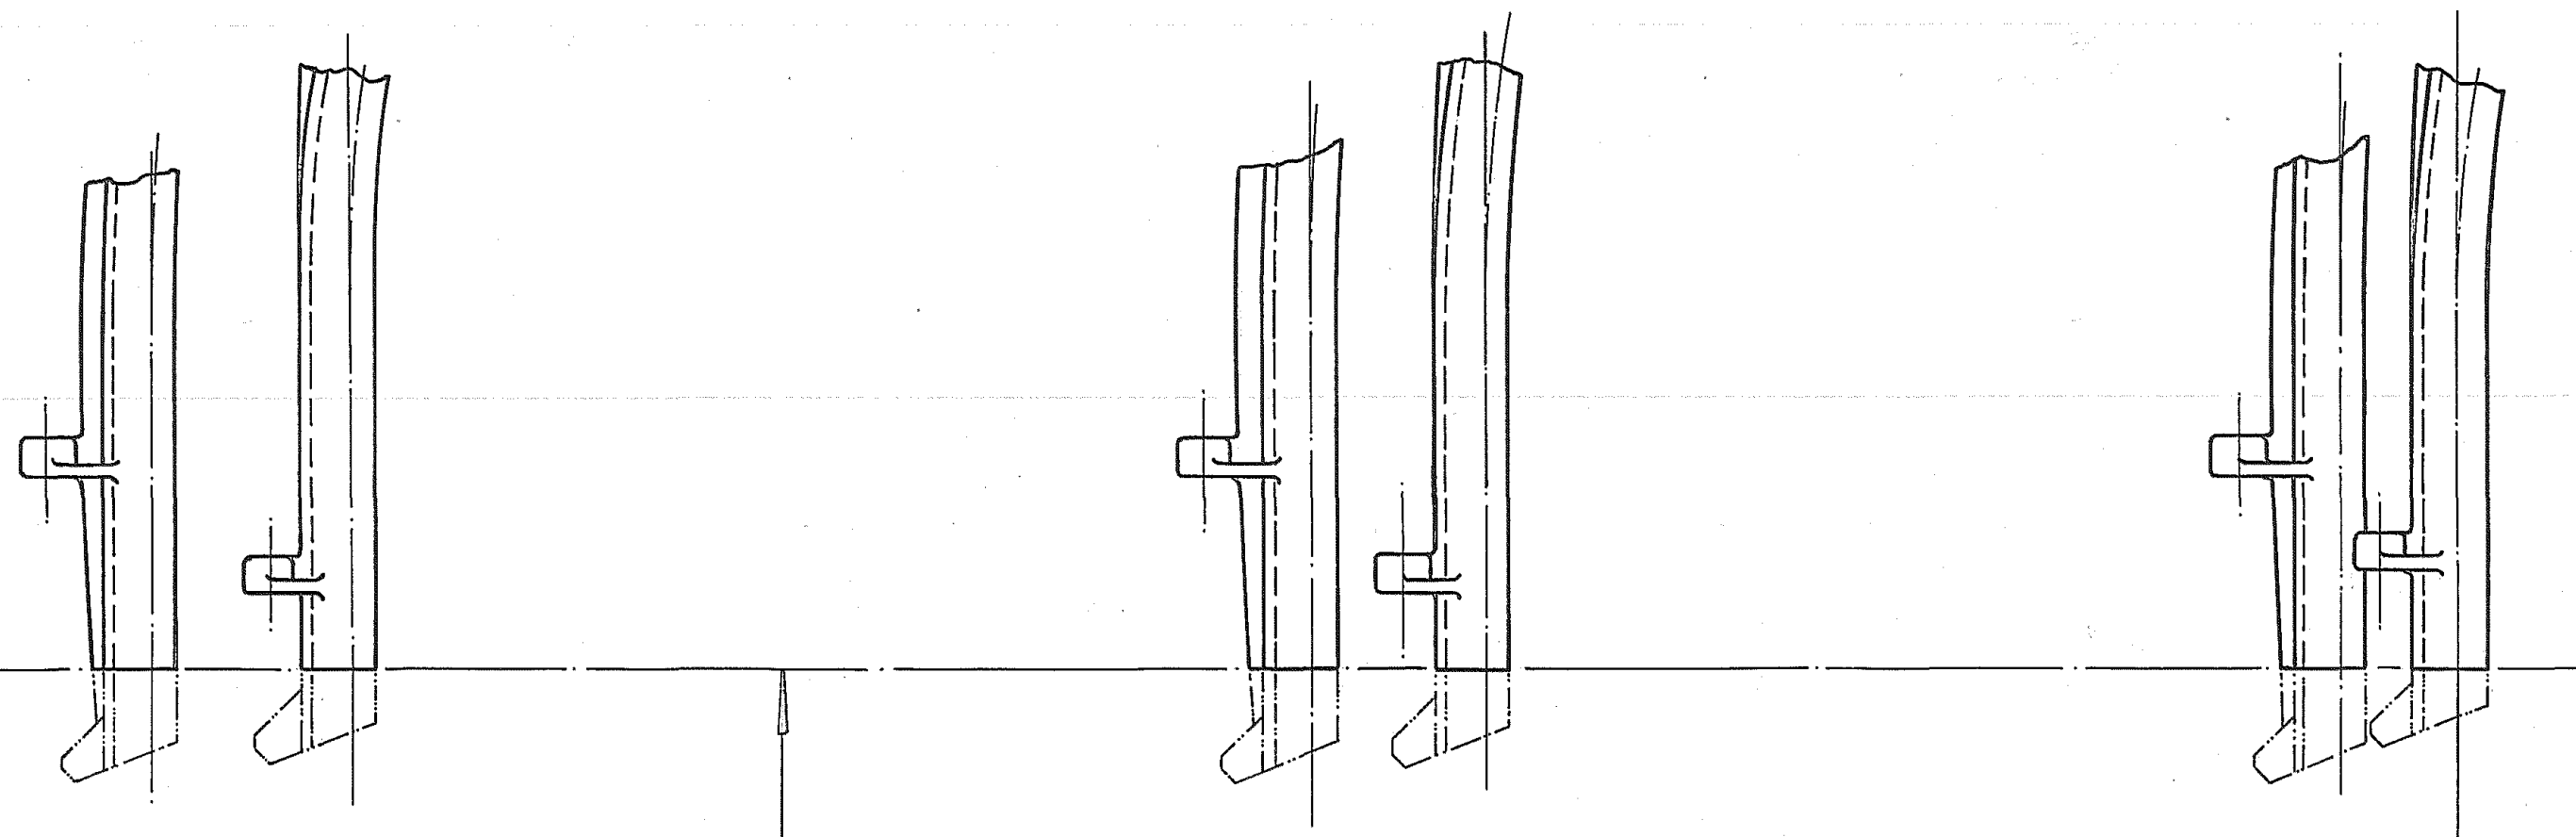

29" (VIDE OBS.)

OBS.: CORTAR NESTA DIMENSÃO
A PONTA DOS DEFLECTORES

TOPO DO FRAME

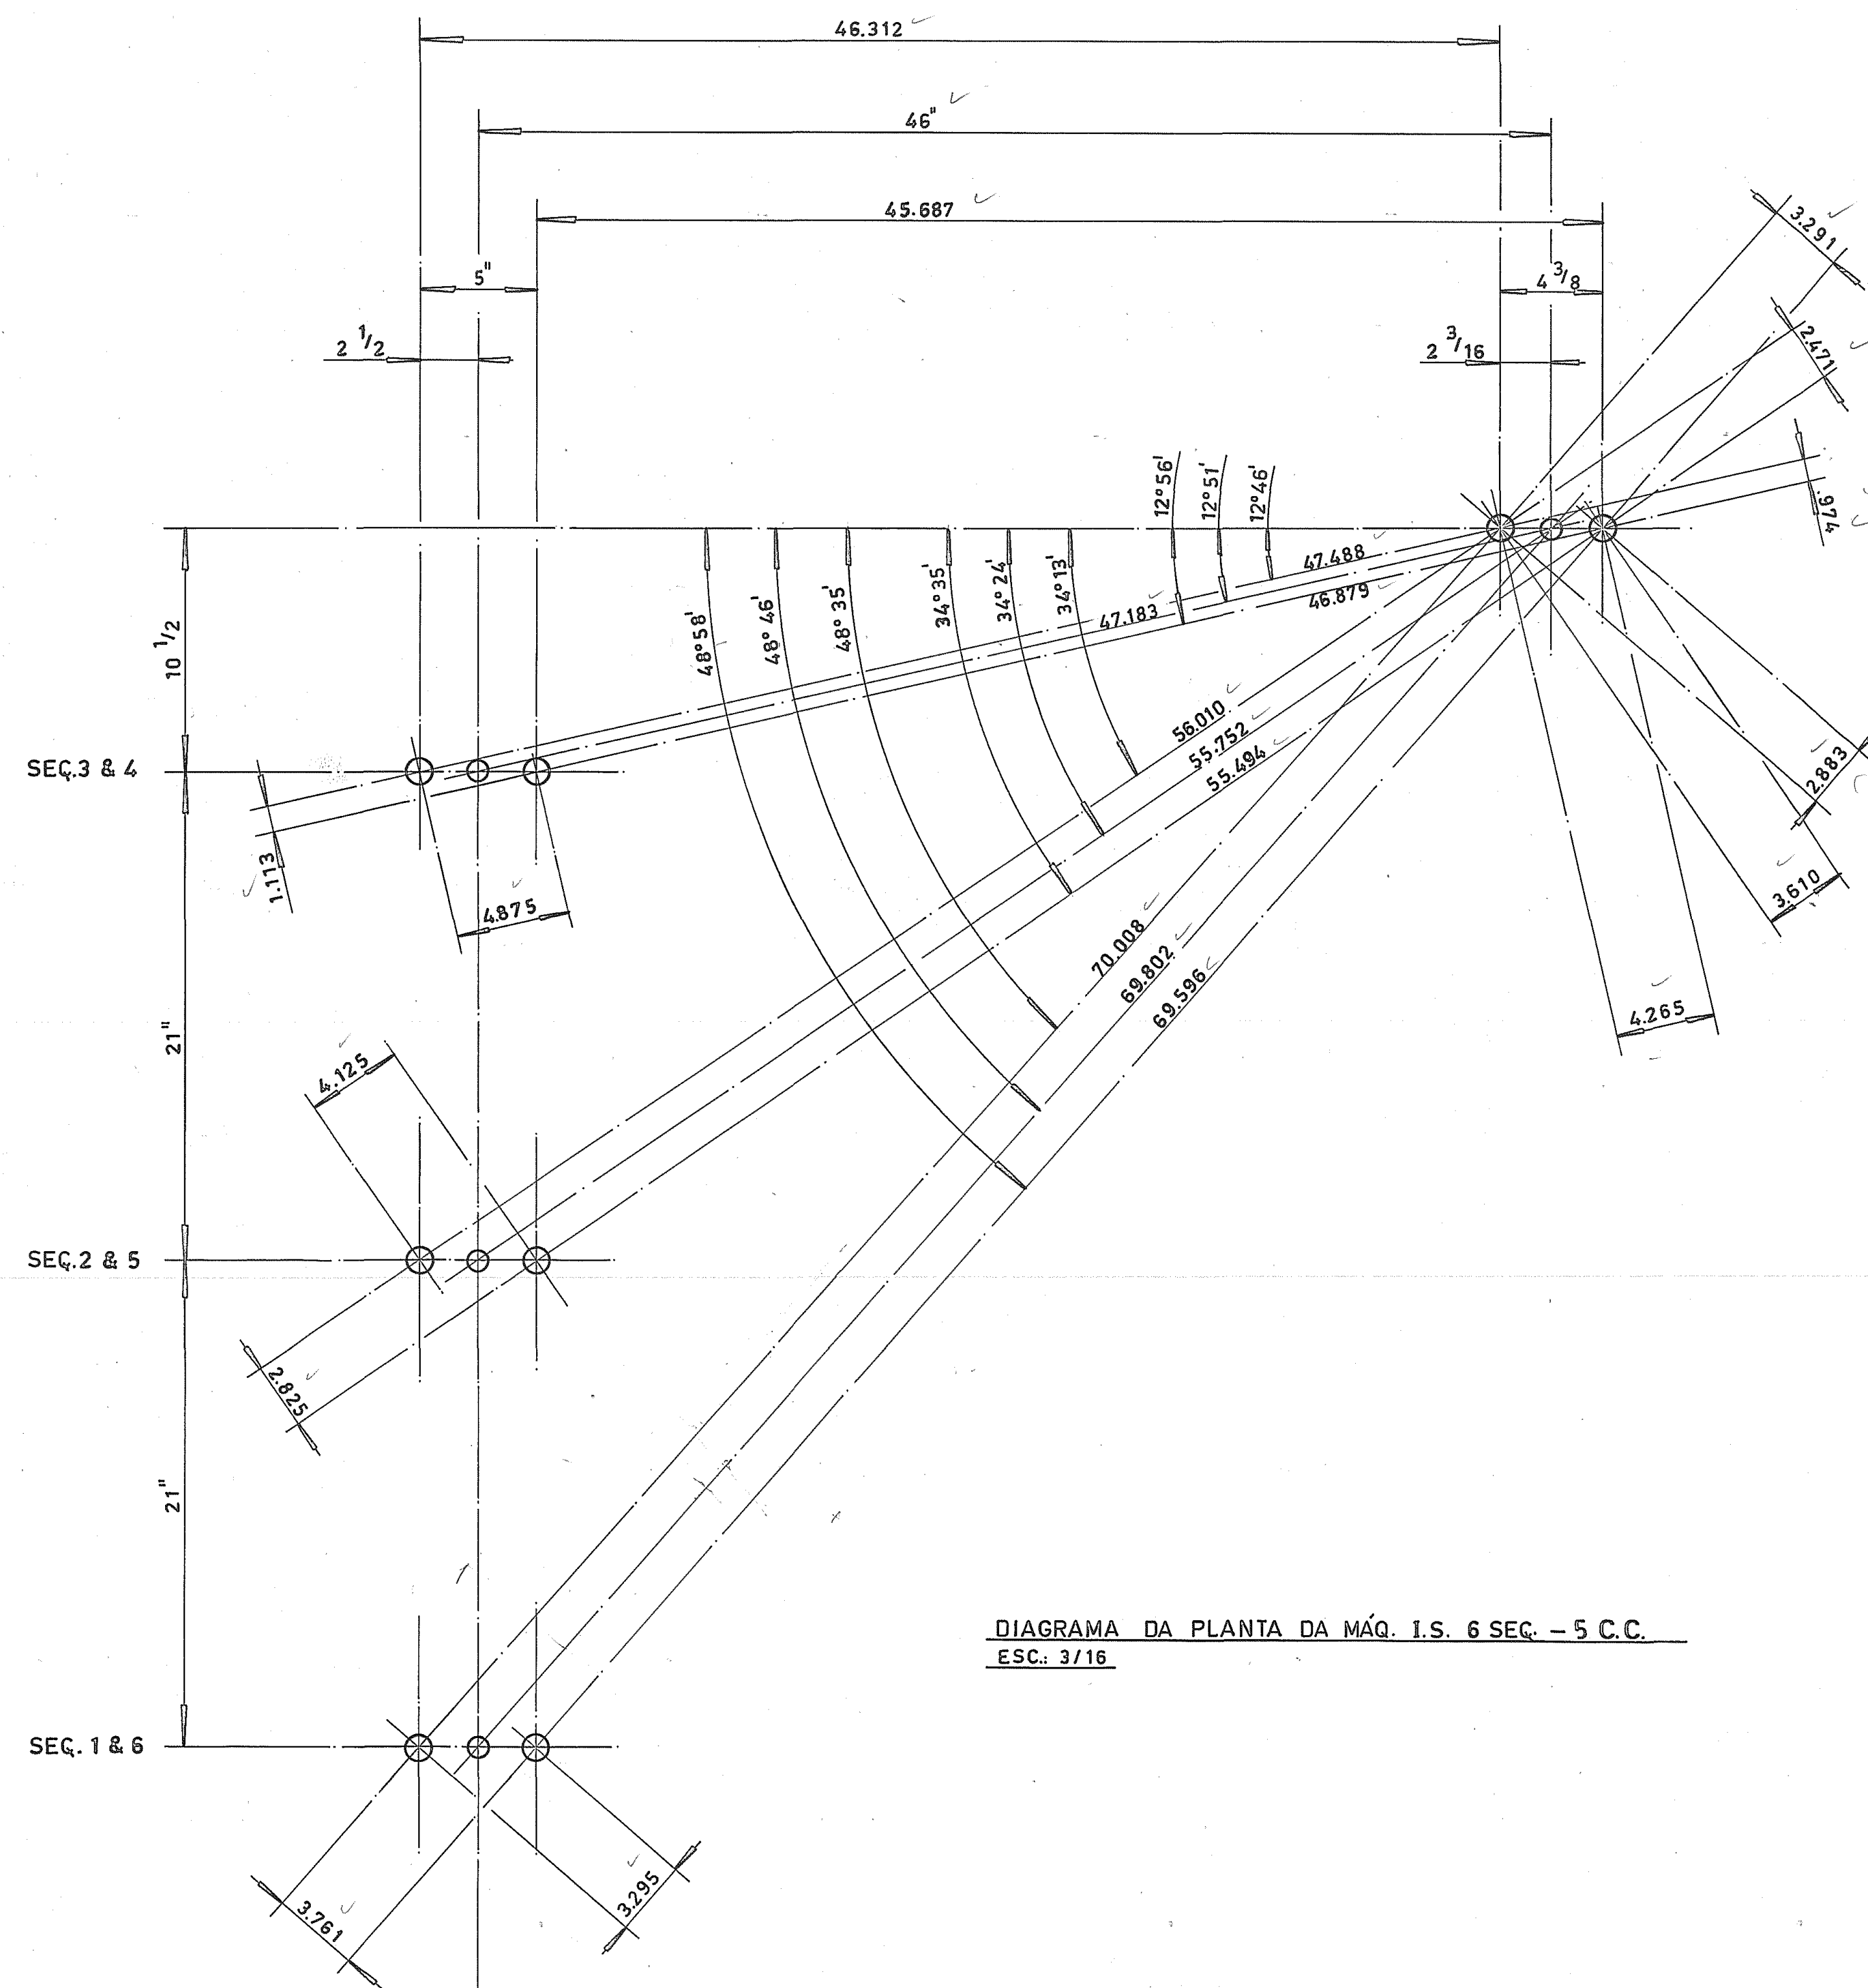


DIAGRAMA DA PLANTA DA MÁQ. I.S. 6 SEQ. - 5 C.C.
ESC.: 3/16

DATA	18/1/88	DES.	Alencar
REVISÃO	ITEM	VER.	1/1
TOLERÂNCIAS STANDARD PARA SUPERFÍCIES USINADAS SEM TOLERÂNCIA INDICADA		VIDROS VITON LTDA.	
DECIMAL ± 0.05"		MATERIAL	
FRAÇÃO		NOME	
DE 0" ATE 5" ± 1/64		SISTEMA DE DISTRIBUIÇÃO D.G.	
DE 5" ATE 24" ± 1/32		CONJ. 3 5/8, 4 1/4 & 5 C.C. (MOLDE)	
ACIMA DE 24" ± 1/16		N.º DO CONJ. 191-D-5698	
		NOME	
		ESQUEMA DE MONTAGEM E	
		DIAGRAMA P/ MAQ. I.S. 5 C.C.	
		N.º DA PEÇA VV-2836	
		TRAT.	
		N.º DO DES.	
		ESCALA 1/4	