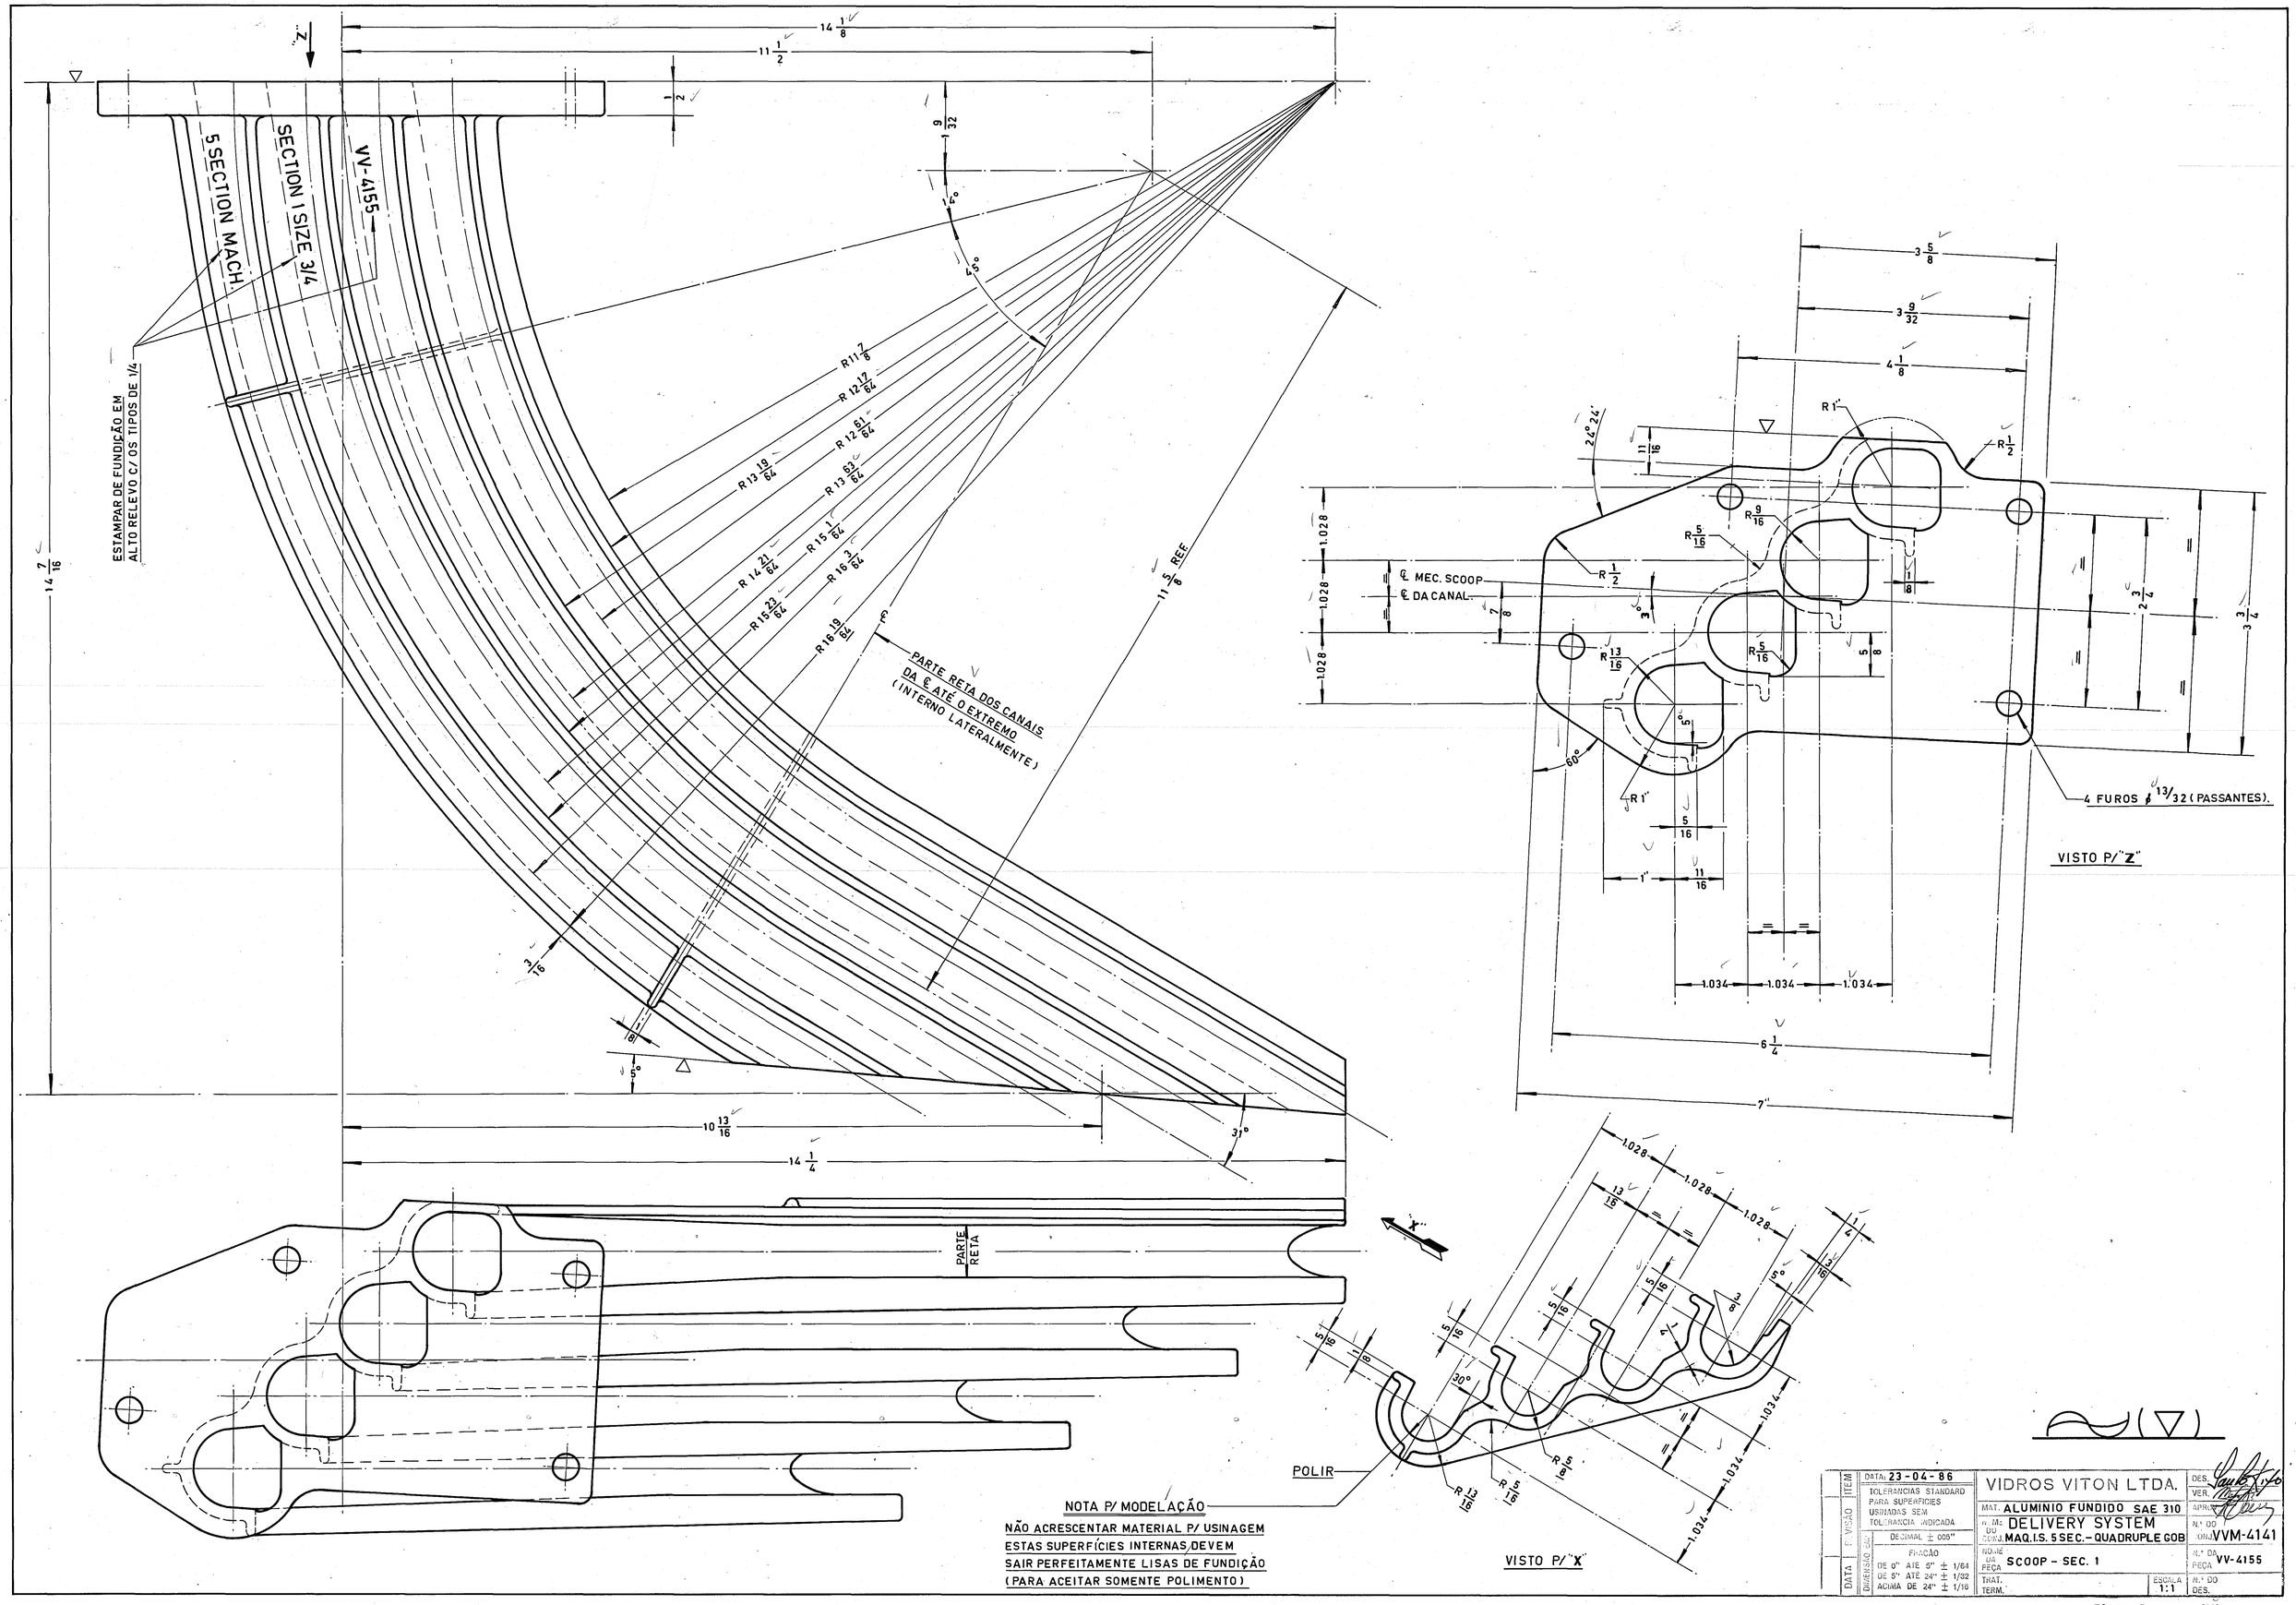

NOTA P/ MODELAÇÃO

NÃO ACRESCENTAR MATERIAL P/ USINAGEM
ESTAS SUPERFÍCIES INTERNAS DEVEM
SAIR PERFEITAMENTE LISAS DE FUNDIÇÃO
(PARA ACEITAR SOMENTE POLIMENTO)

DATA: 23-04-86	VIDROS VITON LTDA.		DES.
TOLERANCIAS STANDARD PARA SUPERFÍCIES USINADAS SEM TOLERANCIA INDICADA	MAT. ALUMINIO FUNDIDO SAE 310		VER.
DECIMAL ± 005"	N.º DO CONJ. DELIVERY SYSTEM MAQ.I.S. 5 SEC.- QUADRUPLE GOB		APROV.
FRAÇÃO DE 0" ATÉ 5" ± 1/64 DE 5" ATÉ 24" ± 1/32 ACIMA DE 24" ± 1/16	NOME DA PEÇA SCOOP - SEC. 1		N.º DO CONJ. VVM-4141
	TRAT. TERM.	ESCALA 1:1	N.º DA PEÇA VV-4155
			N.º DO DES.

FOLHA 5 (M)